


PODS

The POD has been updated with new construction and proportions, simplifying the load-bearing structure and the possible configurations.


The entrance door can be placed in the front or on the side, depending on the configuration and available space.

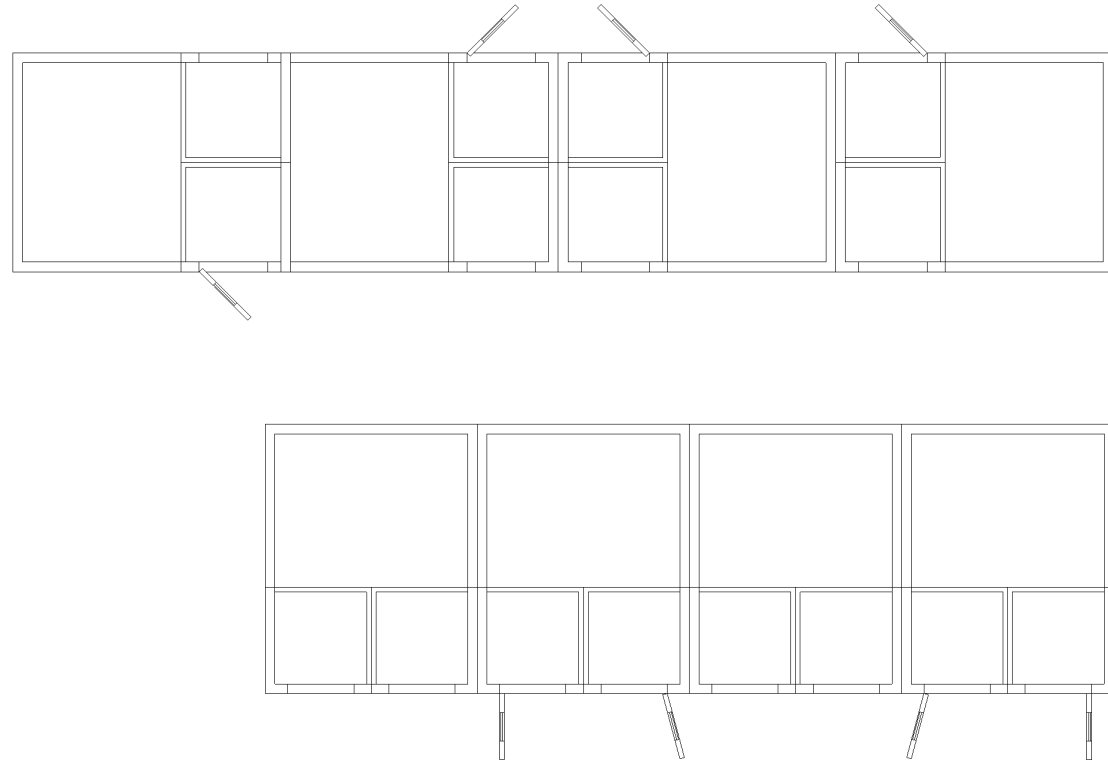


PODS 2.0


Each POD module consists of two sleeping spaces based on a bunk-bed structure, with separate full-height entrances. The sleeping space is accessible from the side of the bed.

The entrance area is equipped with a shelf, hooks, a mirror, and coat hangers. The top bunk is accessible with a combined shelf and step ladder.

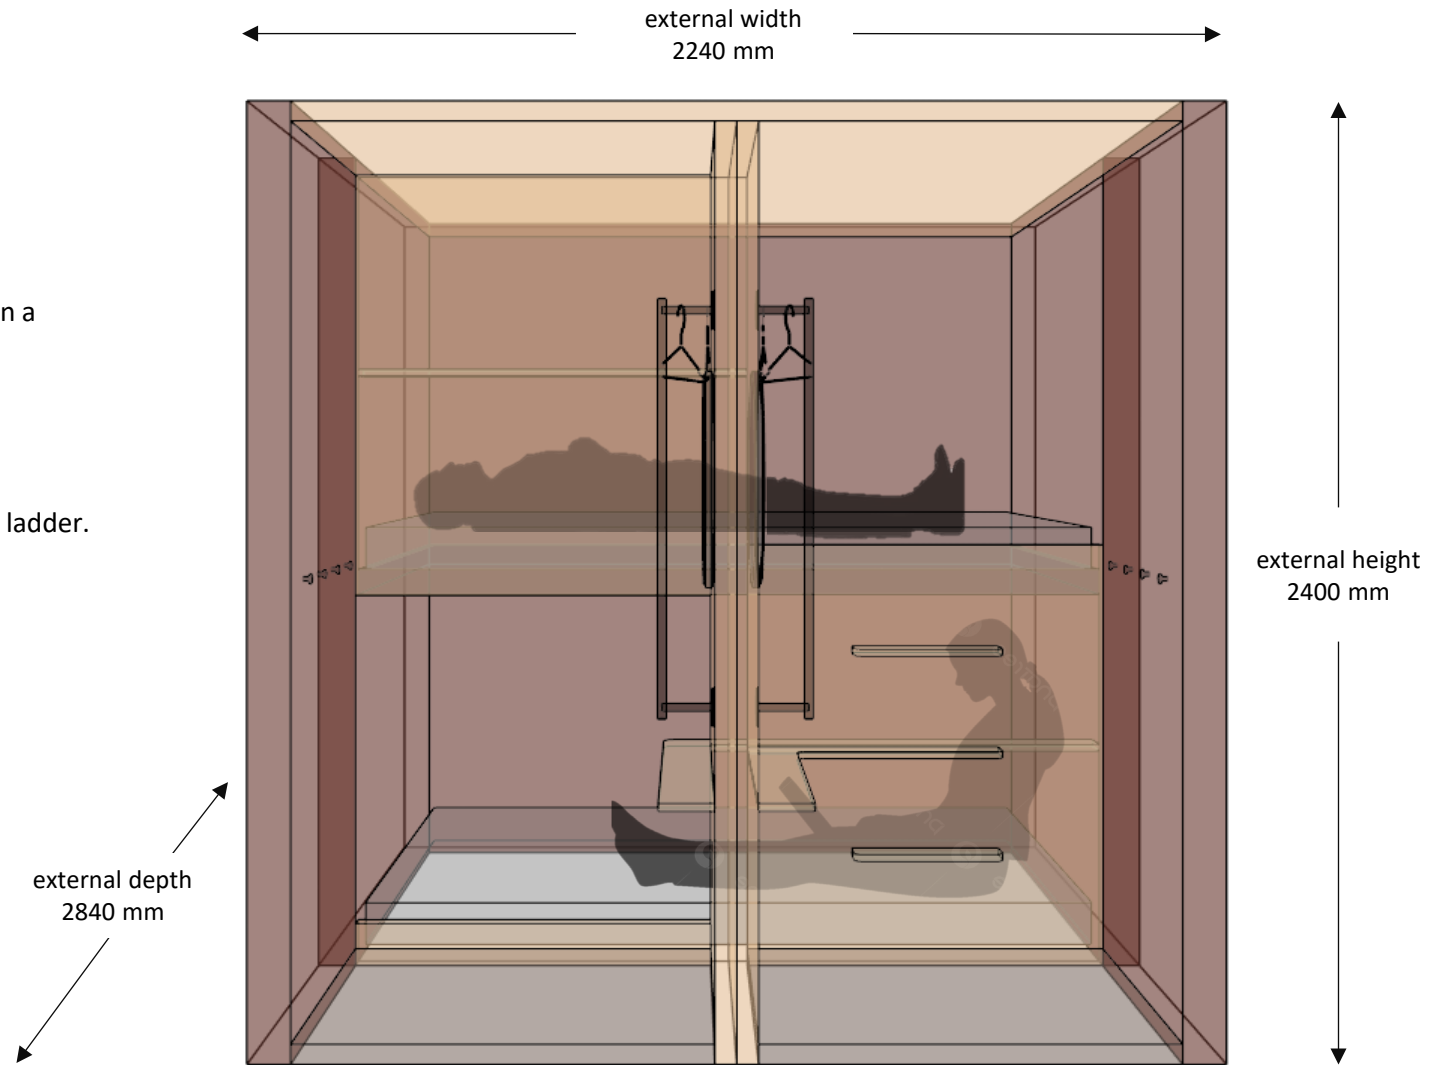


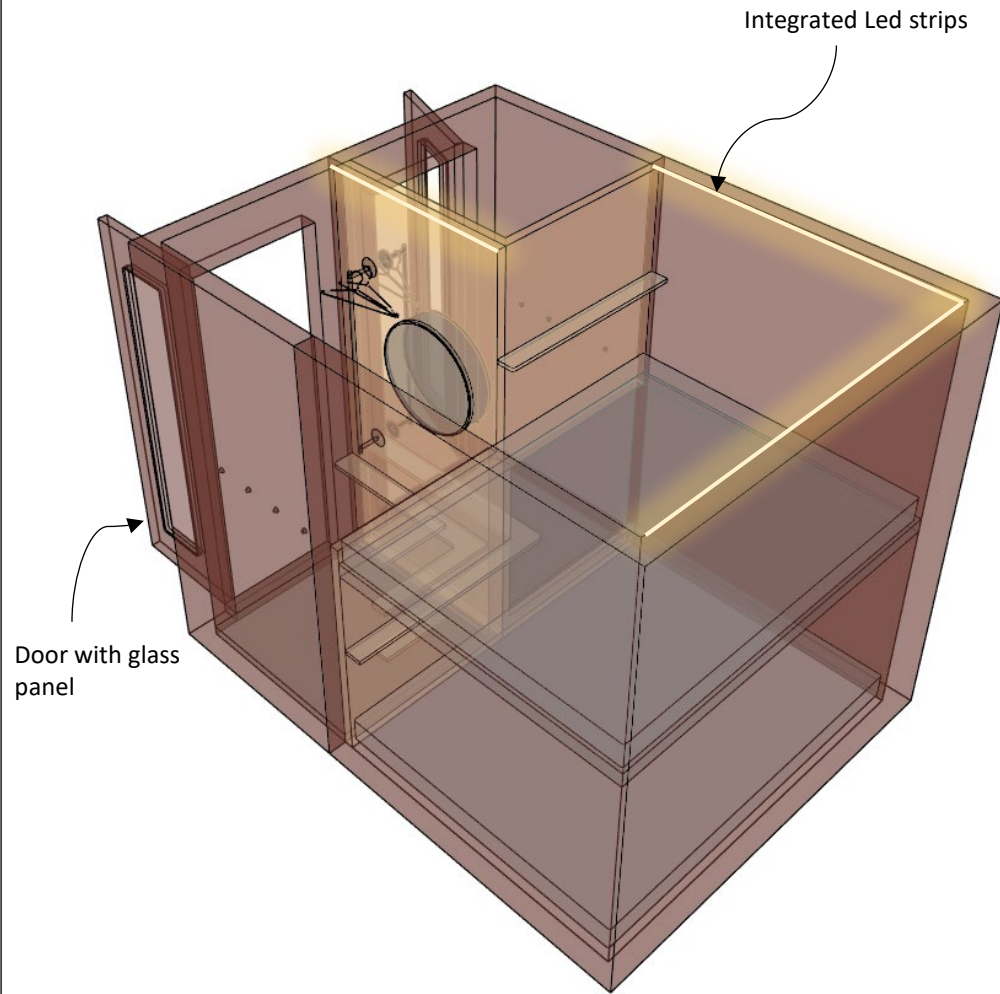


Left view


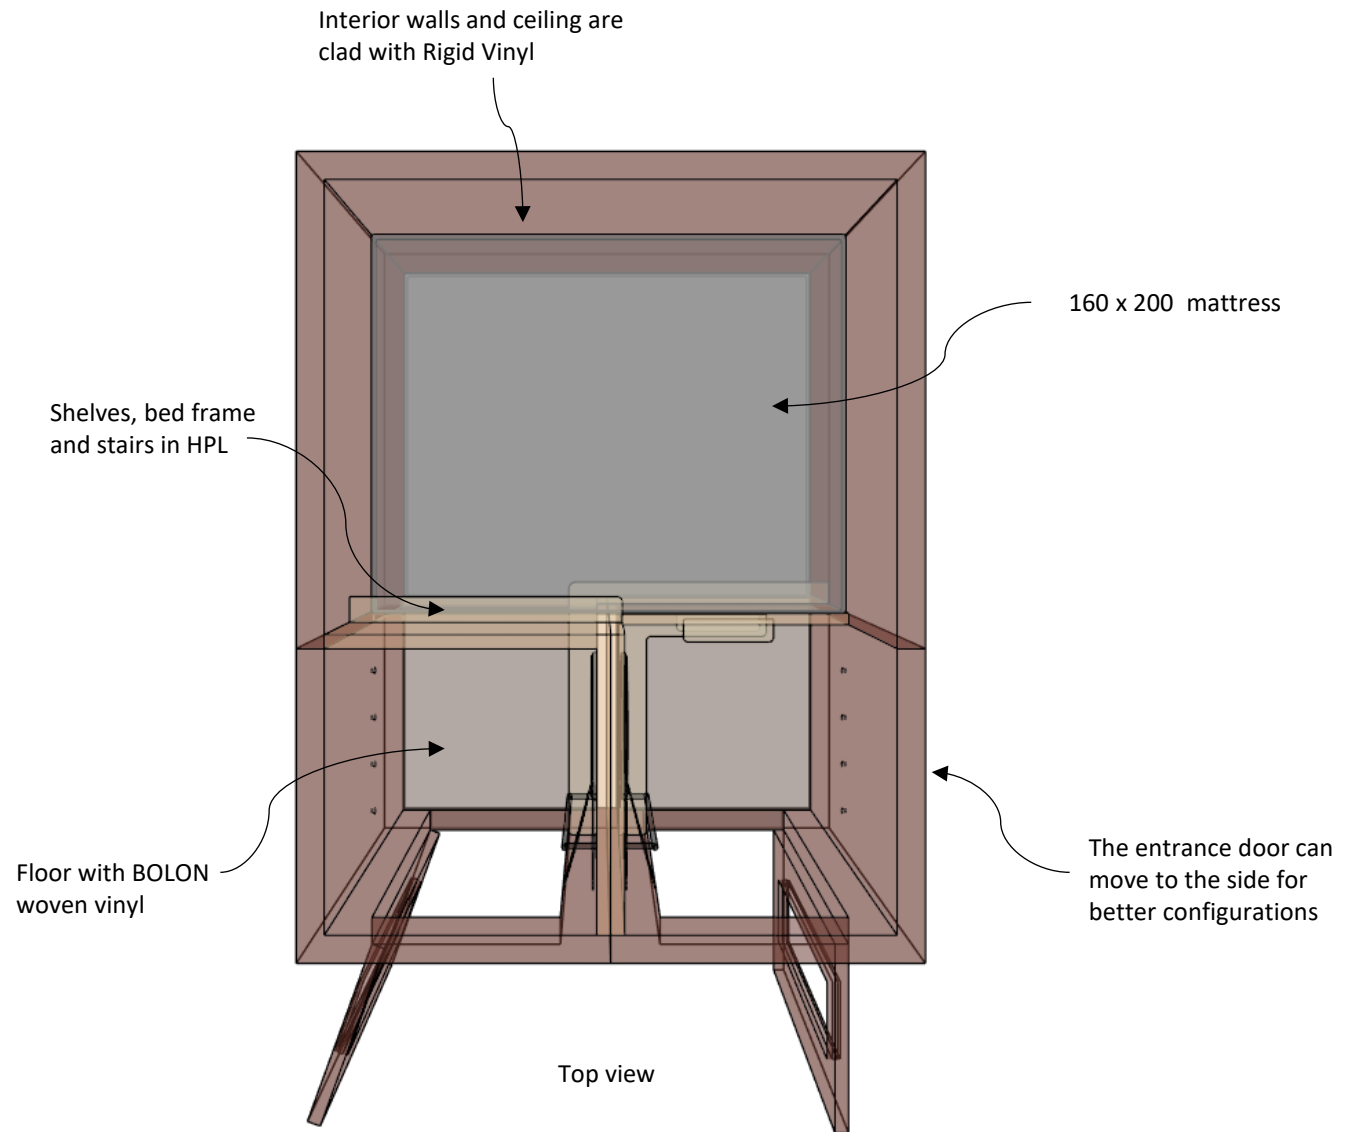


Top view

Top bunk

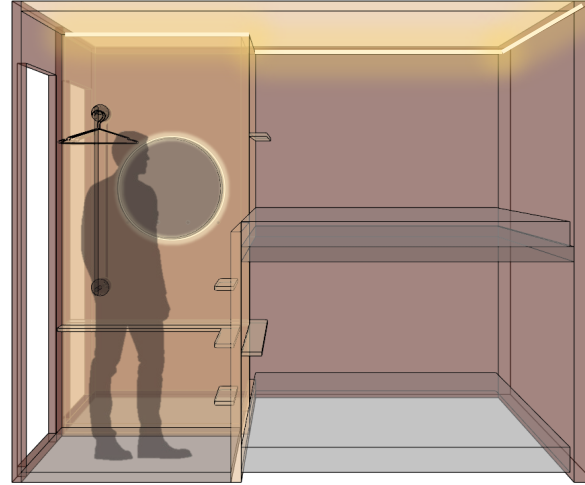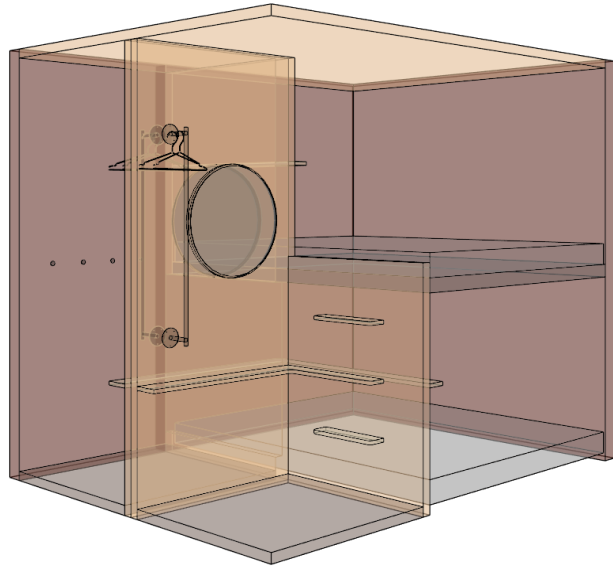


Bottom bunk

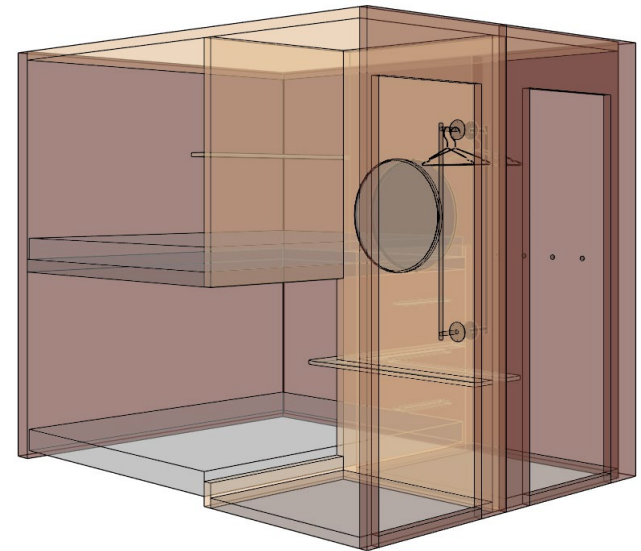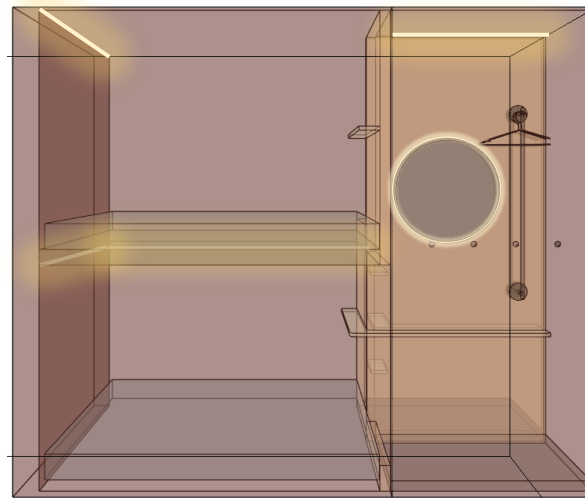


Functionality





- Sound Insulation
- Fire Insulation
- Ventilation
- Smoke detector
- Electrical outlets
- Integrated lighting, LED strips along the ceiling
- Lighting control, dimmable
- Door with Ving Card Essence reader
- Door with a window. Electronic frosting on the glass for privacy
- Interior walls clad with rigid vinyl, to provide a durable, low-maintenance finish (Palladium Rigid Sheet by Inpro or equivalent)
- Floor with BOLON, woven vinyl.

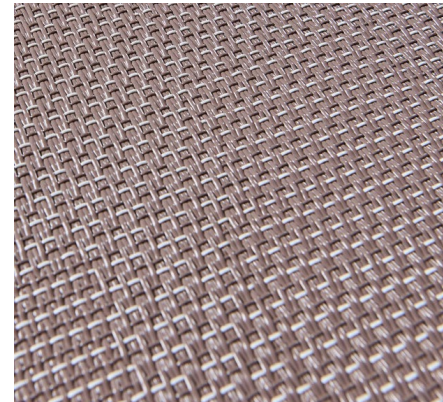

Example of BOLON flooring

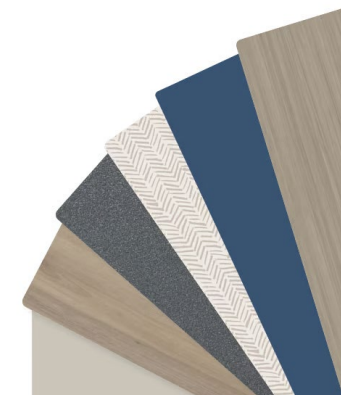

<https://www.inprocorp.com/products/palladium-rigid-sheet-405-wall-cladding>

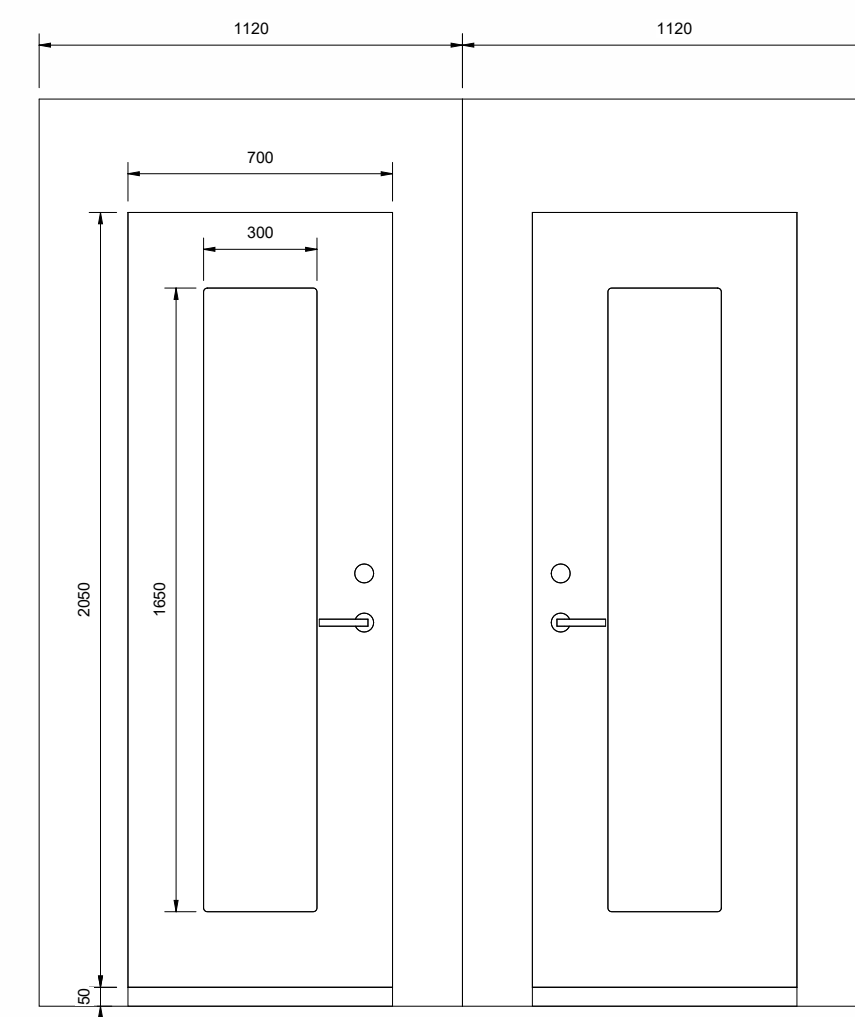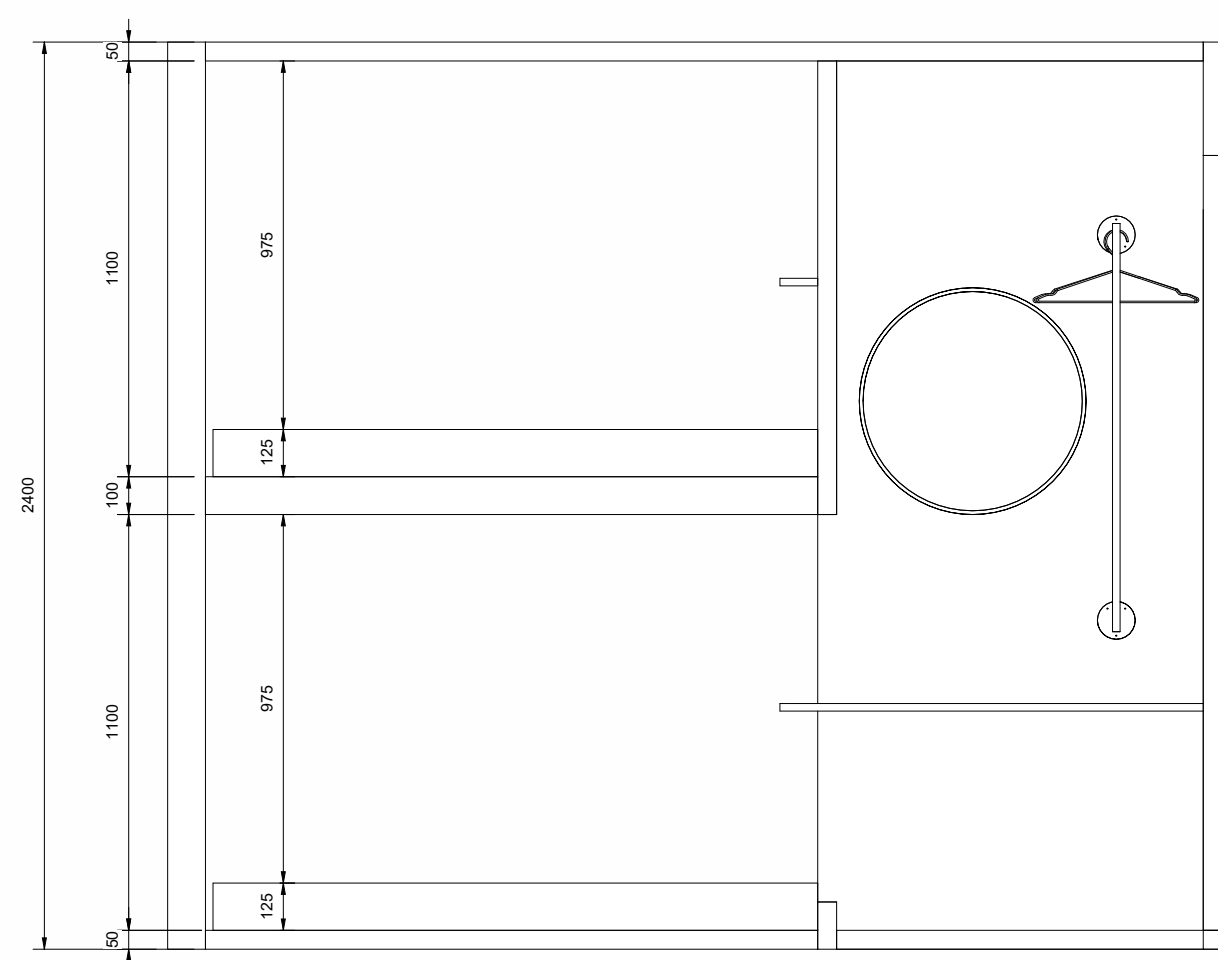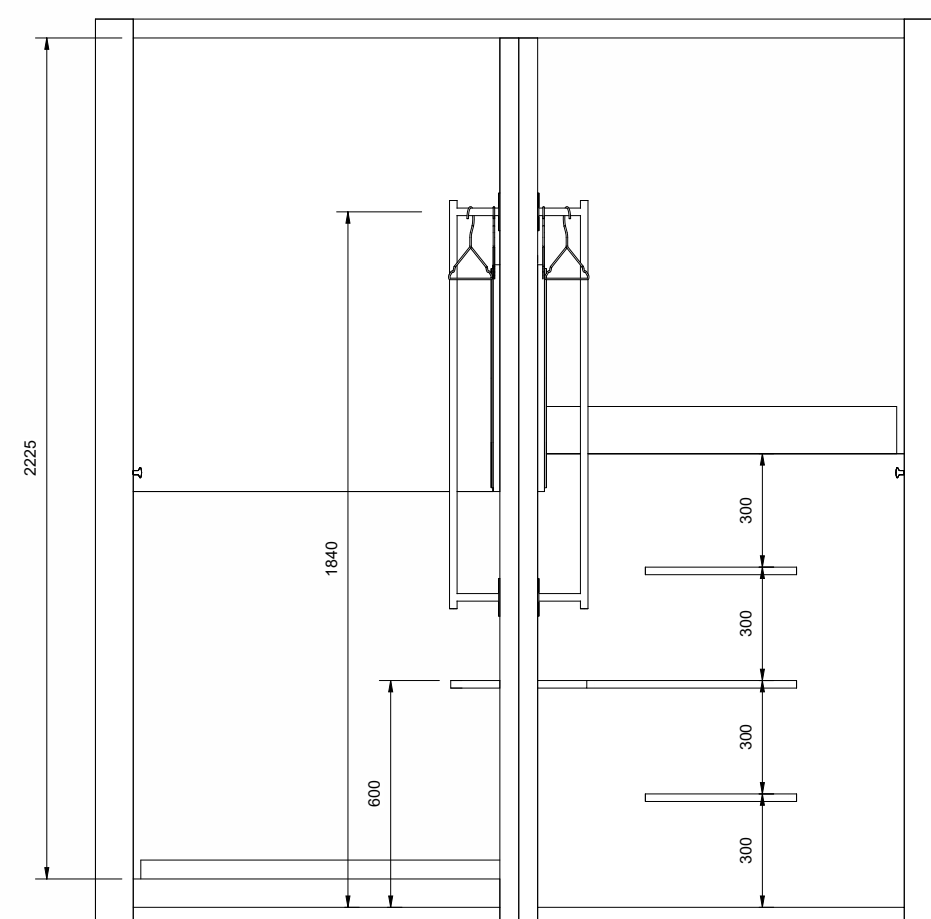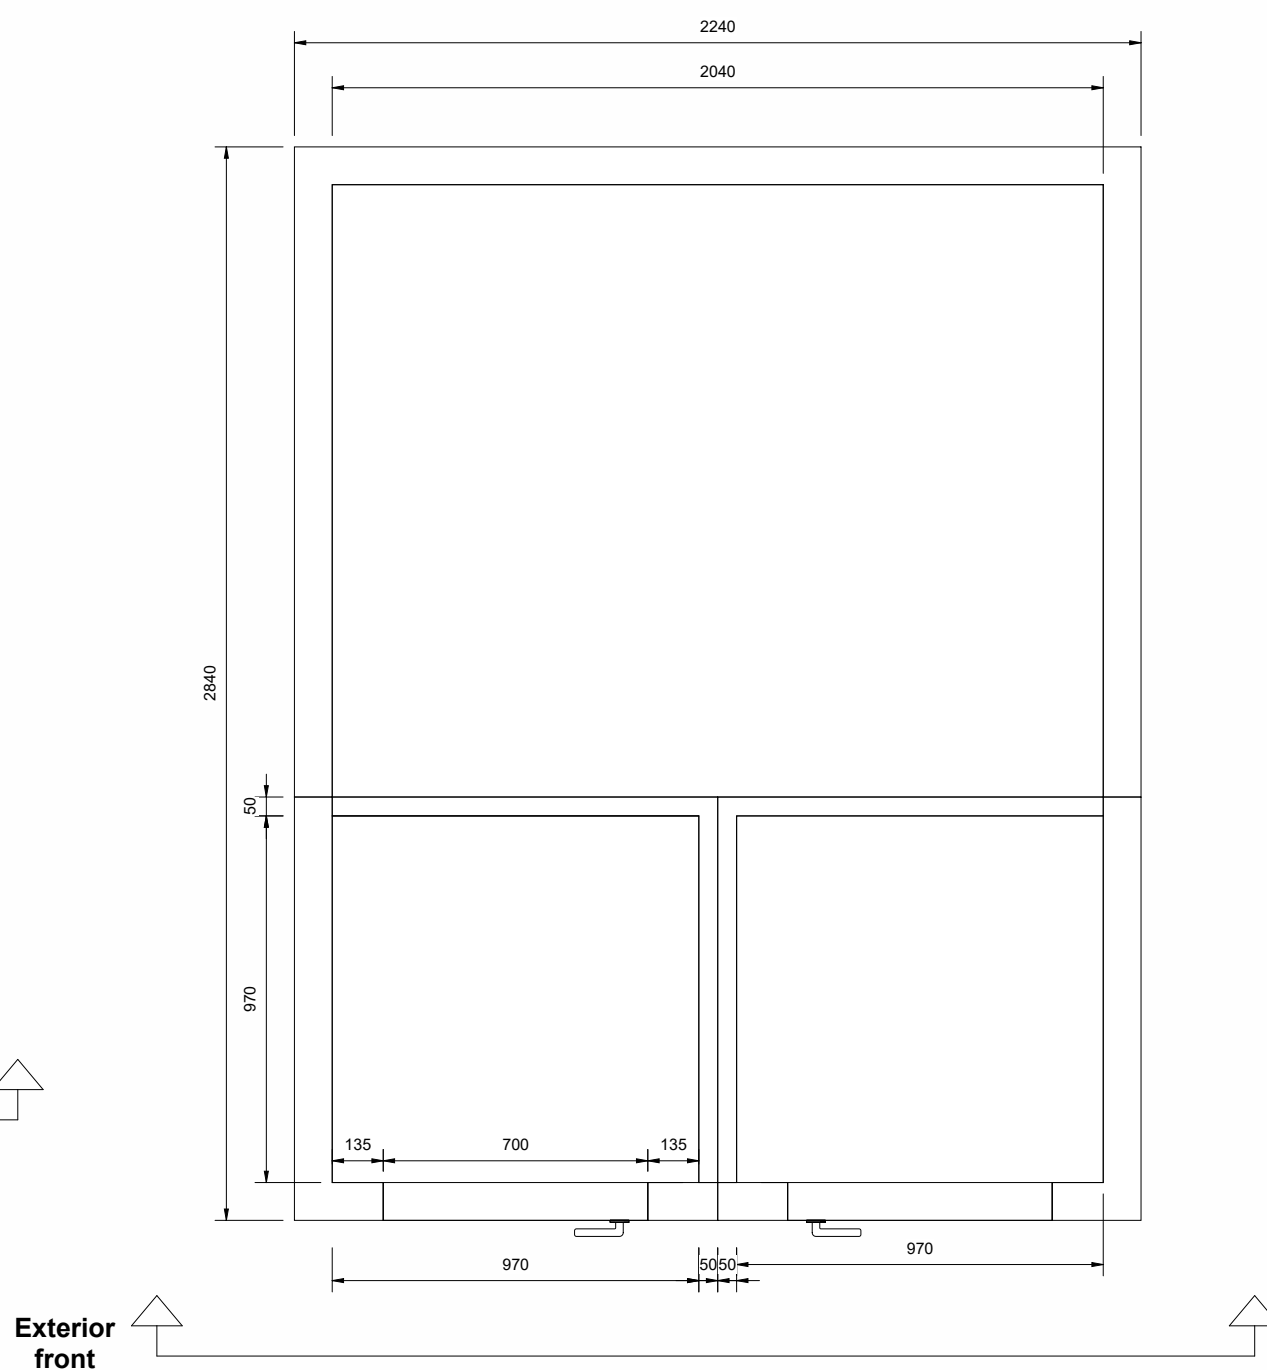

2 Interior front
1 : 20

3 Interior side
1 : 20

4 Exterior front
1 : 20

No.	Description		Date
Sheet name:			
Sheet status:			
PREPROJECT			
Issue date:		10.04.26	
Drawn by:			
Scale	1 : 20	Sheet	A2
Sheet number (Level, Field, System code, Drawing type, Serial number)			Rev
A101			