



Single Pods (H=257cm)


Single Pods

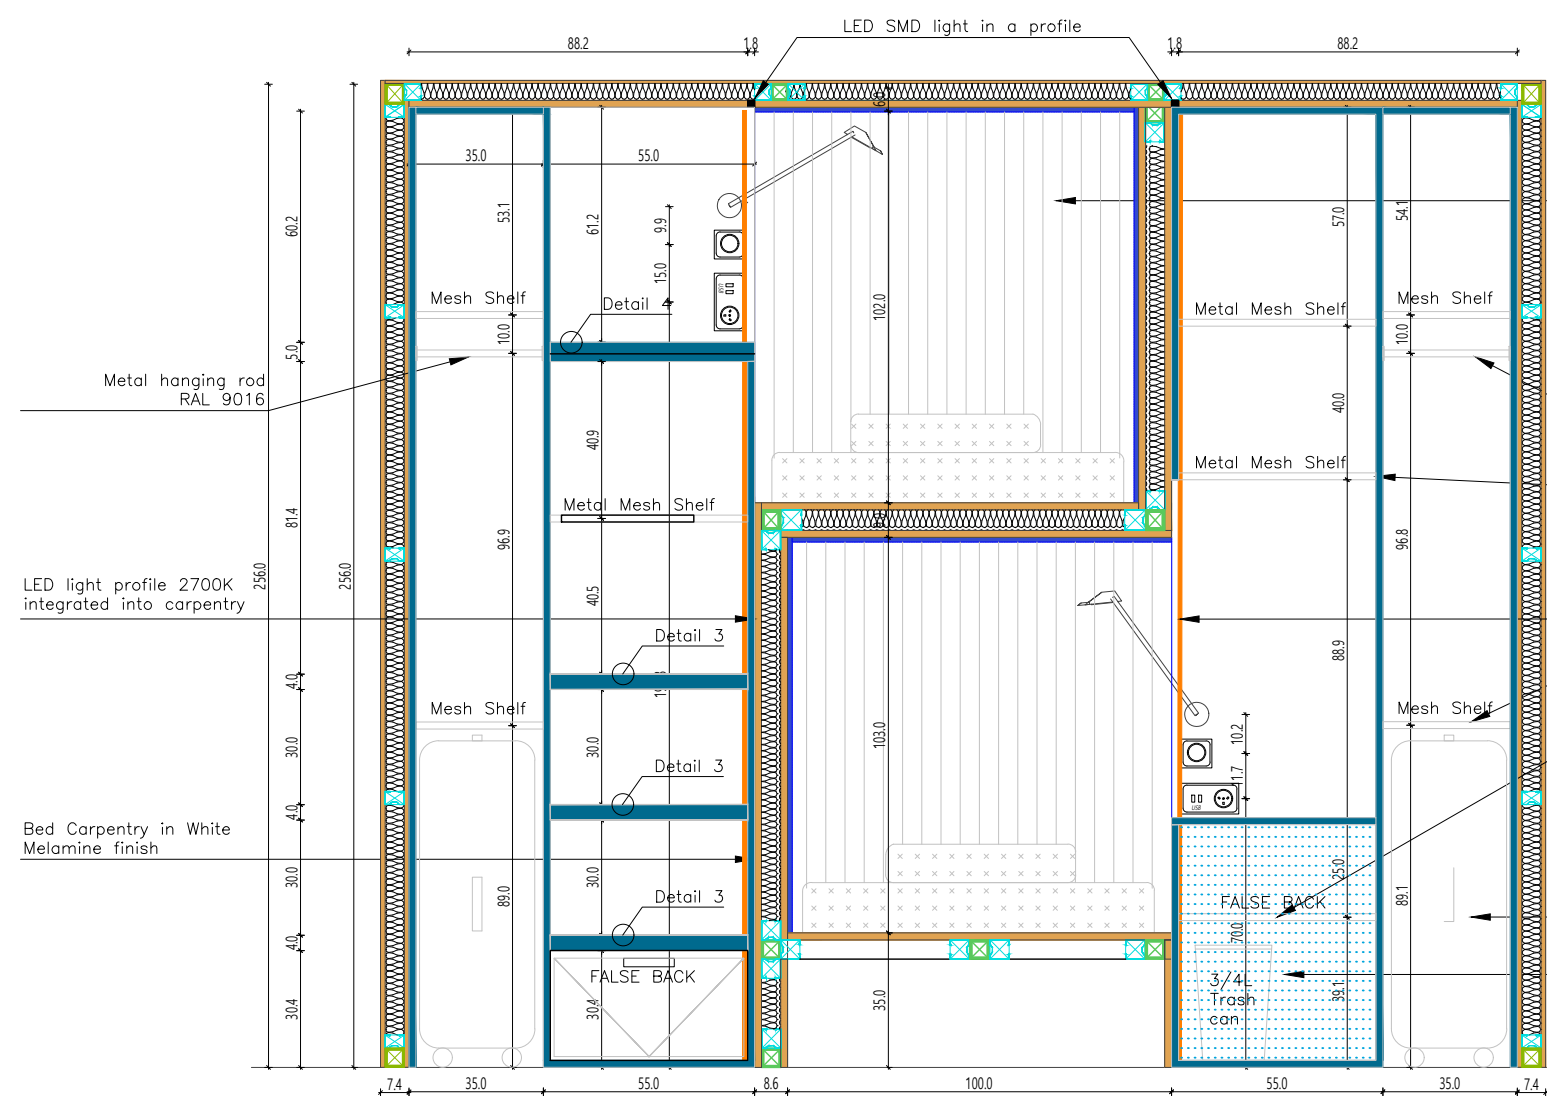


Section 1-1
Scale 1:25

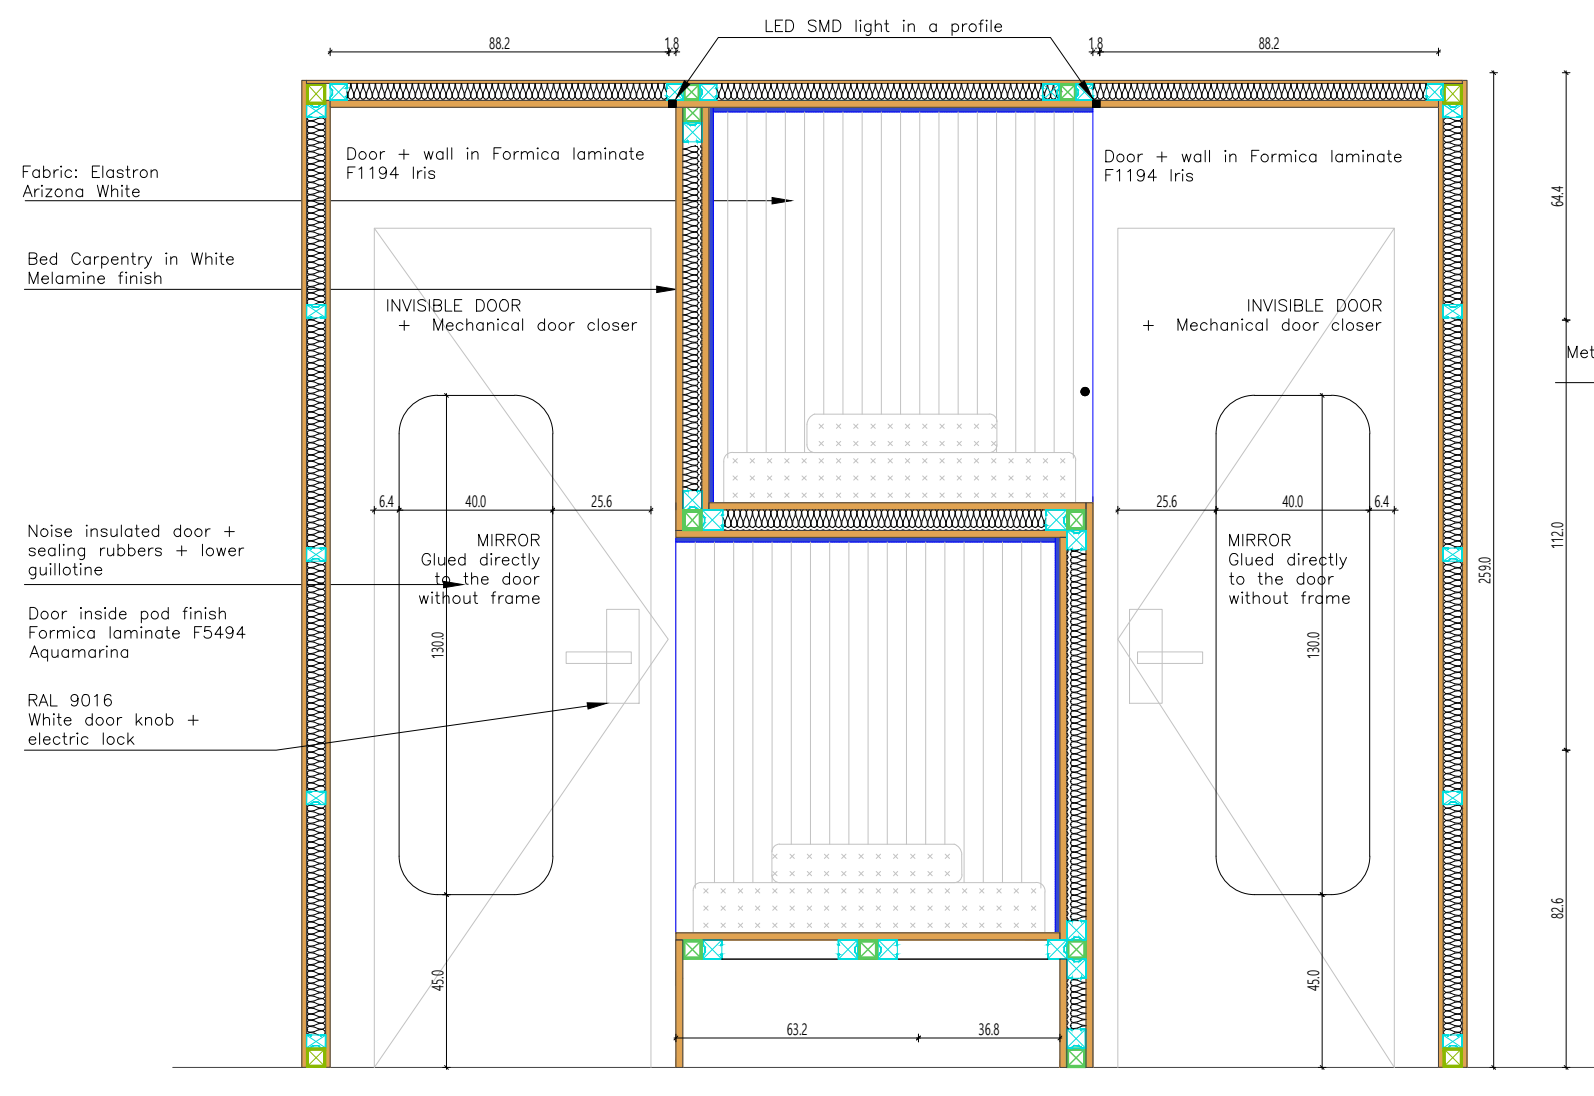







Section 2-2
Scale 1:25

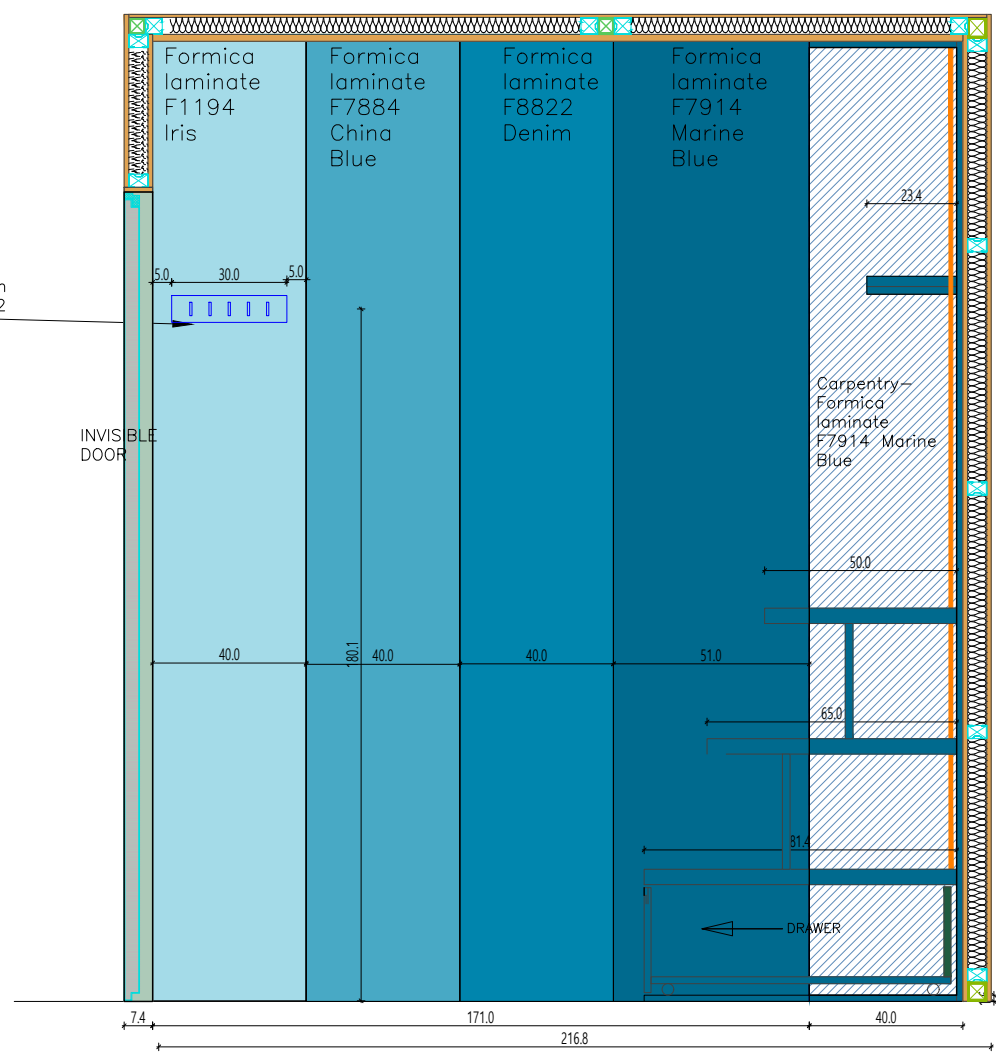


Section 3-3
Scale 1:25

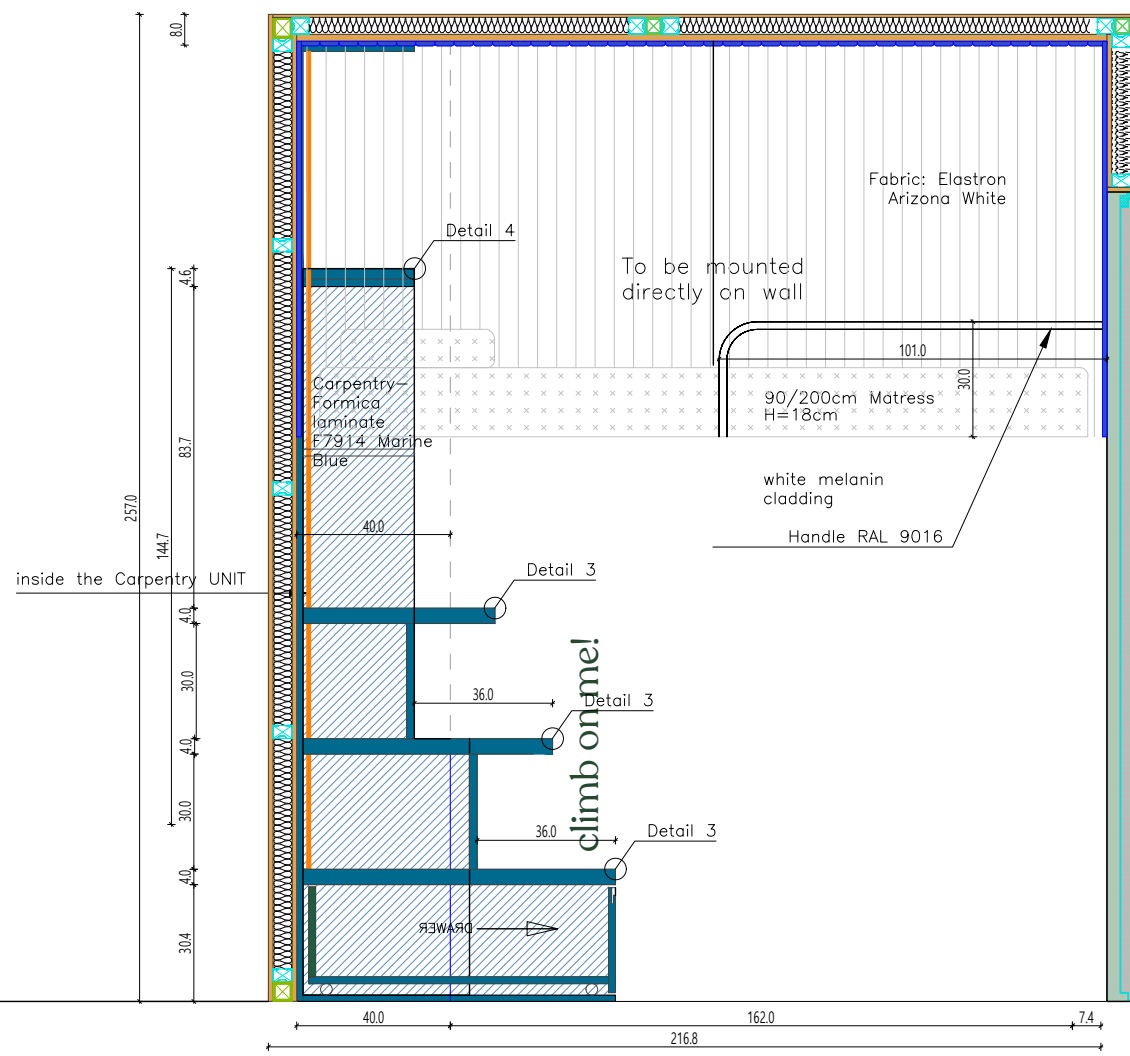


Section 4-4
Scale 1:25

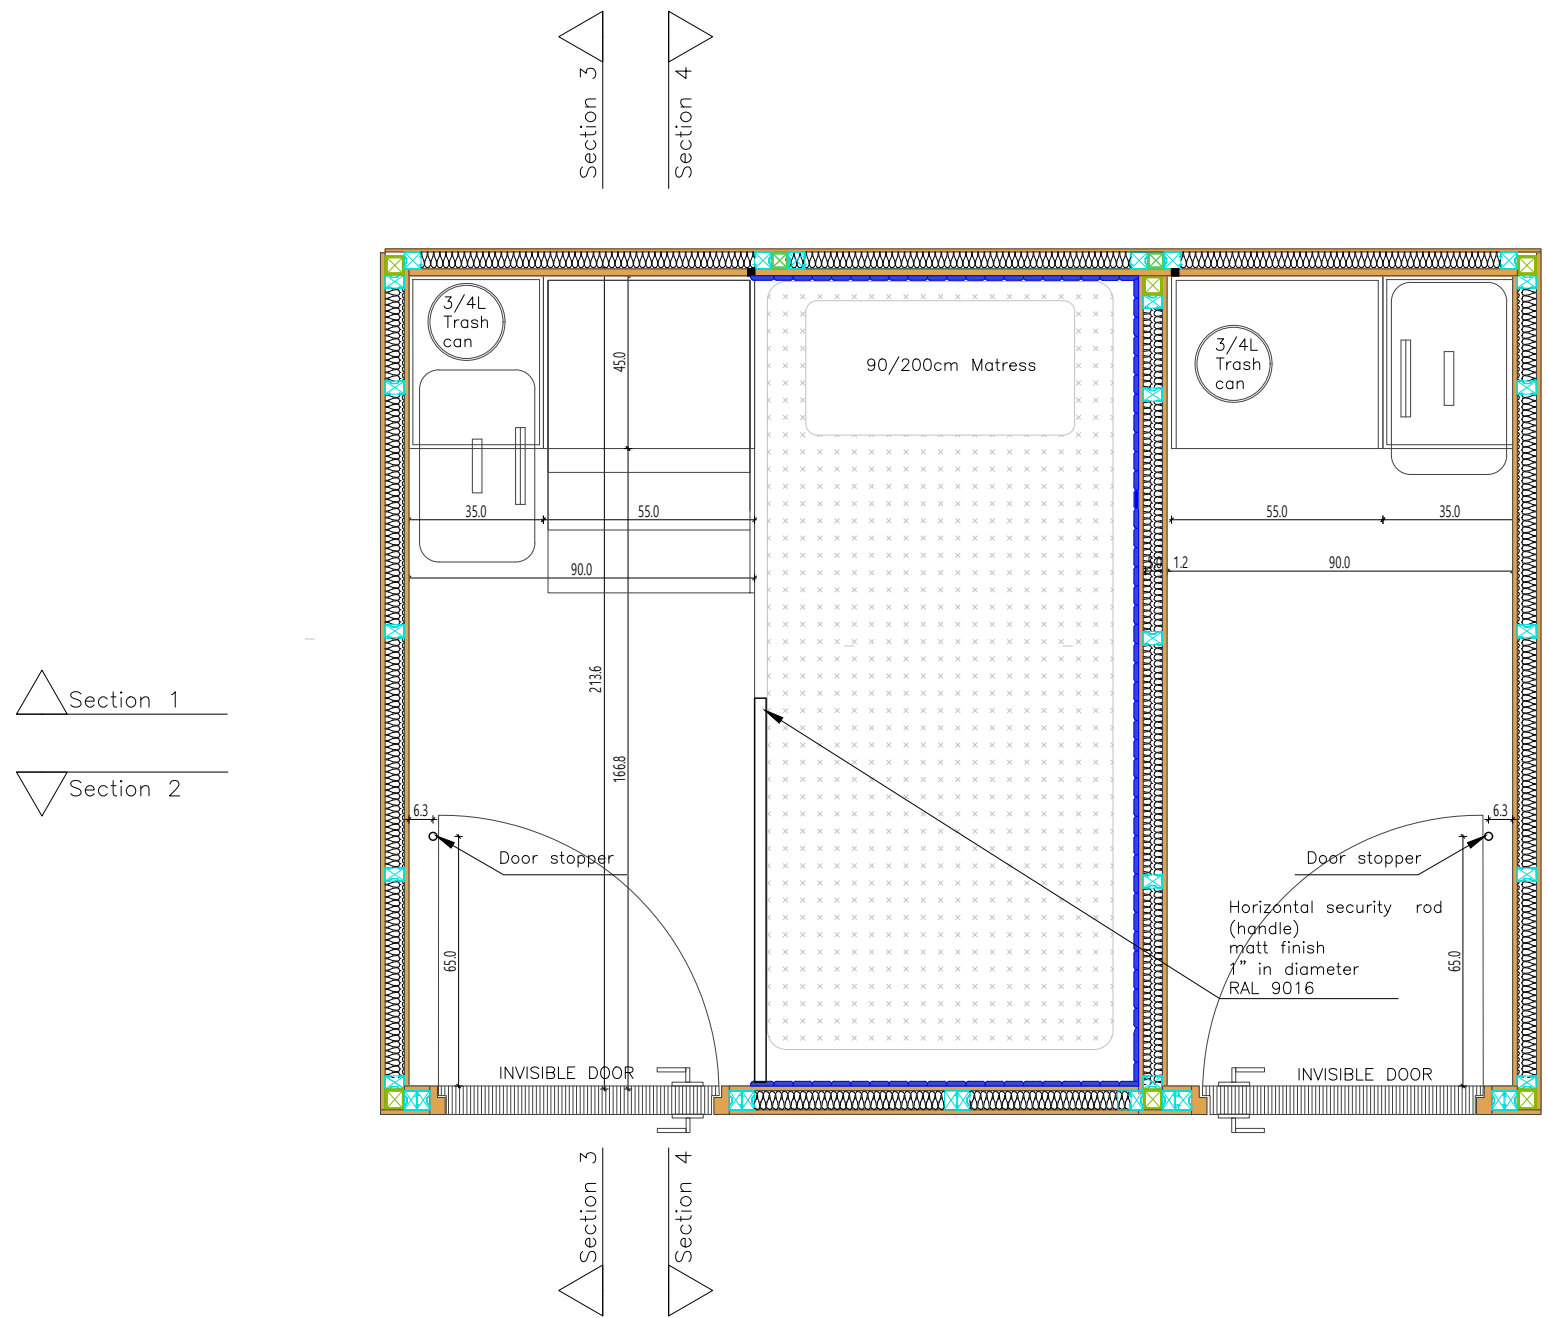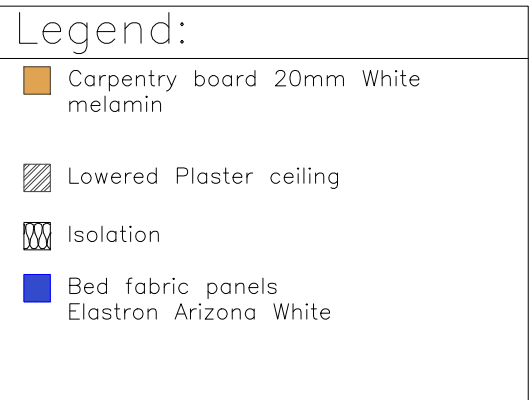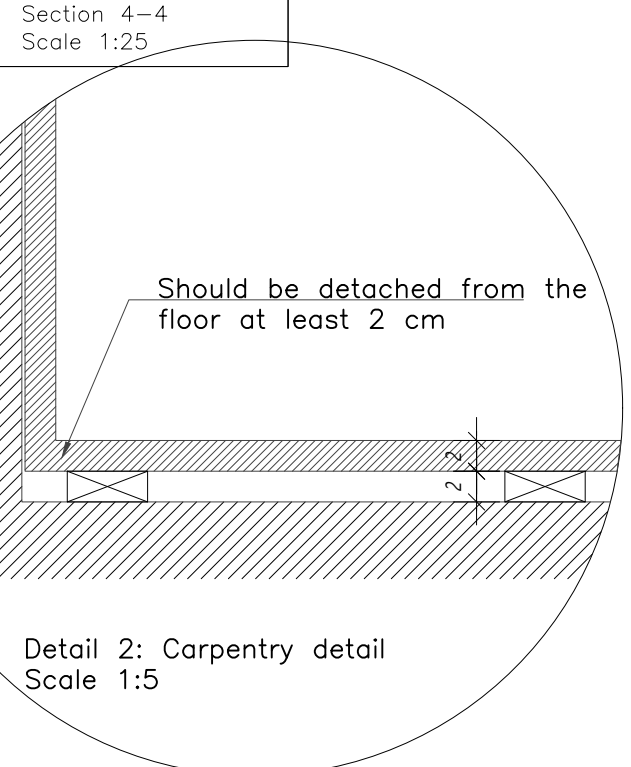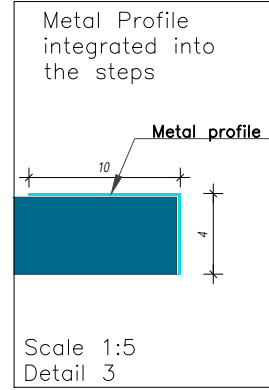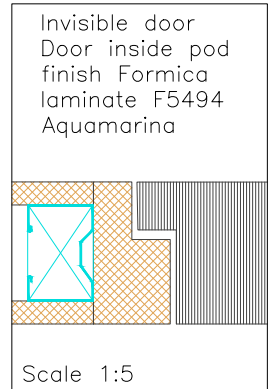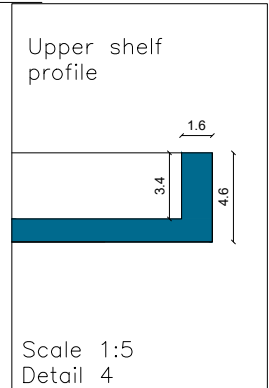

Plan; Level +2.20
Scale 1:25

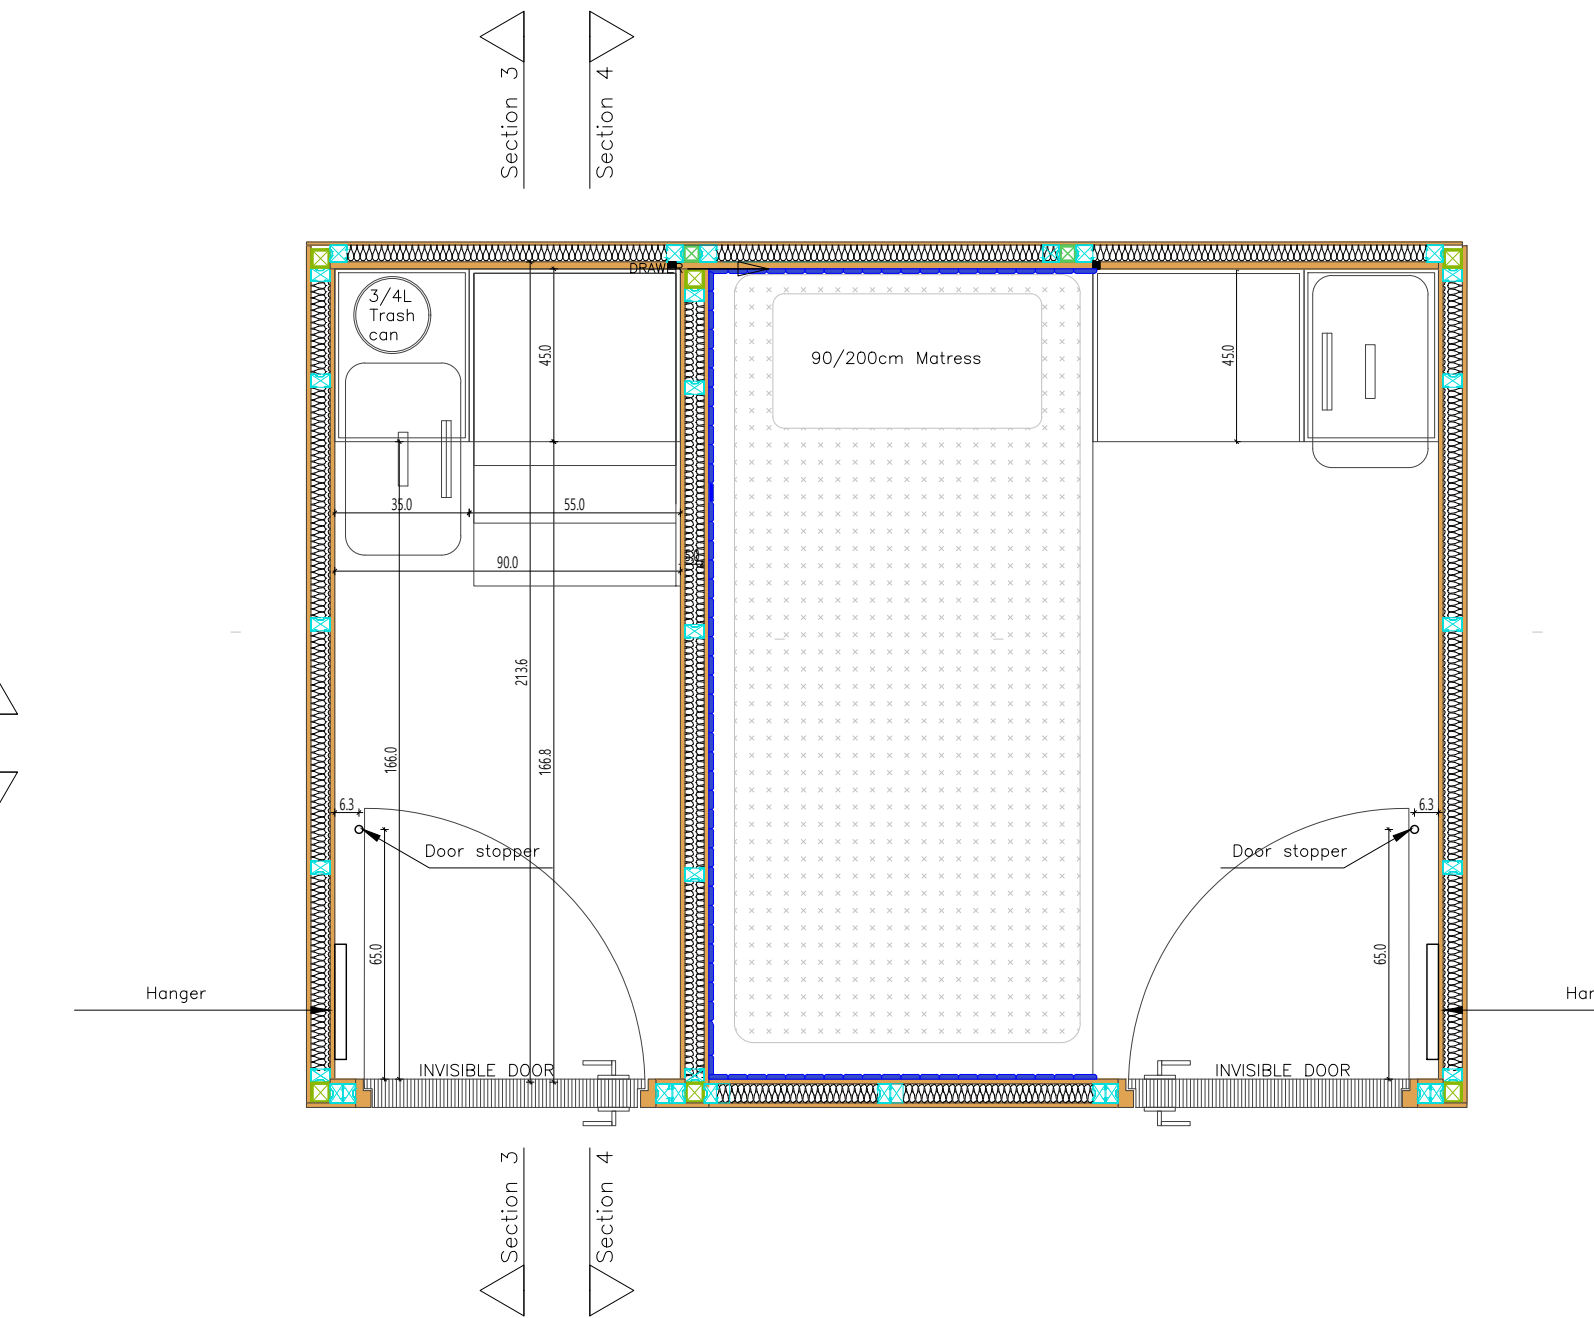

Plan; Level +1.20
Scale 1:25

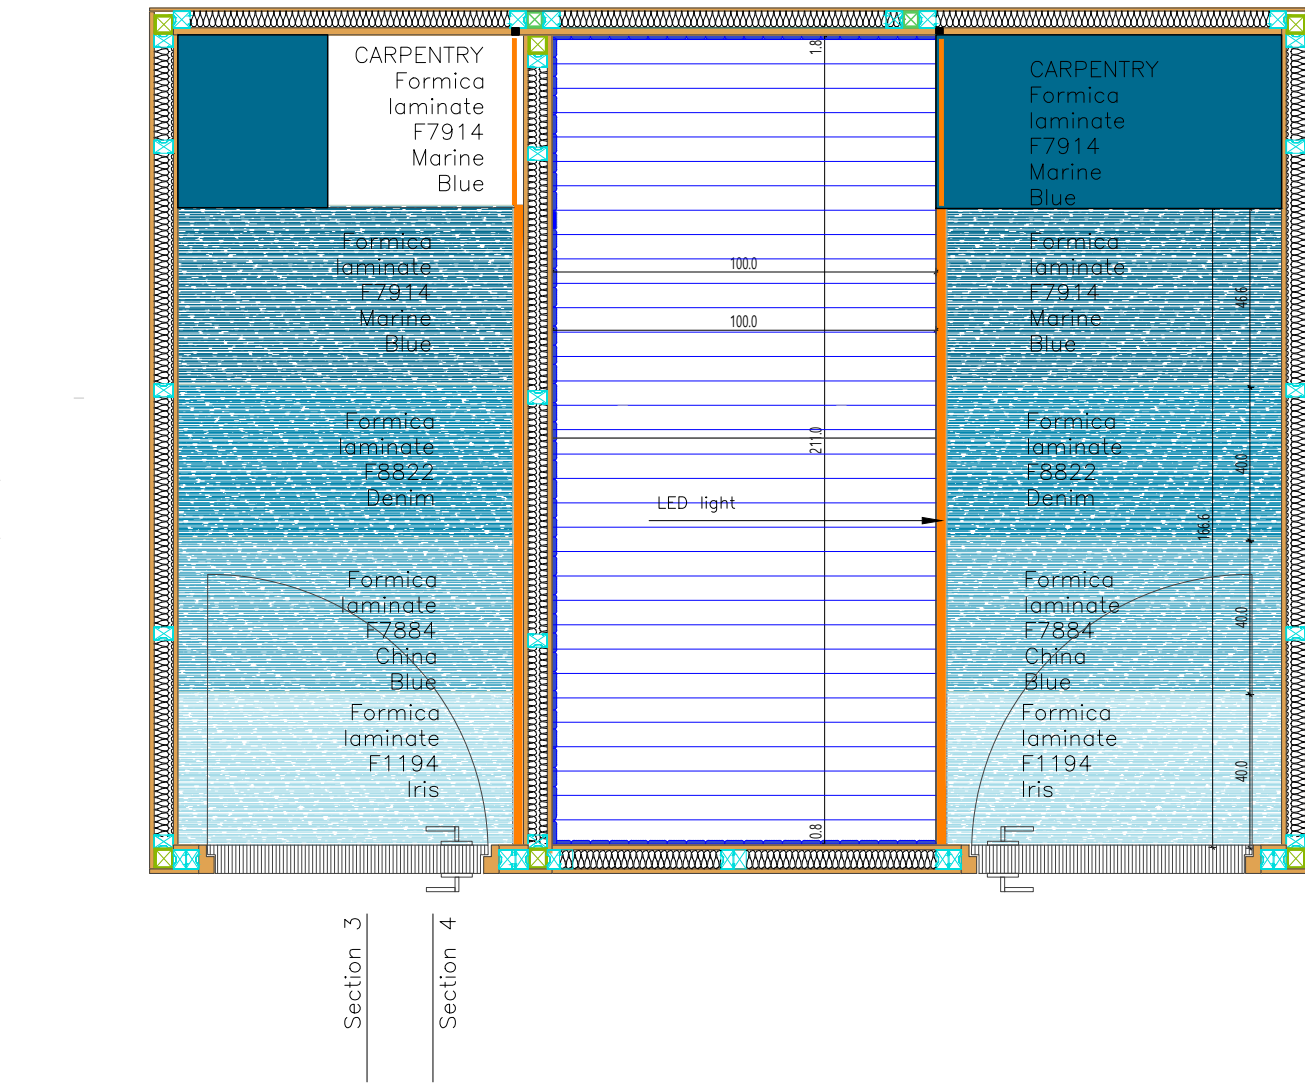

Plan; Ceiling
Scale 1:25

שרן בנדרמן אדריכלות ועיצוב 03-6204960
רוח כנן יורדי הסירה 5 תל אביב 03-5107833
טל: 03-6204960 | פקס: 03-5107833
eran@bdm-arc.com | www.bdm-arc.com

BINDER
MAN
ARCHITECTS