

For



CLINK BEDS
CLINK HOSTELS - CLINK 78


INDEX A - Drawing Pack - DRAFT 003

Client:	Clink Hostels
Project:	Clink 78 - Clink Beds
Address:	78 King's Cross Rd, London WC1X 9QG, United Kingdom
Date:	04/05/2026
Author:	S.Jaensch / A. Alzeyat

DRAFT



DRAWING LIST

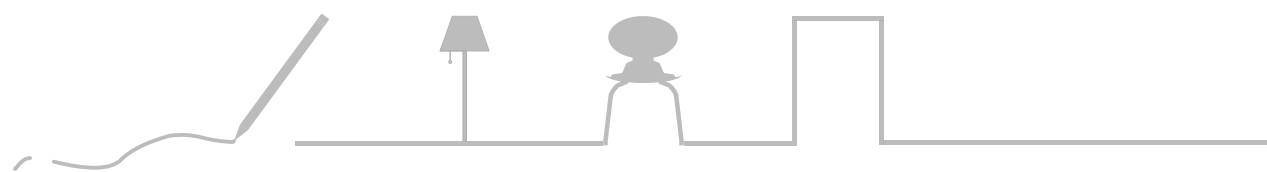

Stefanie Jaensch

INTERIOR DESIGNS

For



TEARAWOOD

- 00 COVER SHEET
- 01 CONTENT
- 02 BUNKBED CONCEPT
- 03 OVERVIEW - BED COUNTS

- 1-000 DOUBLE BEDS
 - 1-DB1-100 DOUBLE BED - AXO
 - 1-DB1-110 DOUBLE BED - DB1 GA

- 2-000 BUNKBEDS - TYPE 2
 - 2-001 TYPE 2 - FRAME
 - 2-002 TYPE 2 - SIGNAGE
 - 2-003 TYPE 2 - LED LIGHTS PLAN
 - 2-004 TYPE 2 - CURTAINS PLAN

- 2-A-100 2-A
 - 2-A-101 BUNKBED 2-A GA
 - 2-A-102 BUNKBED 2-A FRONT ELEVATION
 - 2-A-103 BUNKBED 2-A BACK ELEVATION
 - 2-A-104 BUNKBED 2-A RIGHT ELEVATION
 - 2-A-105 BUNKBED 2-A LEFT ELEVATION
 - 2-A-106 BUNKBED 2-A SECTION 1
 - 2-A-107 BUNKBED 2-A SECTION 2
 - 2-A-108 BUNKBED 2-A SECTION 3
 - 2-A-109 BUNKBED 2-A SECTION 4

- 2-C1-300 2-C1
 - 2-C1-301 BUNKBED 2-C1 GA
 - 2-C1-302 BUNKBED 2-C1 FRONT ELEVATION
 - 2-C1-303 BUNKBED 2-C1 BACK ELEVATION
 - 2-C1-304 BUNKBED 2-C1 RIGHT ELEVATION
 - 2-C1-305 BUNKBED 2-C1 LEFT ELEVATION
 - 2-C1-306 BUNKBED 2-C1 SECTION 1
 - 2-C1-307 BUNKBED 2-C1 SECTION 2
 - 2-C1-308 BUNKBED 2-C1 SECTION 3
 - 2-C1-309 BUNKBED 2-C1 SECTION 4

- 2-C2-400 2-C2
 - 2-C2-402 BUNKBED 2-C2 FRONT ELEVATION
 - 2-C2-403 BUNKBED 2-C2 BACK ELEVATION
 - 2-C2-404 BUNKBED 2-C2 RIGHT ELEVATION
 - 2-C2-405 BUNKBED 2-C2 LEFT ELEVATION
 - 2-C2-406 BUNKBED 2-C2 SECTION 1
 - 2-C2-407 BUNKBED 2-C2 SECTION 2
 - 2-C2-408 BUNKBED 2-C2 SECTION 3
 - 2-C2-409 BUNKBED 2-C2 SECTION 4

- 2-P-000 PODS - TYPE 2P
 - 2-P-001 TYPE 2 - FRAME
 - 2-P-500 POD 2-P AXO
 - 2-P-501 POD 2-P GA
 - 2-P-502 POD 2-P FRONT ELEVATION
 - 2-P-503 POD 2-P BACK ELEVATION
 - 2-P-504 POD 2-P RIGHT ELEVATION
 - 2-P-505 POD 2-P LEFT ELEVATION
 - 2-P-506 POD 2-P SECTION 1
 - 2-P-507 POD 2-P SECTION 2
 - 2-P-508 POD 2-P SECTION 3
 - 2-P-509 POD 2-P SECTION 4

- 3-000 BUNKBEDS - TYPE 3
 - 3-001 TYPE 3 - FRAME
 - 3-002 TYPE 3 - SIGNAGE
 - 3-003 TYPE 3 - LED LIGHTS PLAN
 - 3-004 TYPE 3 - CURTAINS PLAN


- 3-A-600 3-A
 - 3-A-601 BUNKBED 3-A GA
 - 3-A-602 BUNKBED 3-A FRONT ELEVATION
 - 3-A-603 BUNKBED 3-A BACK ELEVATION
 - 3-A-604 BUNKBED 3-A RIGHT ELEVATION
 - 3-A-605 BUNKBED 3-A LEFT ELEVATION
 - 3-A-606 BUNKBED 3-A SECTION 1
 - 3-A-607 BUNKBED 3-A SECTION 2
 - 3-A-608 BUNKBED 3-A SECTION 3
 - 3-A-609 BUNKBED 3-A SECTION 4

- 3-B-700 3-B
 - 3-B-701 BUNKBED 3-B GA
 - 3-B-702 BUNKBED 3-B FRONT ELEVATION
 - 3-B-703 BUNKBED 3-B BACK ELEVATION
 - 3-B-704 BUNKBED 3-B RIGHT ELEVATION
 - 3-B-705 BUNKBED 3-B LEFT ELEVATION
 - 3-B-706 BUNKBED 3-B SECTION 1
 - 3-B-707 BUNKBED 3-B SECTION 2
 - 3-B-708 BUNKBED 3-B SECTION 3
 - 3-B-709 BUNKBED 3-B SECTION 4

4-000 LOCKERS

5-000 SPECS SHEET

CONCEPT VISUAL

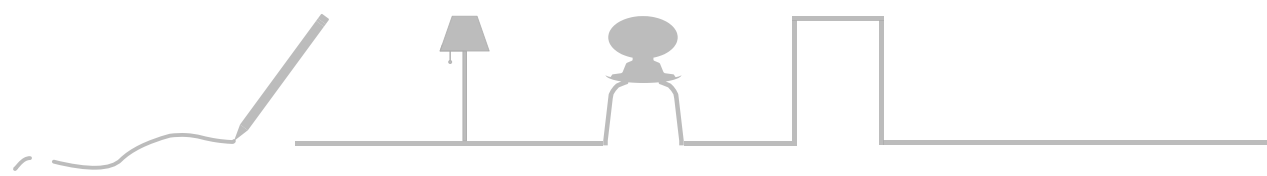


Stefanie Jaensch

INTERIOR DESIGNS


For



WALL COLOUR TBD

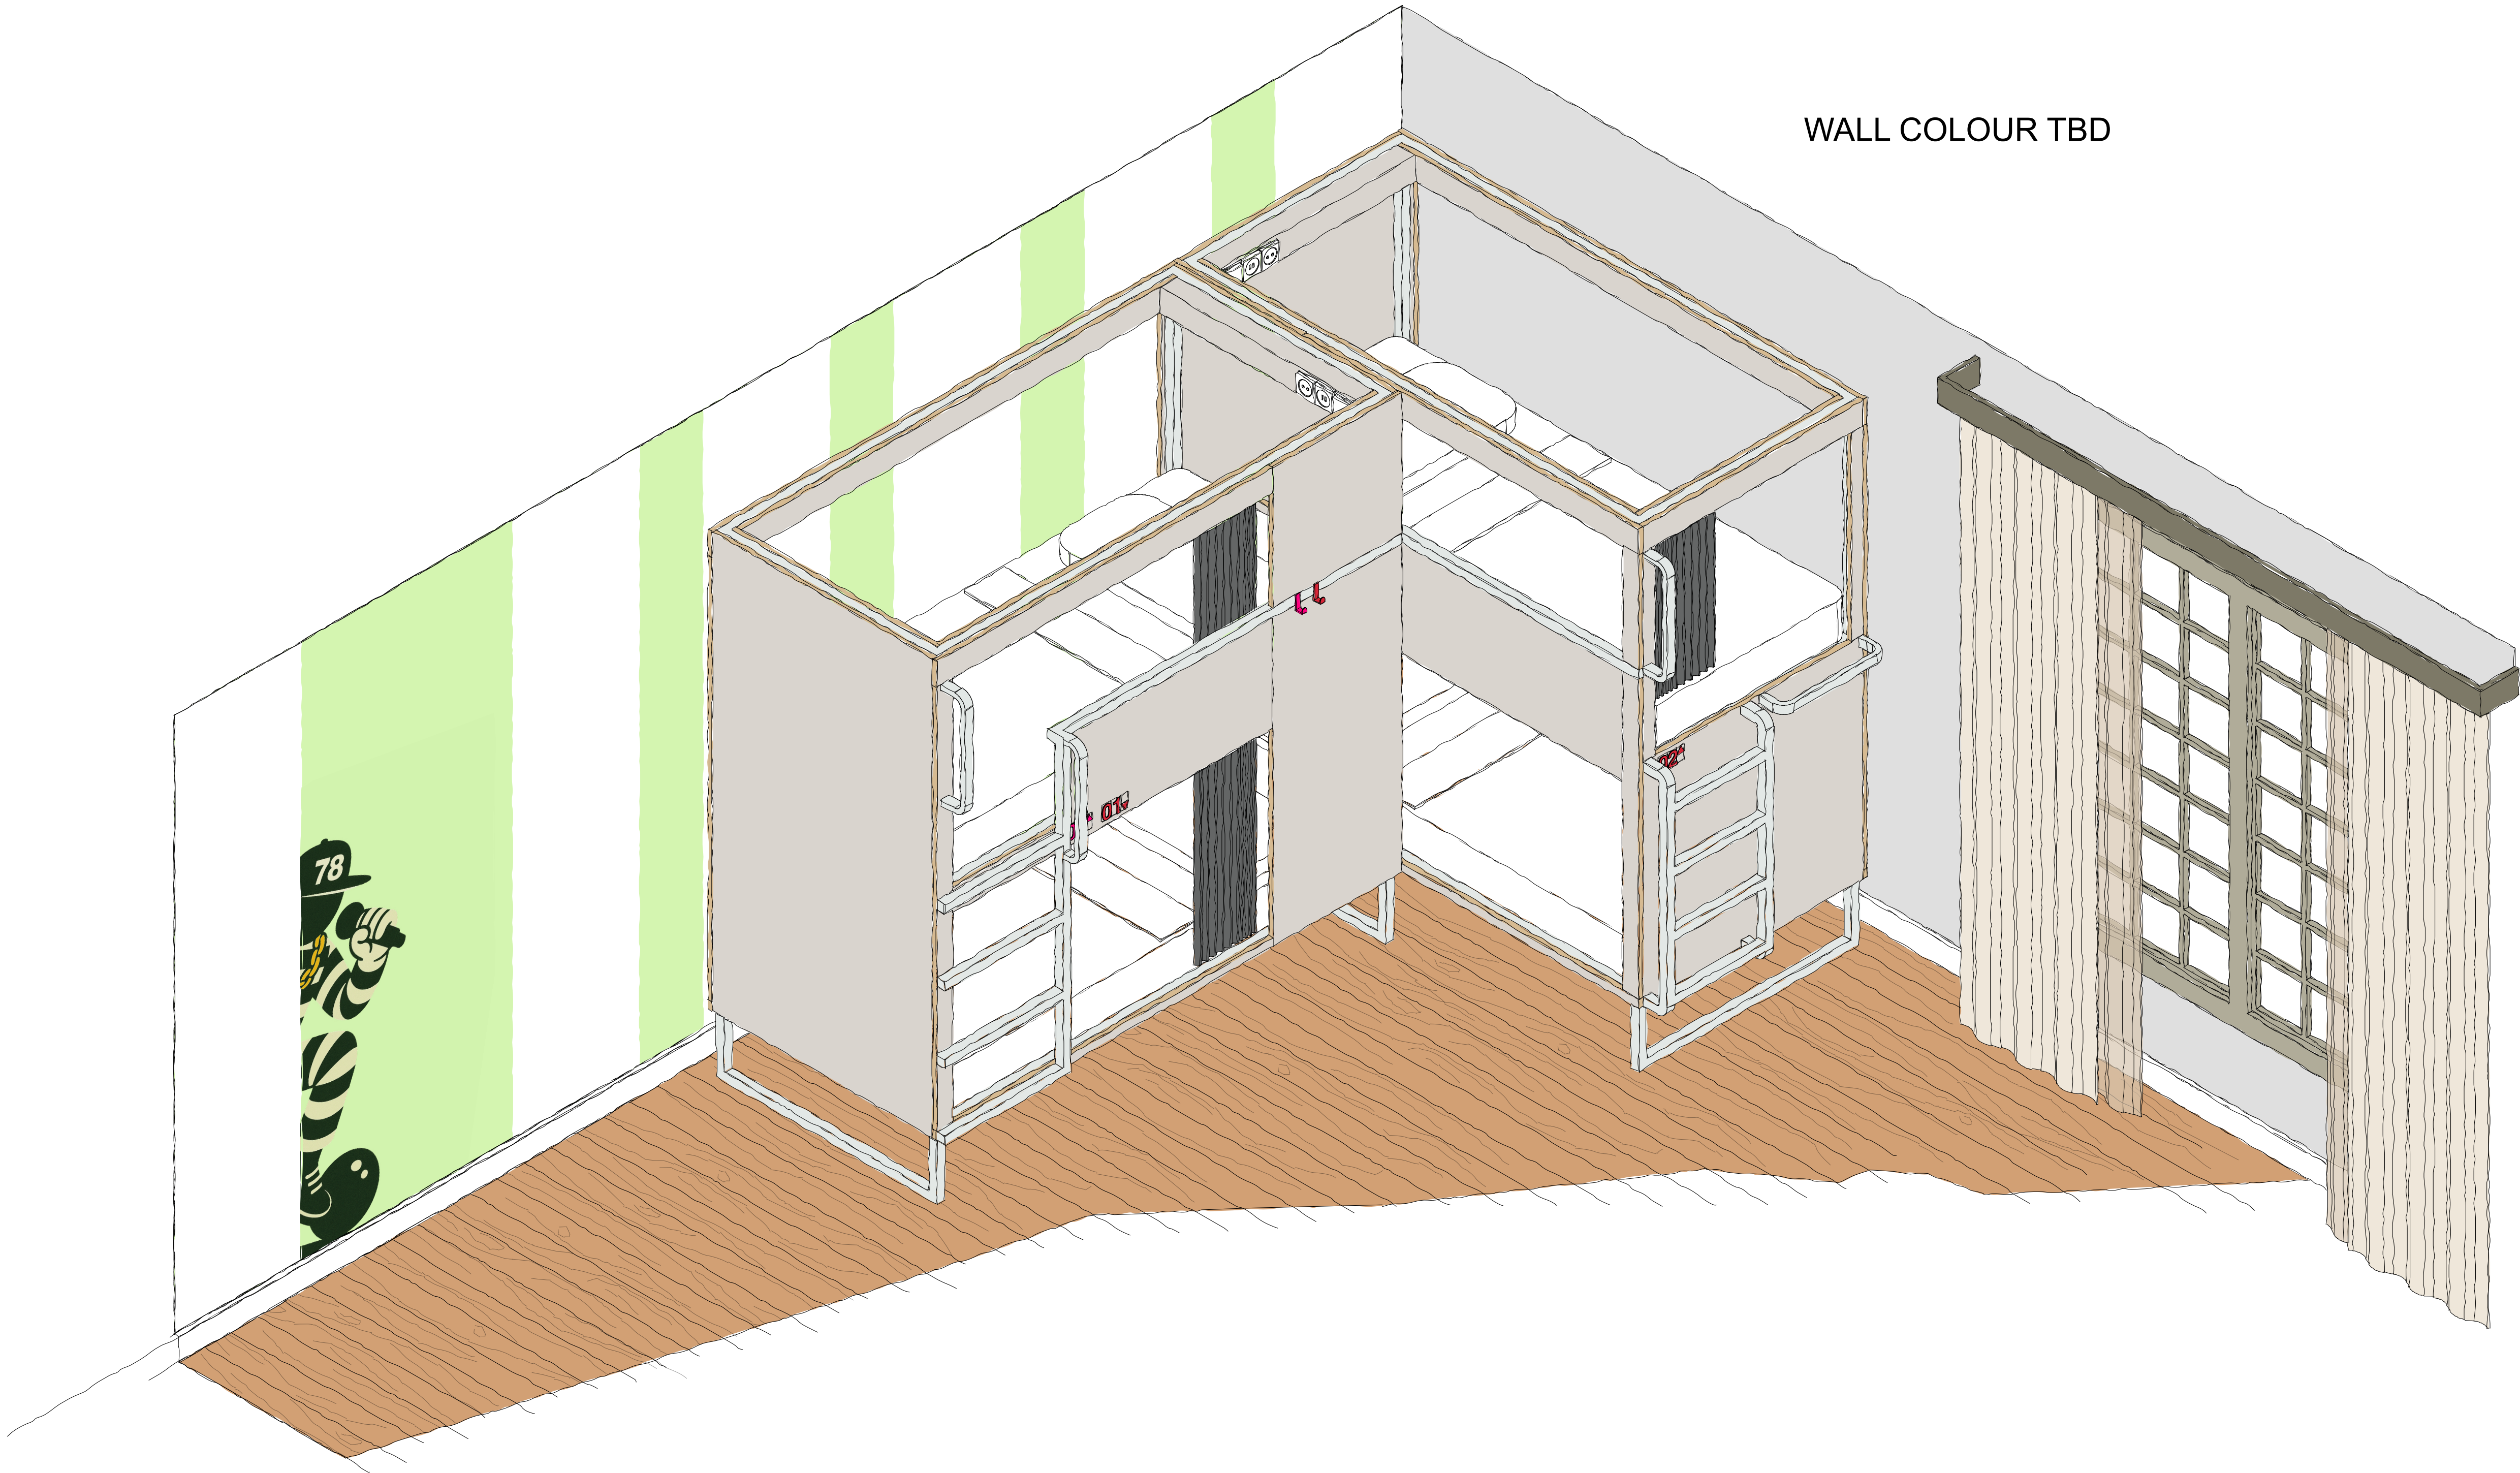


DRAFT

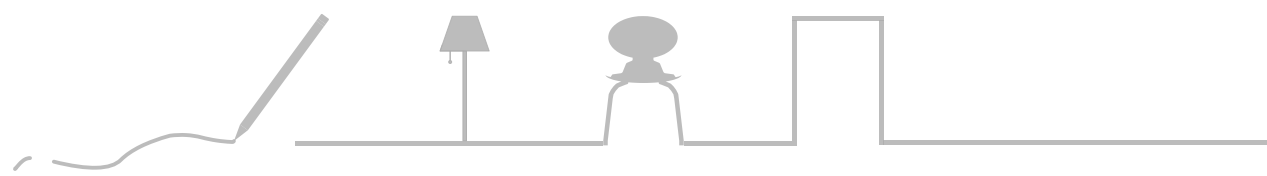

For




OVERVIEW - BED COUNTS

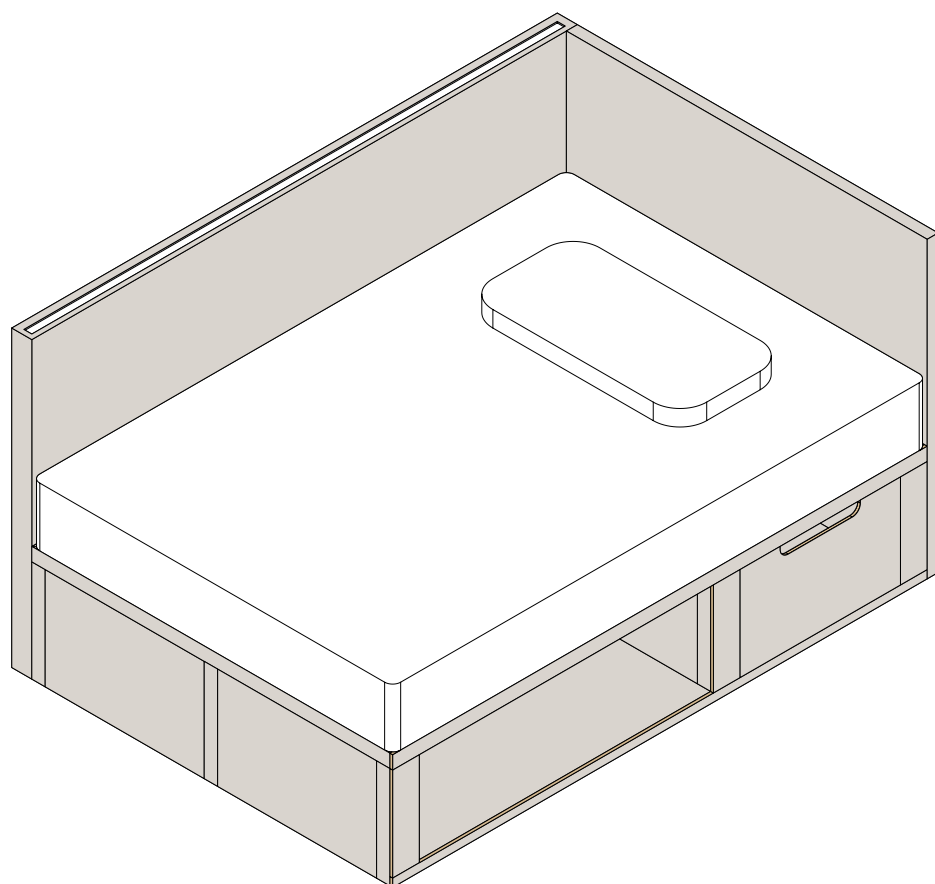


DOUBLE BED 1
QTY: 21

DOUBLE BEDS
142.5 x 204.1 x 110.5 (WxLxH)cm

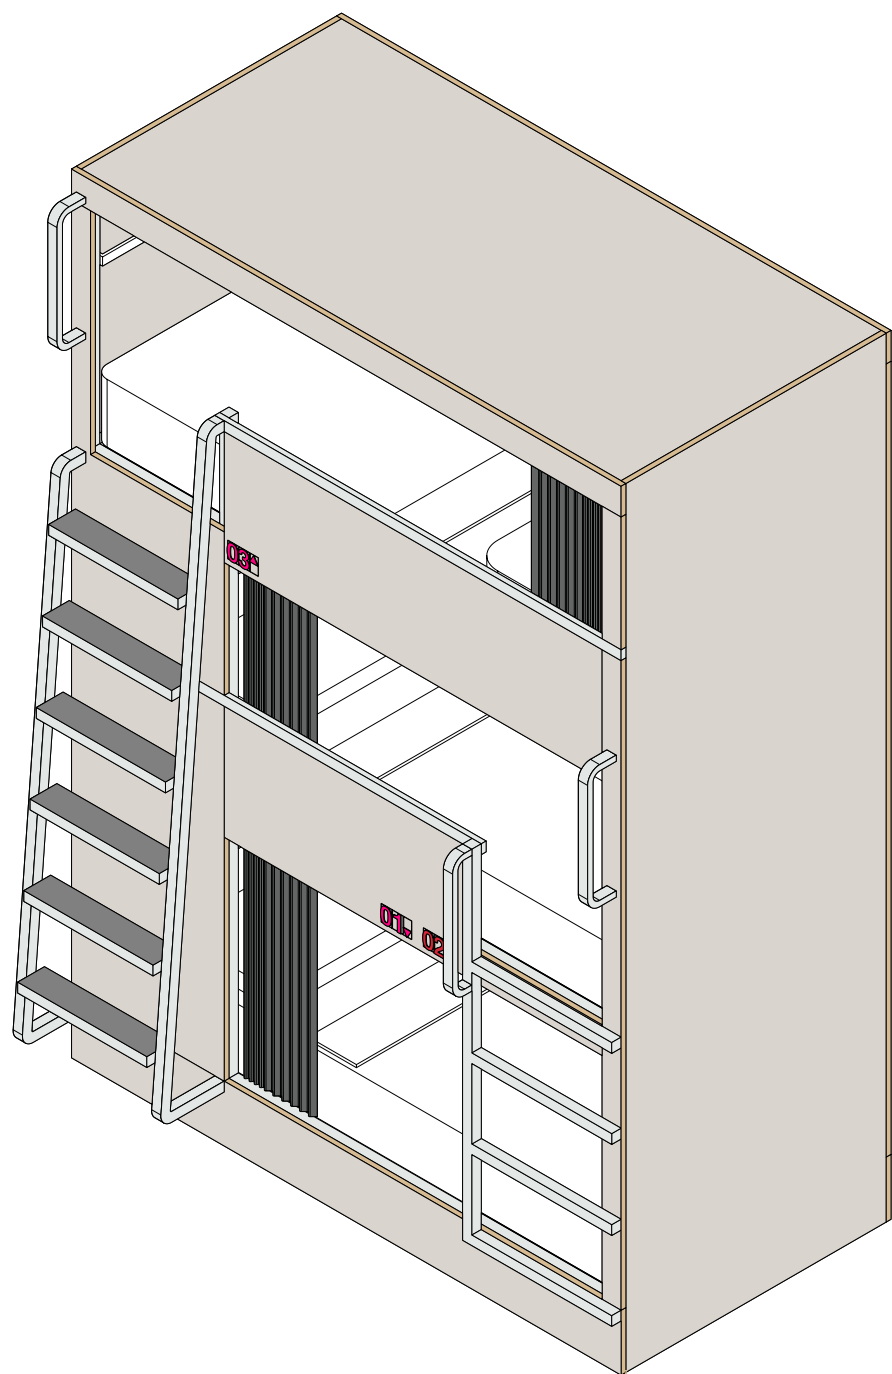


TRIPLE BUNKBED 3-A
QTY: 13

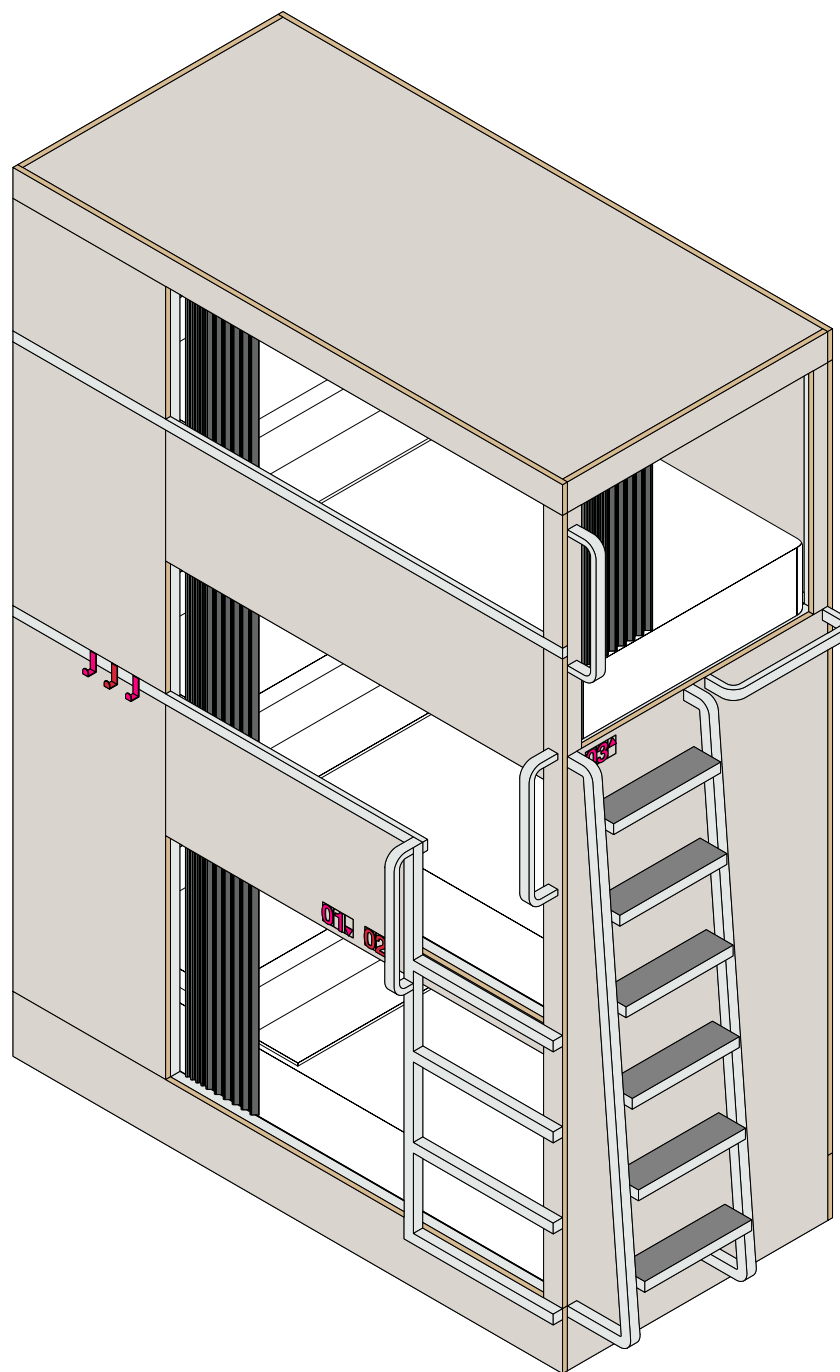


TRIPLE BUNKBED 3-B
QTY: 8


TRIPLE BUNKBEDS - TYPE 3
101 x 205.6 x 290.1 (WxLxH)cm

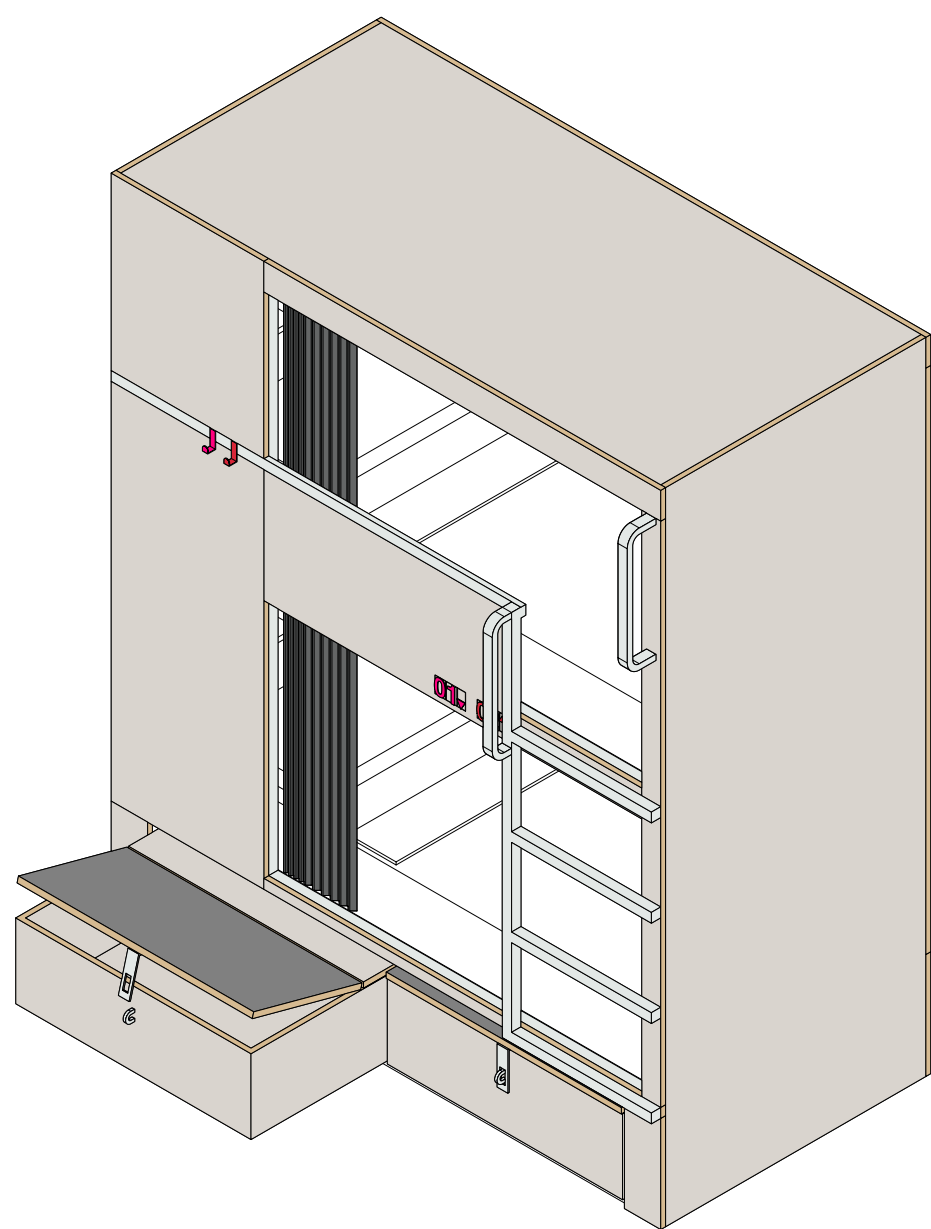


BUNKBED 2-A
QTY: 26

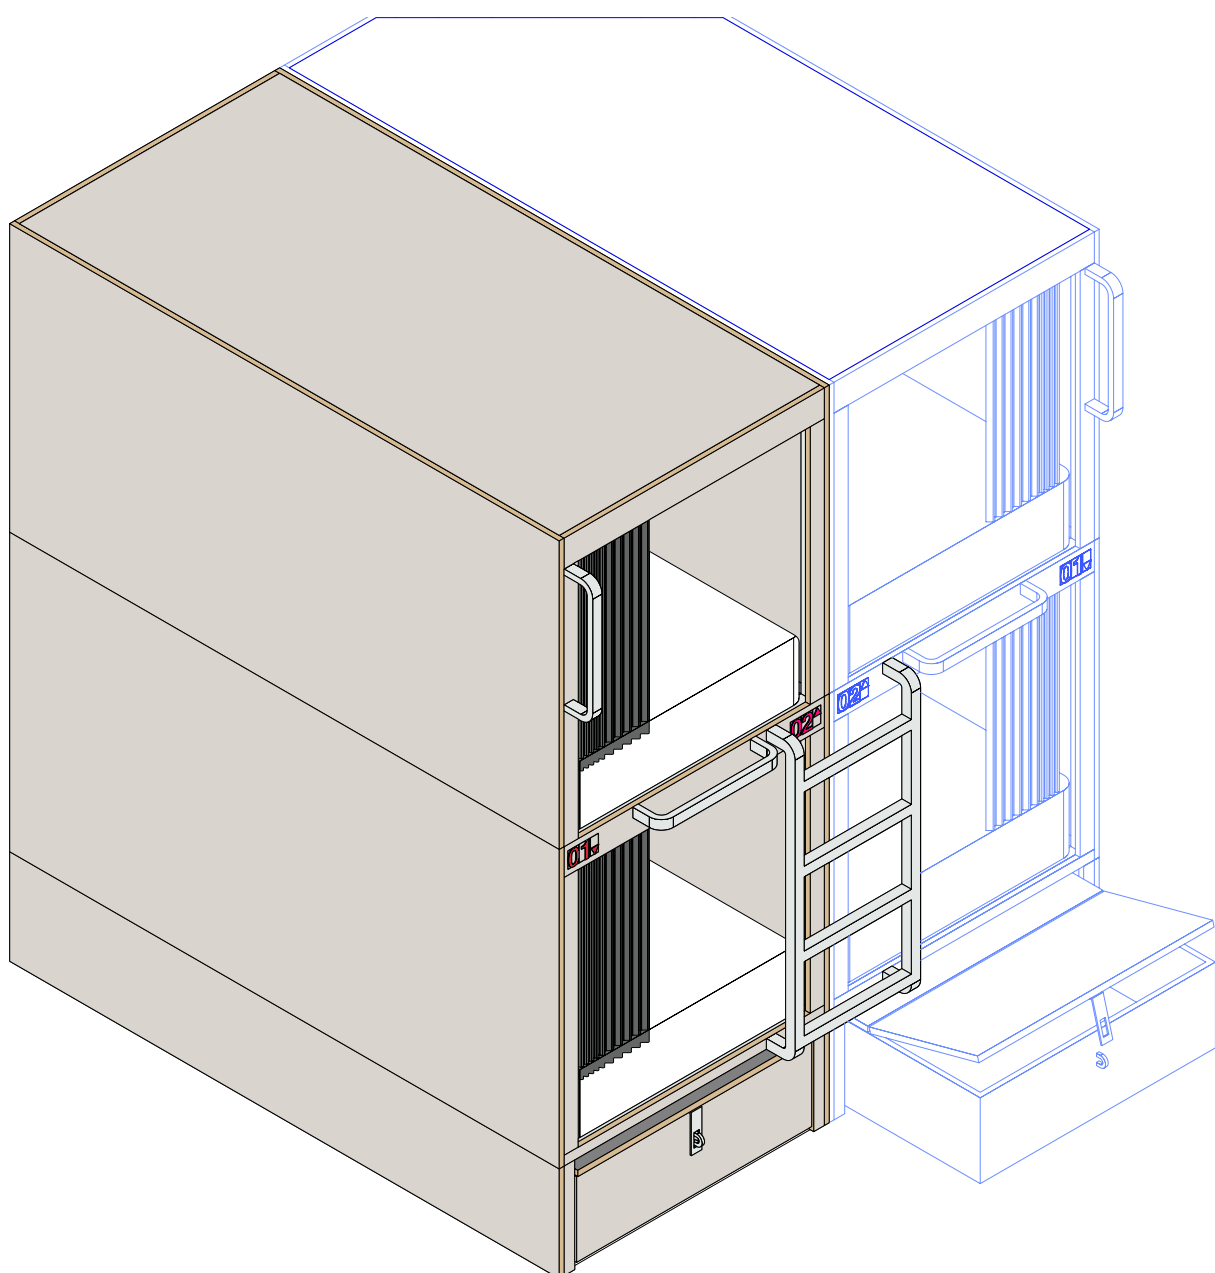

BUNKBED 2-C1
QTY: 150

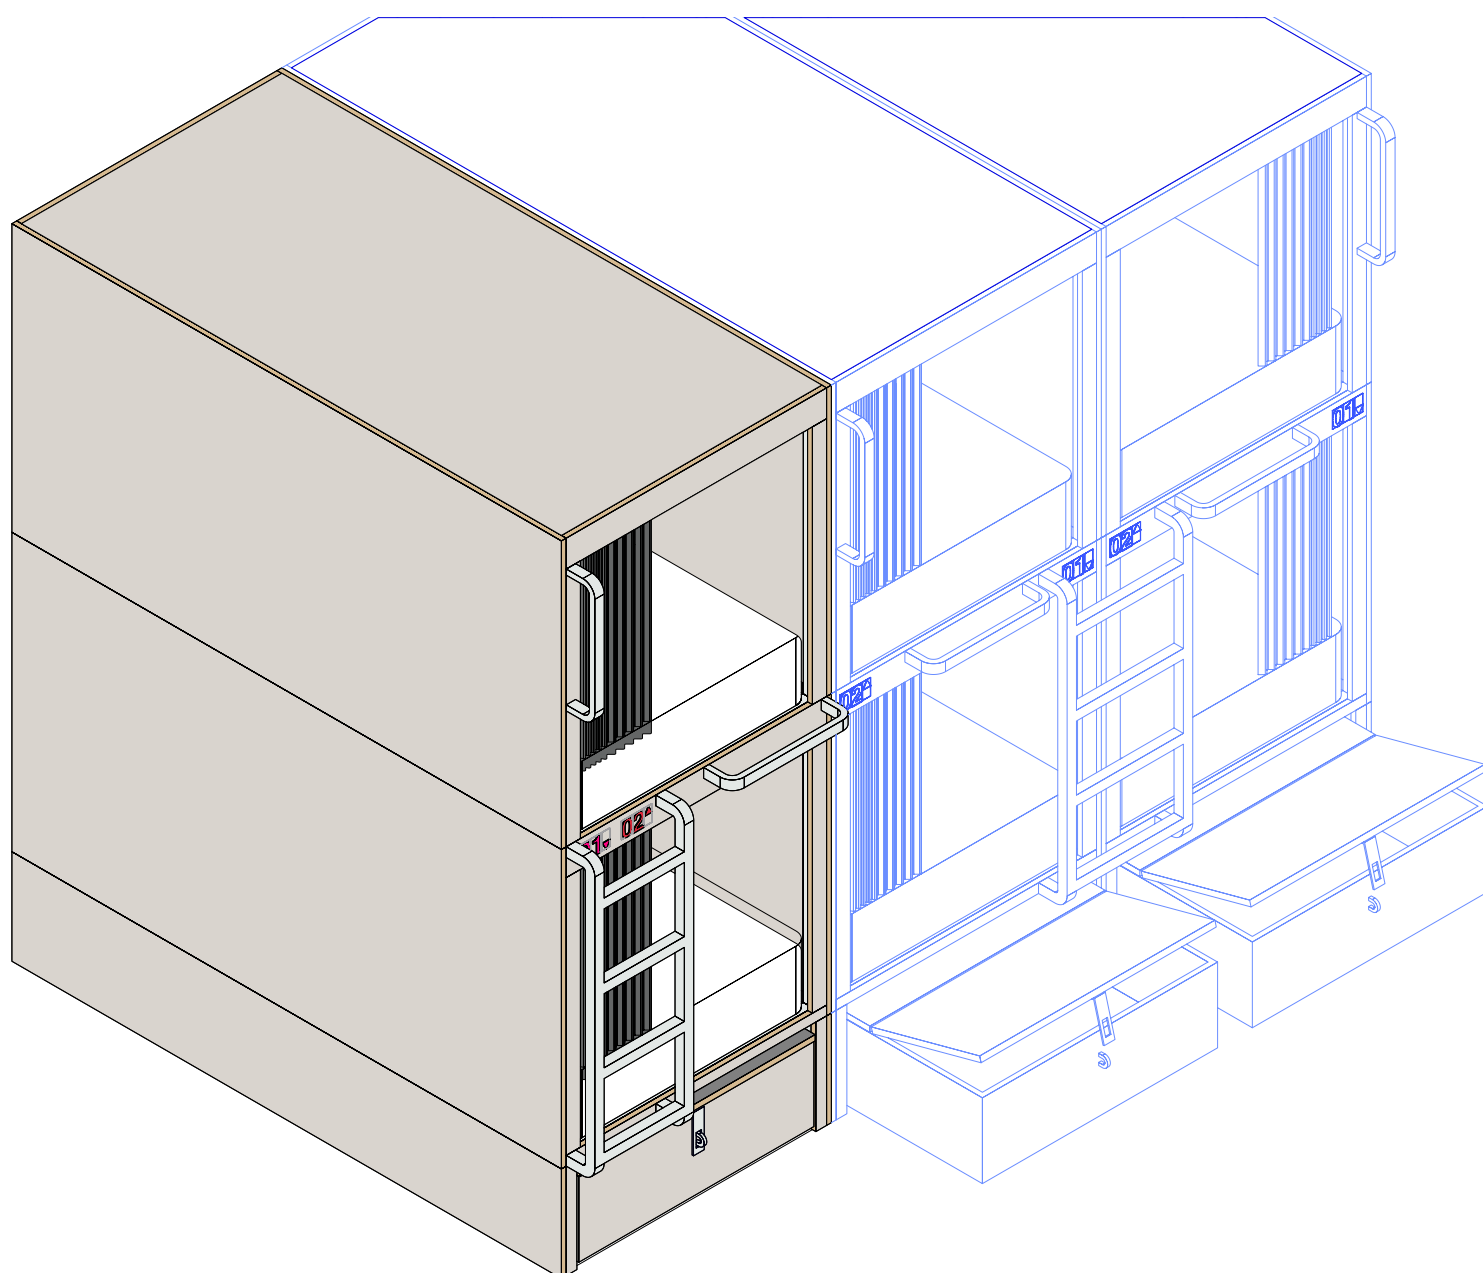

BUNKBED 2-C2
QTY: 42

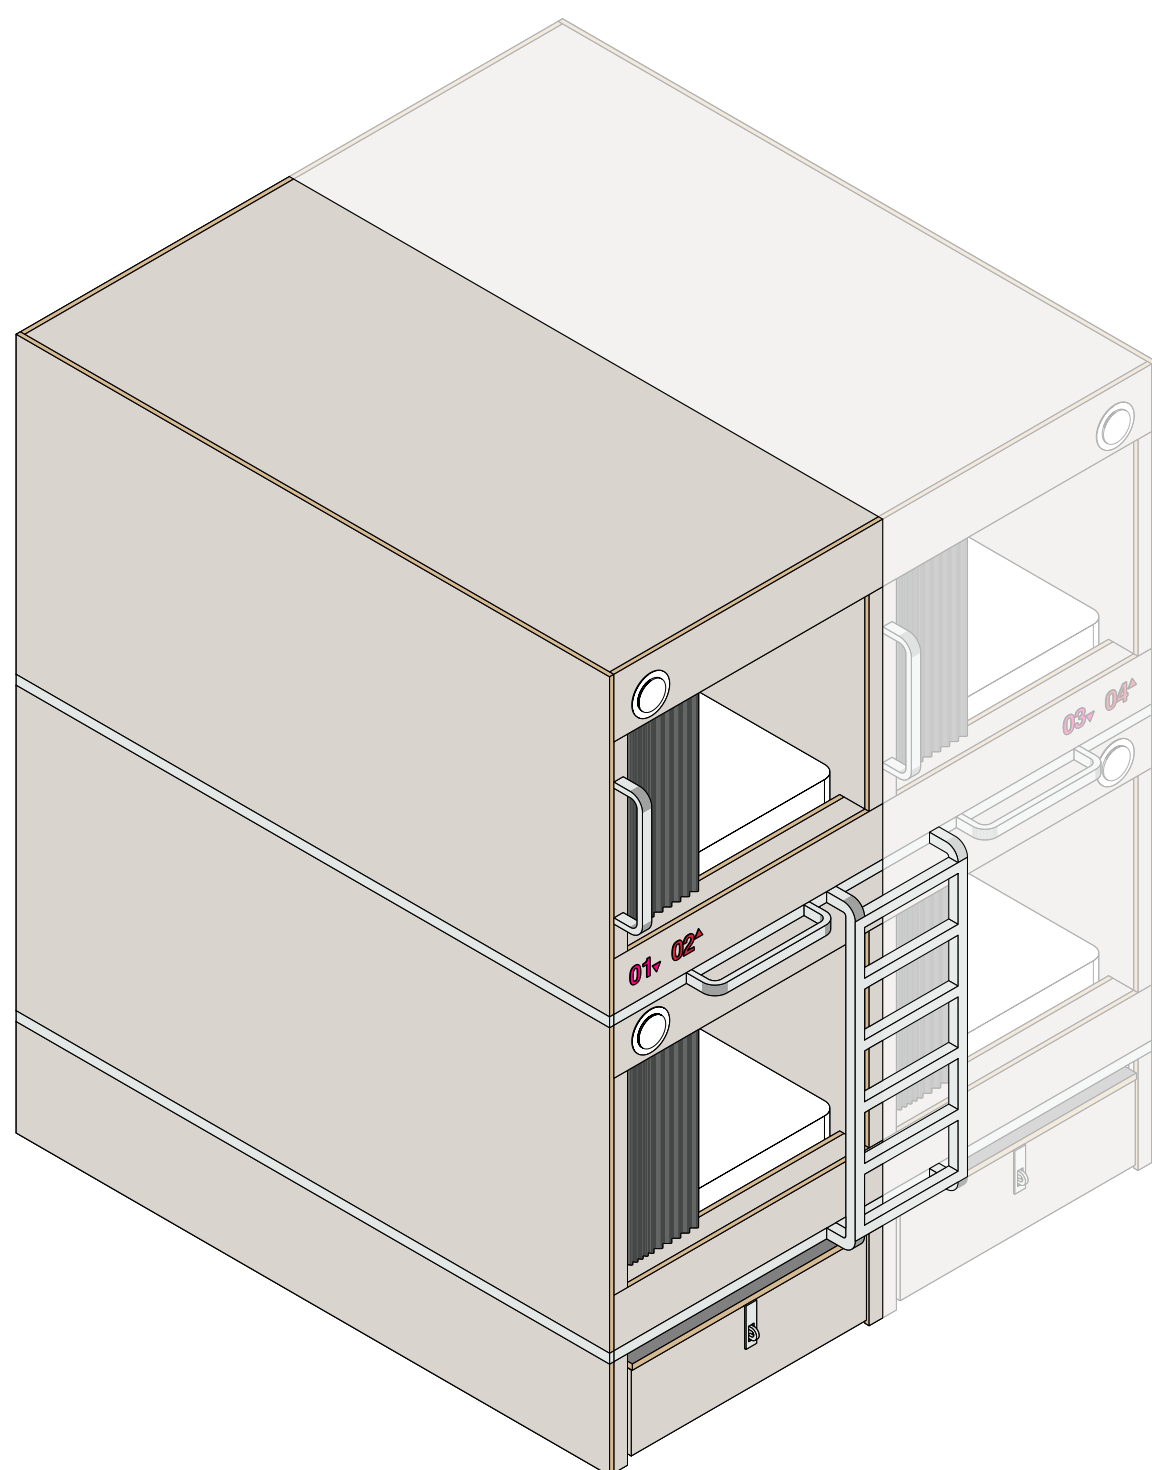


POD 2-P
QTY: 36

BUNKBEDS - TYPE 2
101 x 205.6 x 241.6 (WxLxH)cm

POD - TYPE 2-P
102.2 x 222 x 259.3 (WxLxH)cm

DRAFT

DOUBLE BEDS

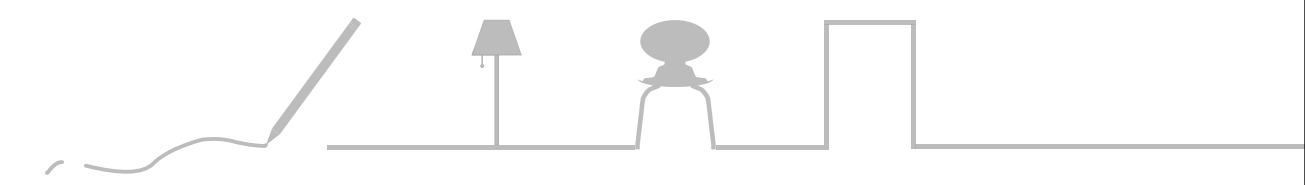

Stefanie Jaensch


INTERIOR DESIGNS

For

CLiNK
HOSTELS


DOUBLE BEDS

THE
ORDER

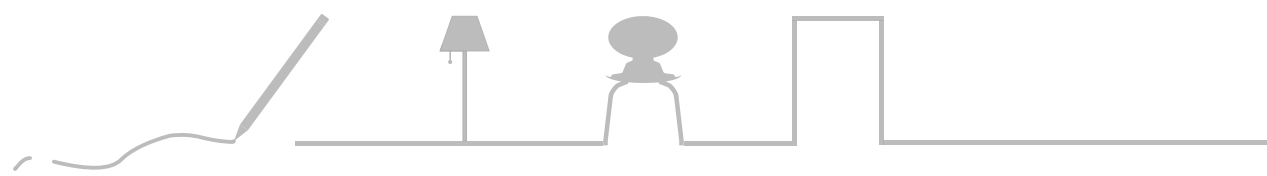

DOUBLE BED

For

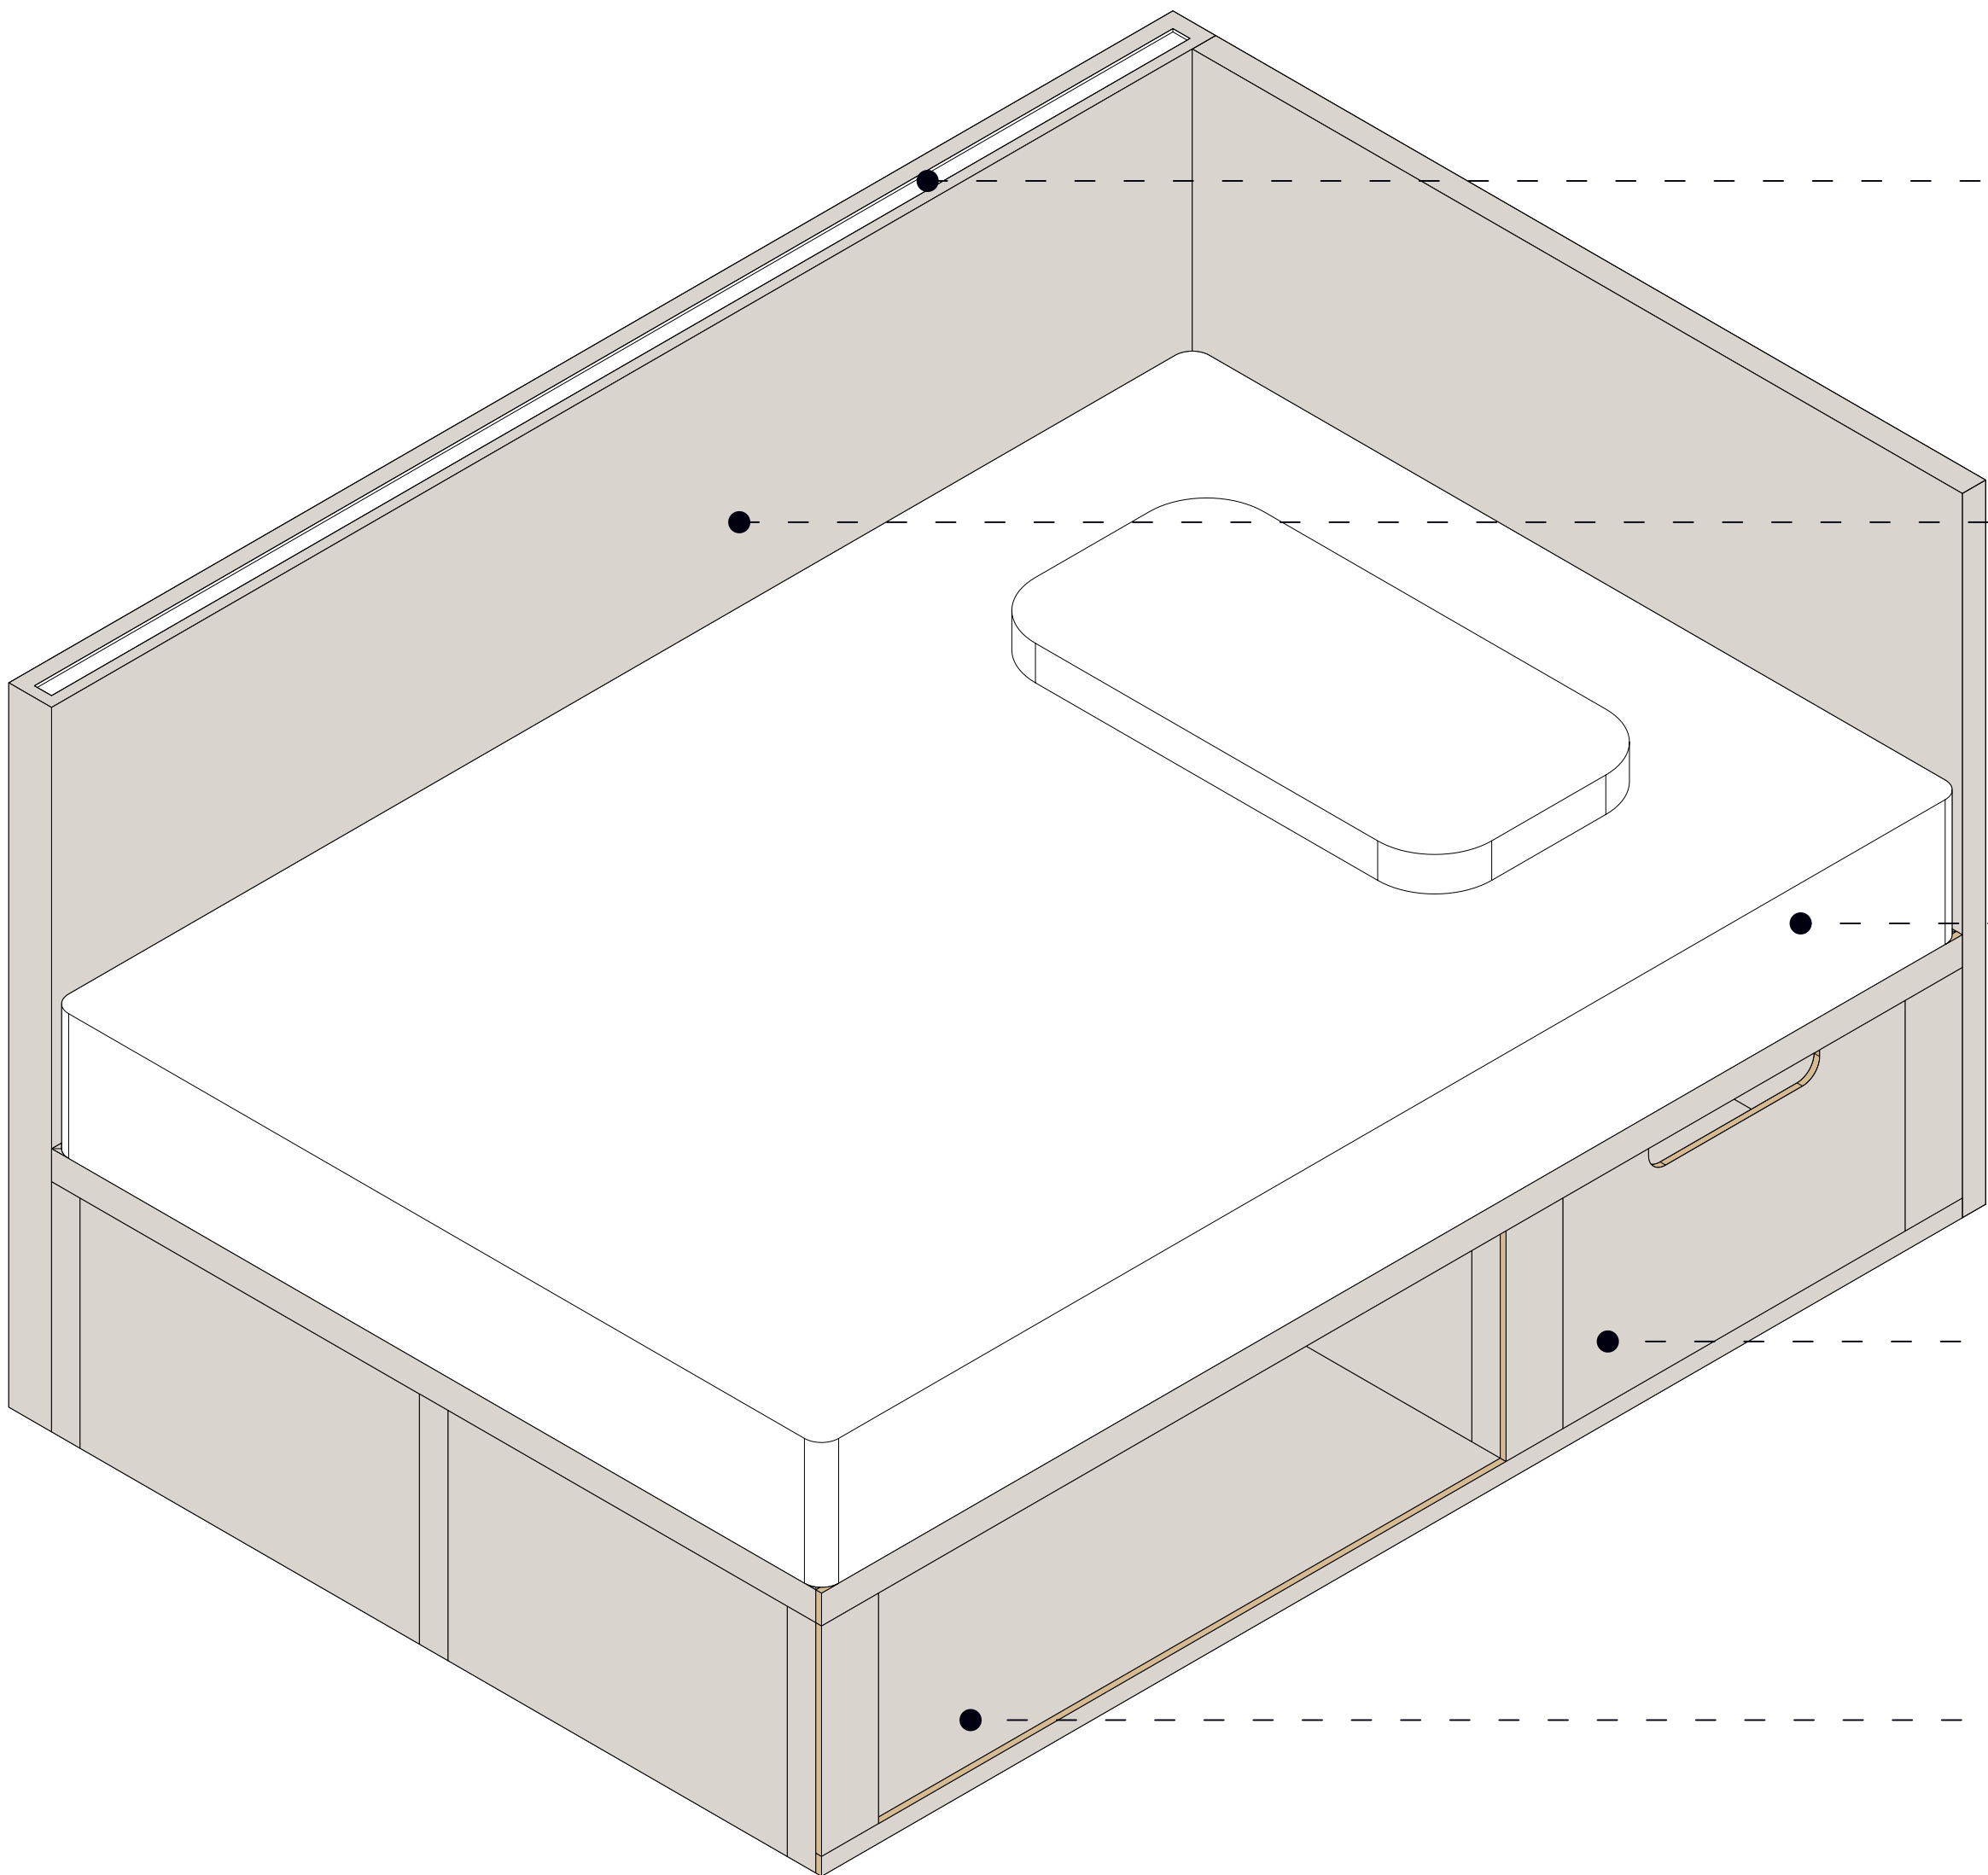

EE-L02
LED light with light diffuser - LED stripes - 2000 Calvin - Warmwhite

CC-M01
Cladding - Laminated chipboard - Colour RAL 7044, (FINAL RAL Colour TBC by Clink) - Thickness 16m

FF-M01
Mattress - 90x200x22cm - (Foam Mattress - Fire retardant fabric and foam (Crib 5) - 100gr/m2 polyester - Reinforcement - Cover should be washable on 40 degrees) FINAL MATTRESS HEIGHT TBC (18/20/22cm)


CC-M01
Drawer - Laminated chipboard - Colour RAL 7044, (FINAL RAL Colour TBC by Clink) - Thickness 16m

Storage


DIMENSIONS

142.5 x 204.1 x 110.5 (WxLxH)cm

DOUBLE BED - DB1 - GA PLANS

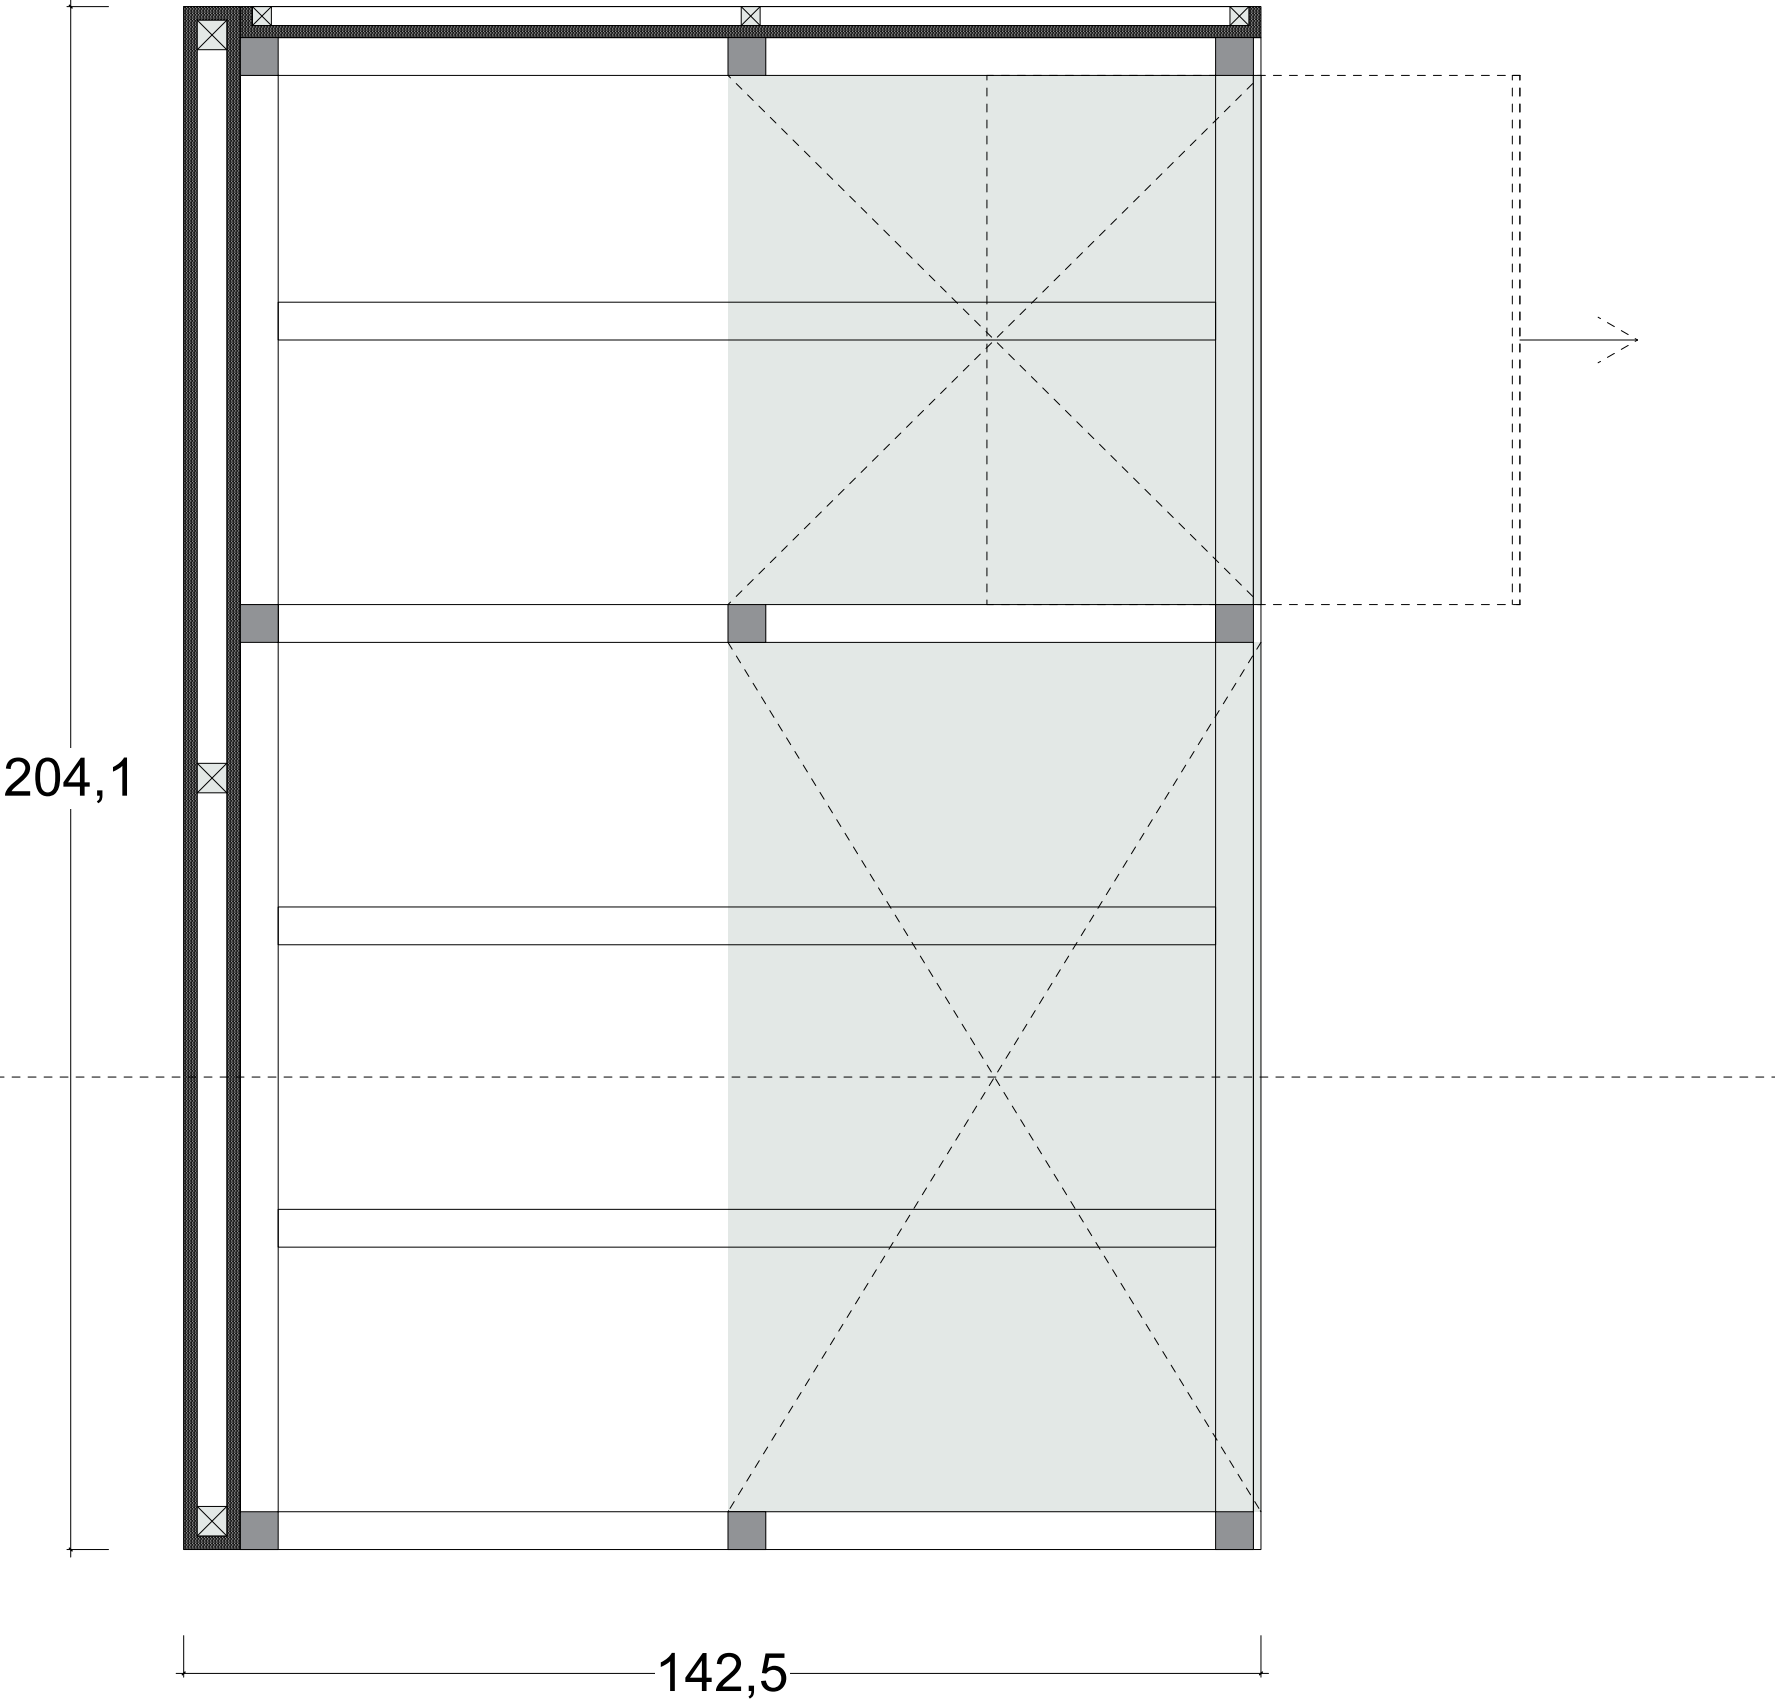


Top view

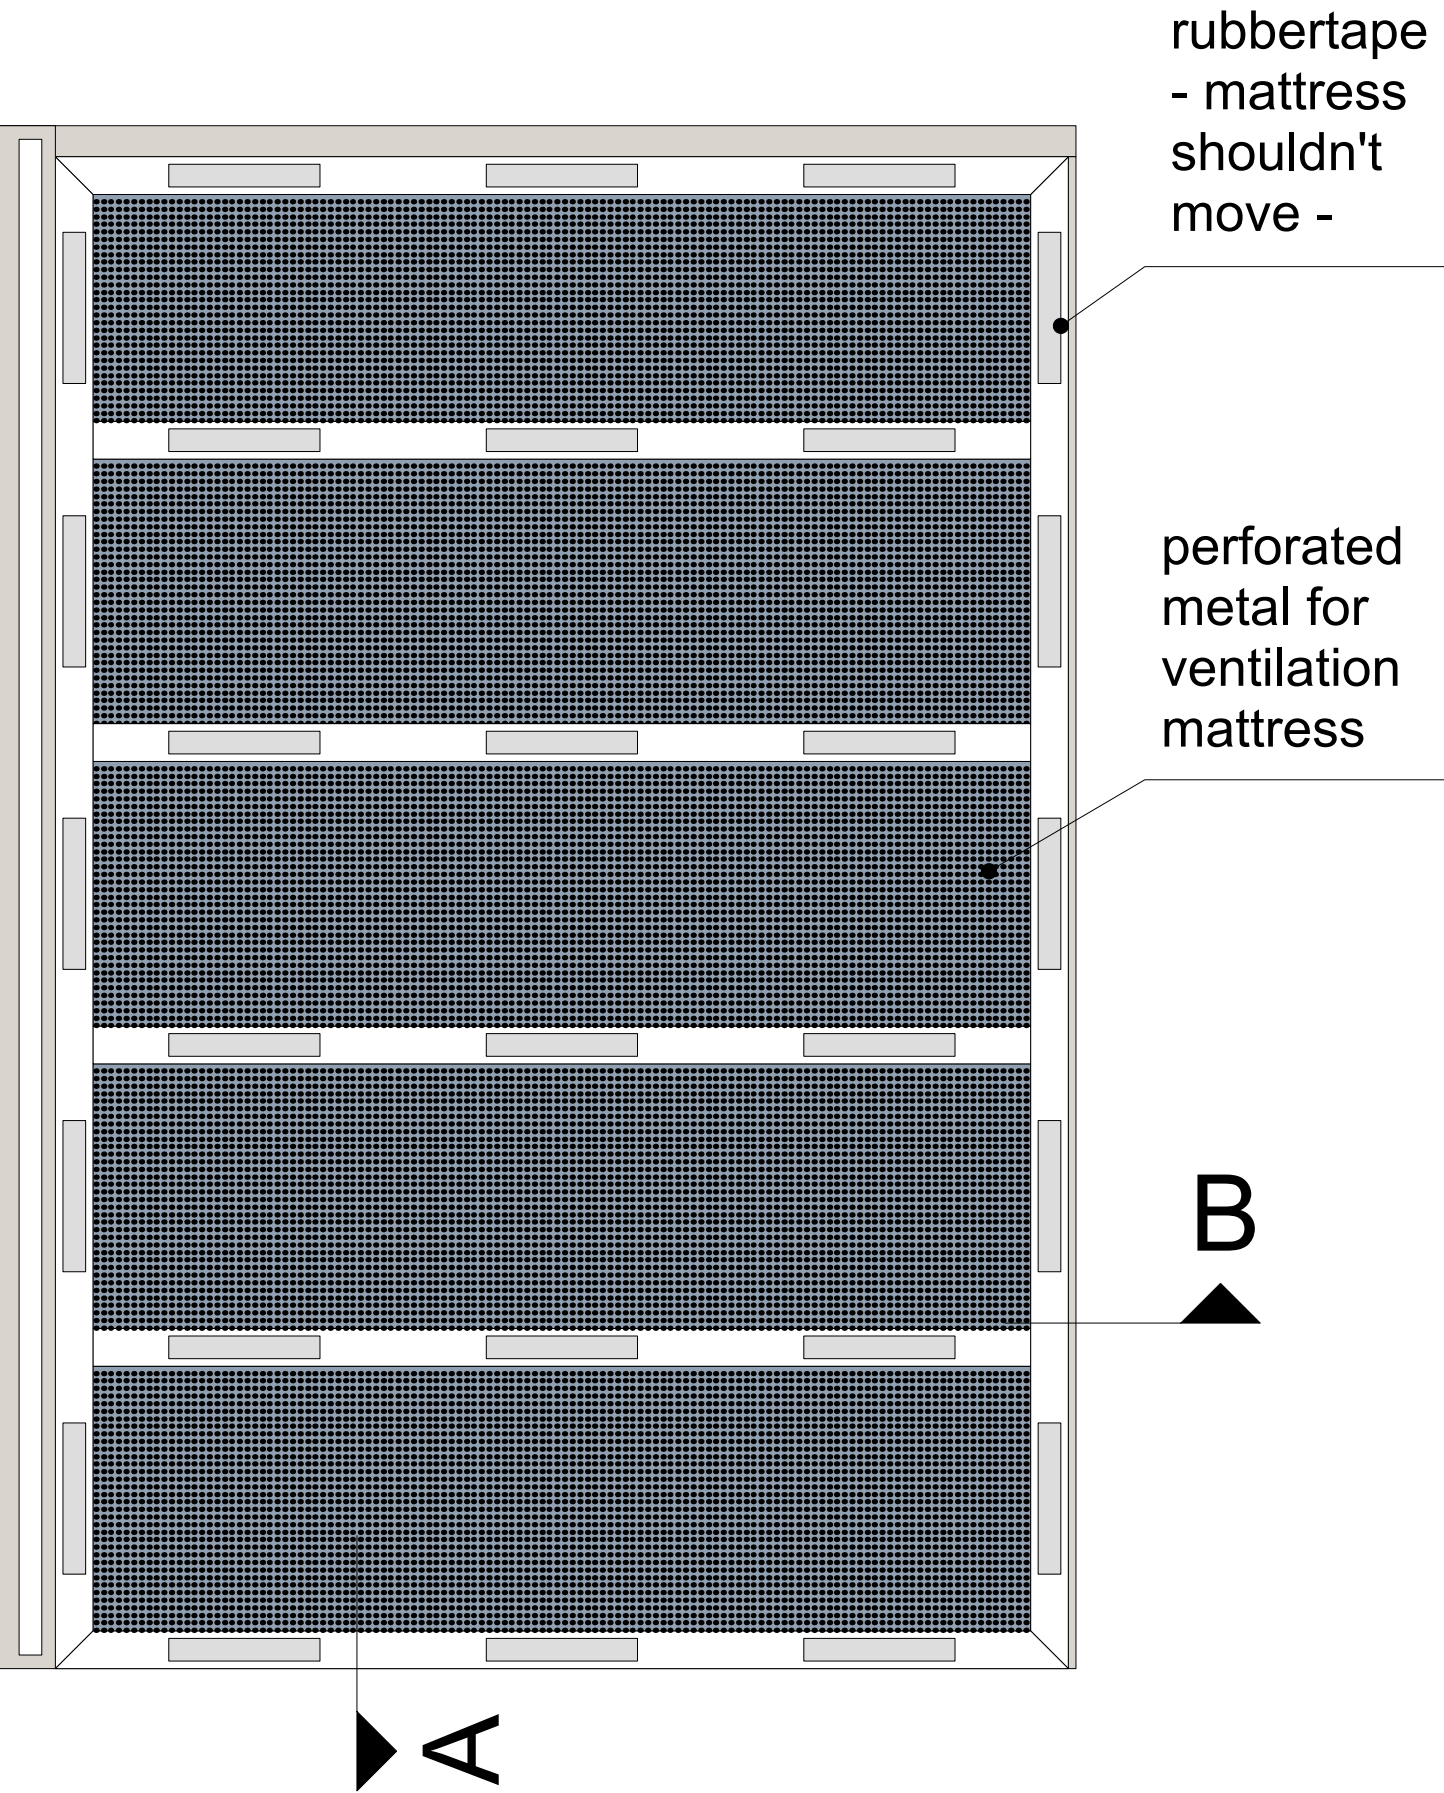


Material & description
Bed frame Steel powder coat Colour TBD
Double Bed DB-1

**Please note that construction of one bed must be very stable and be able to carry more than 150kg per bed. If necessary an additional leg in the center of the bed is okay for stability and construction reasons*


Frontview

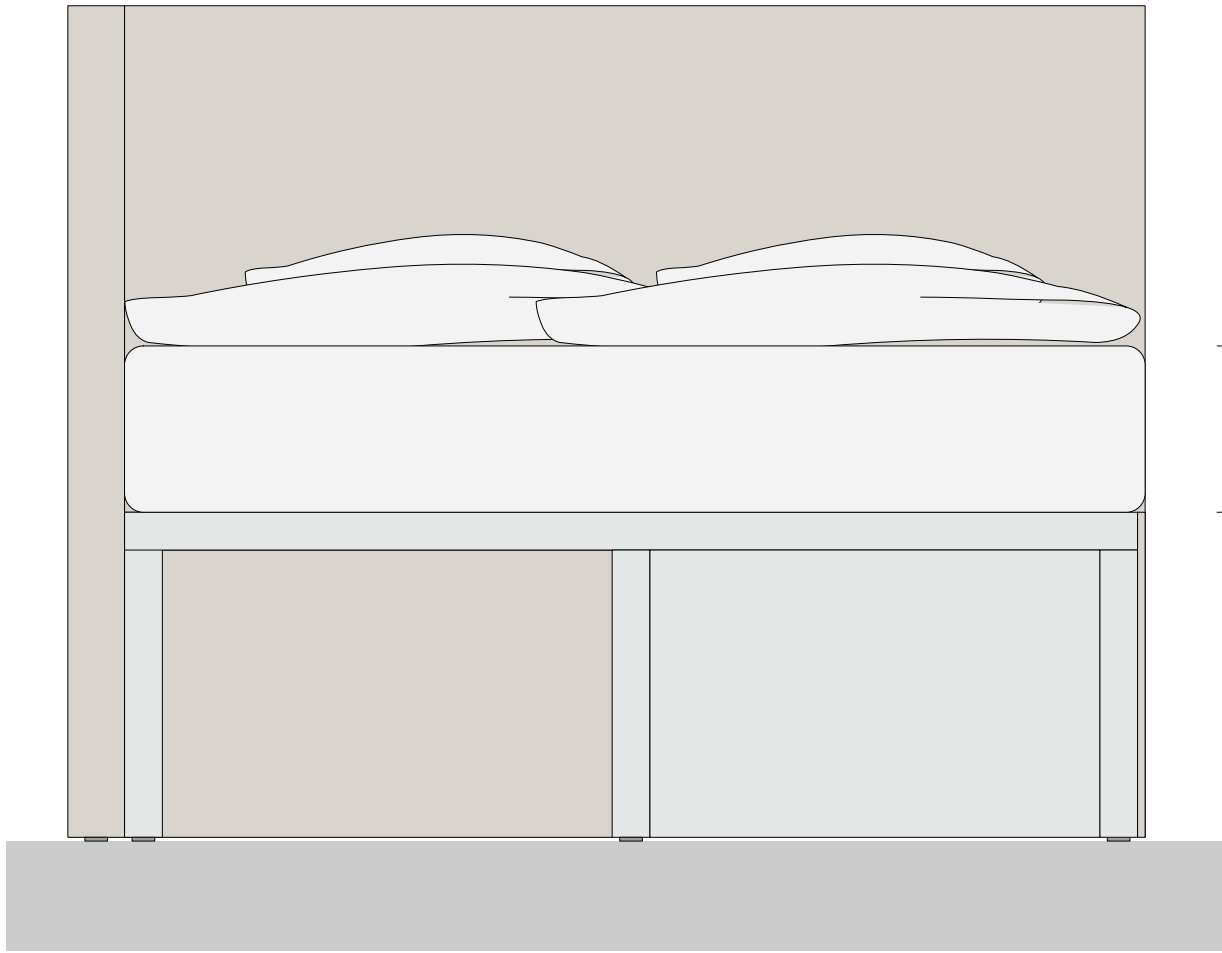


Side view

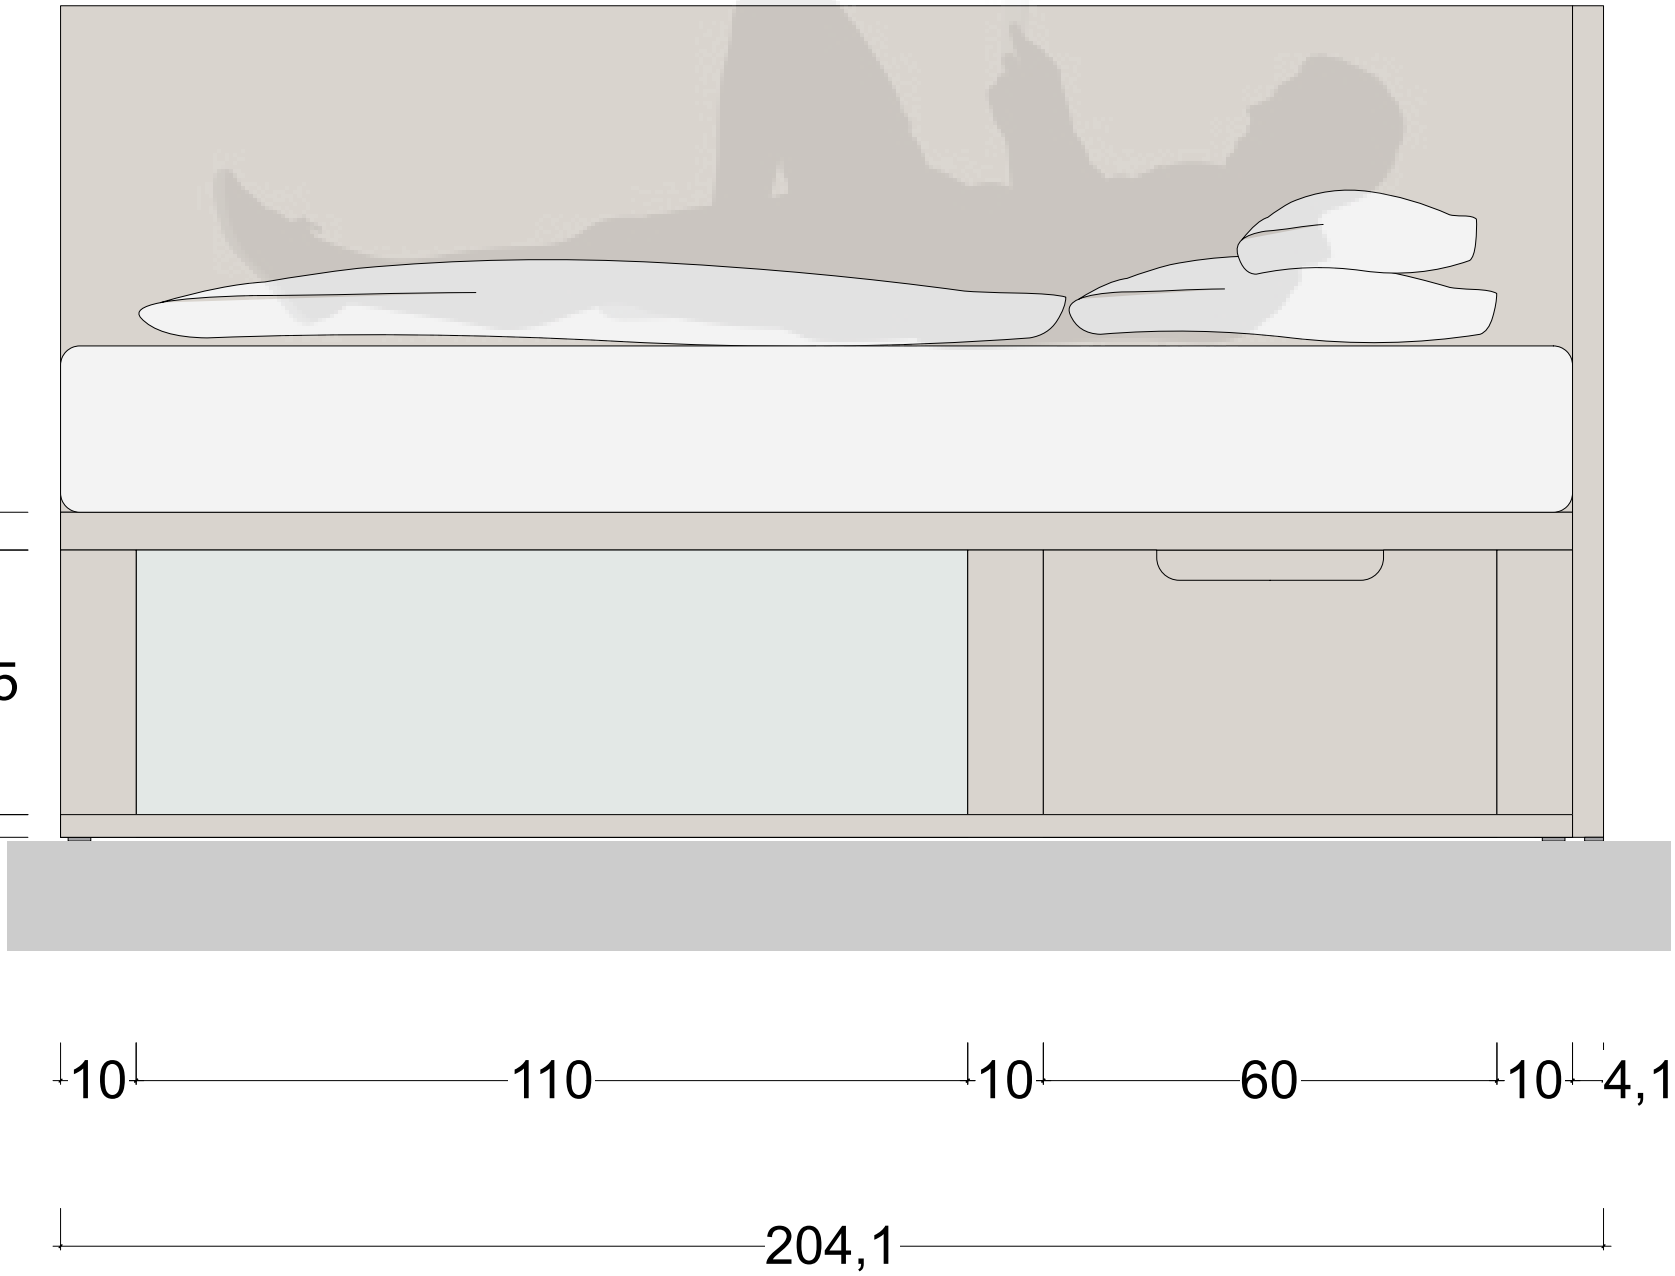

Section B

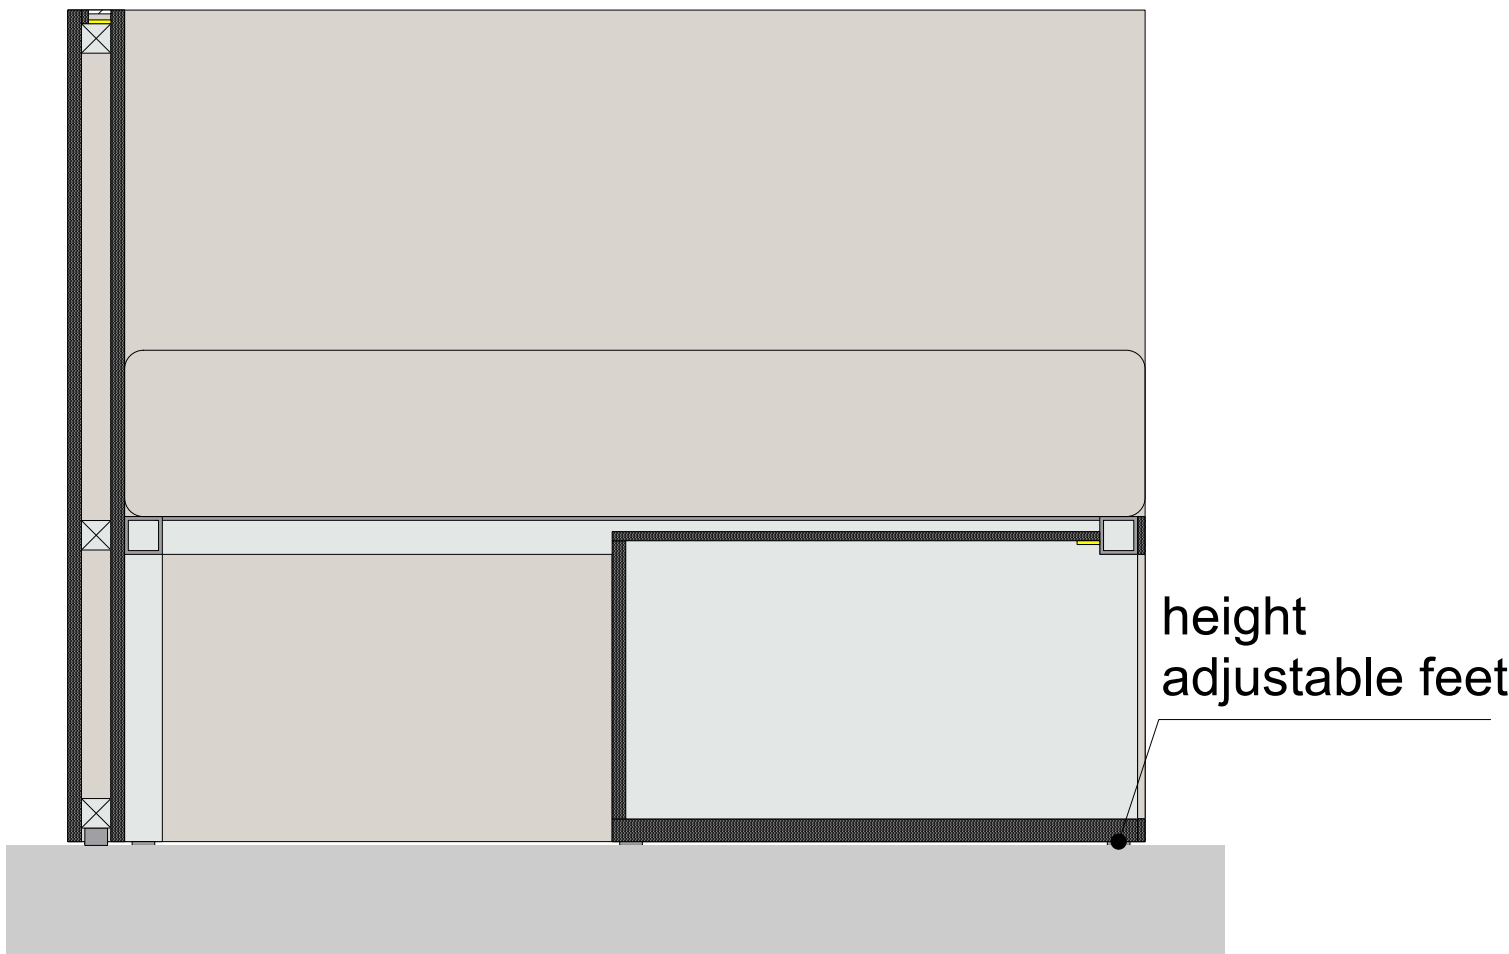

Section A

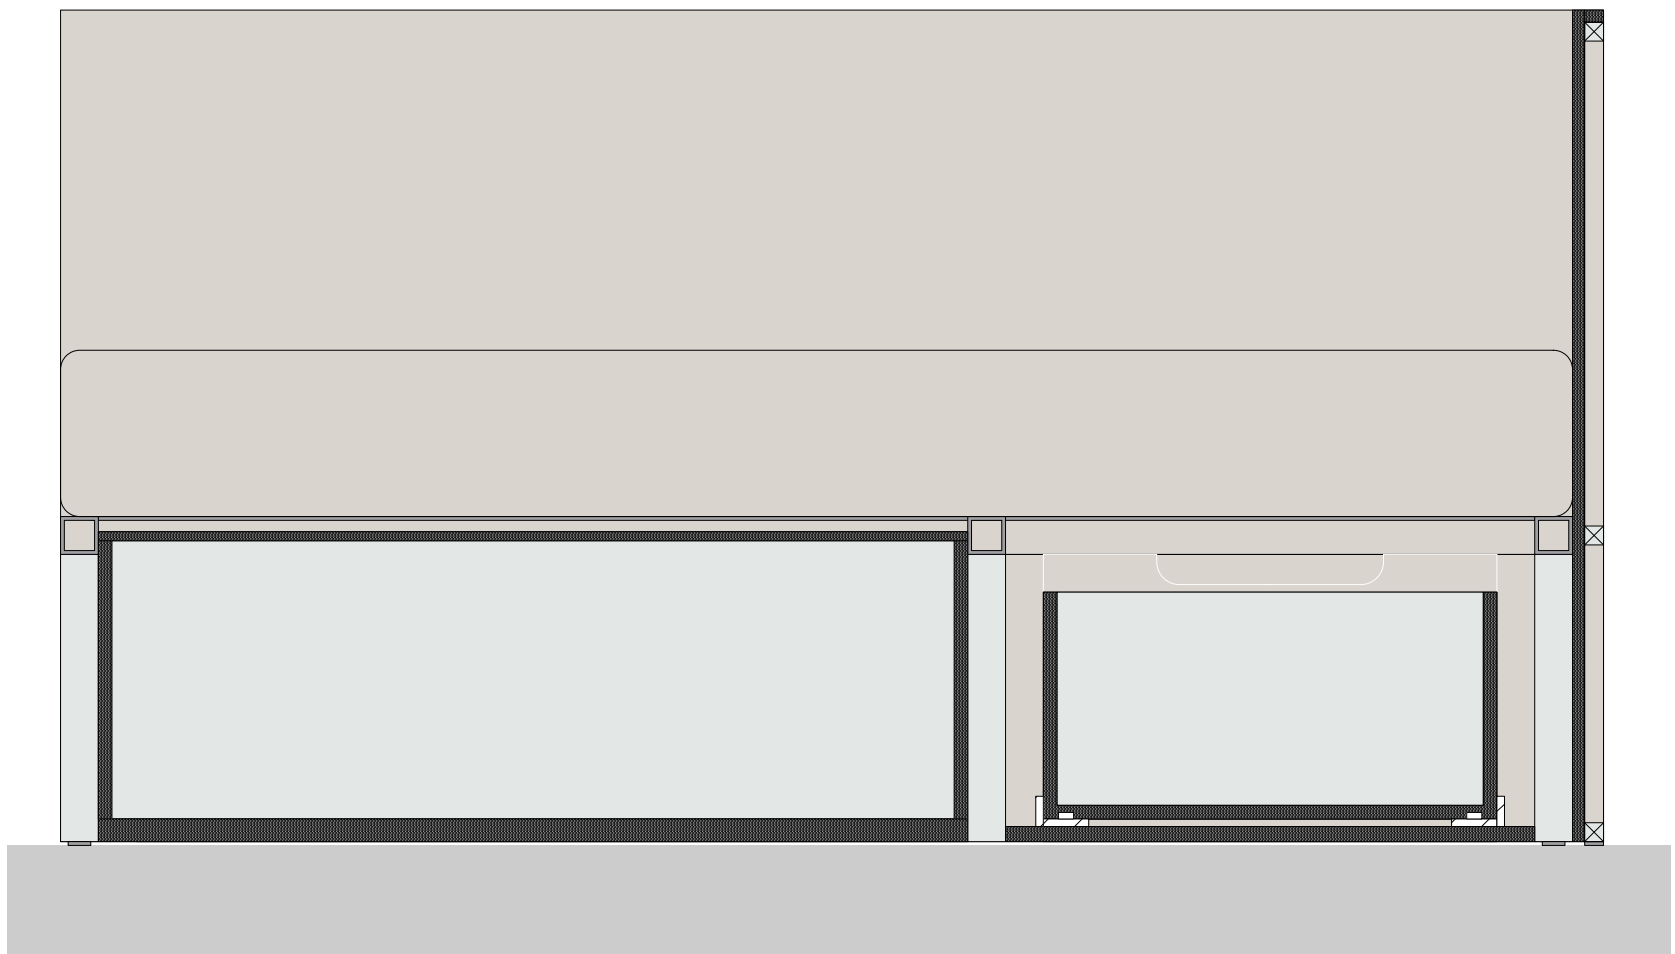

KEY

Index

A) 04.05.2026 Plan Set UP

All measurements have to be verified according to existing conditions by the contractor! Discrepancies must be reported immediately to the responsible project manager. The contractor has to produce fully dimensioned shop drawings prior to the start of the contract and they have to be approved by the client/ investor / interior designer

Project

CLINK 78 - BEDS

Logo



Project Address

CLINK 78
78 King's Cross Rd
London WC1X 9QG
United Kingdom

Client's Address


CLINK 78
78 King's Cross Rd
London WC1X 9QG
United Kingdom

Sheet Number	1-DB1-110	Total Sheets	82
Sheet Title	DOUBLE BED - DB GA	Level	
File Name	260426_CLINK 78_BEDs AA DRAFT 03.vwx		

Date	Sheet Size	Scale	Signed
10.04.26	A1	1:10	AA

Stefanie Jaensch INTERIOR DESIGNS

Global Headquarter | Stefanie Jaensch c/o WeWork
Taubusanlage 8 | 60329 Frankfurt a.M.
E-Mail info@stefaniejaensch.de | DE +49 (0) 174 6756098
www.stefaniejaensch.de
Legal address | Stefanie Jaensch | Offenbacher Landstraße 434 | 60599 Frankfurt a.M.
© 2023 All Rights Reserved | Stefanie Jaensch

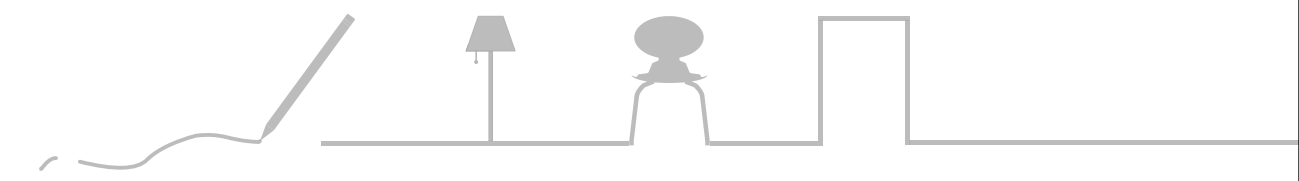

For




BUNKBEDS

TYPE 2

TEARAW


BUNKBEDS TYPE 2

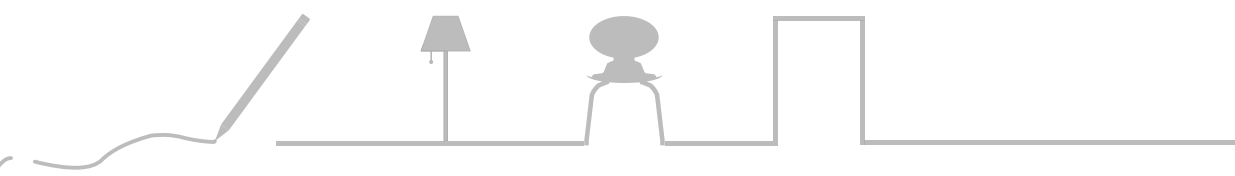

Stefanie Jaensch

INTERIOR DESIGNS


For

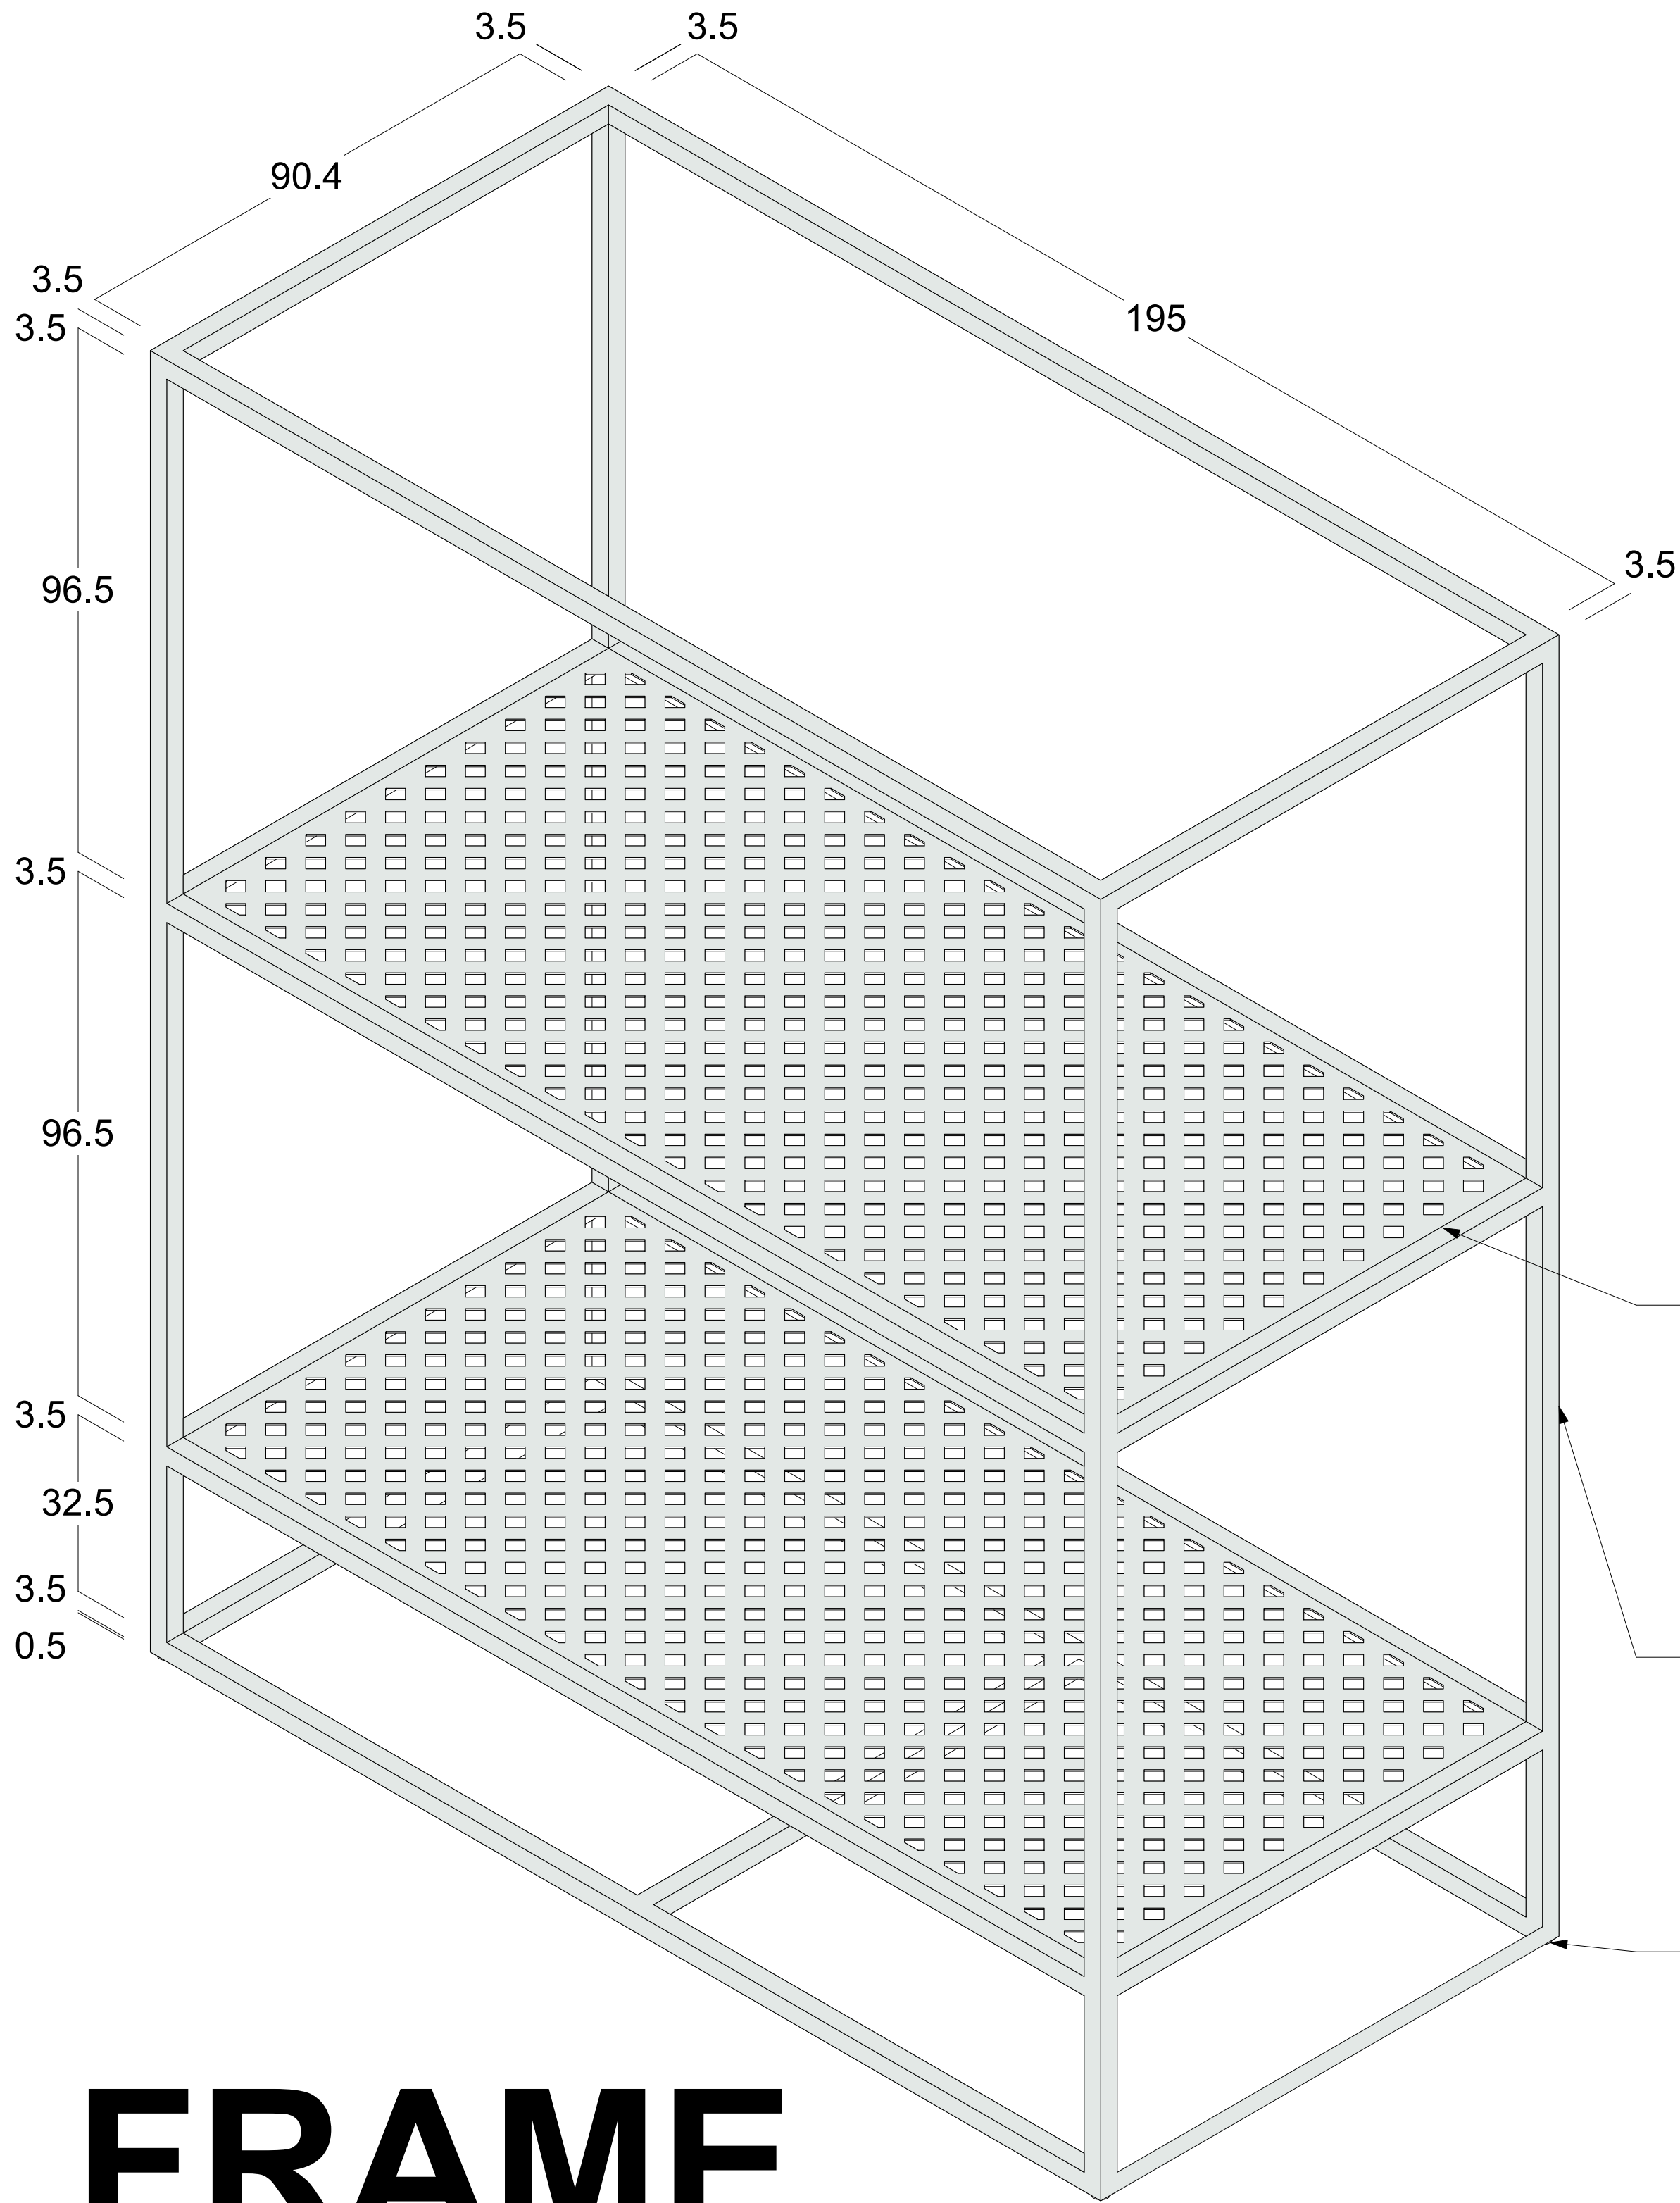



SS-B01
BED BASE 02_BUNKBED 2-ABC
SS-B01 SLAB - 90x200cm
Perforated metal slab for ventilation

SS-F01
FRAME_BUNKBED 2-AB
SS-F01/F02/F03 Frame -
3.5x3.5 cm Powder Coated
Steel Frame Structure - Colour
to match Telegrey 4 RAL 7047
- Semi gloss finish (RAL colour
to be confirmed by Clink)


SS-T01
FOOT_BUNKBED 2-ABC
SS-T01 Height Adjustable Feet

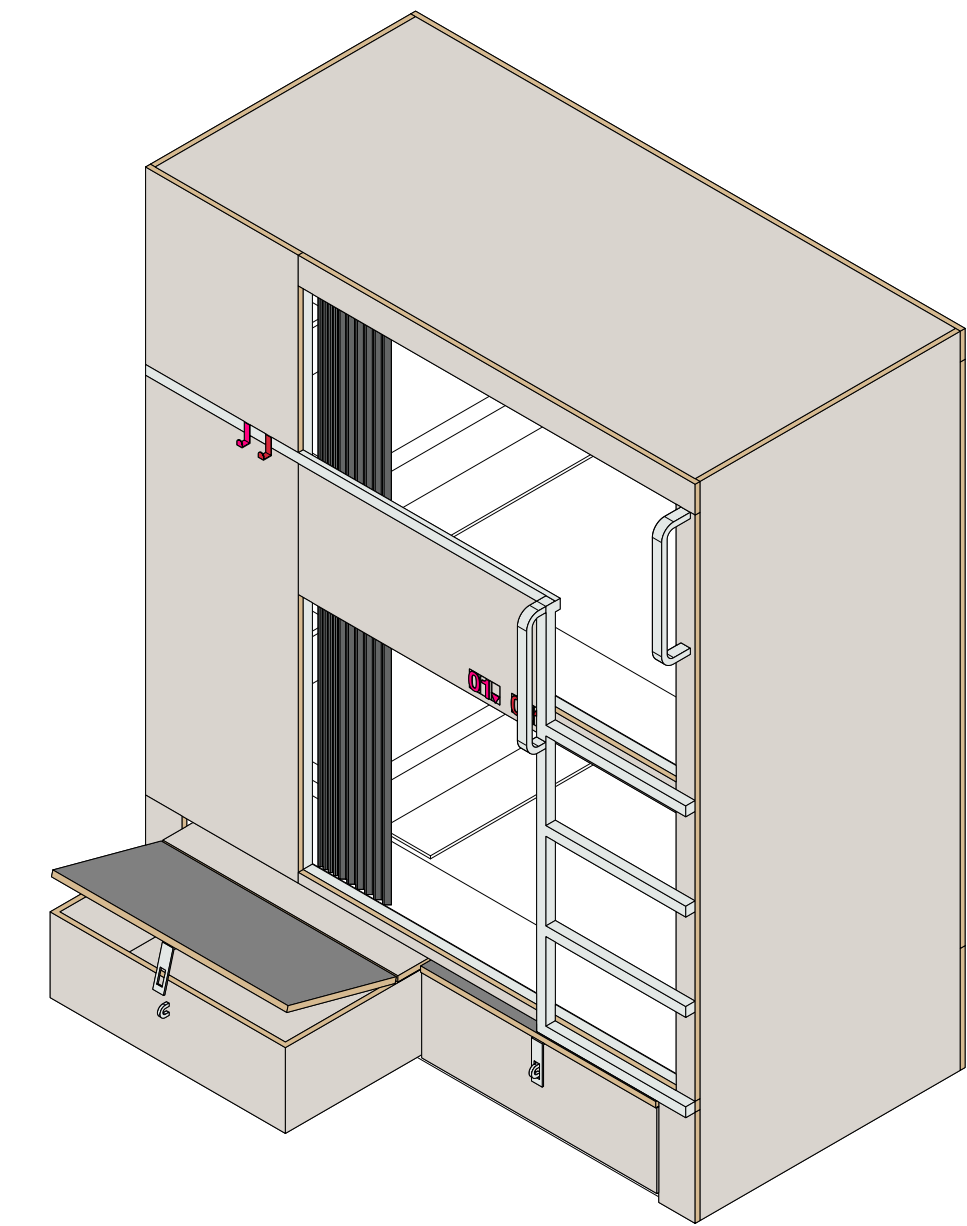

2-A

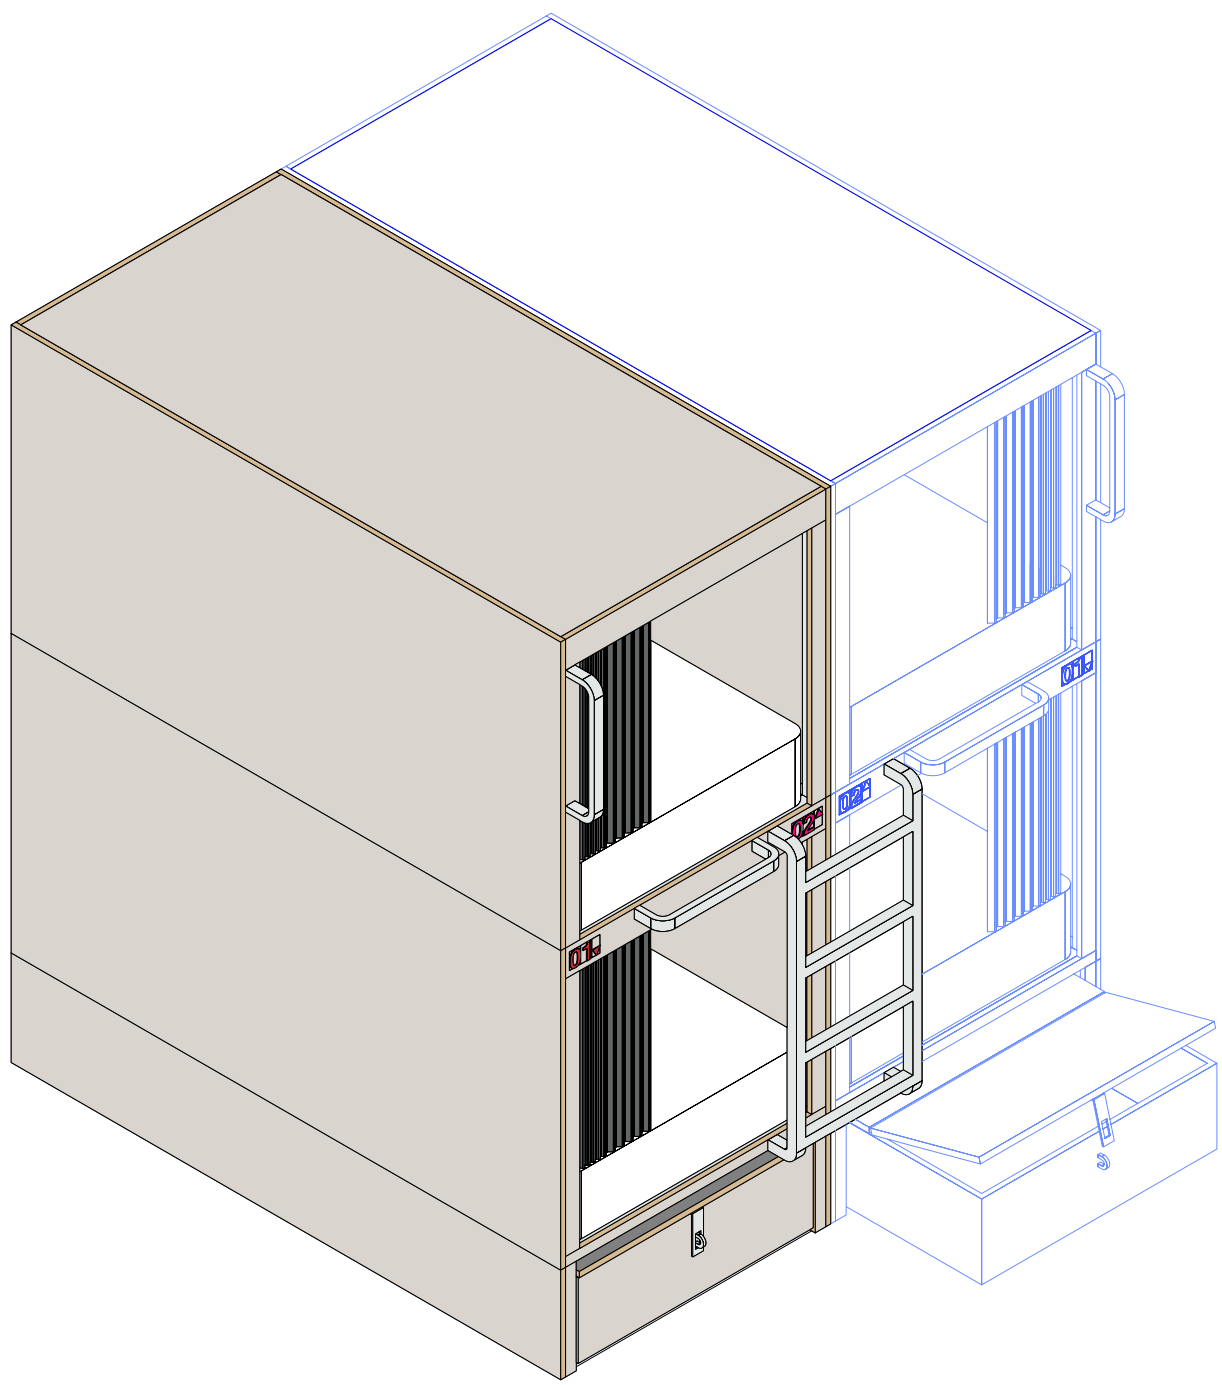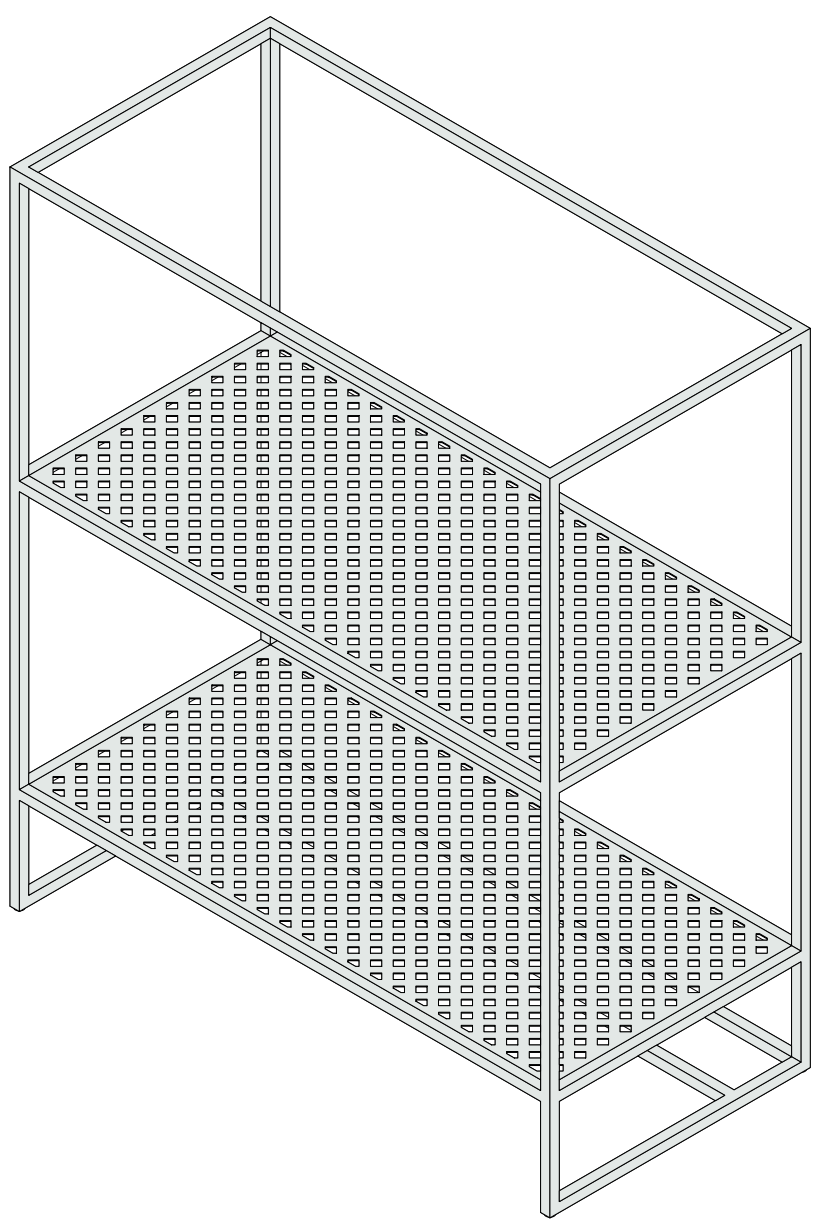

2-C1

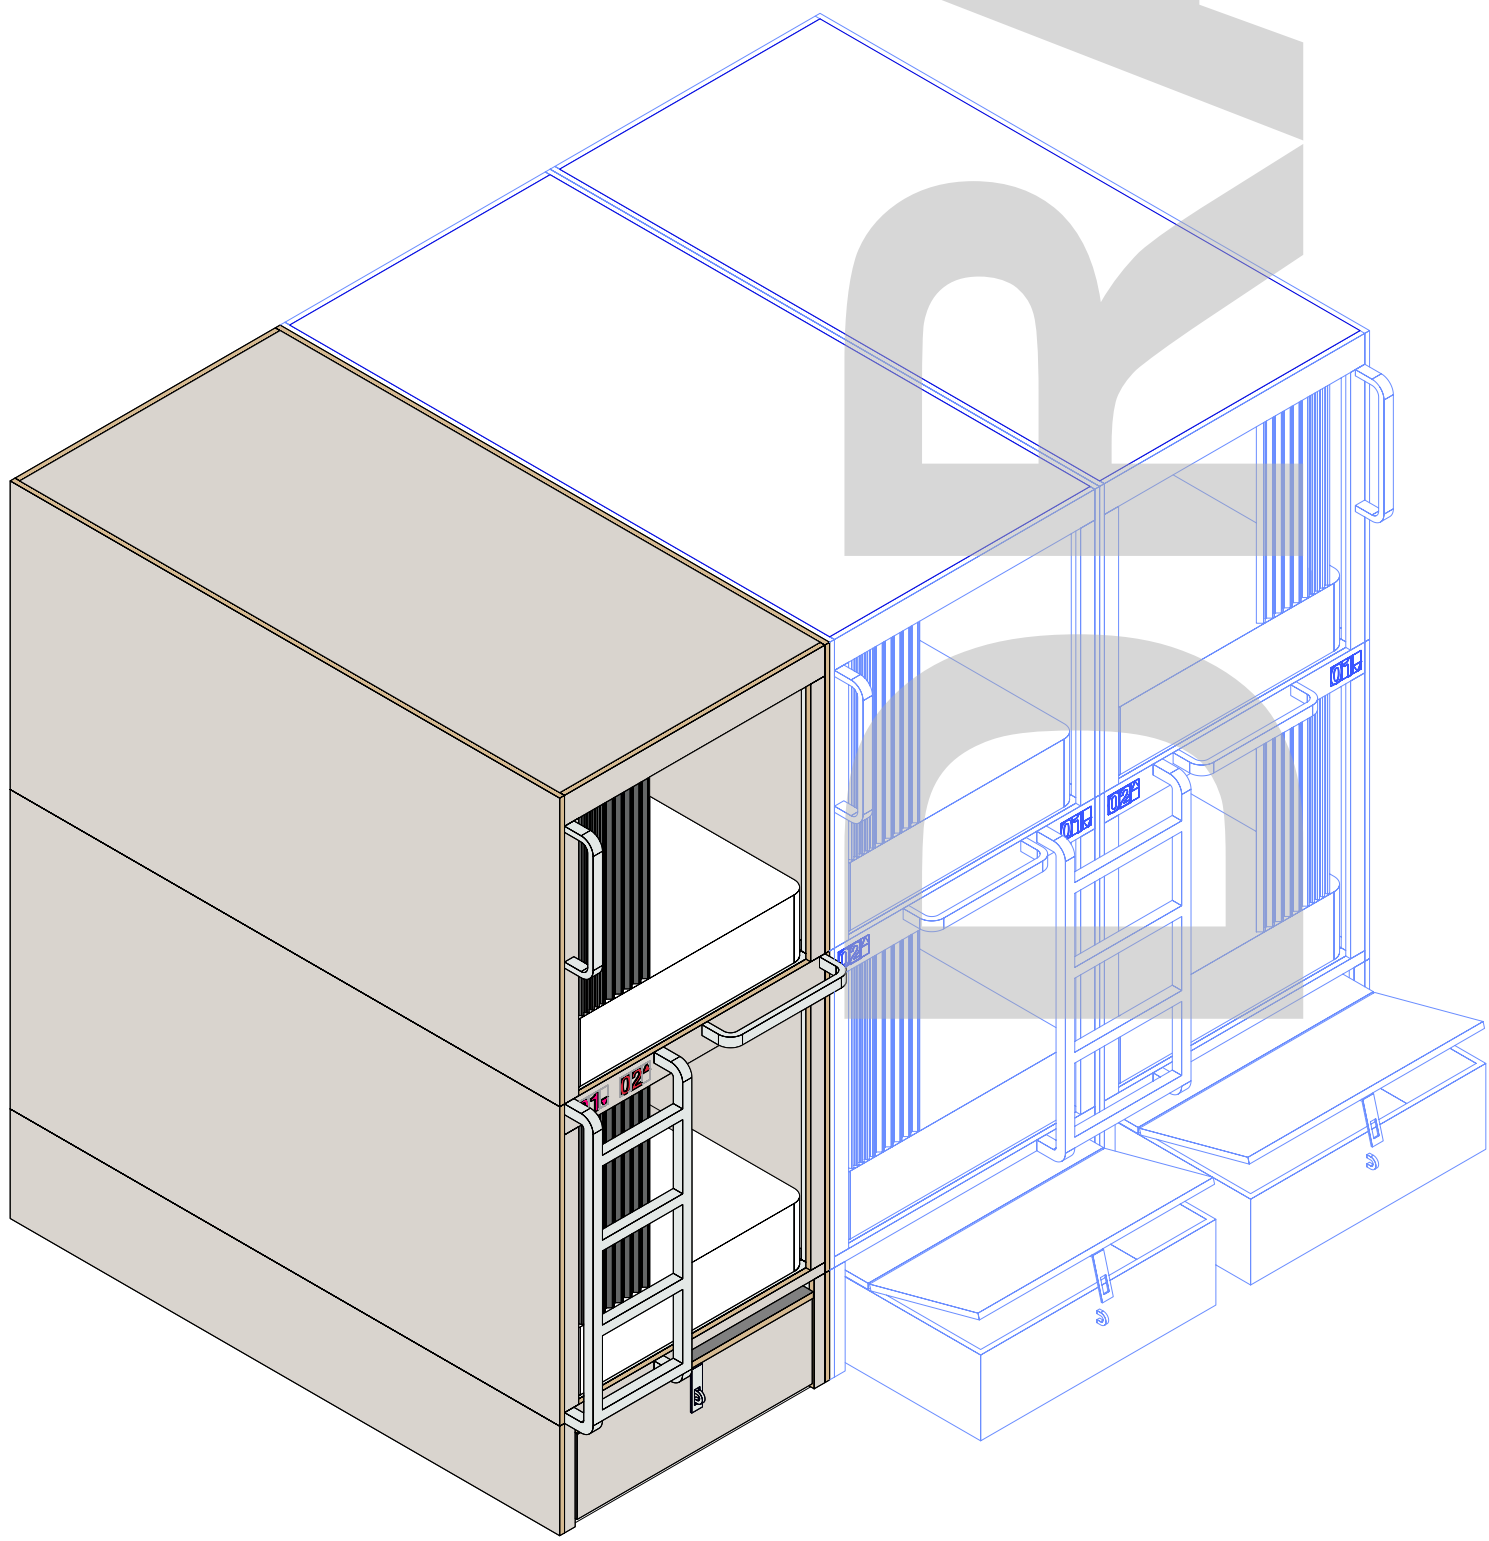


2-C2

FRAME

202 x 97.4 x 240
(L x W x H) cm




BUNKBEDS TYPE 2 - SIGNANGE

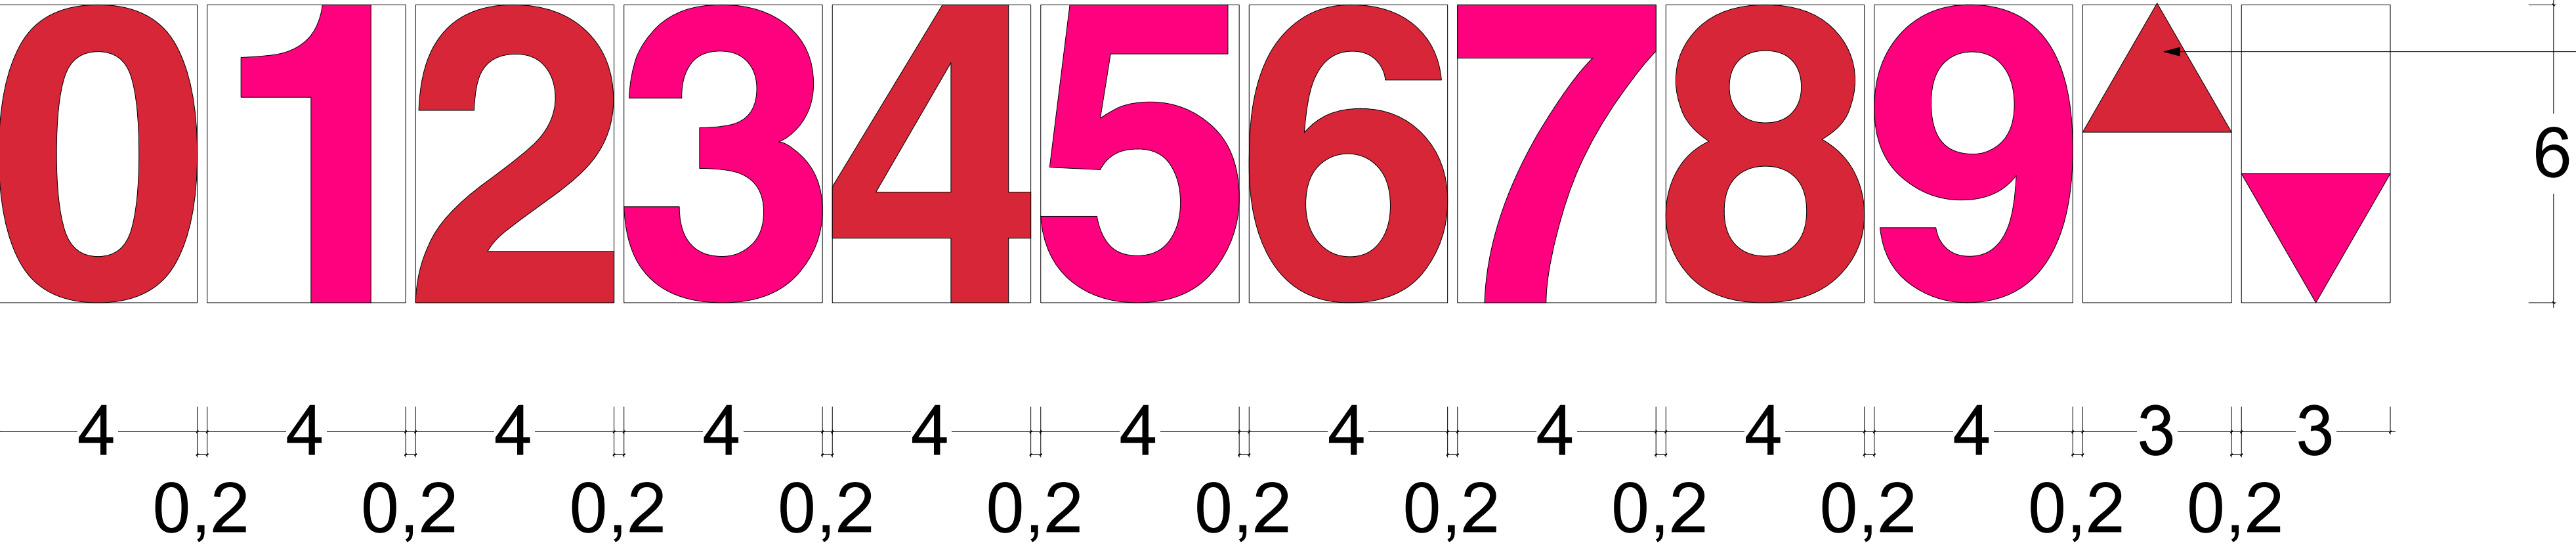


AA-S01
2-001 NUMBERS
AA-R01 TOWEL RACK - stainless steel - powder coated
- The same colour as the metal frame, polished edges for safety reasons, to fit into the metal frame size - according to the drawing (RAL colour to be confirmed by Clink)

COLOUR EXAMPLE	
RAL 3020	BUNKBED 1: 02↑, 01↓ BUNKBED 2: 04↑, 03↓
RAL 4010	


FINAL COLOURS TBC BY CLINK

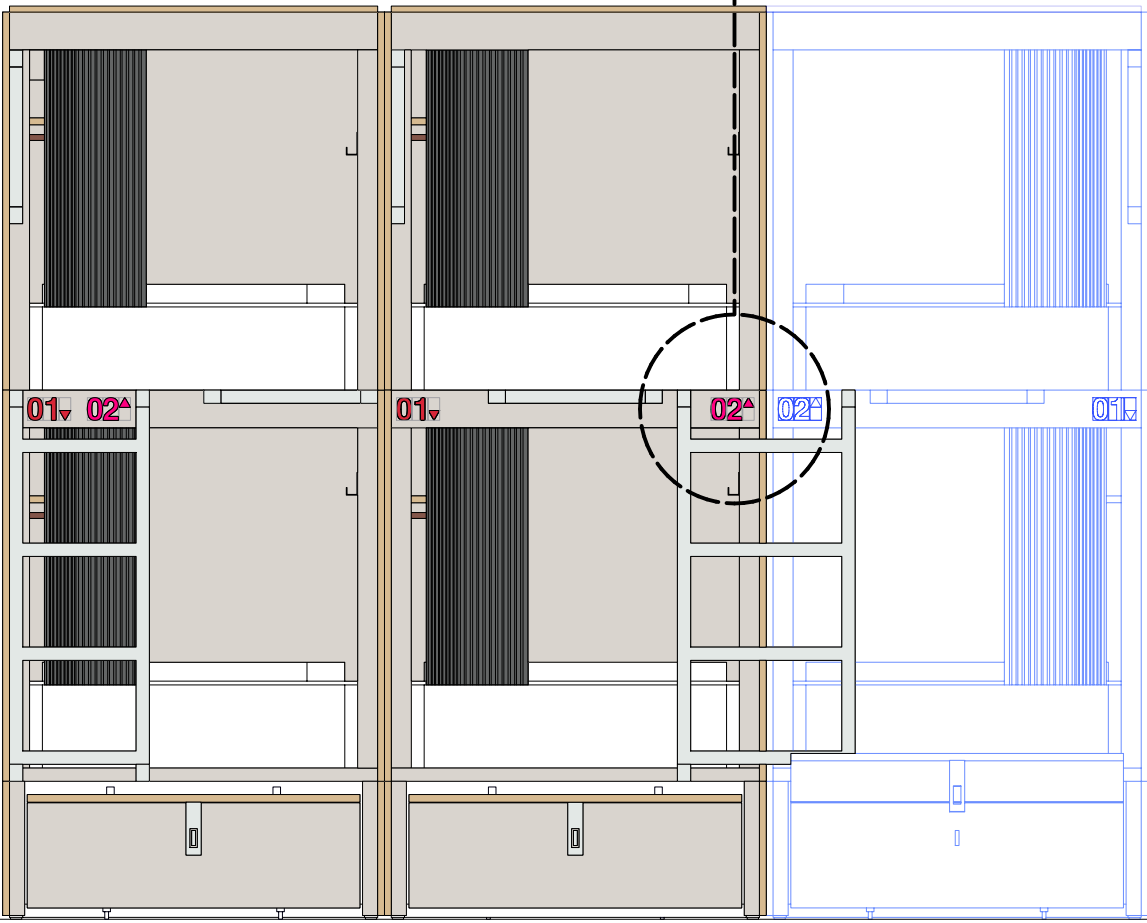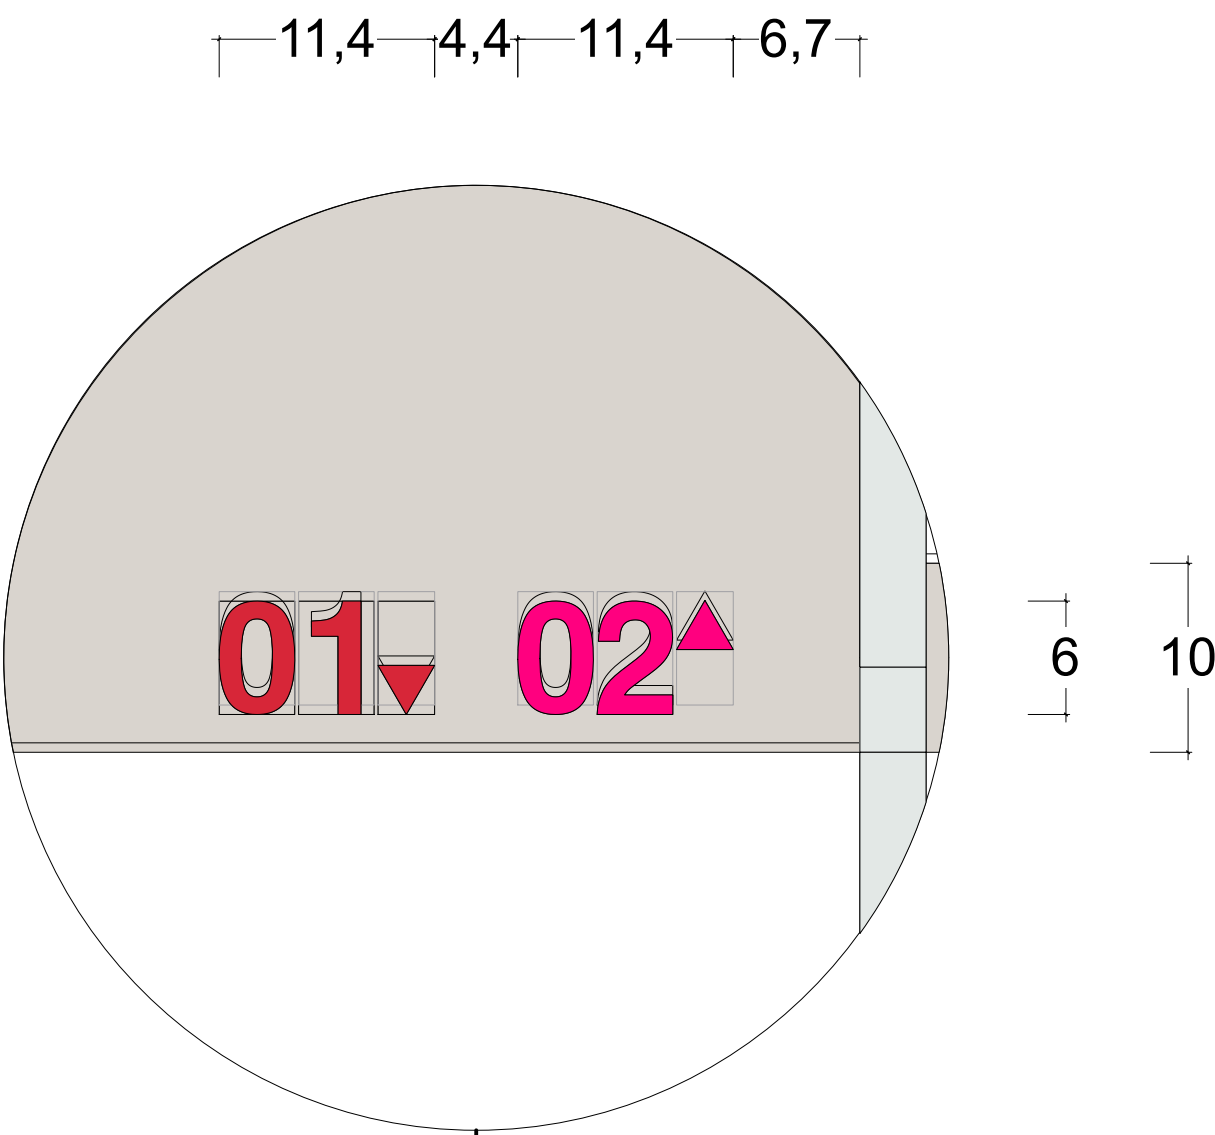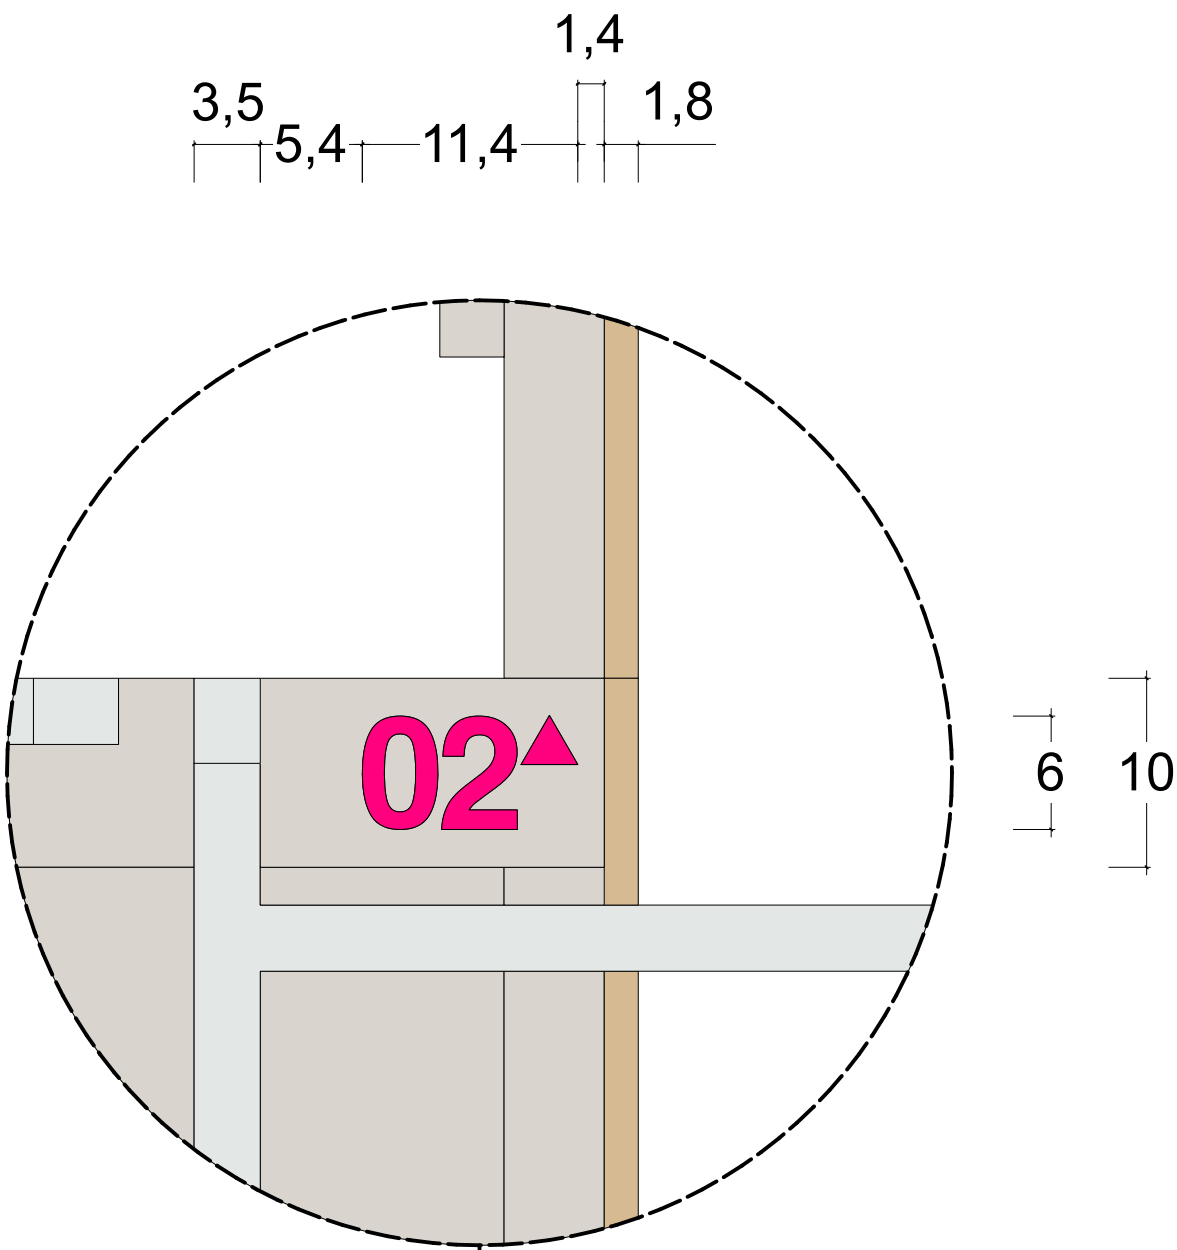

BUNKBED 2-C ELEVATIONS

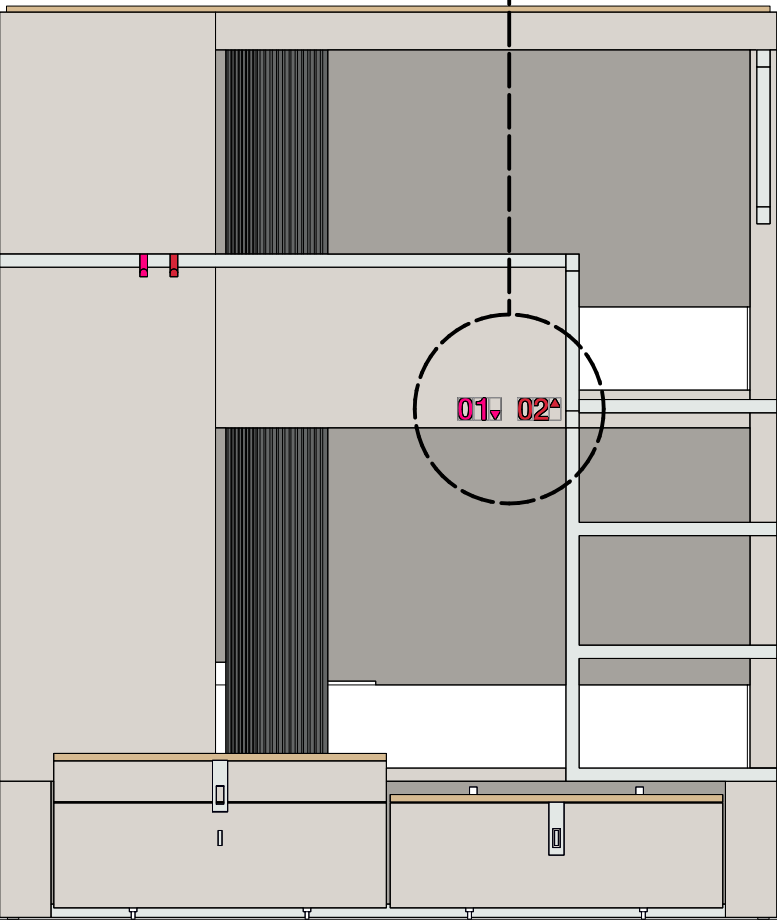

BUNKBED 2-A ELEVATIONS

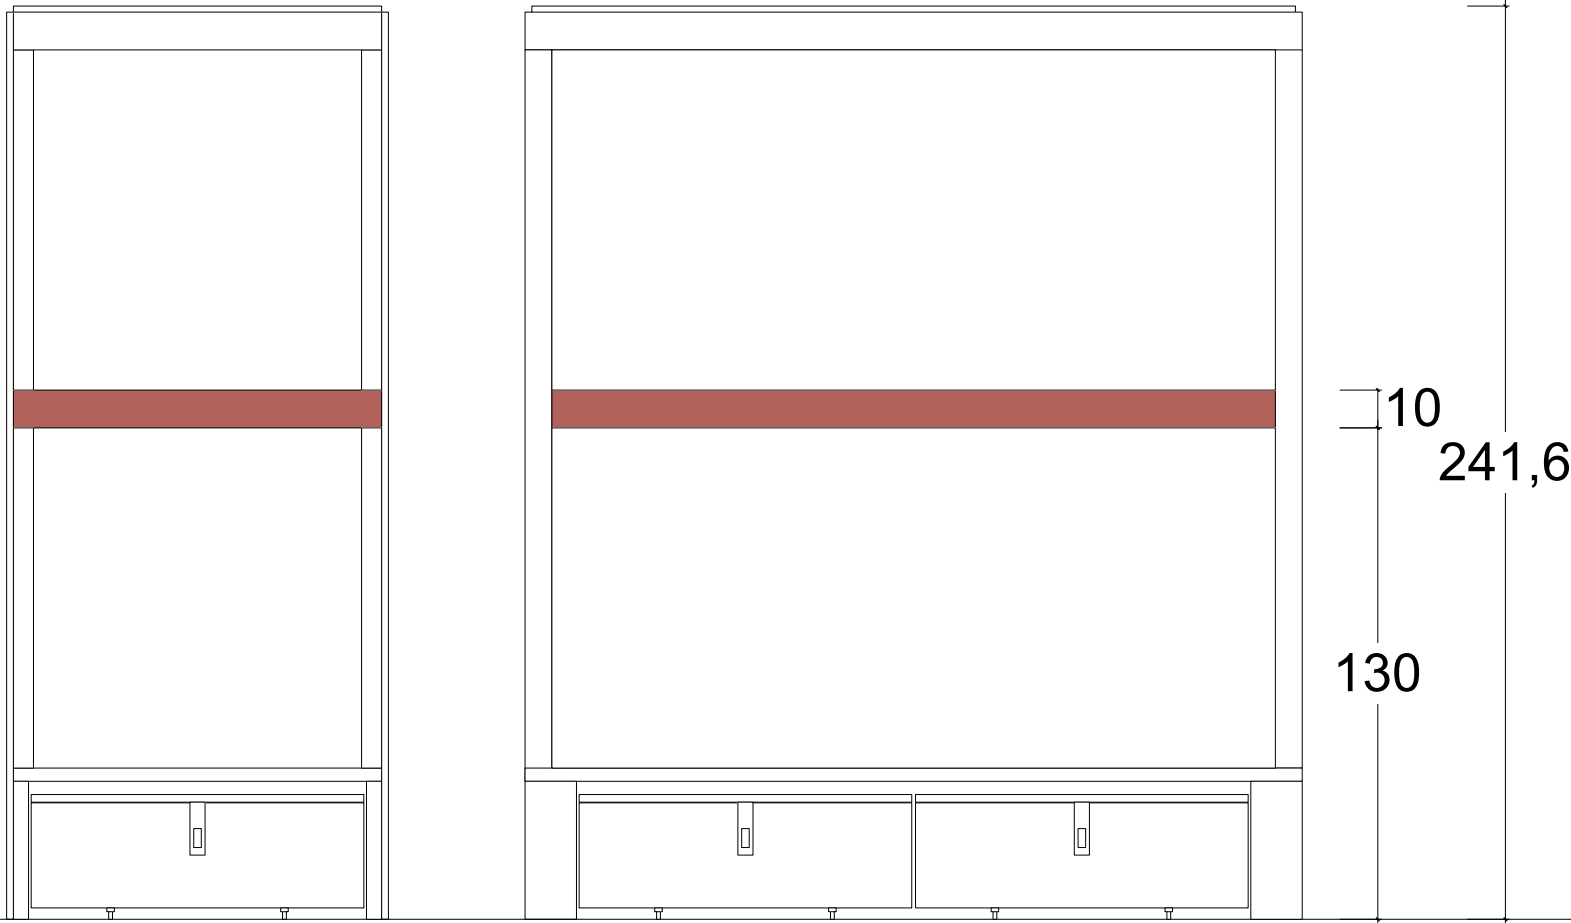

SIGNAGE BAR
Signage numbers to be assigned after bunkbeds are installed.

KEY

Index

A) 04.05.2026 Plan Set UP

CLINK HOSTELS

Project Address

CLINK 78
78 King's Cross Rd
London WC1X 9QG
United Kingdom

Client's Address

CLINK 78
78 King's Cross Rd
London WC1X 9QG
United Kingdom


Sheet Number	2-002	Total Sheets	82
Sheet Title	TYPE 2 - SIGNAGE	Level	
File Name			
260425_CLINK 78_BEDs AA DRAFT 03.vwx			
Date	Sheet Size	Scale	Signed
28.04.26	A1	1:20	AA

Stefanie Jaensch INTERIOR DESIGNS




Global Headquarter | Stefanie Jaensch c/o WeWork
Taubusanlage 8 | 60329 Frankfurt a.M.
E-Mail info@stefaniejaensch.de | DE +49 (0) 174 6756098
www.stefaniejaensch.de

Legal address | Stefanie Jaensch | Offenbacher Landstraße 434 | 60599 Frankfurt a.M.
© 2023 All Rights Reserved | Stefanie Jaensch




BUNKBEDS TYPE 2 - LED LIGHTS PLAN

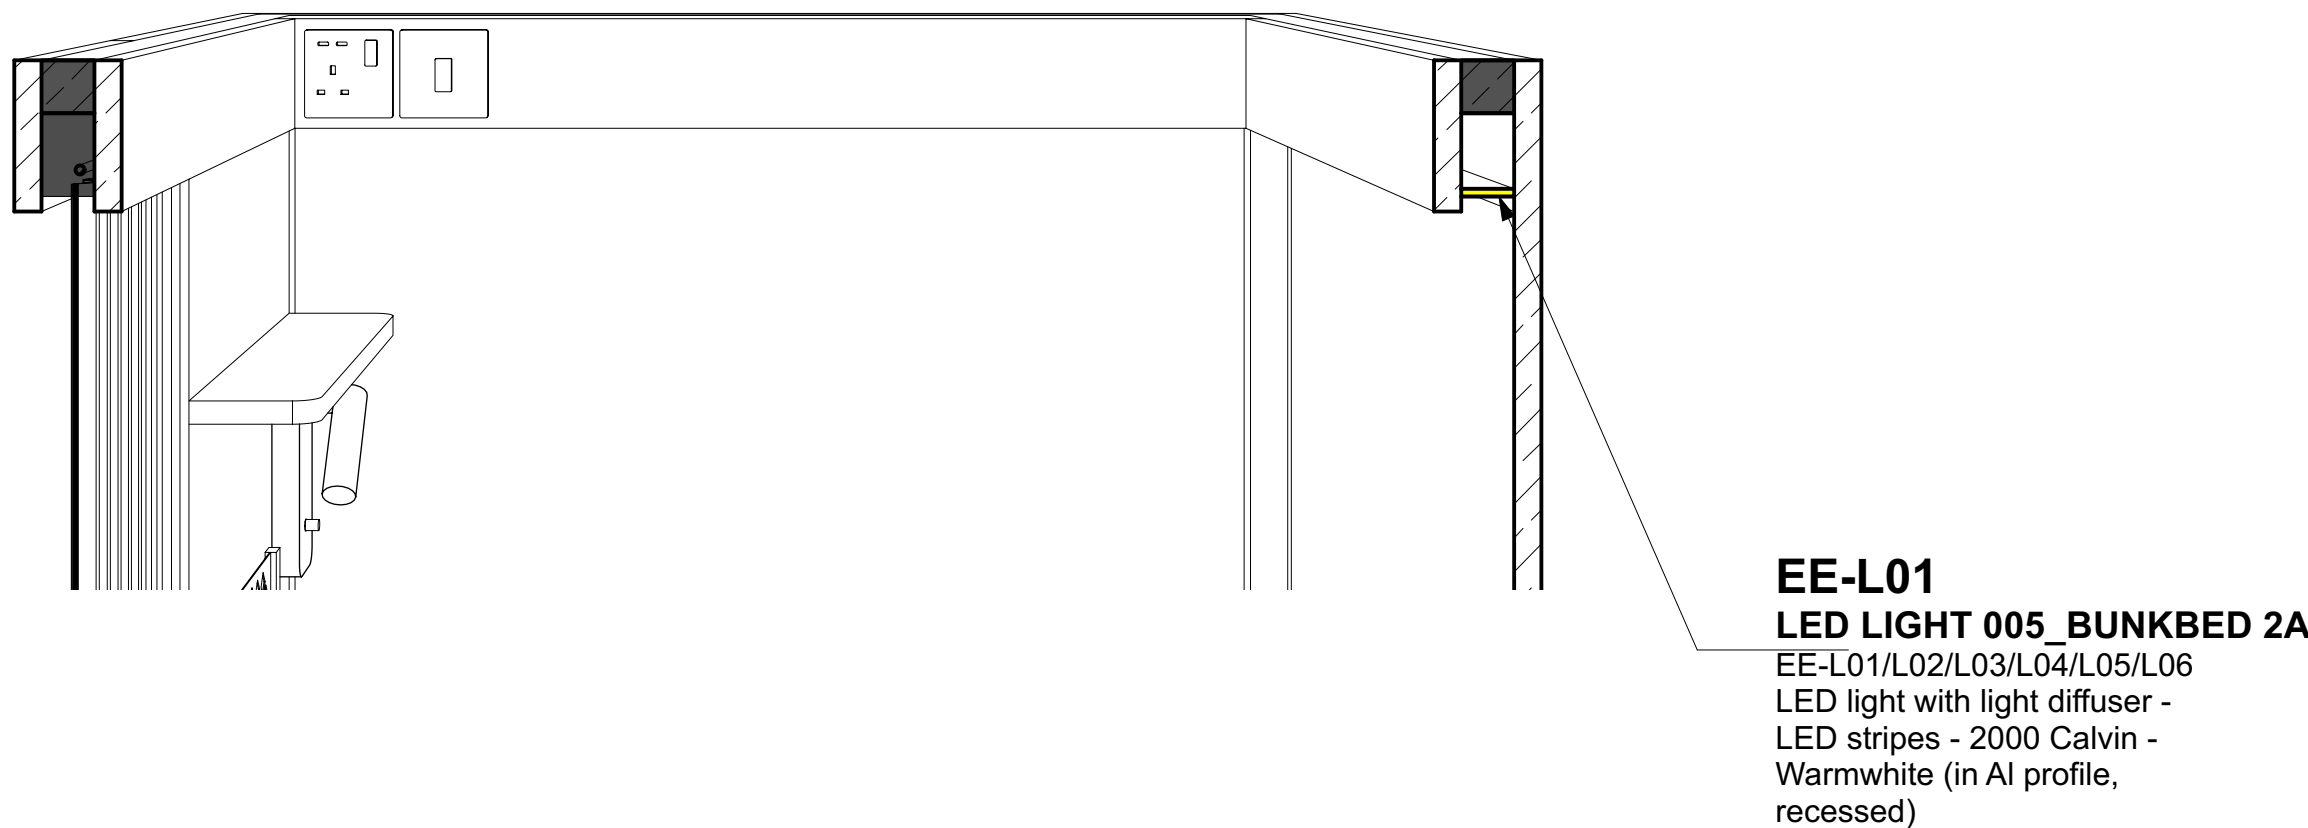

LEVEL 2

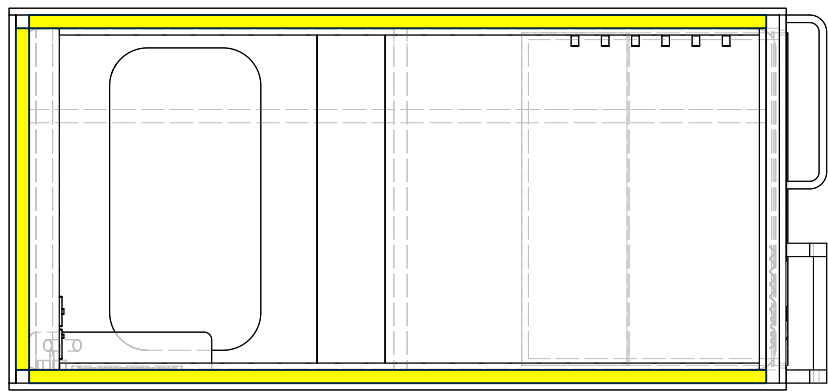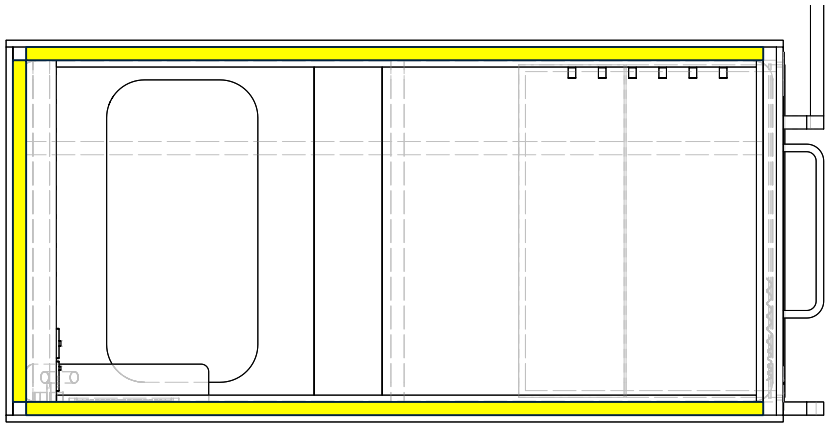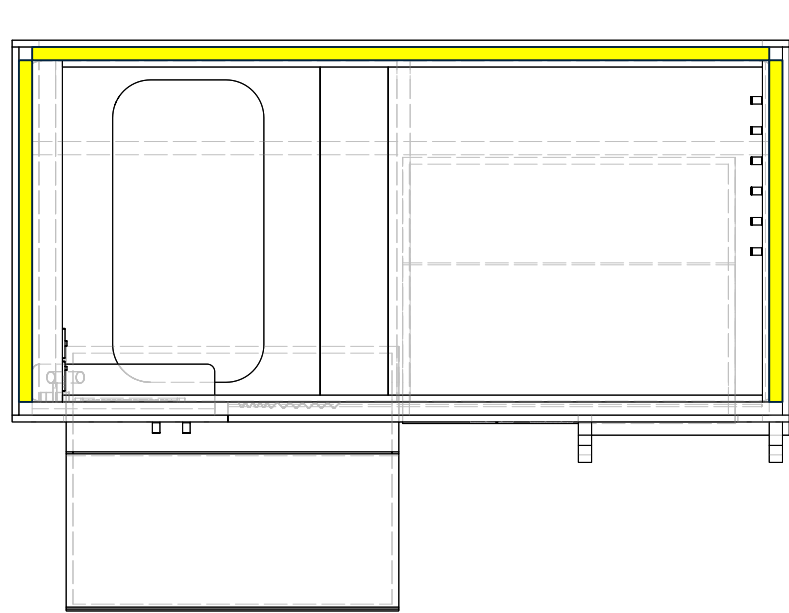


LEVEL 1

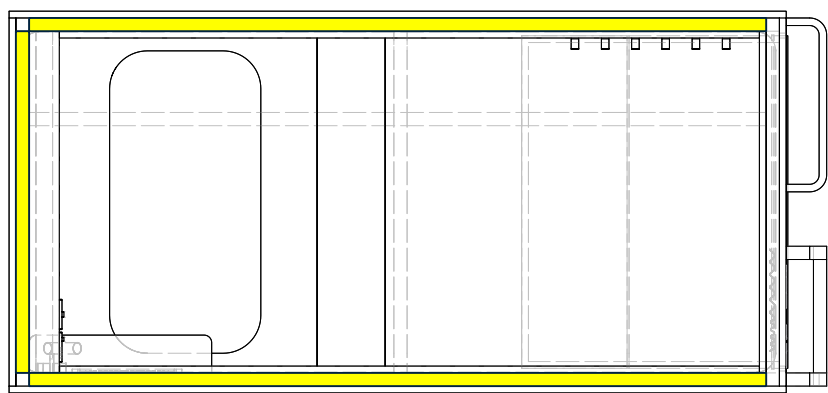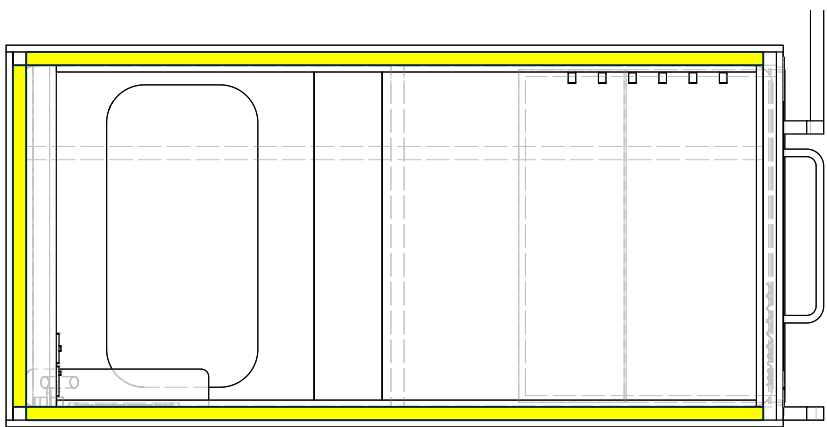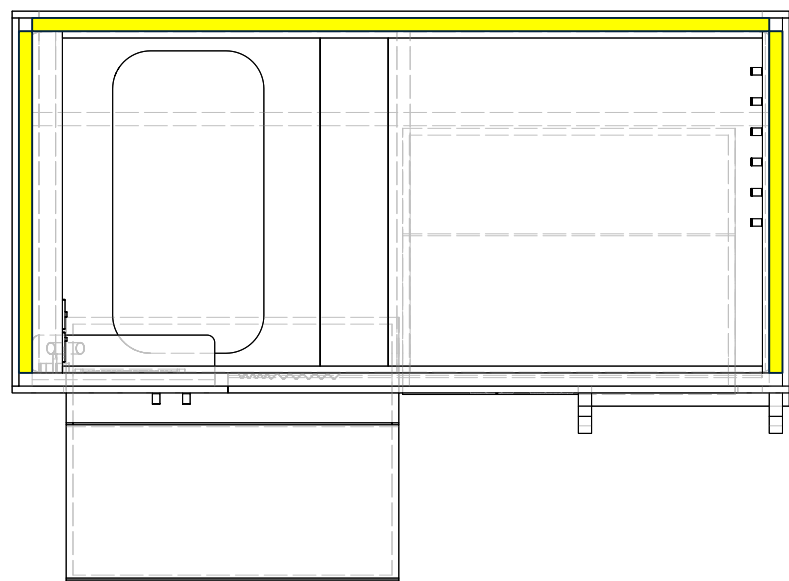

2-A

2-C1

2-C2

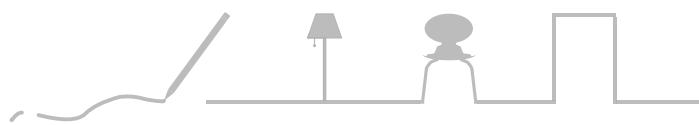

KEY

Index

A) 04.05.2026 Plan Set UP

All measurements have to be verified according to existing conditions by the contractor! Discrepancies must be reported immediately to the responsible project manager. The contractor has to produce fully dimensioned shop drawings prior to the start of the contract and they have to be approved by the client/ investor / interior designer

Project

CLINK 78 - BEDS

Logo



Project Address

CLINK 78
78 King's Cross Rd
London WC1X 9QG
United Kingdom


Client's Address

CLINK 78
78 King's Cross Rd
London WC1X 9QG
United Kingdom

Sheet Number	2-003	Total Sheets	82
Sheet Title	TYPE 2 - LED LIGHTS PLAN	Level	
File Name	260425_CLINK 78_BEDs AA DRAFT 03.vwx		




Date	Sheet Size	Scale	Signed
28.04.26	A1		AA

BUNKBEDS TYPE 2 - CURTAINS PLAN



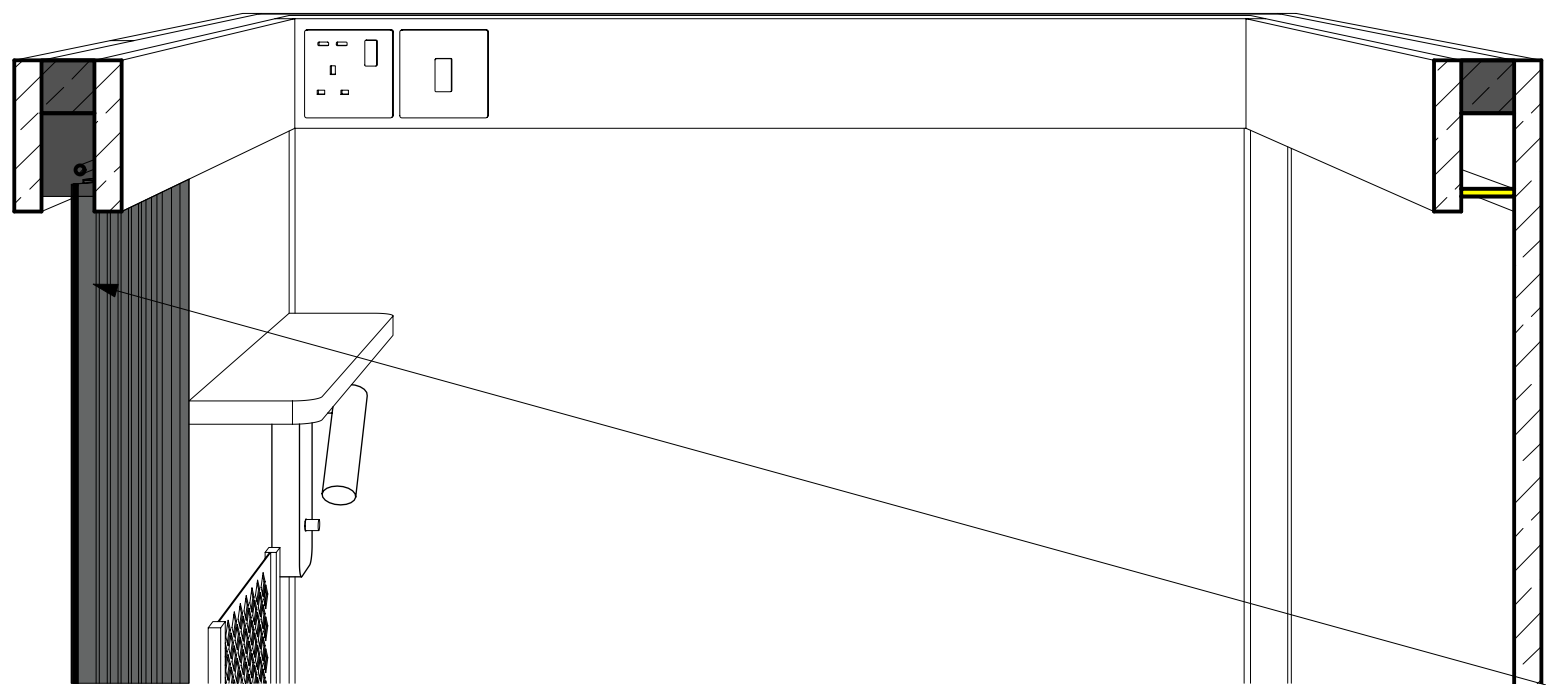


FF-C01
CURTAINS 02_BUNKBED 2-AB
FF-C01/C02/C03 Privacy
curtain - Washable Fabric
-colour: dark grey/ anthracite
less fold -Almost 1:1 fold factor
to open horizontally-
fire-retardant fabric - Matt
Finish - CURTAINS-LUNA
BLACKOUT-by SKOPOS-
TEX L15 GUNMETAL-(RAL
colour tbc by Clink)

LEVEL 2

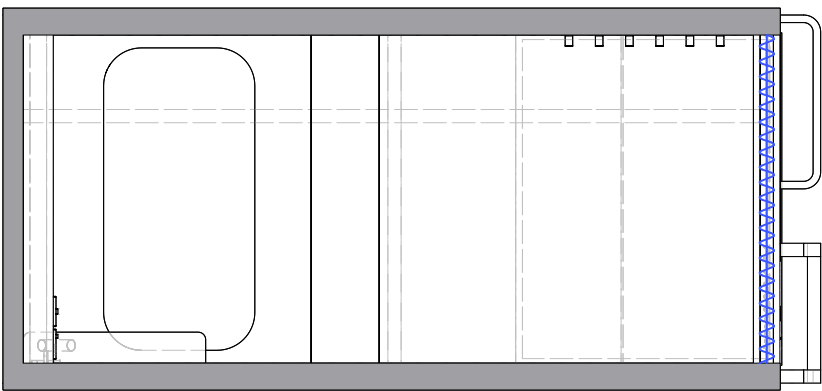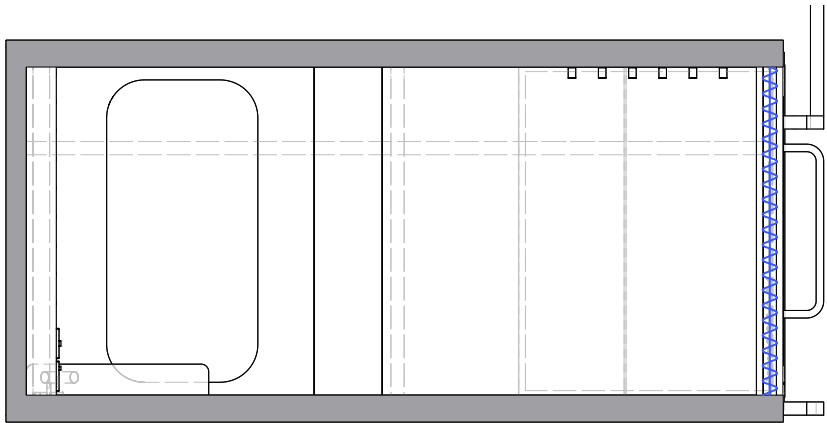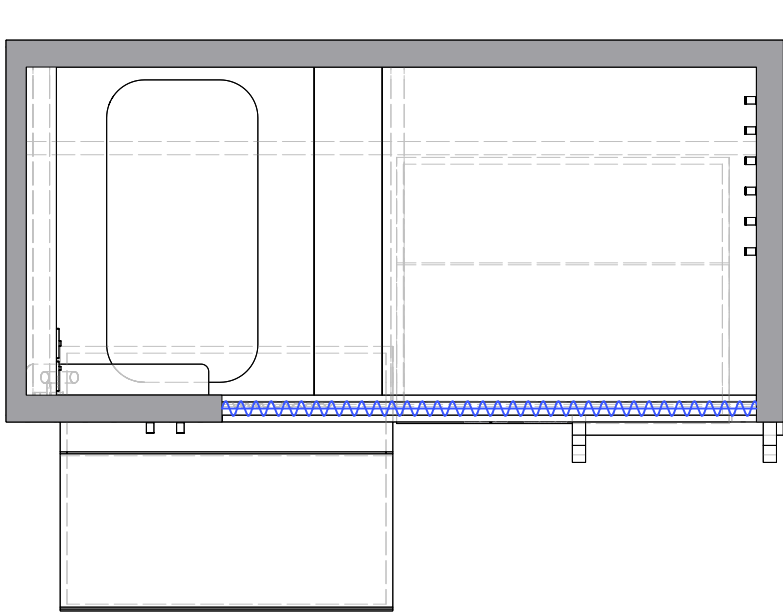


LEVEL 1

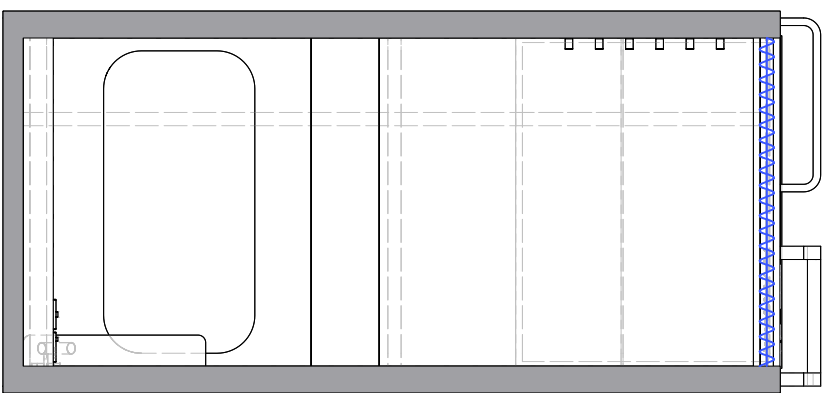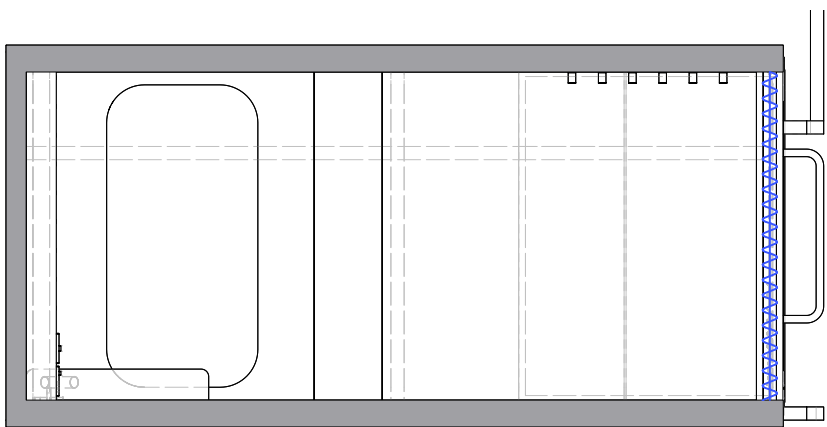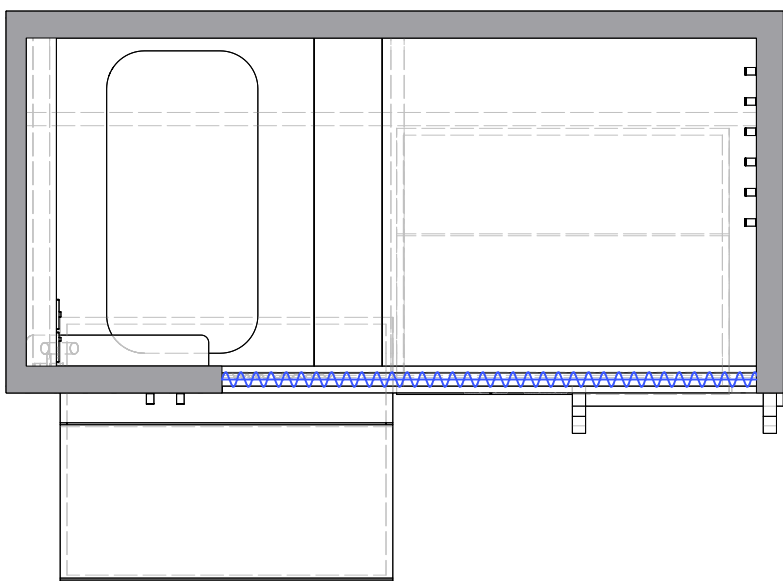

2-A

2-C1

2-C2

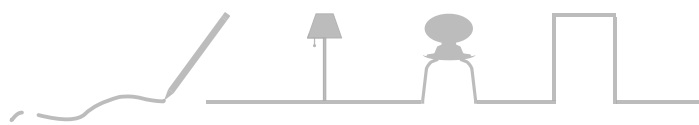

KEY

Index
A) 04.05.2026 Plan Set UP

All measurements have to be verified according to existing conditions by the contractor! Discrepancies must be reported immediately to the responsible project manager. The contractor has to produce fully dimensioned shop drawings prior to the start of the contract and they have to be approved by the client/ investor / interior designer

Project
CLINK 78 - BEDS



Project Address
CLINK 78
78 King's Cross Rd
London WC1X 9QG
United Kingdom


Client's Address
CLINK 78
78 King's Cross Rd
London WC1X 9QG
United Kingdom

Sheet Number	2-004	Total Sheets	82
Sheet Title	TYPE 2 - CURTAINS PLAN	Level	

Date	Sheet Size	Scale	Signed
28.04.26	A1		AA

Stefanie Jaensch INTERIOR DESIGNS
Global Headquarter | Stefanie Jaensch c/o WeWork
Taubusanlage 8 | 60329 Frankfurt a.M.
E-Mail info@stefaniejaensch.de | DE +49 (0) 174 6756098
www.stefaniejaensch.de
Legal address | Stefanie Jaensch | Offenbacher Landstraße 434 | 60599 Frankfurt a.M.
© 2023 All Rights Reserved | Stefanie Jaensch

BUNKBEDS - TYPE 2-A

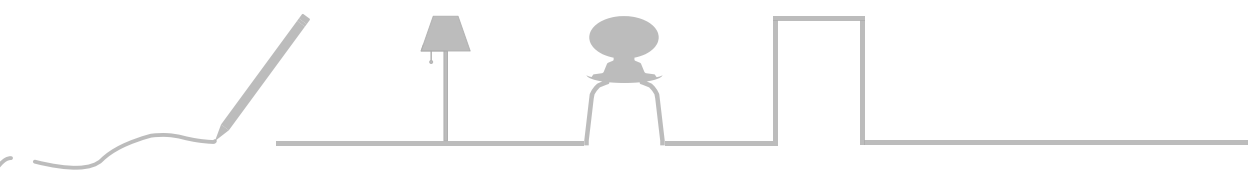


Stefanie Jaensch

INTERIOR DESIGNS

For



2-A

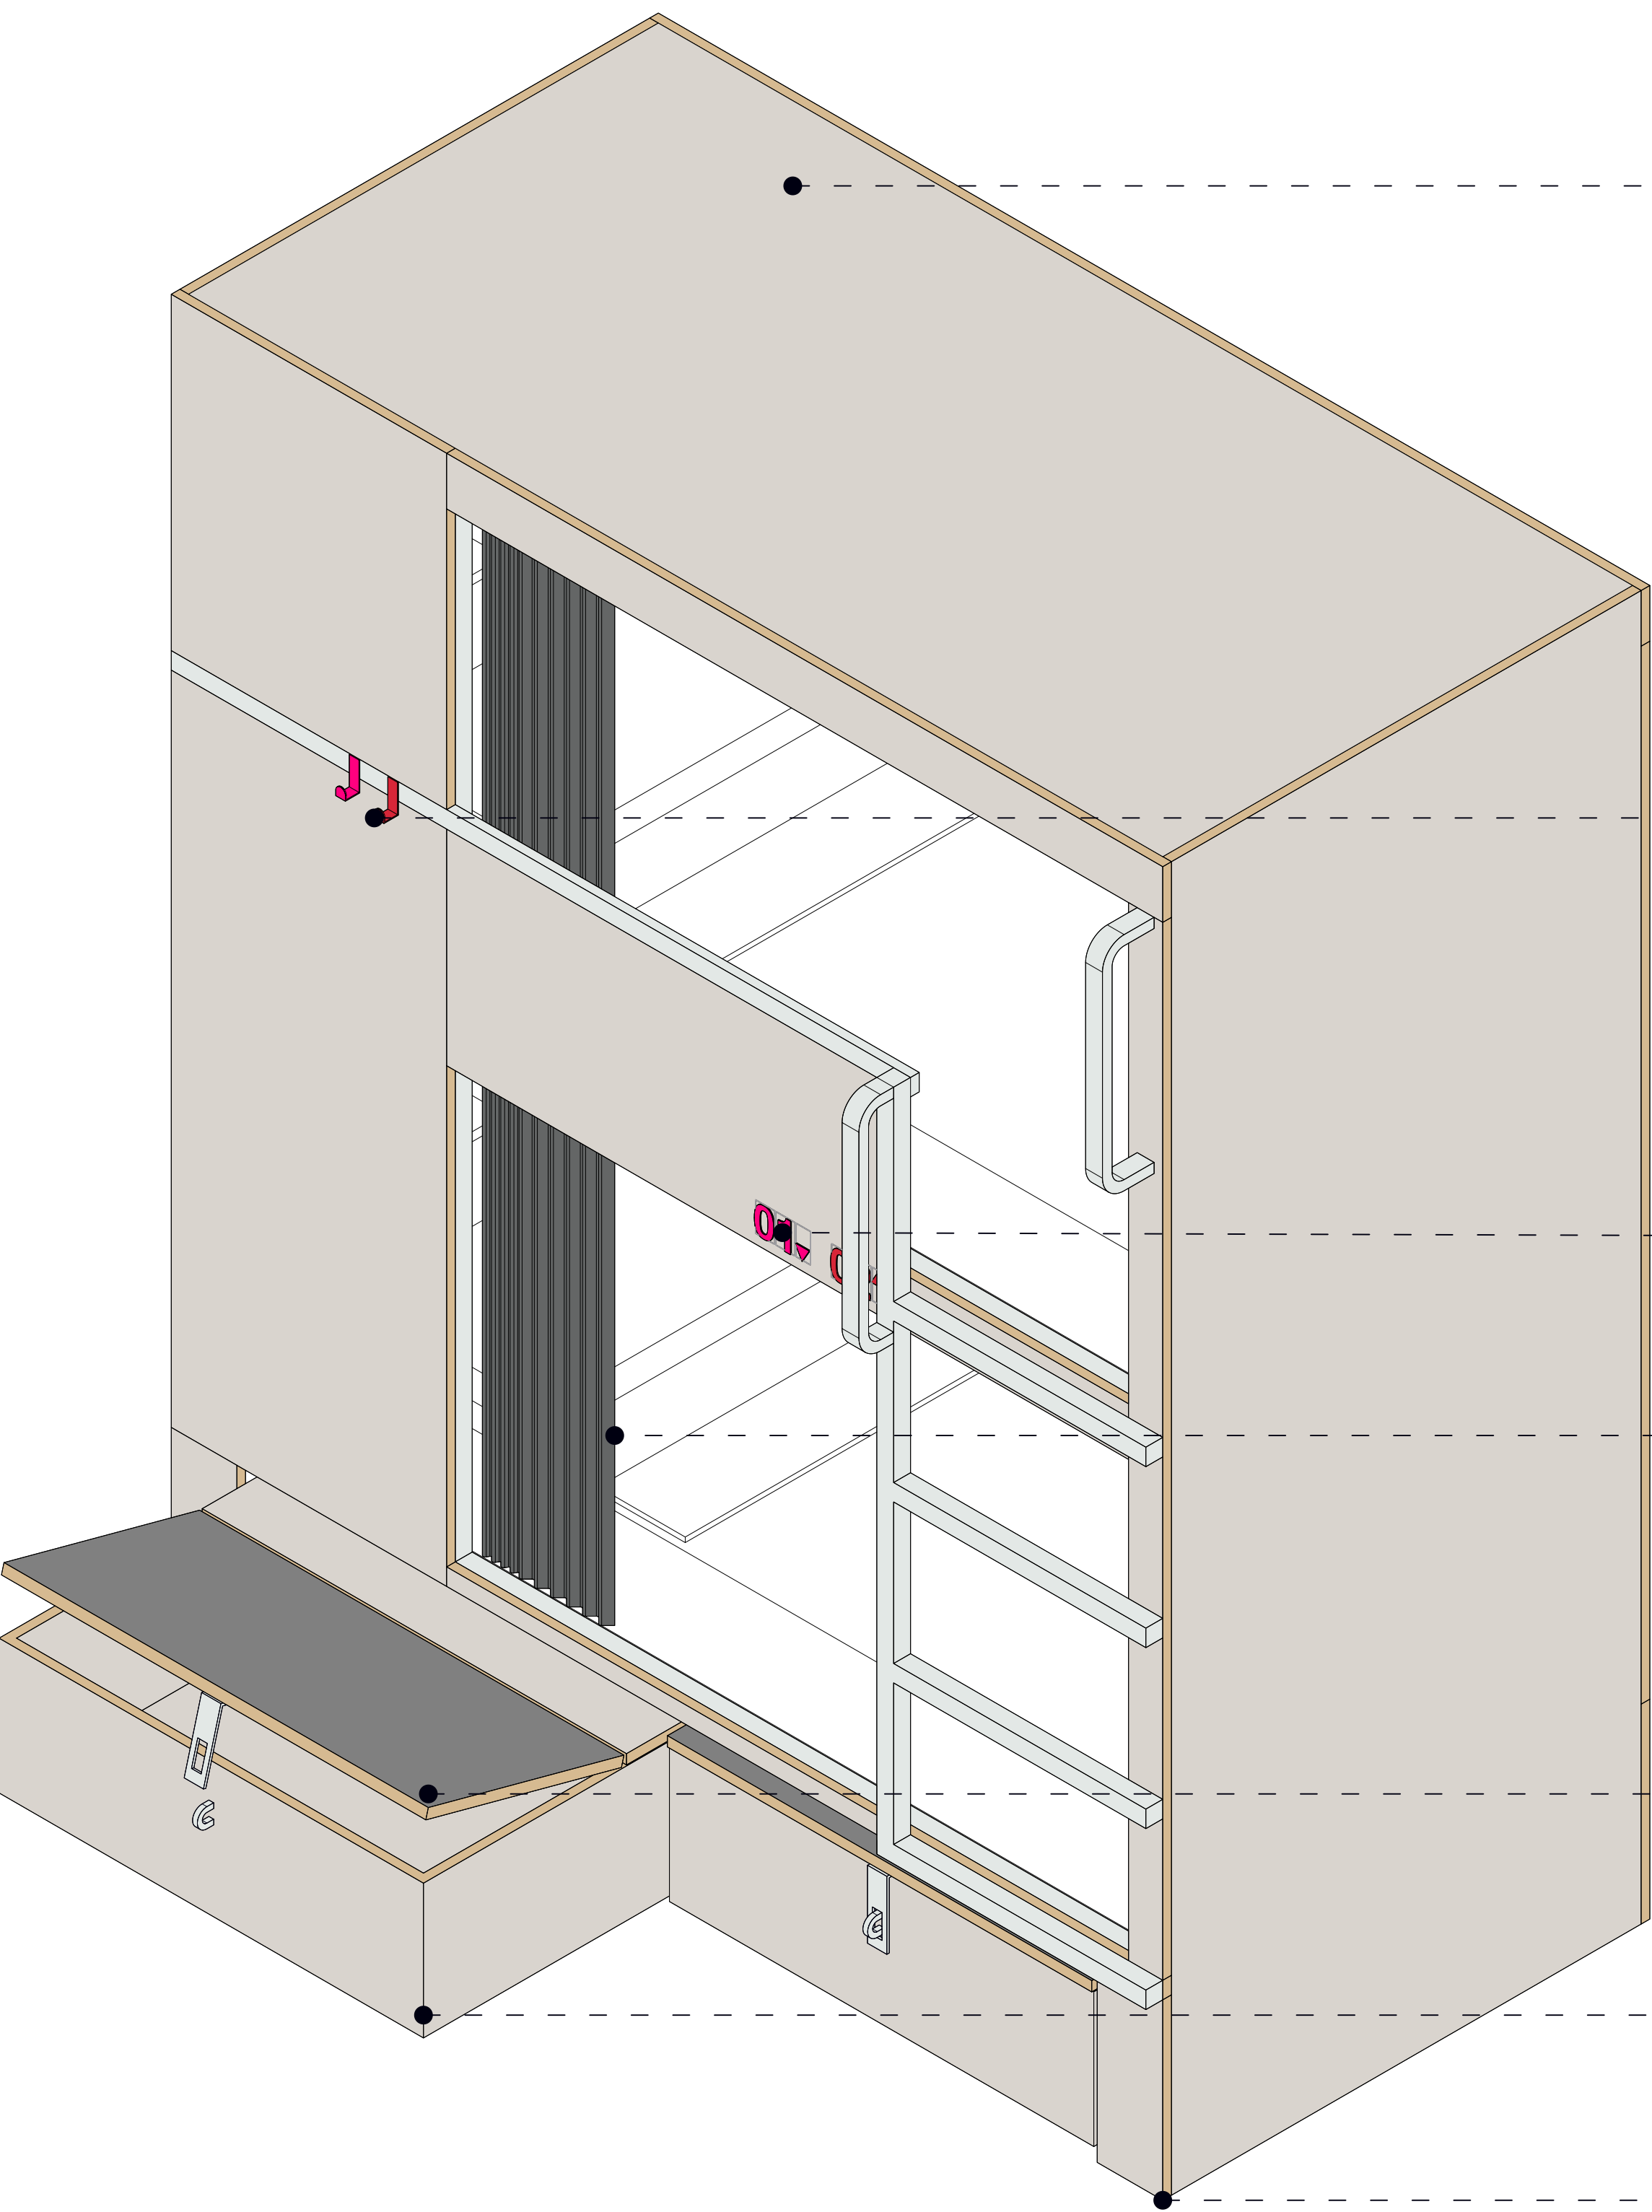

CC-M01
Cladding - Laminated
chipboard - Colour
(TBC) RAL 7044,
Thickness 18m

AA-H01 Hooks - stainless
steel powder-coated -
RAL 3020 Red & RAL
4010 Rose
FINAL HOOKS
QUANTITY & Colour
TBC


AA-S01
SIGNAGE - Numbers -
laser-cut acrylic or MDF -
thickness 5mm - spray
painted - RAL 3020 Red &
RAL 4010 Rose - font
according to wayfinding
signage design (RAL Colour
TBC by Clink)

FF-C01 Metal ring curtains with
a sturdy/durable pole
Privacy curtain - washable
textile - colour: dark grey/
anthracite less fold - Almost 1:1
fold factor to open horizontally -
fire-retardant fabric
LUNA BLACKOUT by SKOPOS
TEXTURED L15 GUNMETAL
(RAL Colour TBC by Clink)

Laminated chipboard
with Rubber Pad on top (Colour
TBC)

88x70x33 Locker

CC-M07 Visible Edges
Plywood edges

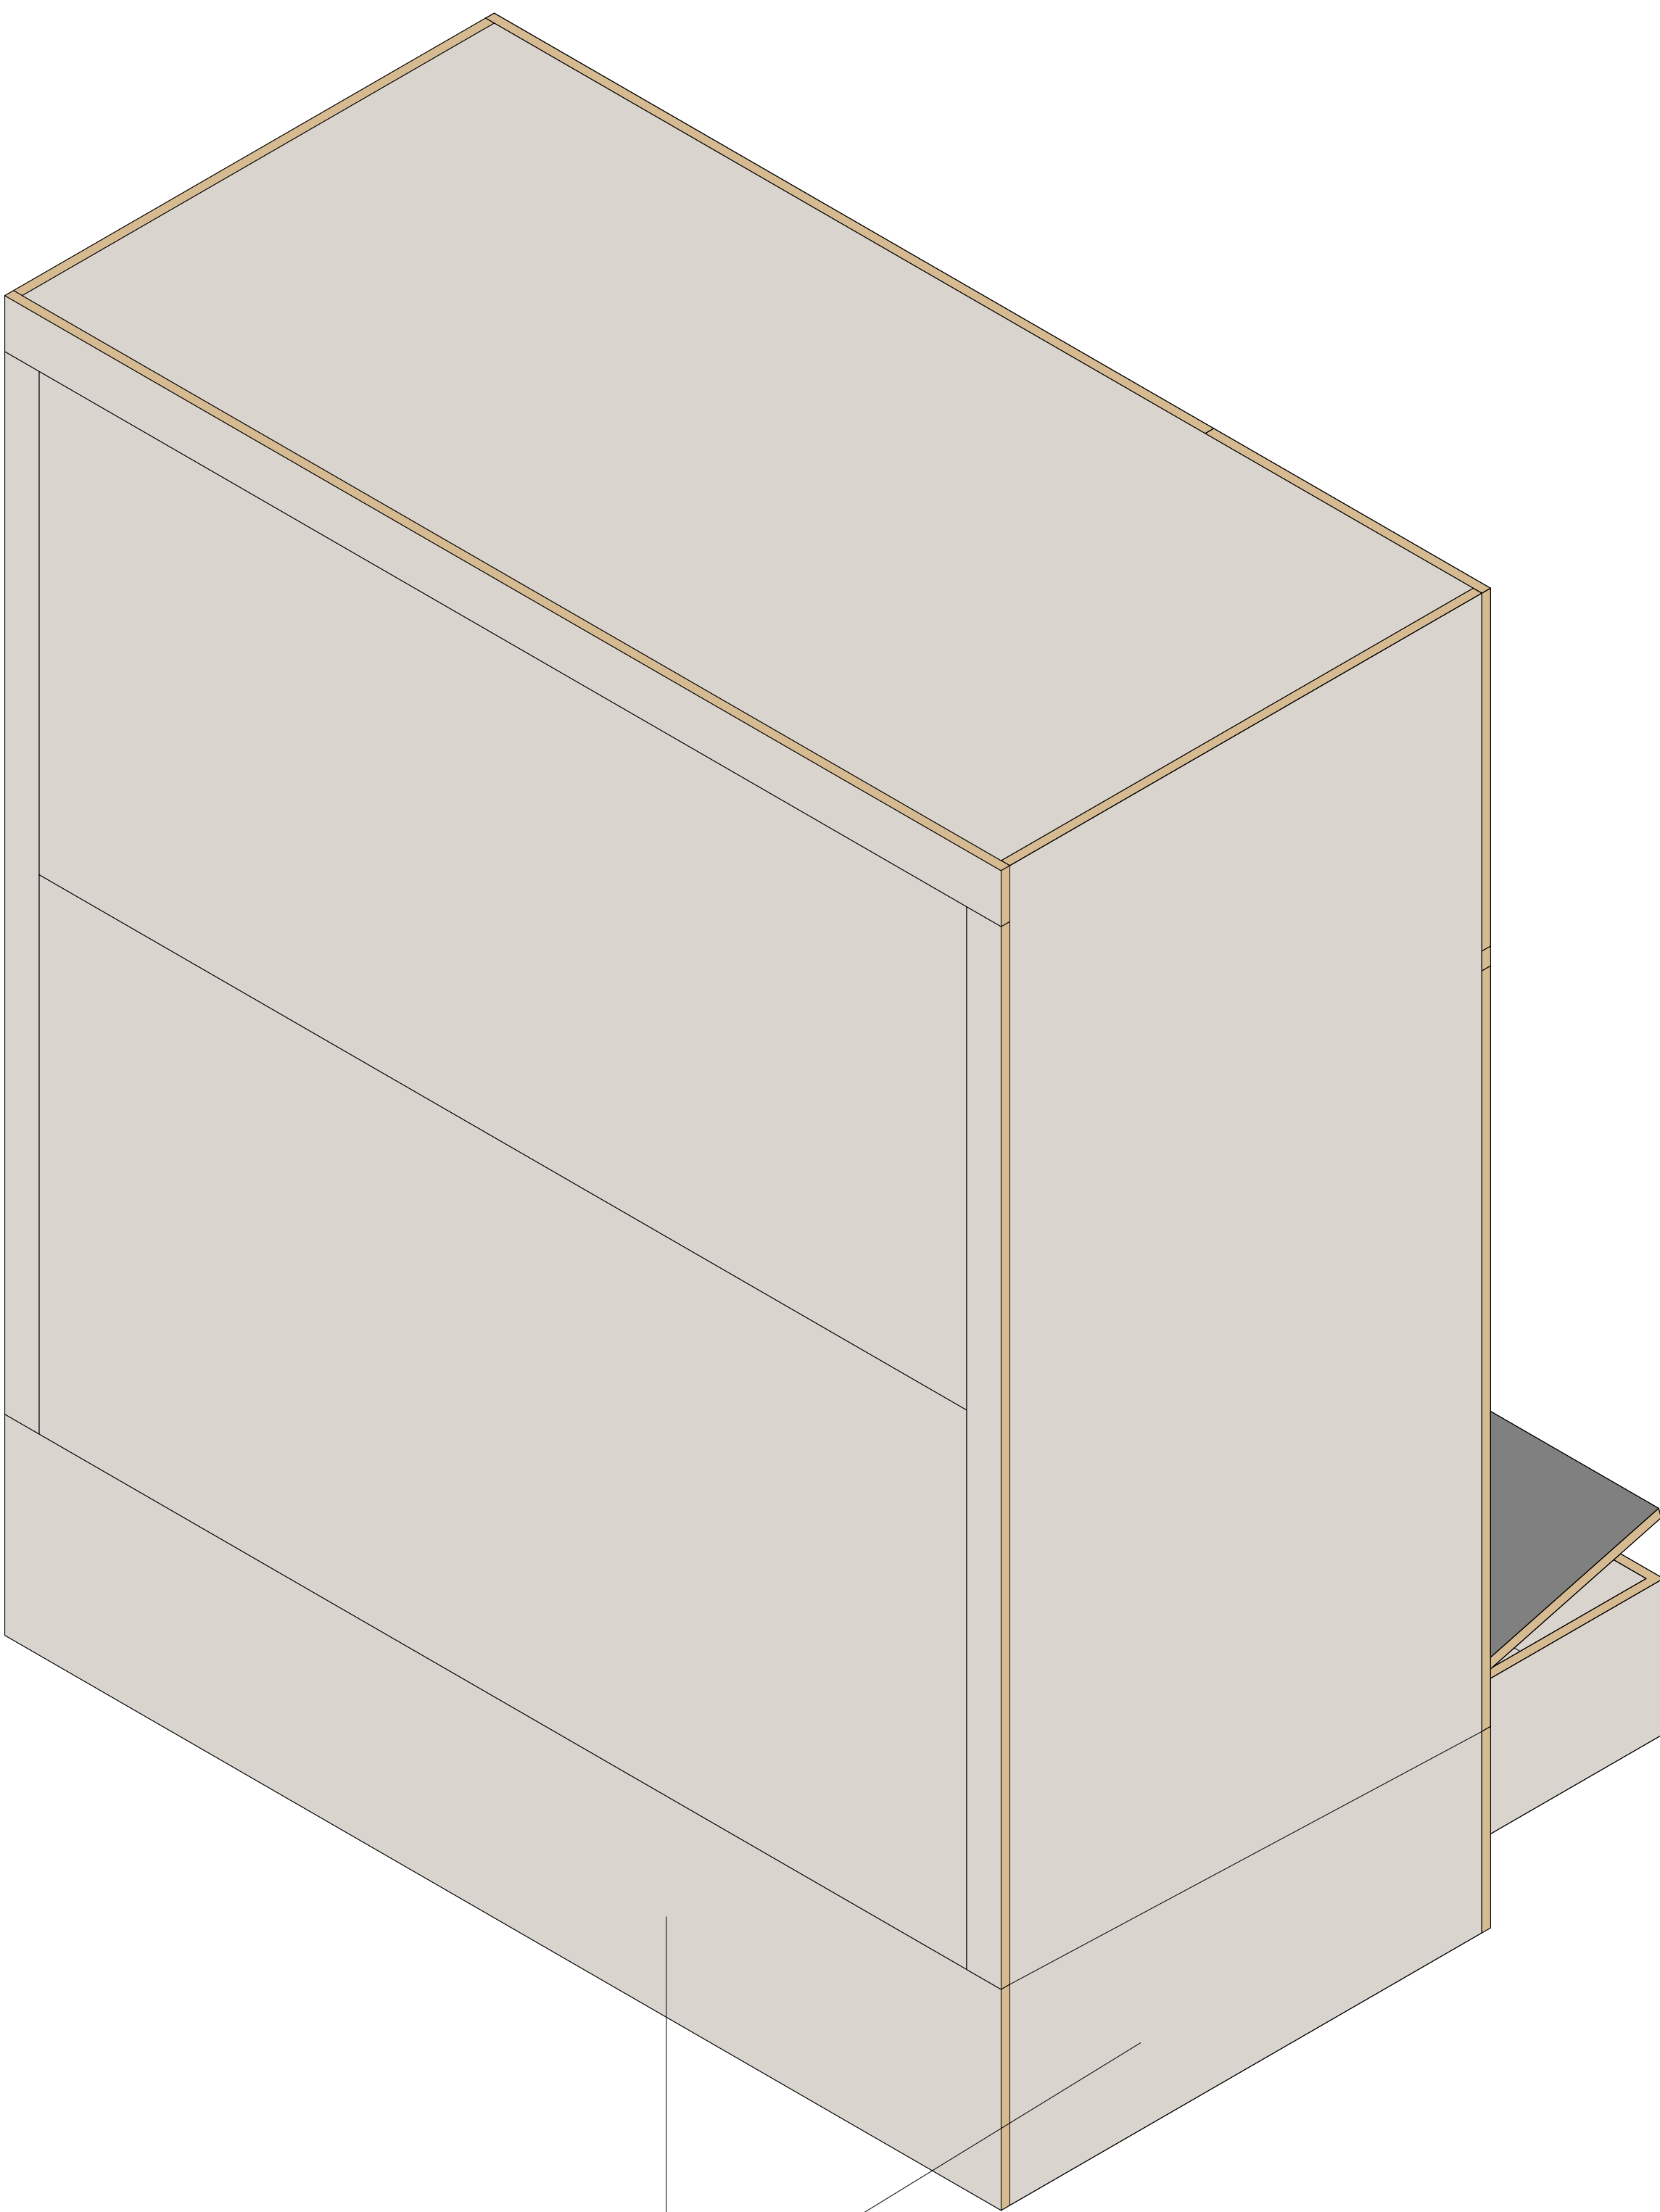



Lower side panels may be
removed to allow cable
connections.

DRAFT

DIMENSIONS

101 x 205.6 x 241.6 (WxLxH)cm

BUNKBEDS - TYPE 2-A - GA PLAN

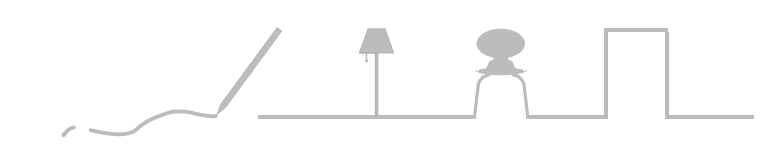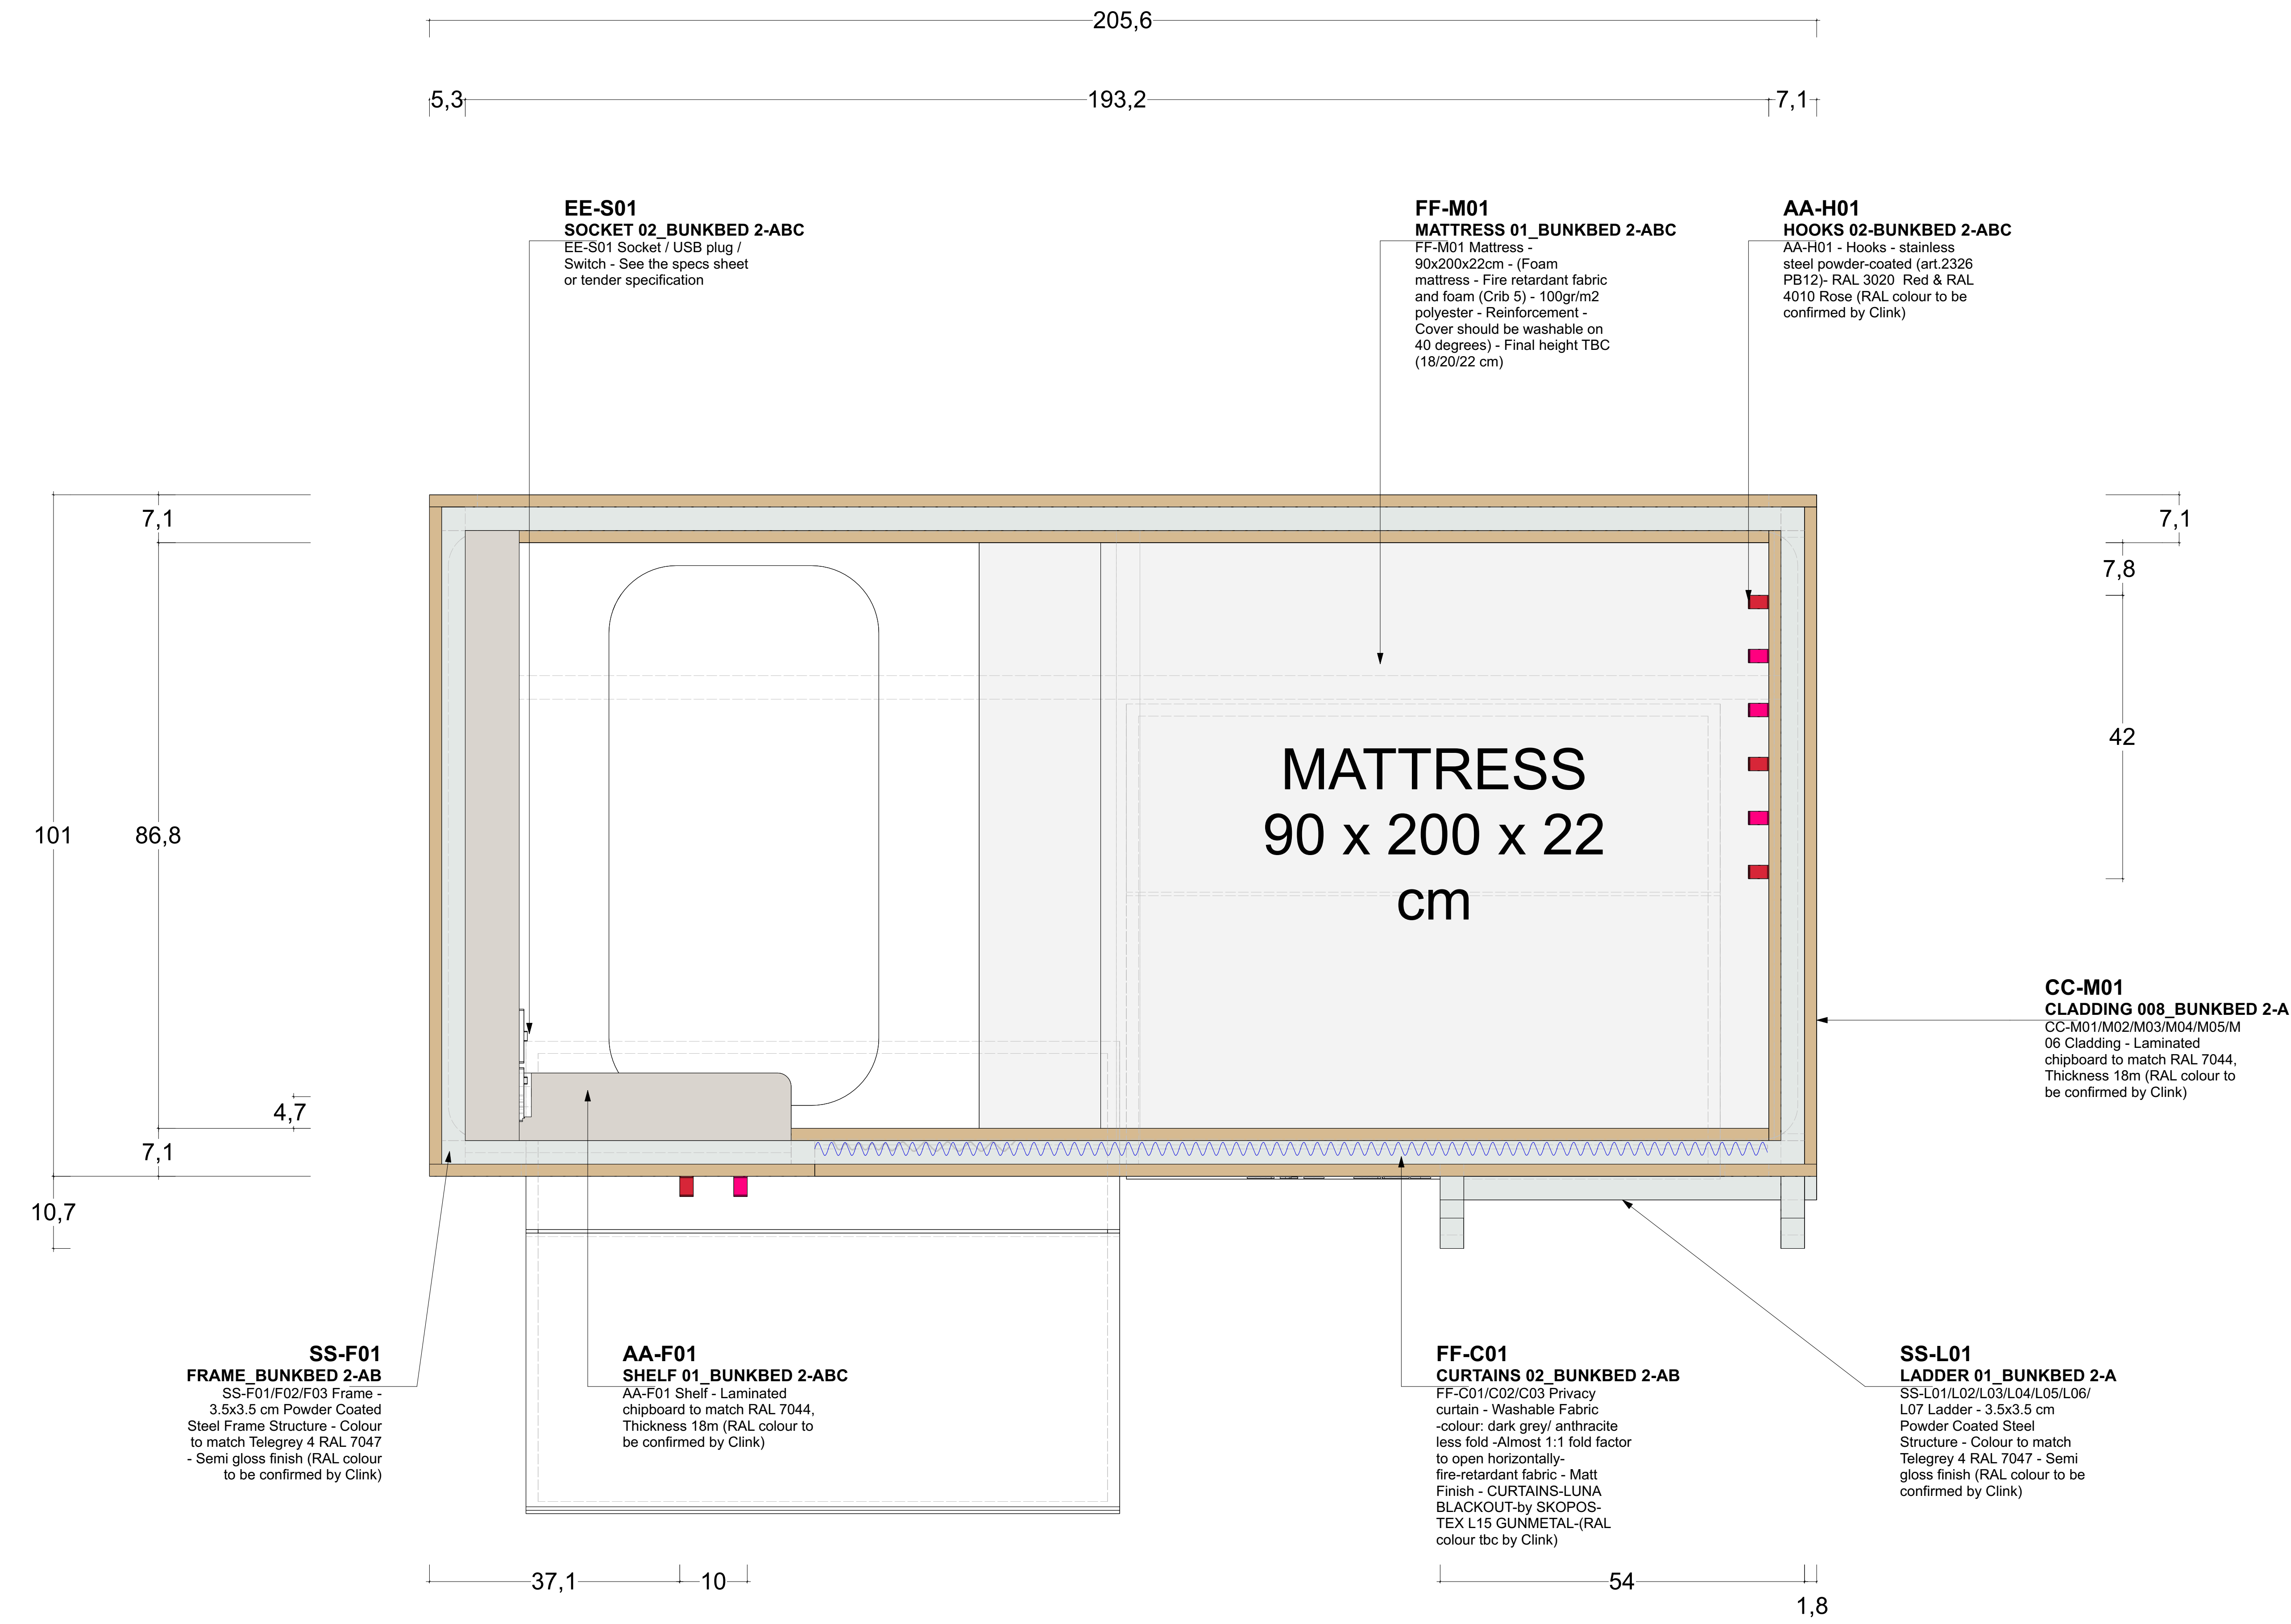

KEY

Index

A) 04.05.2026 Plan Set UP

All measurements have to be verified according to existing conditions by the contractor! Discrepancies must be reported immediately to the responsible project manager. The contractor has to produce fully dimensioned shop drawings prior to the start of the contract and they have to be approved by the client/ investor / interior designer

Project
CLINK 78 - BEDS



Project Address
CLINK 78
78 King's Cross Rd
London WC1X 9QG
United Kingdom

Client's Address
CLINK 78
78 King's Cross Rd
London WC1X 9QG
United Kingdom

Sheet Number	2-A-101	Total Sheets	82
--------------	---------	--------------	----


Sheet Title	BUNKBED 2-A GA	Level	
-------------	----------------	-------	--

File Name
260425_CLINK 78_BEDs AA DRAFT 03.vwx

Date	Sheet Size	Scale	Signed
28.04.26	A1	1:5	AA

Stefanie Jaensch INTERIOR DESIGNS
Global Headquarter | Stefanie Jaensch c/o WeWork
Taubusanlage 8 | 60329 Frankfurt a.M.
E-Mail info@stefaniejaensch.de | DE +49 (0) 174 6756098
www.stefaniejaensch.de
Legal address | Stefanie Jaensch | Offenbacher Landstraße 434 | 60599 Frankfurt a.M.
© 2023 All Rights Reserved | Stefanie Jaensch

BUNKBEDS - TYPE 2-A - FRONT ELEVATION

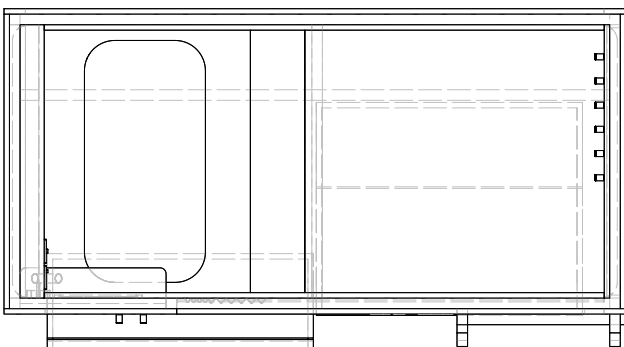

KEY

Index

A) 04.05.2026 Plan Set UP

All measurements have to be verified according to existing conditions by the contractor! Discrepancies must be reported immediately to the responsible project manager. The contractor has to produce fully dimensioned shop drawings prior to the start of the contract and they have to be approved by the client/ investor / interior designer

Project

CLINK 78 - BEDS

Logo



Project Address

CLINK 78
78 King's Cross Rd
London WC1X 9QG
United Kingdom

Client's Address

CLINK 78
78 King's Cross Rd
London WC1X 9QG
United Kingdom

Sheet Number 2-A-102

Total Sheets 82

Sheet Title
BUNKBED 2-A FRONT ELEVATION

Level


File Name

260425_CLINK 78_BEDs AA DRAFT 03.vwx

Date	Sheet Size	Scale	Signed
28.04.26	A1	1:8	AA

Stefanie Jaensch INTERIOR DESIGNS

Global Headquarter | Stefanie Jaensch c/o WeWork
Taubusanlage 8 | 60329 Frankfurt a.M.
E-Mail info@stefaniejaensch.de | DE +49 (0) 174 6756098
www.stefaniejaensch.de
Legal address | Stefanie Jaensch | Offenbacher Landstraße 434 | 60599 Frankfurt a.M.
© 2023 All Rights Reserved | Stefanie Jaensch

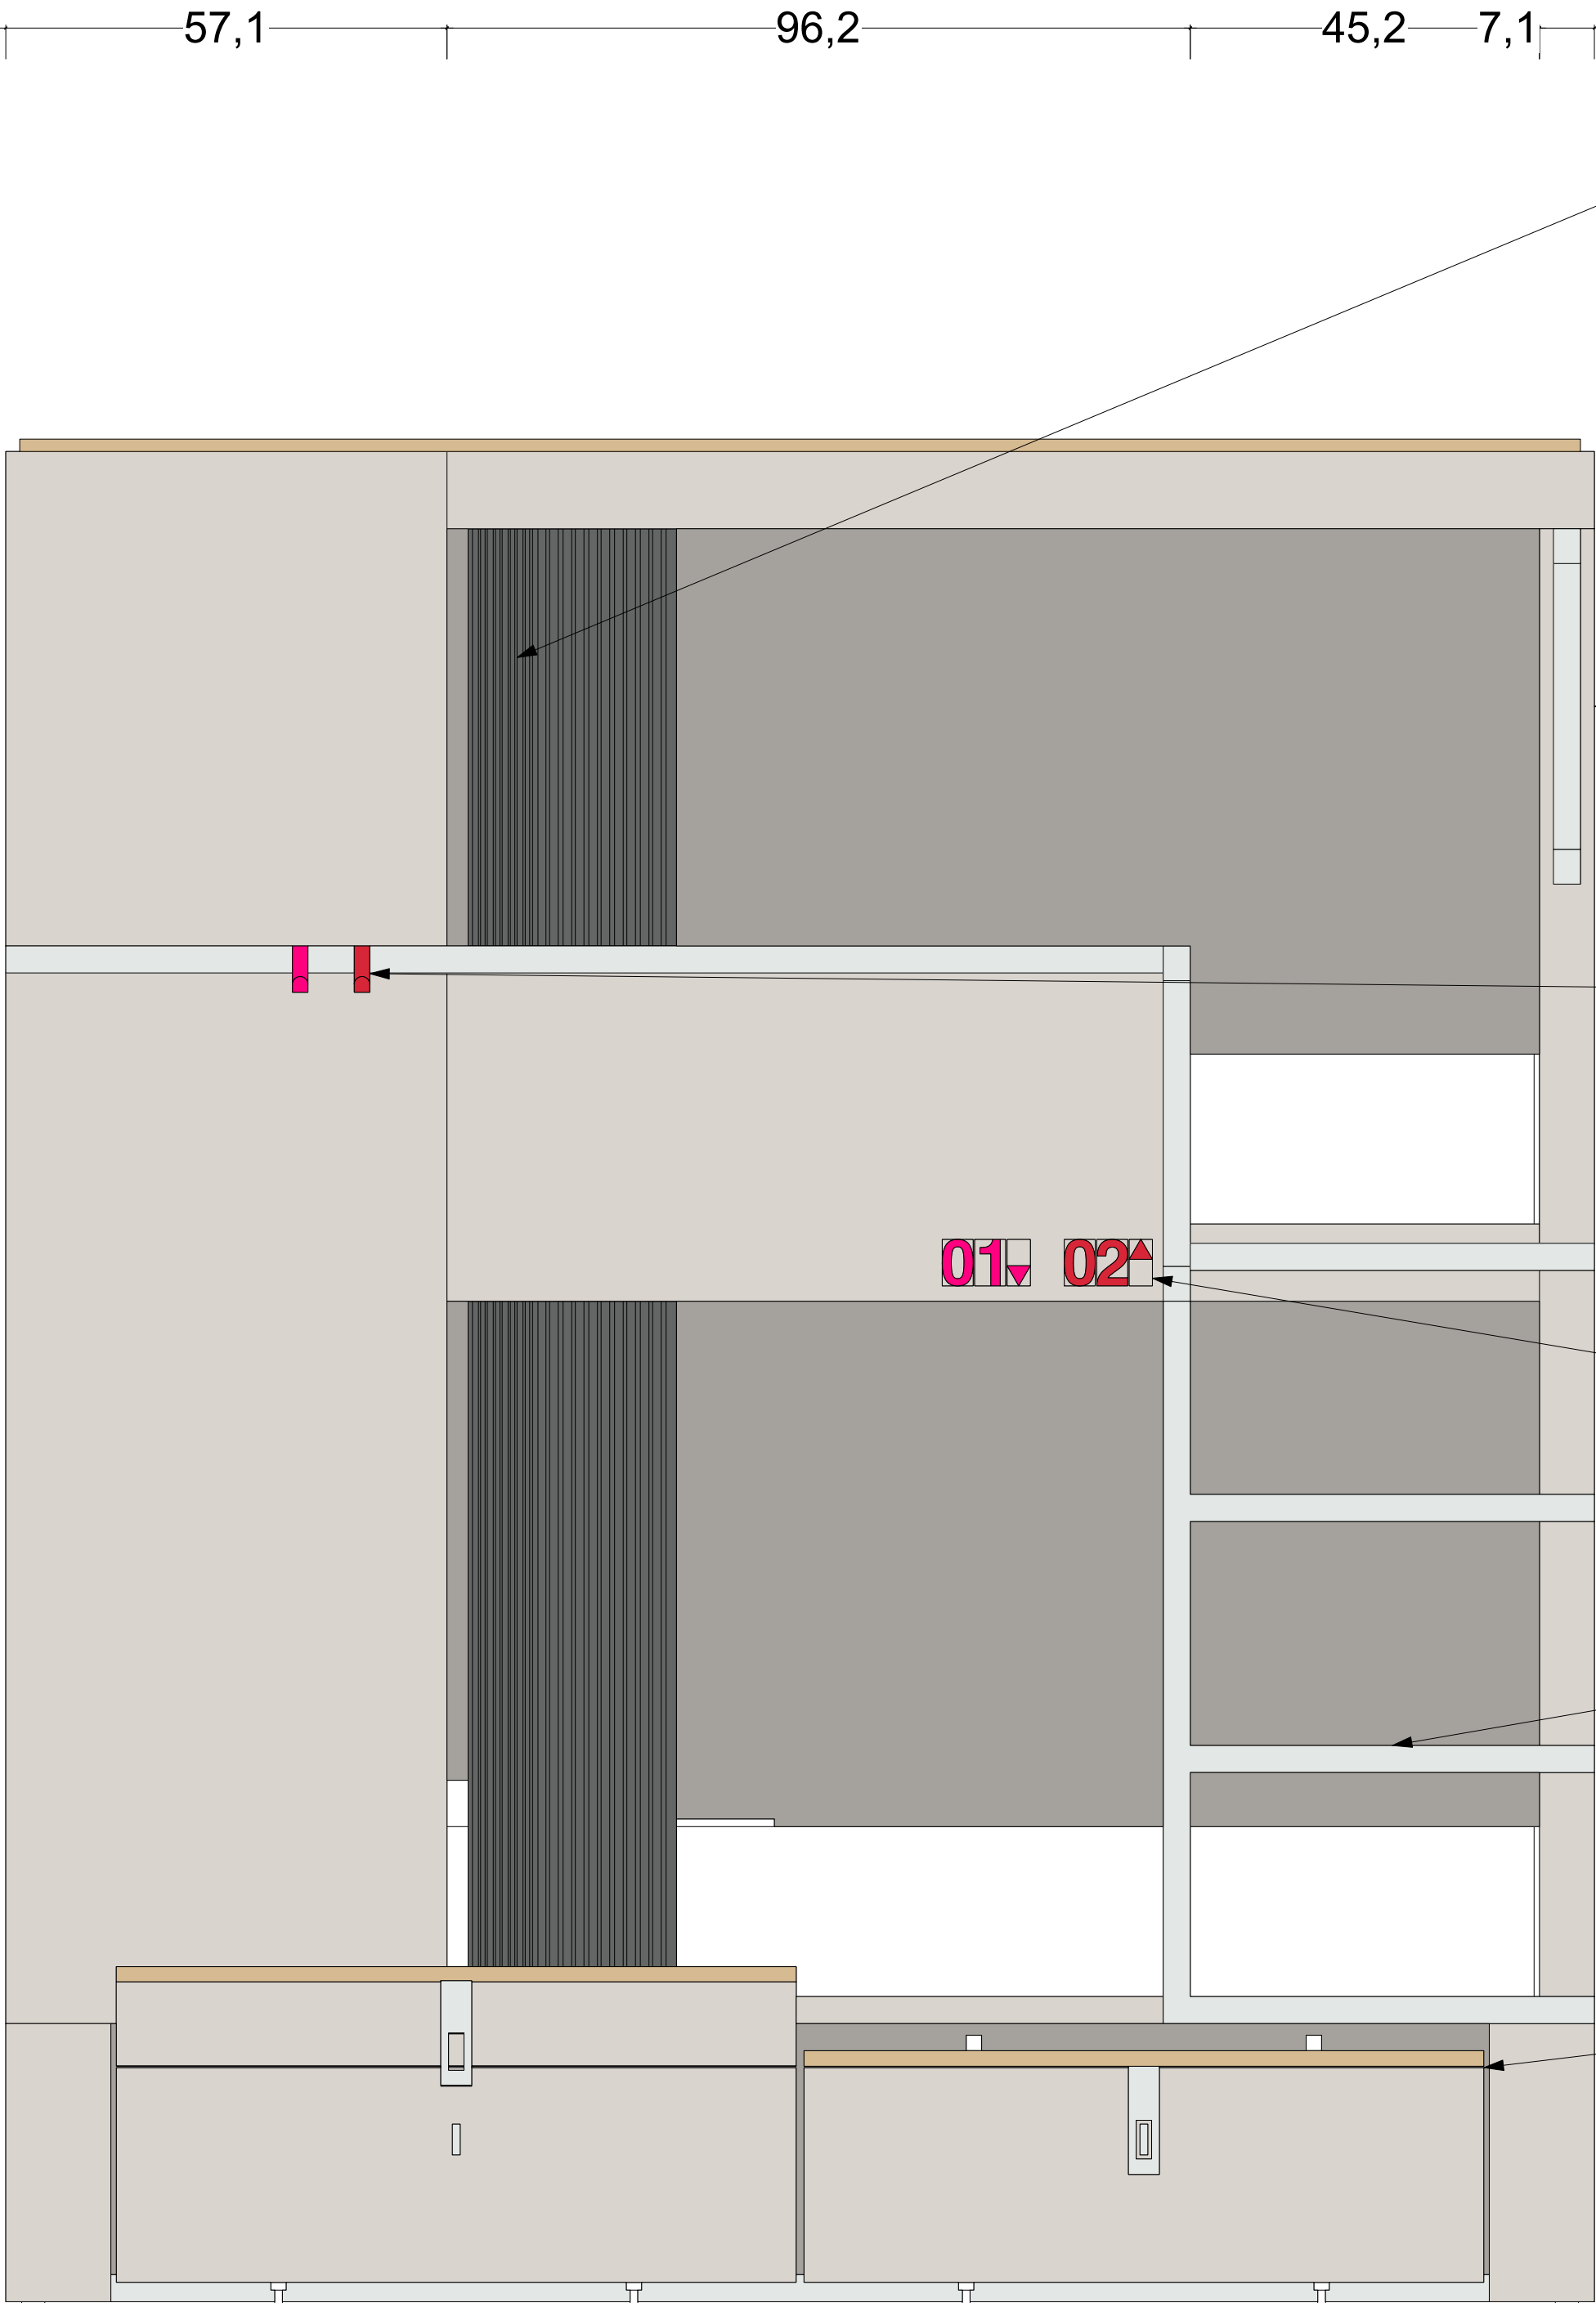

FF-C01
CURTAINS 02_BUNKBED 2-AB
FF-C01/C02/C03 Privacy
curtain - Washable Fabric
-colour: dark grey/ anthracite
less fold -Almost 1:1 fold factor
to open horizontally-
fire-retardant fabric - Matt
Finish - CURTAINS-LUNA
BLACKOUT-by SKOPOS-
TEX L15 GUNMETAL-(RAL
colour tbc by Clink)

CC-M01
CLADDING 006_BUNKBED 2-A
CC-M01/M02/M03/M04/M05/M
06 Cladding - Laminated
chipboard to match RAL 7044,
Thickness 18m (RAL colour to
be confirmed by Clink)


AA-H01
HOOKS 03-BUNKBED 2-ABC
AA-H01 - Hooks - stainless
steel powder-coated (art.2326
PB12)- RAL 3020 Red & RAL
4010 Rose (RAL colour to be
confirmed by Clink)

AA-S01
SIGNAGE 02_BUNKBED 2-ABC
AA-S01 SIGNAGE - Numbers
- laser-cut acrylic or MDF -
thickness 5mm - spray painted
- RAL 3020 Red & RAL 4010
Rose - font according to
wayfinding signage design
(RAL colour to be confirmed
by Clink)

SS-L01
LADDER 01_BUNKBED 2-A
SS-L01/L02/L03/L04/L05/L06/
L07 Ladder - 3.5x3.5 cm
Powder Coated Steel
Structure - Colour to match
Telegrey 4 RAL 7047 - Semi
gloss finish (RAL colour to be
confirmed by Clink)


CC-L01
CLADDING 001_LOCKER 2-A
CC-L01 LOCKER - Panels -
Laminated chipboard to match
RAL 7044, Thickness 18m
(RAL colour to be confirmed
by Clink)

BUNKBEDS - TYPE 2-A - BACK ELEVATION

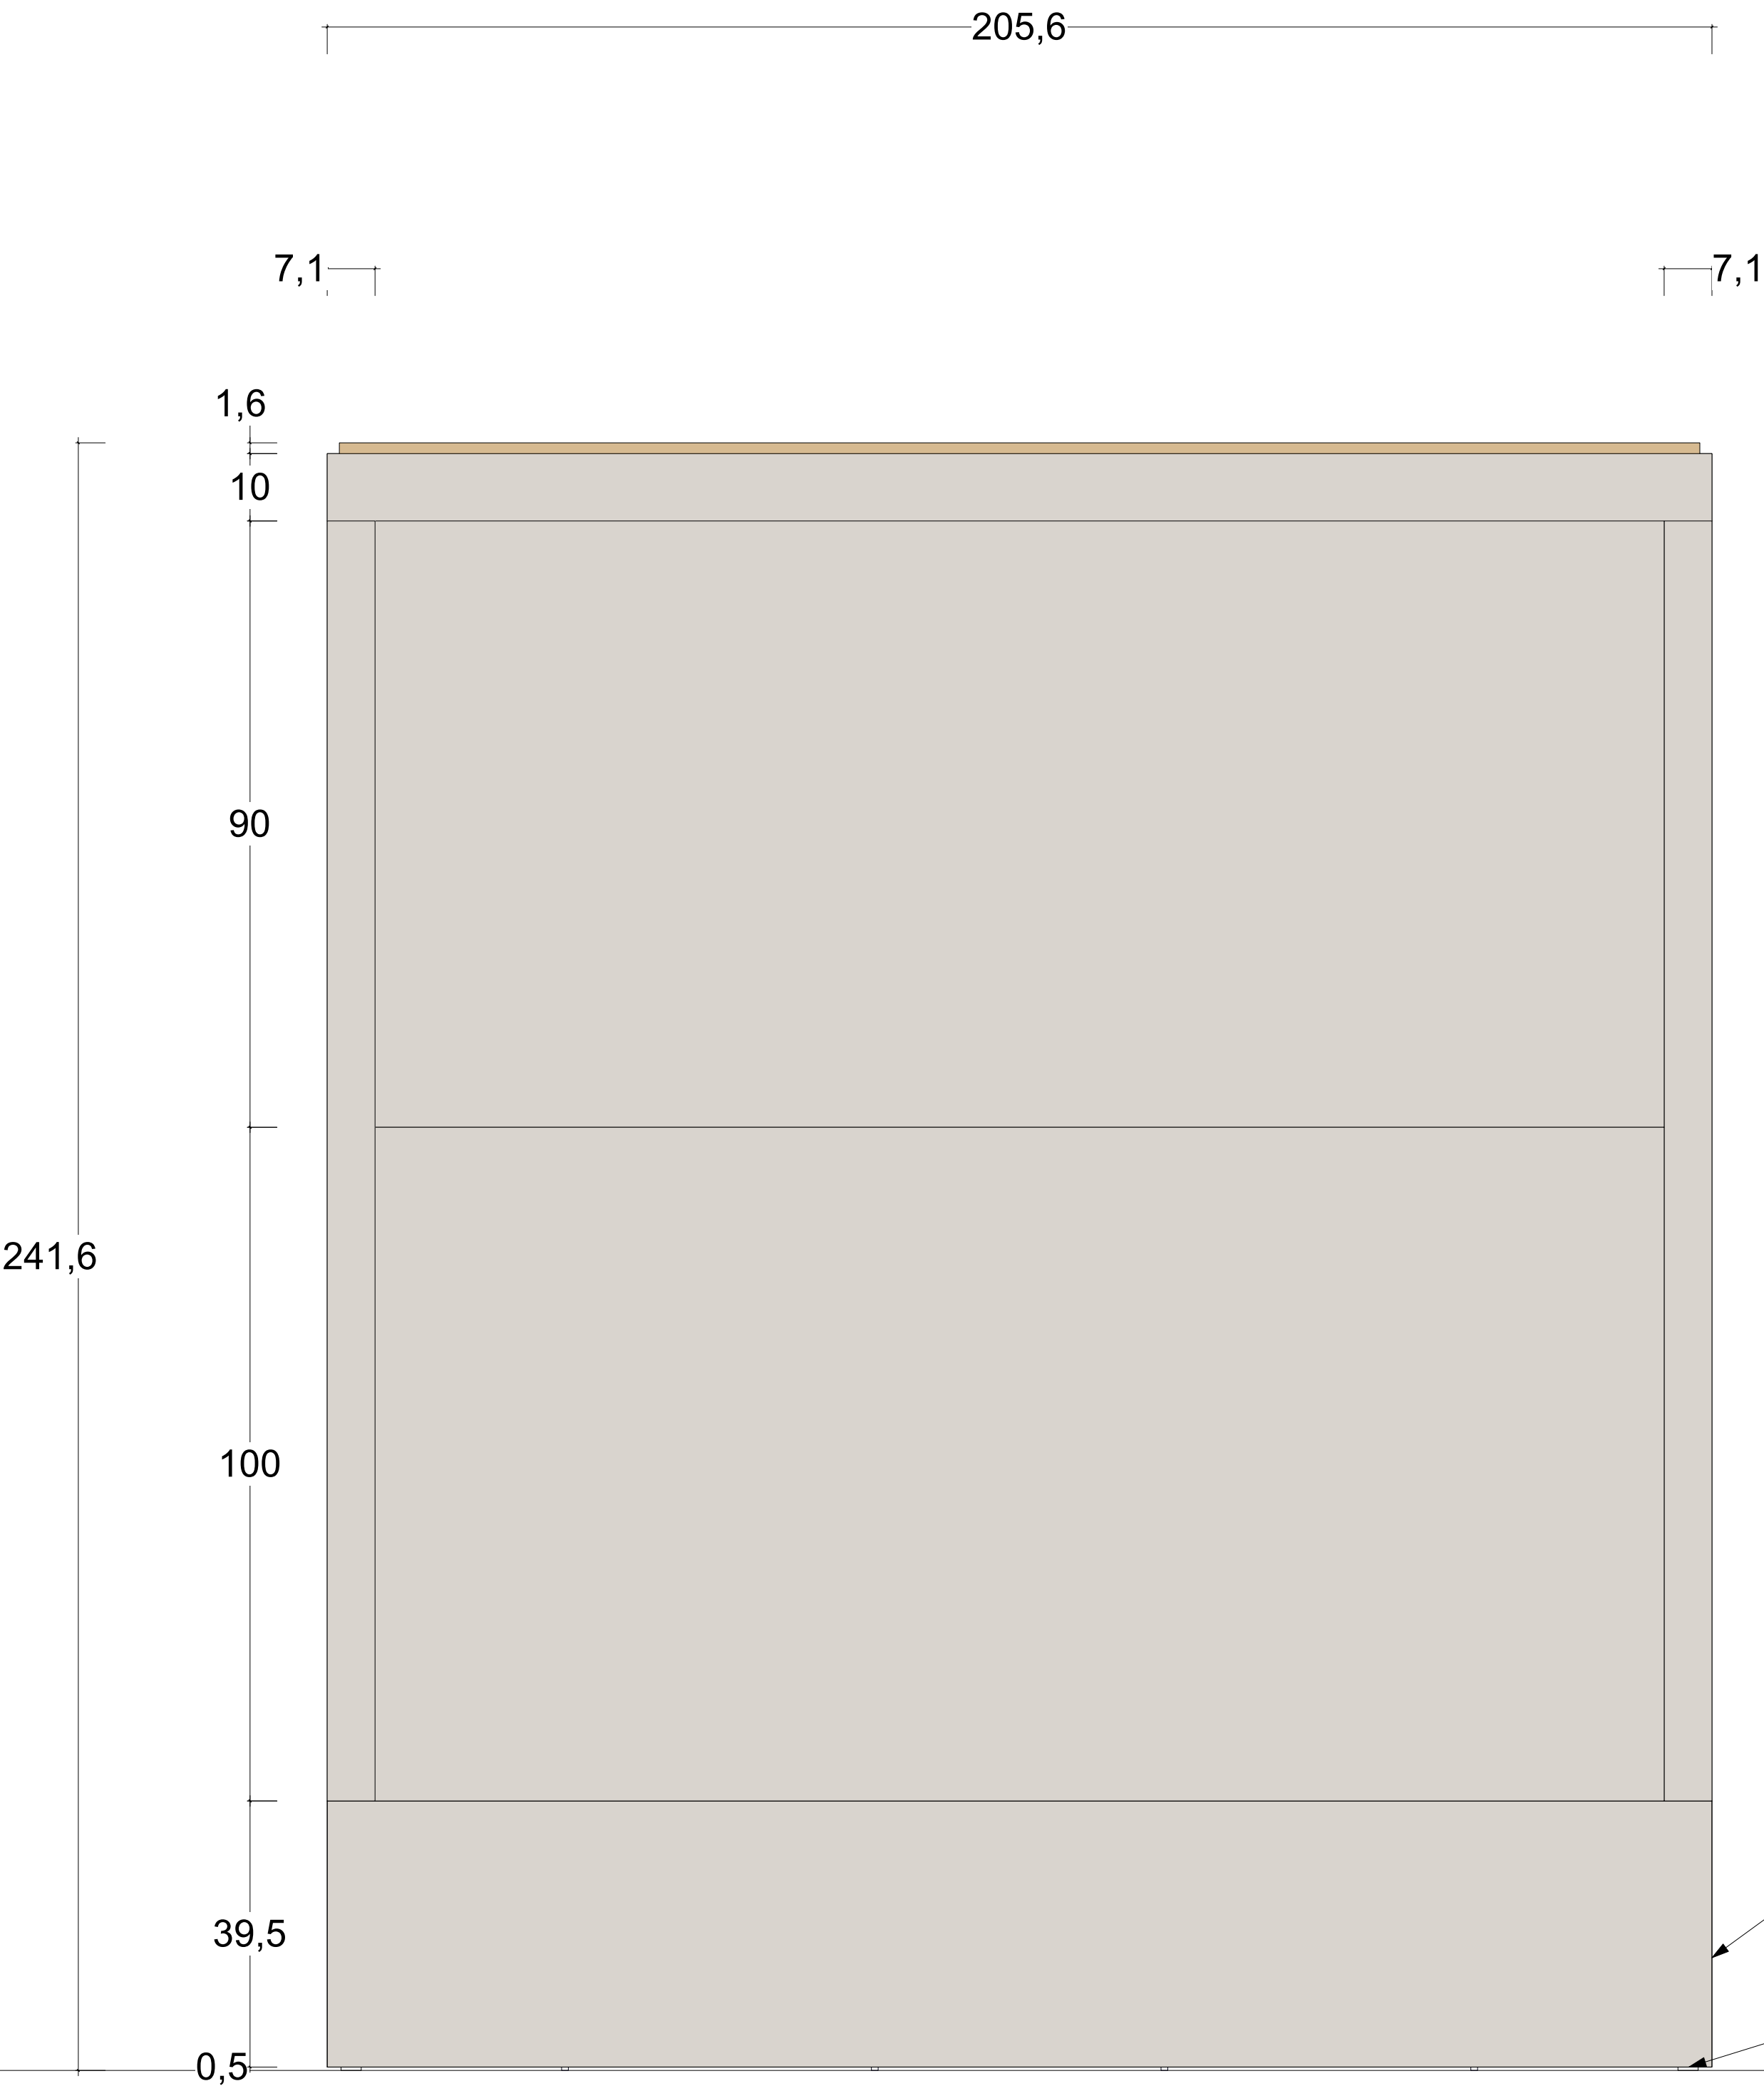

CC-M01
CLADDING 025_BUNKBED 2-A
CC-M01/M02/M03/M04/M05/M
06 Cladding - Laminated
chipboard to match RAL 7044,
Thickness 18m (RAL colour to
be confirmed by Clink)

SS-T01
FOOT_BUNKBED 2-ABC
SS-T01 Height Adjustable Feet

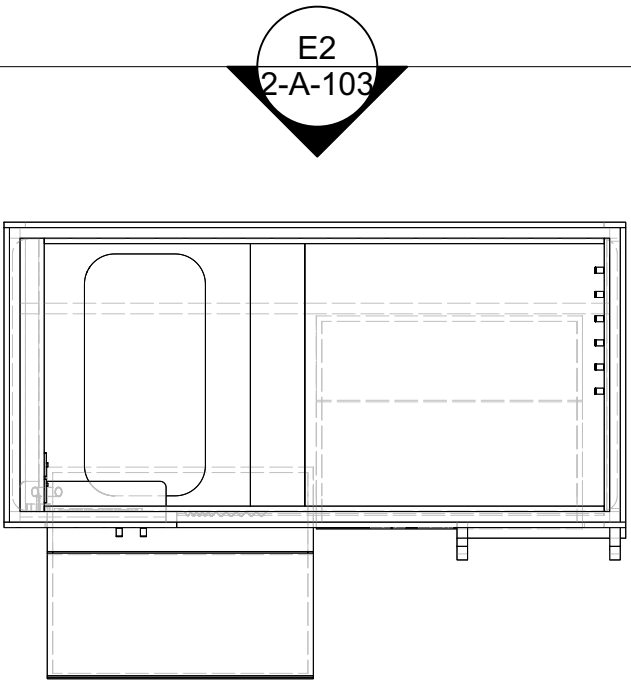

KEY

Index
A) 04.05.2026 Plan Set UP

All measurements have to be verified according to existing conditions by the contractor! Discrepancies must be reported immediately to the responsible project manager. The contractor has to produce fully dimensioned shop drawings prior to the start of the contract and they have to be approved by the client/ investor / interior designer

Project
CLINK 78 - BEDS





Project Address
CLINK 78
78 King's Cross Rd
London WC1X 9QG
United Kingdom

Client's Address
CLINK 78
78 King's Cross Rd
London WC1X 9QG
United Kingdom

Sheet Number 2-A-103		Total Sheets 82
Sheet Title BUNKBED 2-A BACK ELEVATION		Level
File Name 260425_CLINK 78_BEDs AA DRAFT 03.vwx		

Date	Sheet Size	Scale	Signed
28.04.26	A1	1:8	AA

Stefanie Jaensch INTERIOR DESIGNS
Global Headquarter | Stefanie Jaensch c/o WeWork
Taunusanlage 8 | 60329 Frankfurt a.M.
E-Mail info@stefaniejaensch.de | DE +49 (0) 174 6756098
www.stefaniejaensch.de
Legal address | Stefanie Jaensch | Offenbacher Landstraße 434 | 60599 Frankfurt a.M.
© 2023 All Rights Reserved | Stefanie Jaensch

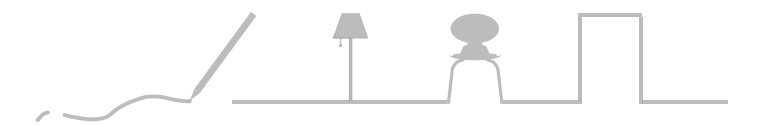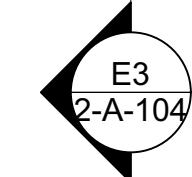

CLINK 78
78 King's Cross Rd
London WC1X 9QG
United Kingdom

Stefanie Jaensch INTERIOR DESIGNS


Global Headquarter | Stefanie Jaensch c/o WeWork
Taunusanlage 8 | 60329 Frankfurt a.M.

E-Mail info@stefaniejaensch.de | DE +49 (0) 174 6756098


www.stefaniejaensch.de

Legal address | Stefanie Jaensch | Offenbacher Landstraße 434 | 60599 Frankfurt a.M.


© 2023 All Rights Reserved | Stefanie Jaensch

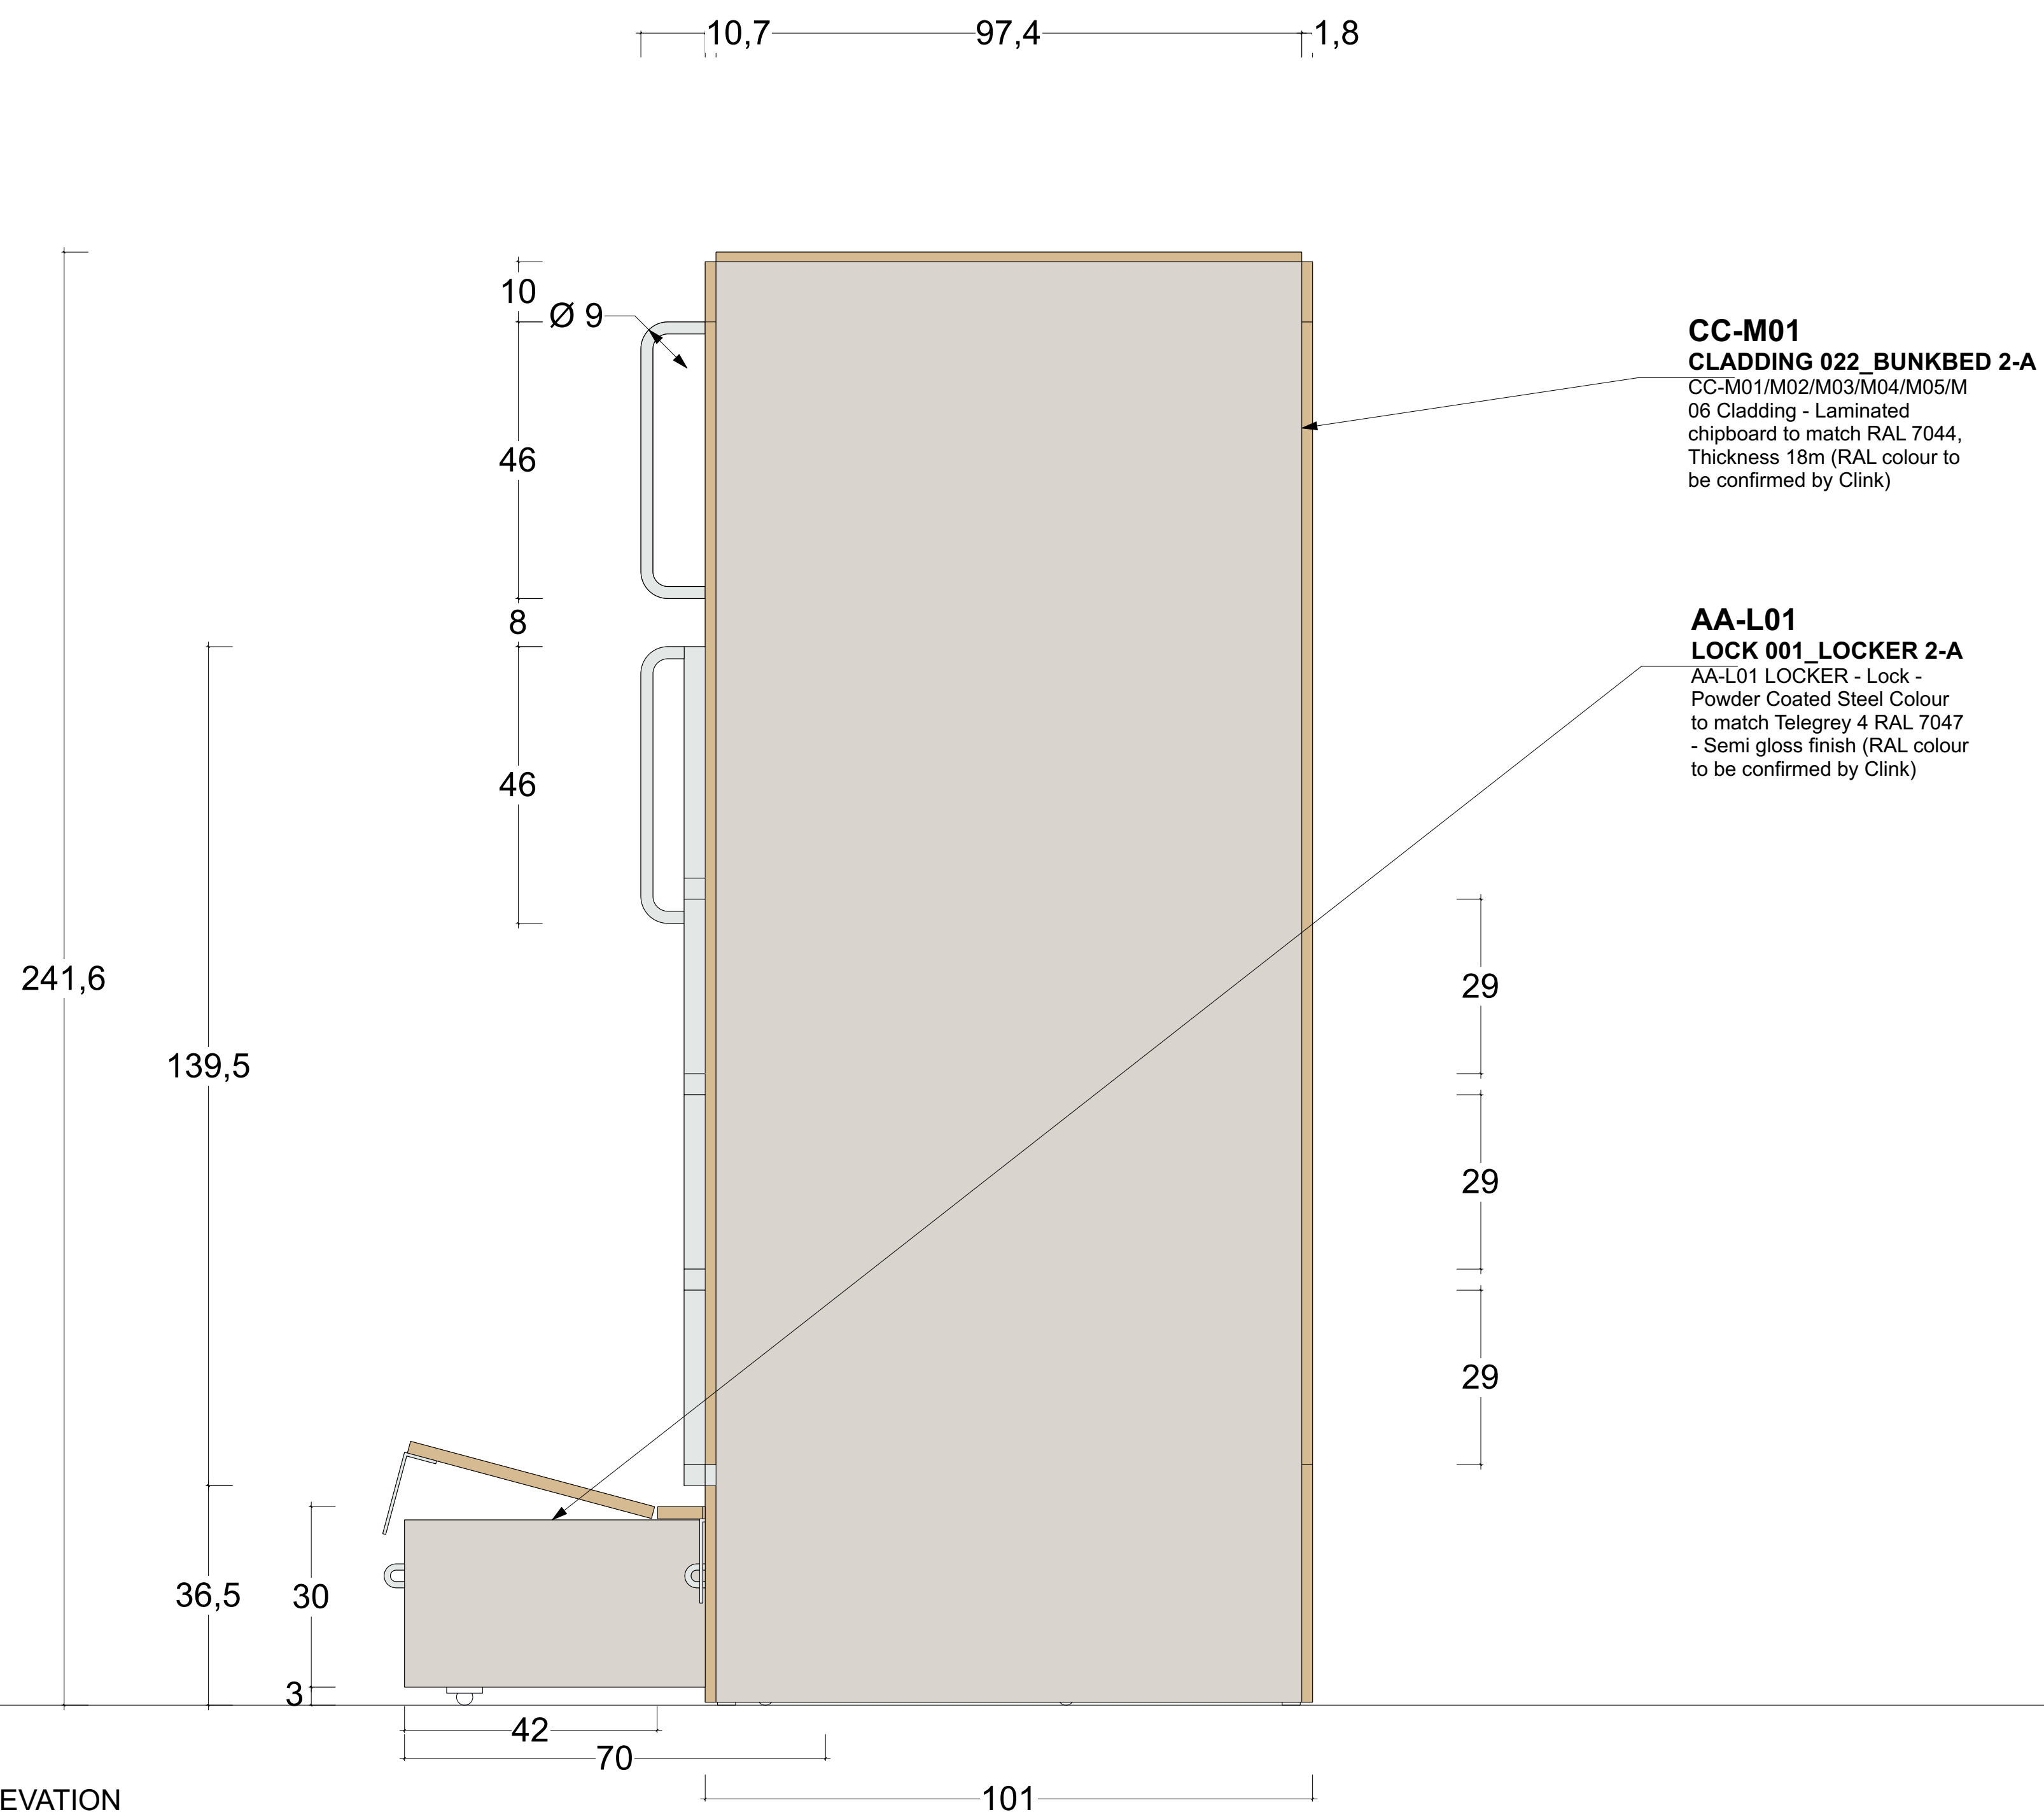

BUNKBEDS - TYPE 2-A - LEFT ELEVATION

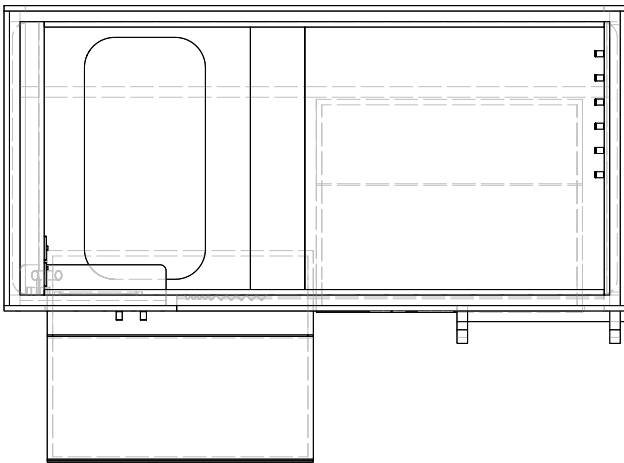

E4
2-A-105

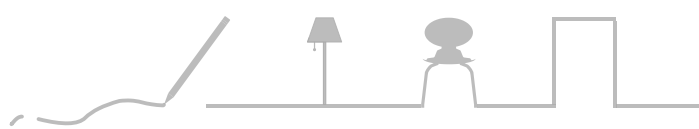

KEY

Index
A) 04.05.2026 Plan Set UP

All measurements have to be verified according to existing conditions by the contractor! Discrepancies must be reported immediately to the responsible project manager. The contractor has to produce fully dimensioned shop drawings prior to the start of the contract and they have to be approved by the client/ investor / interior designer

Project
CLINK 78 - BEDS



Project Address
CLINK 78
78 King's Cross Rd
London WC1X 9QG
United Kingdom

Client's Address
CLINK 78
78 King's Cross Rd
London WC1X 9QG
United Kingdom

Sheet Number	2-A-105	Total Sheets	82
--------------	---------	--------------	----

Sheet Title	BUNKBED 2-A LEFT ELEVATION	Level	
-------------	----------------------------	-------	--

File Name
260425_CLINK 78_BEDs AA DRAFT 03.vwx

Date	Sheet Size	Scale	Signed
28.04.26	A1	1:8	AA

Stefanie Jaensch INTERIOR DESIGNS

Global Headquarter | Stefanie Jaensch c/o WeWork

Taunusanlage 8 | 60329 Frankfurt a.M.


E-Mail info@stefaniejaensch.de | DE +49 (0) 174 6756098

www.stefaniejaensch.de

Legal address | Stefanie Jaensch | Offenbacher Landstraße 434 | 60599 Frankfurt a.M.


© 2023 All Rights Reserved | Stefanie Jaensch

101 10,7

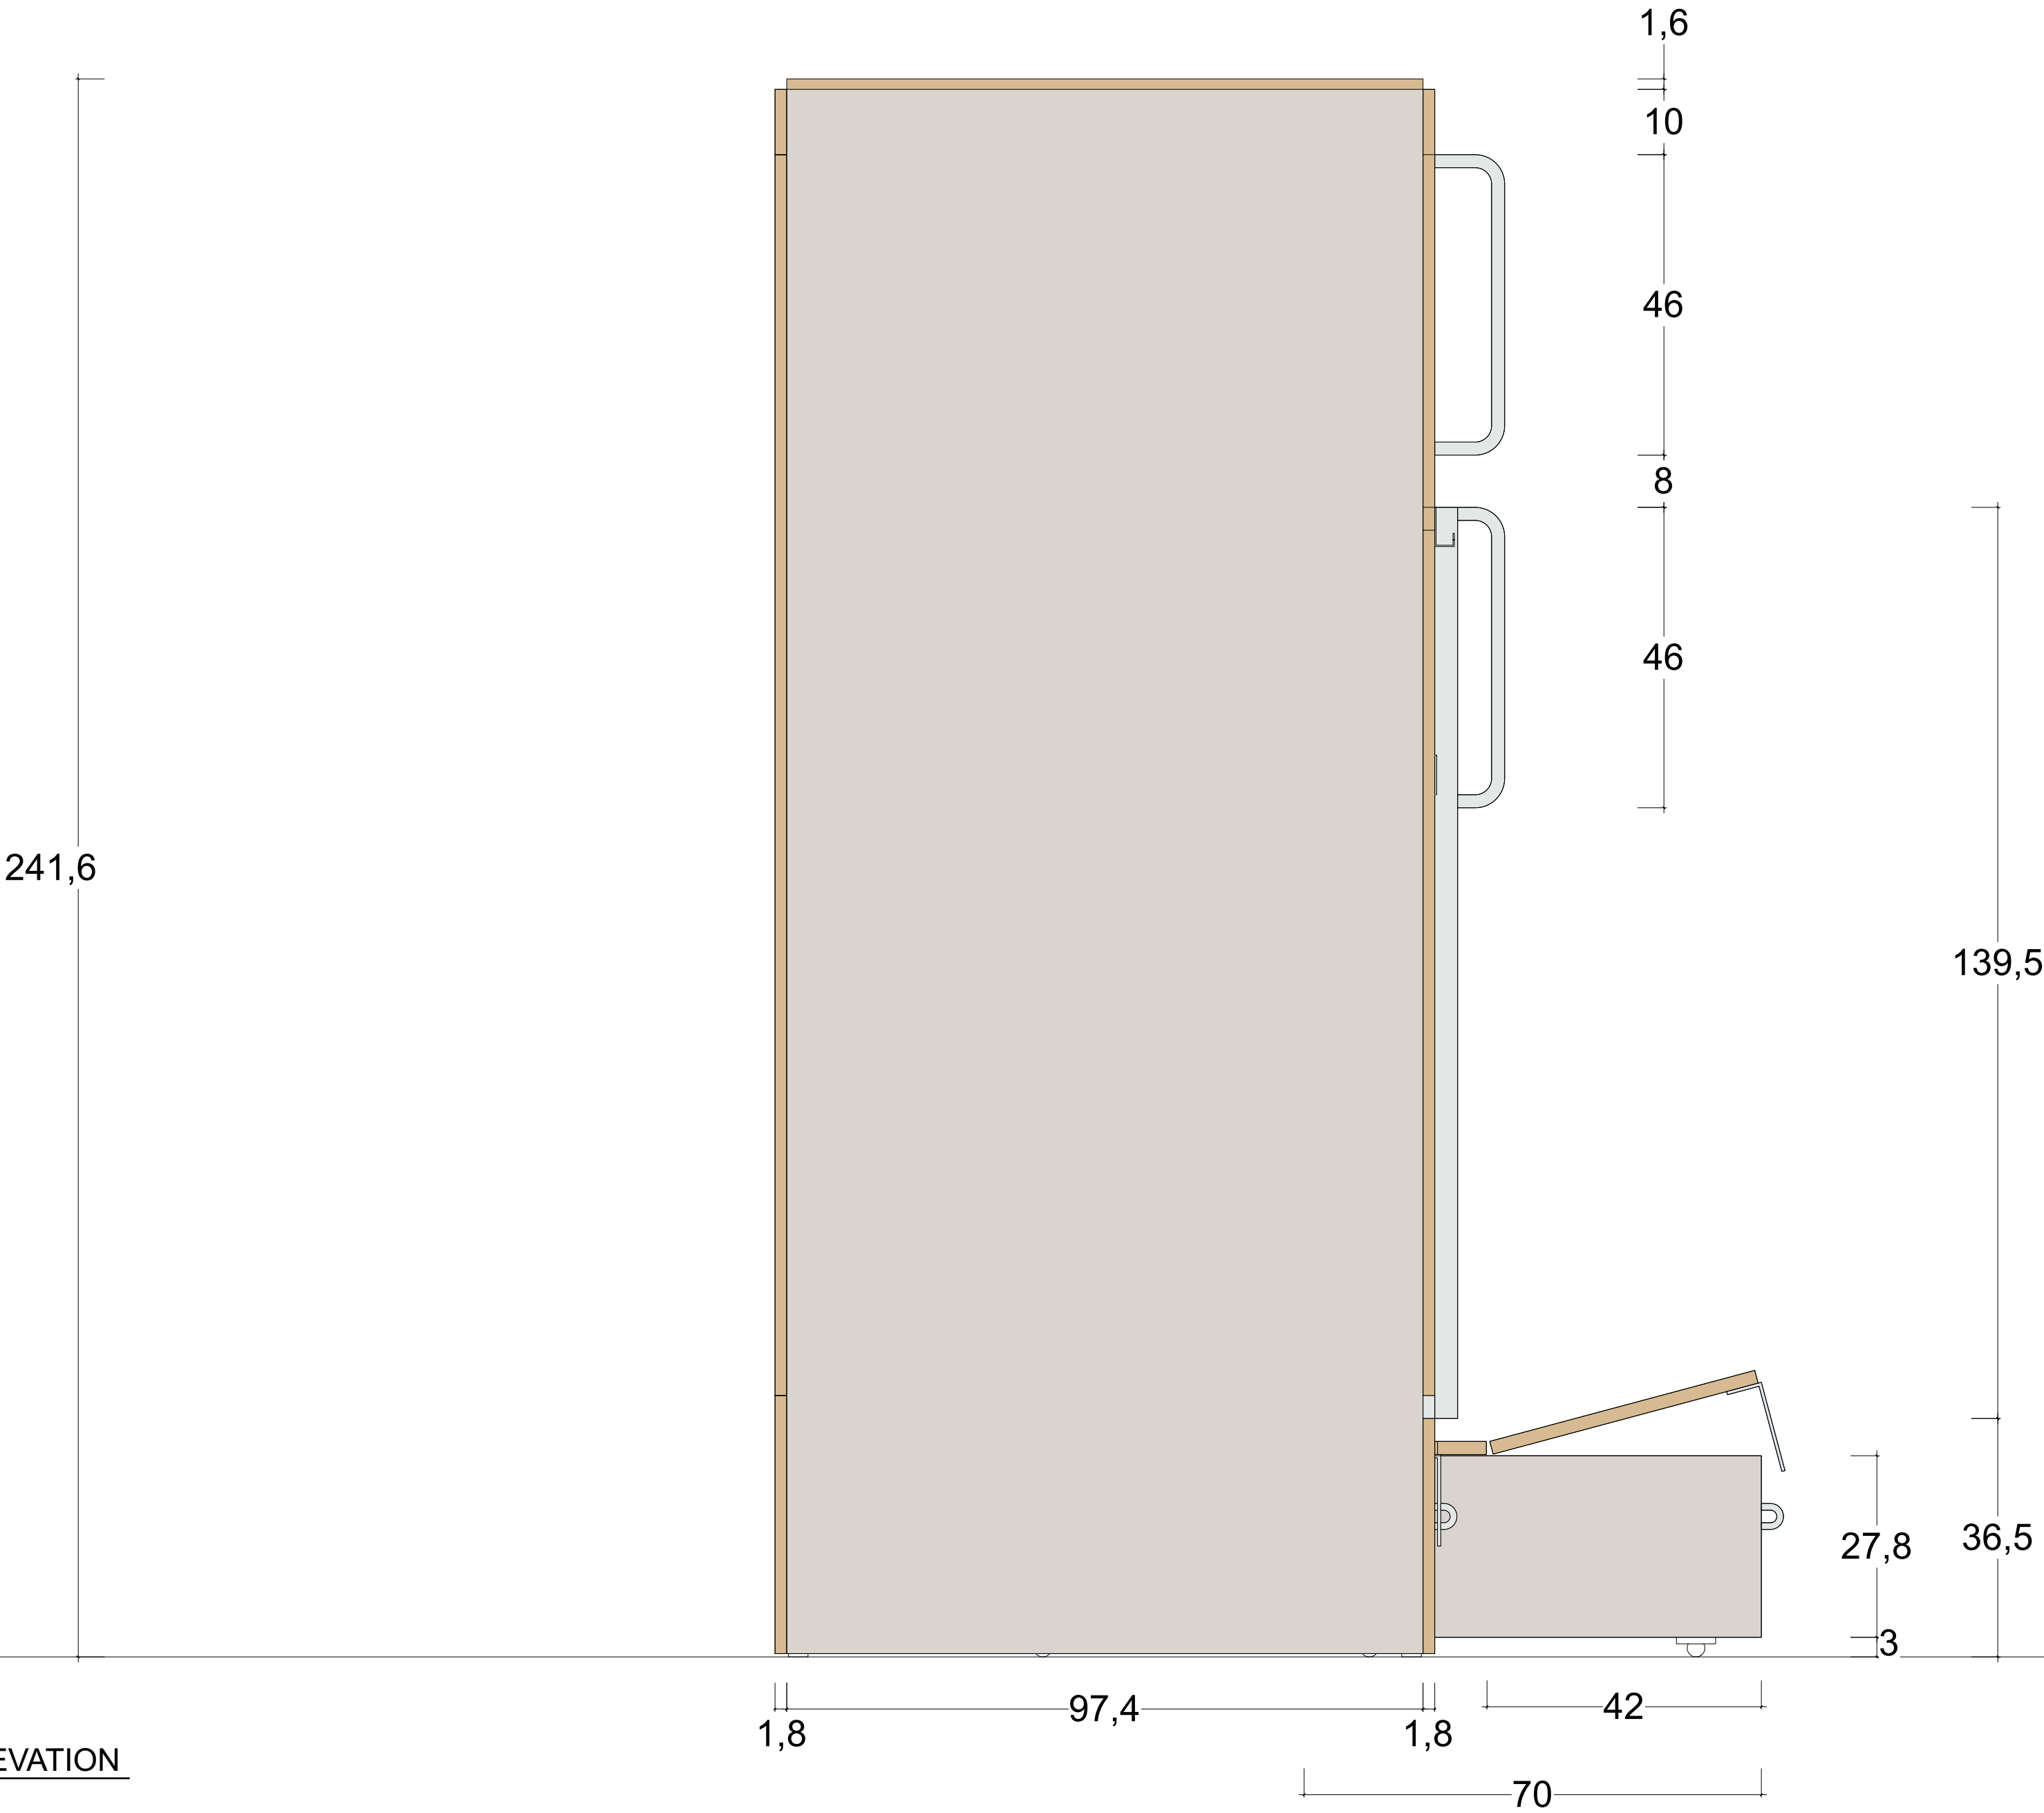

1,8 97,4 1,8 42 70

BUNKBEDS - TYPE 2-A - SECTION 1

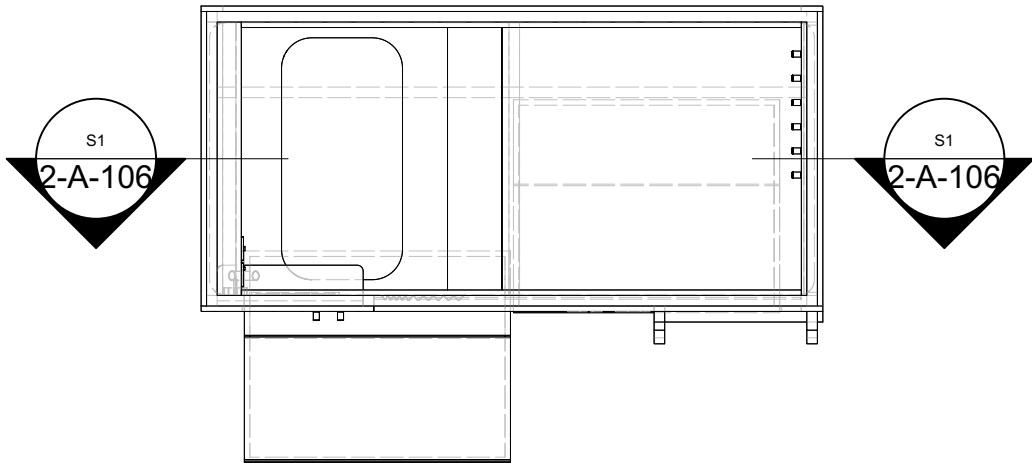

KEY

Index

A) 04.05.2026 Plan Set UP

All measurements have to be verified according to existing conditions by the contractor! Discrepancies must be reported immediately to the responsible project manager. The contractor has to produce fully dimensioned shop drawings prior to the start of the contract and they have to be approved by the client/ investor / interior designer

Project

CLINK 78 - BEDS

Logo



Project Address

CLINK 78
78 King's Cross Rd
London WC1X 9QG
United Kingdom

Client's Address

CLINK 78
78 King's Cross Rd
London WC1X 9QG
United Kingdom

Sheet Number 2-A-106

Total Sheets 82

Sheet Title
BUNKBED 2-A SECTION 1

Level

File Name


260425_CLINK 78_BEDs AA DRAFT 03.vwx

Date	Sheet Size	Scale	Signed
28.04.26	A1	1:8	AA




Stefanie Jaensch INTERIOR DESIGNS

Global Headquarter | Stefanie Jaensch c/o WeWork
Taunusanlage 8 | 60329 Frankfurt a.M.
E-Mail info@stefaniejaensch.de | DE +49 (0) 174 6756098
www.stefaniejaensch.de


Legal address | Stefanie Jaensch | Offenbacher Landstraße 434 | 60599 Frankfurt a.M.
© 2023 All Rights Reserved | Stefanie Jaensch

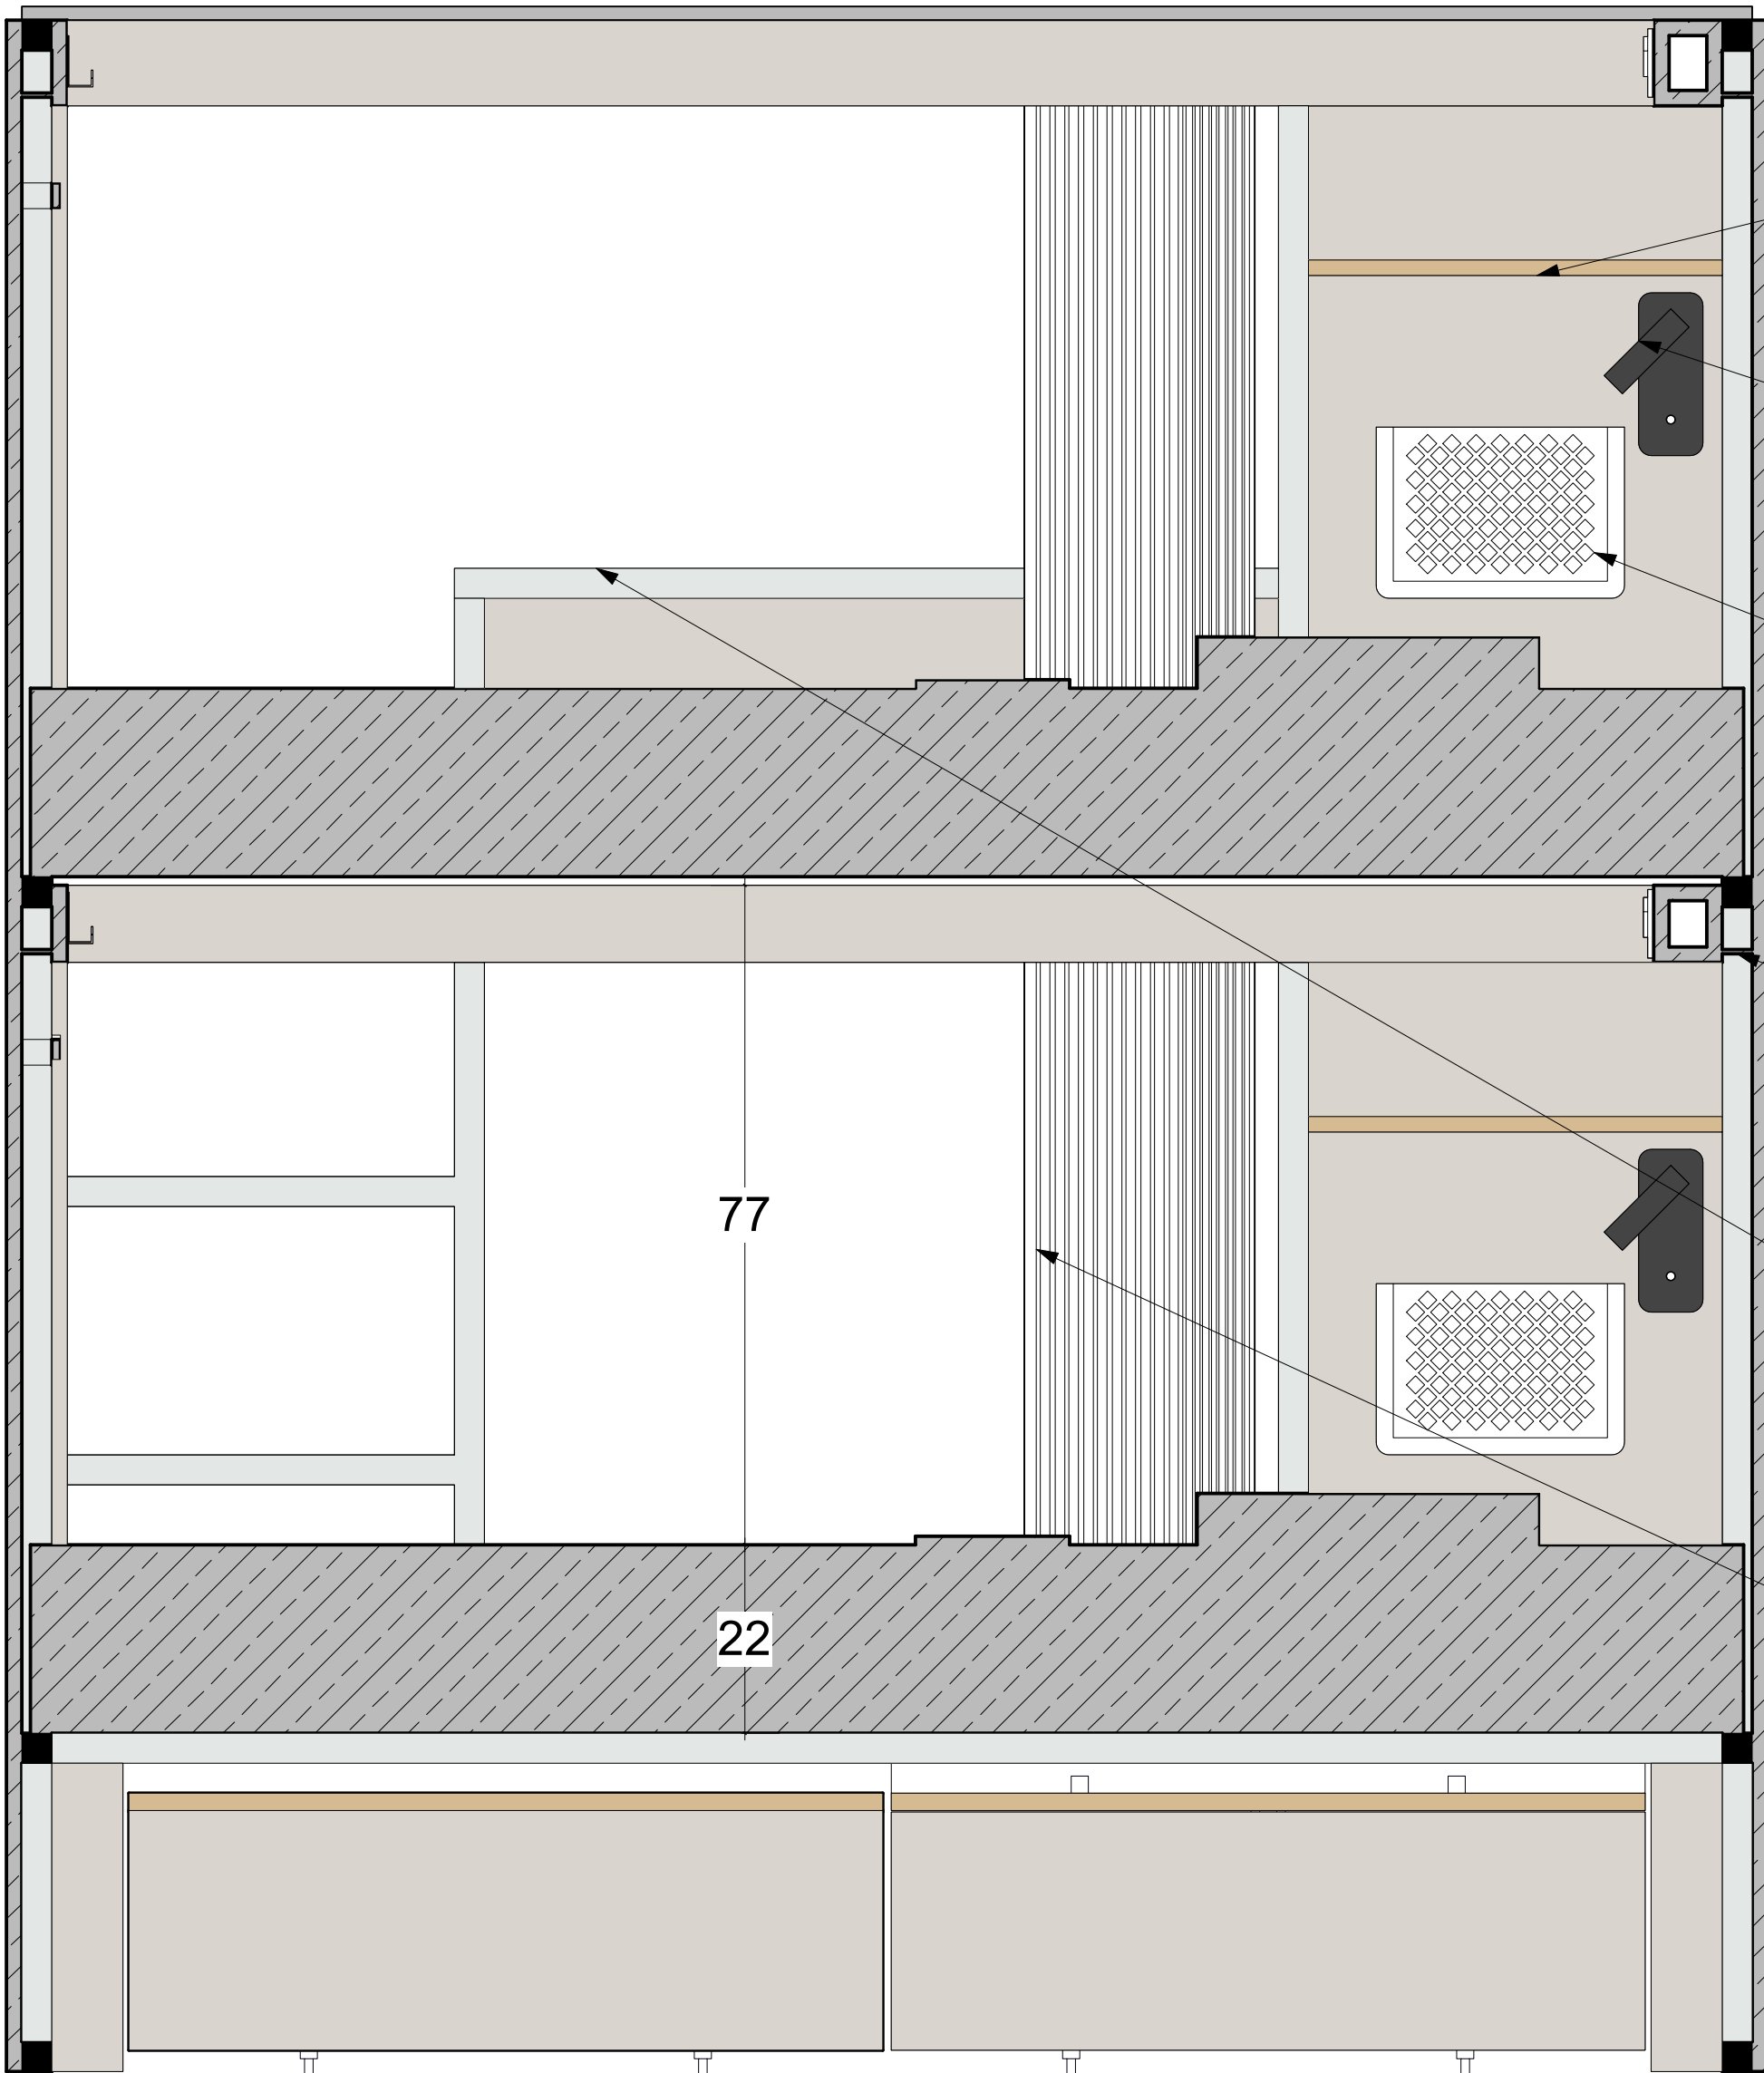

- AA-F01**
SHELF 02_BUNKBED 2-ABC
AA-F01 Shelf - Laminated chipboard to match RAL 7044, Thickness 18mm (RAL colour to be confirmed by Clink)
- EE-L07**
READING LIGHT 004_BUNKBED 2-ABC
EE-L07 Reading light - Aron 16/3240 Wall Lamp Textured Black,
- AA-M01**
MESH POCKET 004_BUNKBED 2-ABC
AA-M01 Mesh pocket 30x20cm frame: white - net: white - 2 pc. per bunk bed (final colour to be confirmed by Clink)
- EE-L01**
LED LIGHT 003_BUNKBED 2A
EE-L01/L02/L03/L04/L05/L06 LED light with light diffuser - LED stripes - 2000 Calvin - Warmwhite (in AI profile, recessed)
- SS-G01**
GUARD 01_BUNKBED 2-A
AA-H01 - Hooks - stainless steel powder-coated (art.2326 PB12)- RAL 3020 Red & RAL 4010 Rose (RAL colour to be confirmed by Clink)
- FF-C01**
CURTAINS 01_BUNKBED 2-AB
FF-C01/C02/C03 Privacy curtain - Washable Fabric -colour: dark grey/ anthracite less fold -Almost 1:1 fold factor to open horizontally- fire-retardant fabric - Matt Finish - CURTAINS-LUNA BLACKOUT-by SKOPOS-TEX L15 GUNMETAL-(RAL colour tbc by Clink)

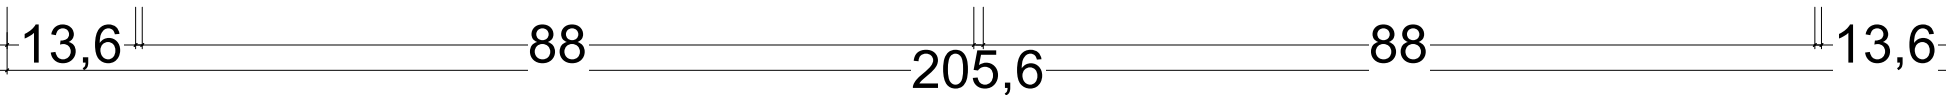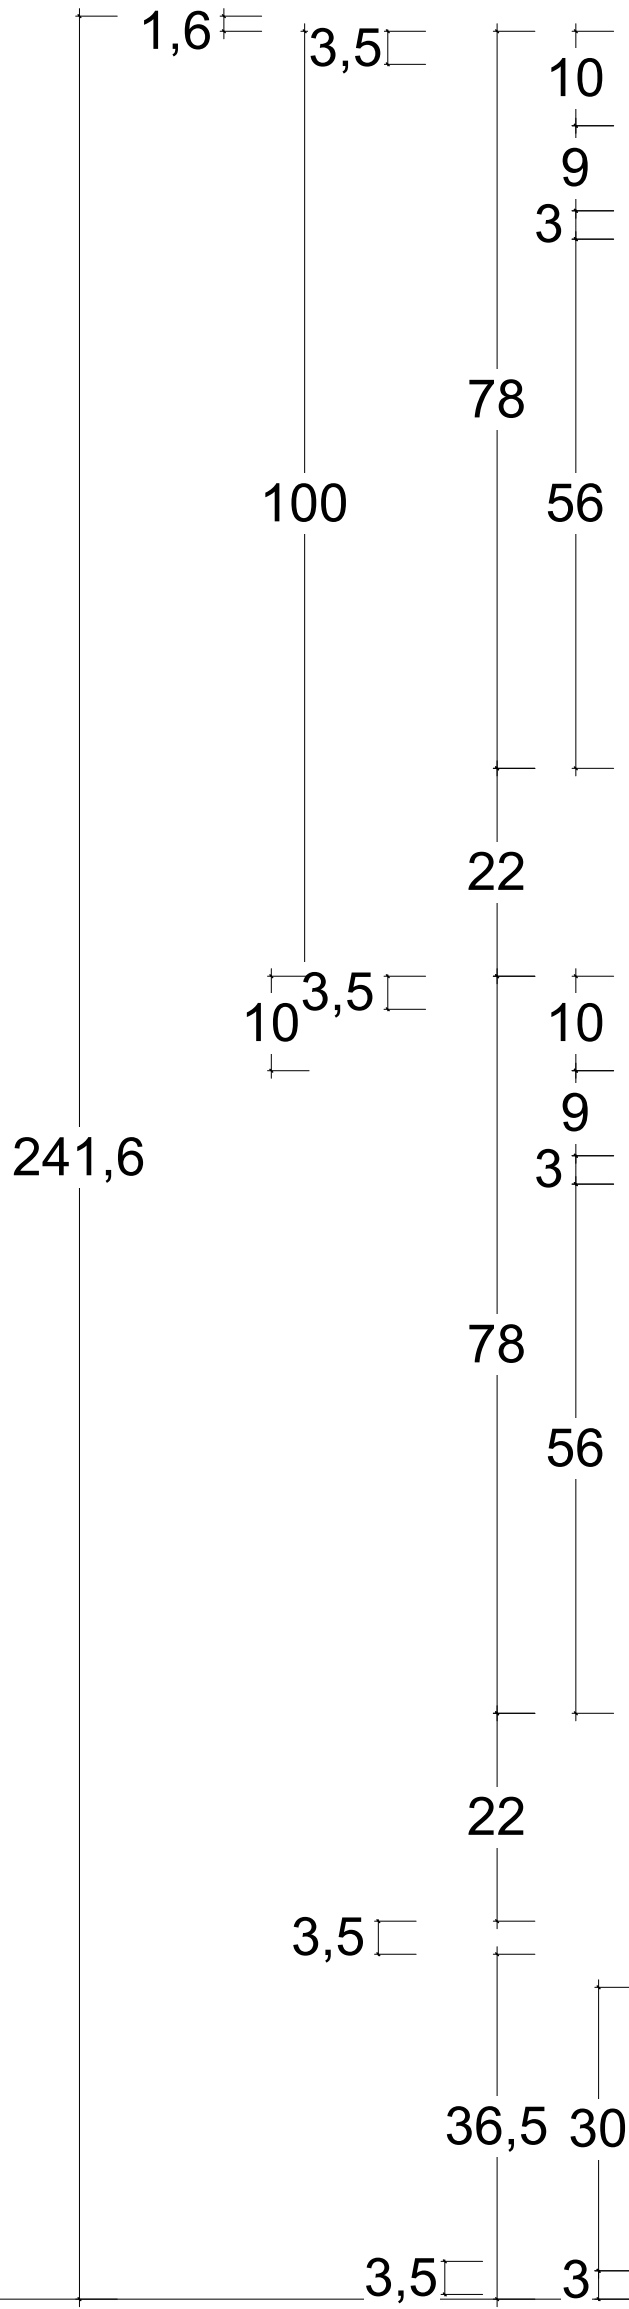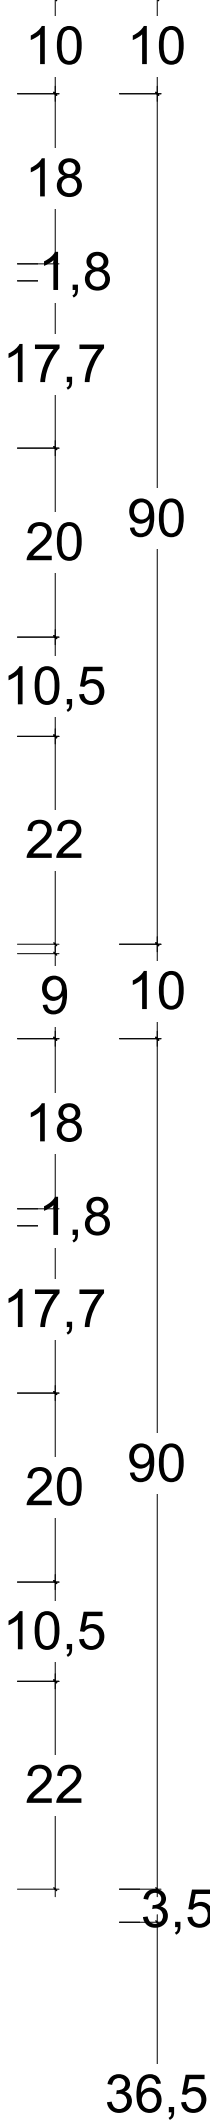

BUNKBEDS - TYPE 2-A - SECTION 2

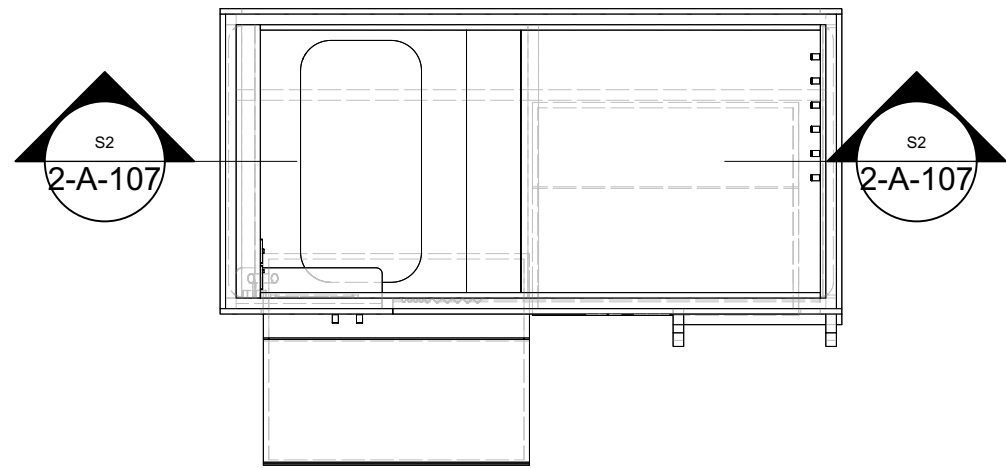

KEY

Index

A) 04.05.2026 Plan Set UP

All measurements have to be verified according to existing conditions by the contractor! Discrepancies must be reported immediately to the responsible project manager. The contractor has to produce fully dimensioned shop drawings prior to the start of the contract and they have to be approved by the client/ investor / interior designer

Project
CLINK 78 - BEDS



Project Address
CLINK 78
78 King's Cross Rd
London WC1X 9QG
United Kingdom

Client's Address
CLINK 78
78 King's Cross Rd
London WC1X 9QG
United Kingdom


Sheet Number 2-A-107 Total Sheets 82

Sheet Title BUNKBED 2-A SECTION 2 Level

File Name 260425_CLINK 78_BEDs AA DRAFT 03.vwx

Date	Sheet Size	Scale	Signed
28.04.26	A1	1:8	AA

Stefanie Jaensch INTERIOR DESIGNS
Global Headquarter | Stefanie Jaensch c/o WeWork
Taubusanlage 8 | 60329 Frankfurt a.M.
E-Mail info@stefaniejaensch.de | DE +49 (0) 174 6756098
www.stefaniejaensch.de
Legal address | Stefanie Jaensch | Offenbacher Landstraße 434 | 60599 Frankfurt a.M.
© 2023 All Rights Reserved | Stefanie Jaensch

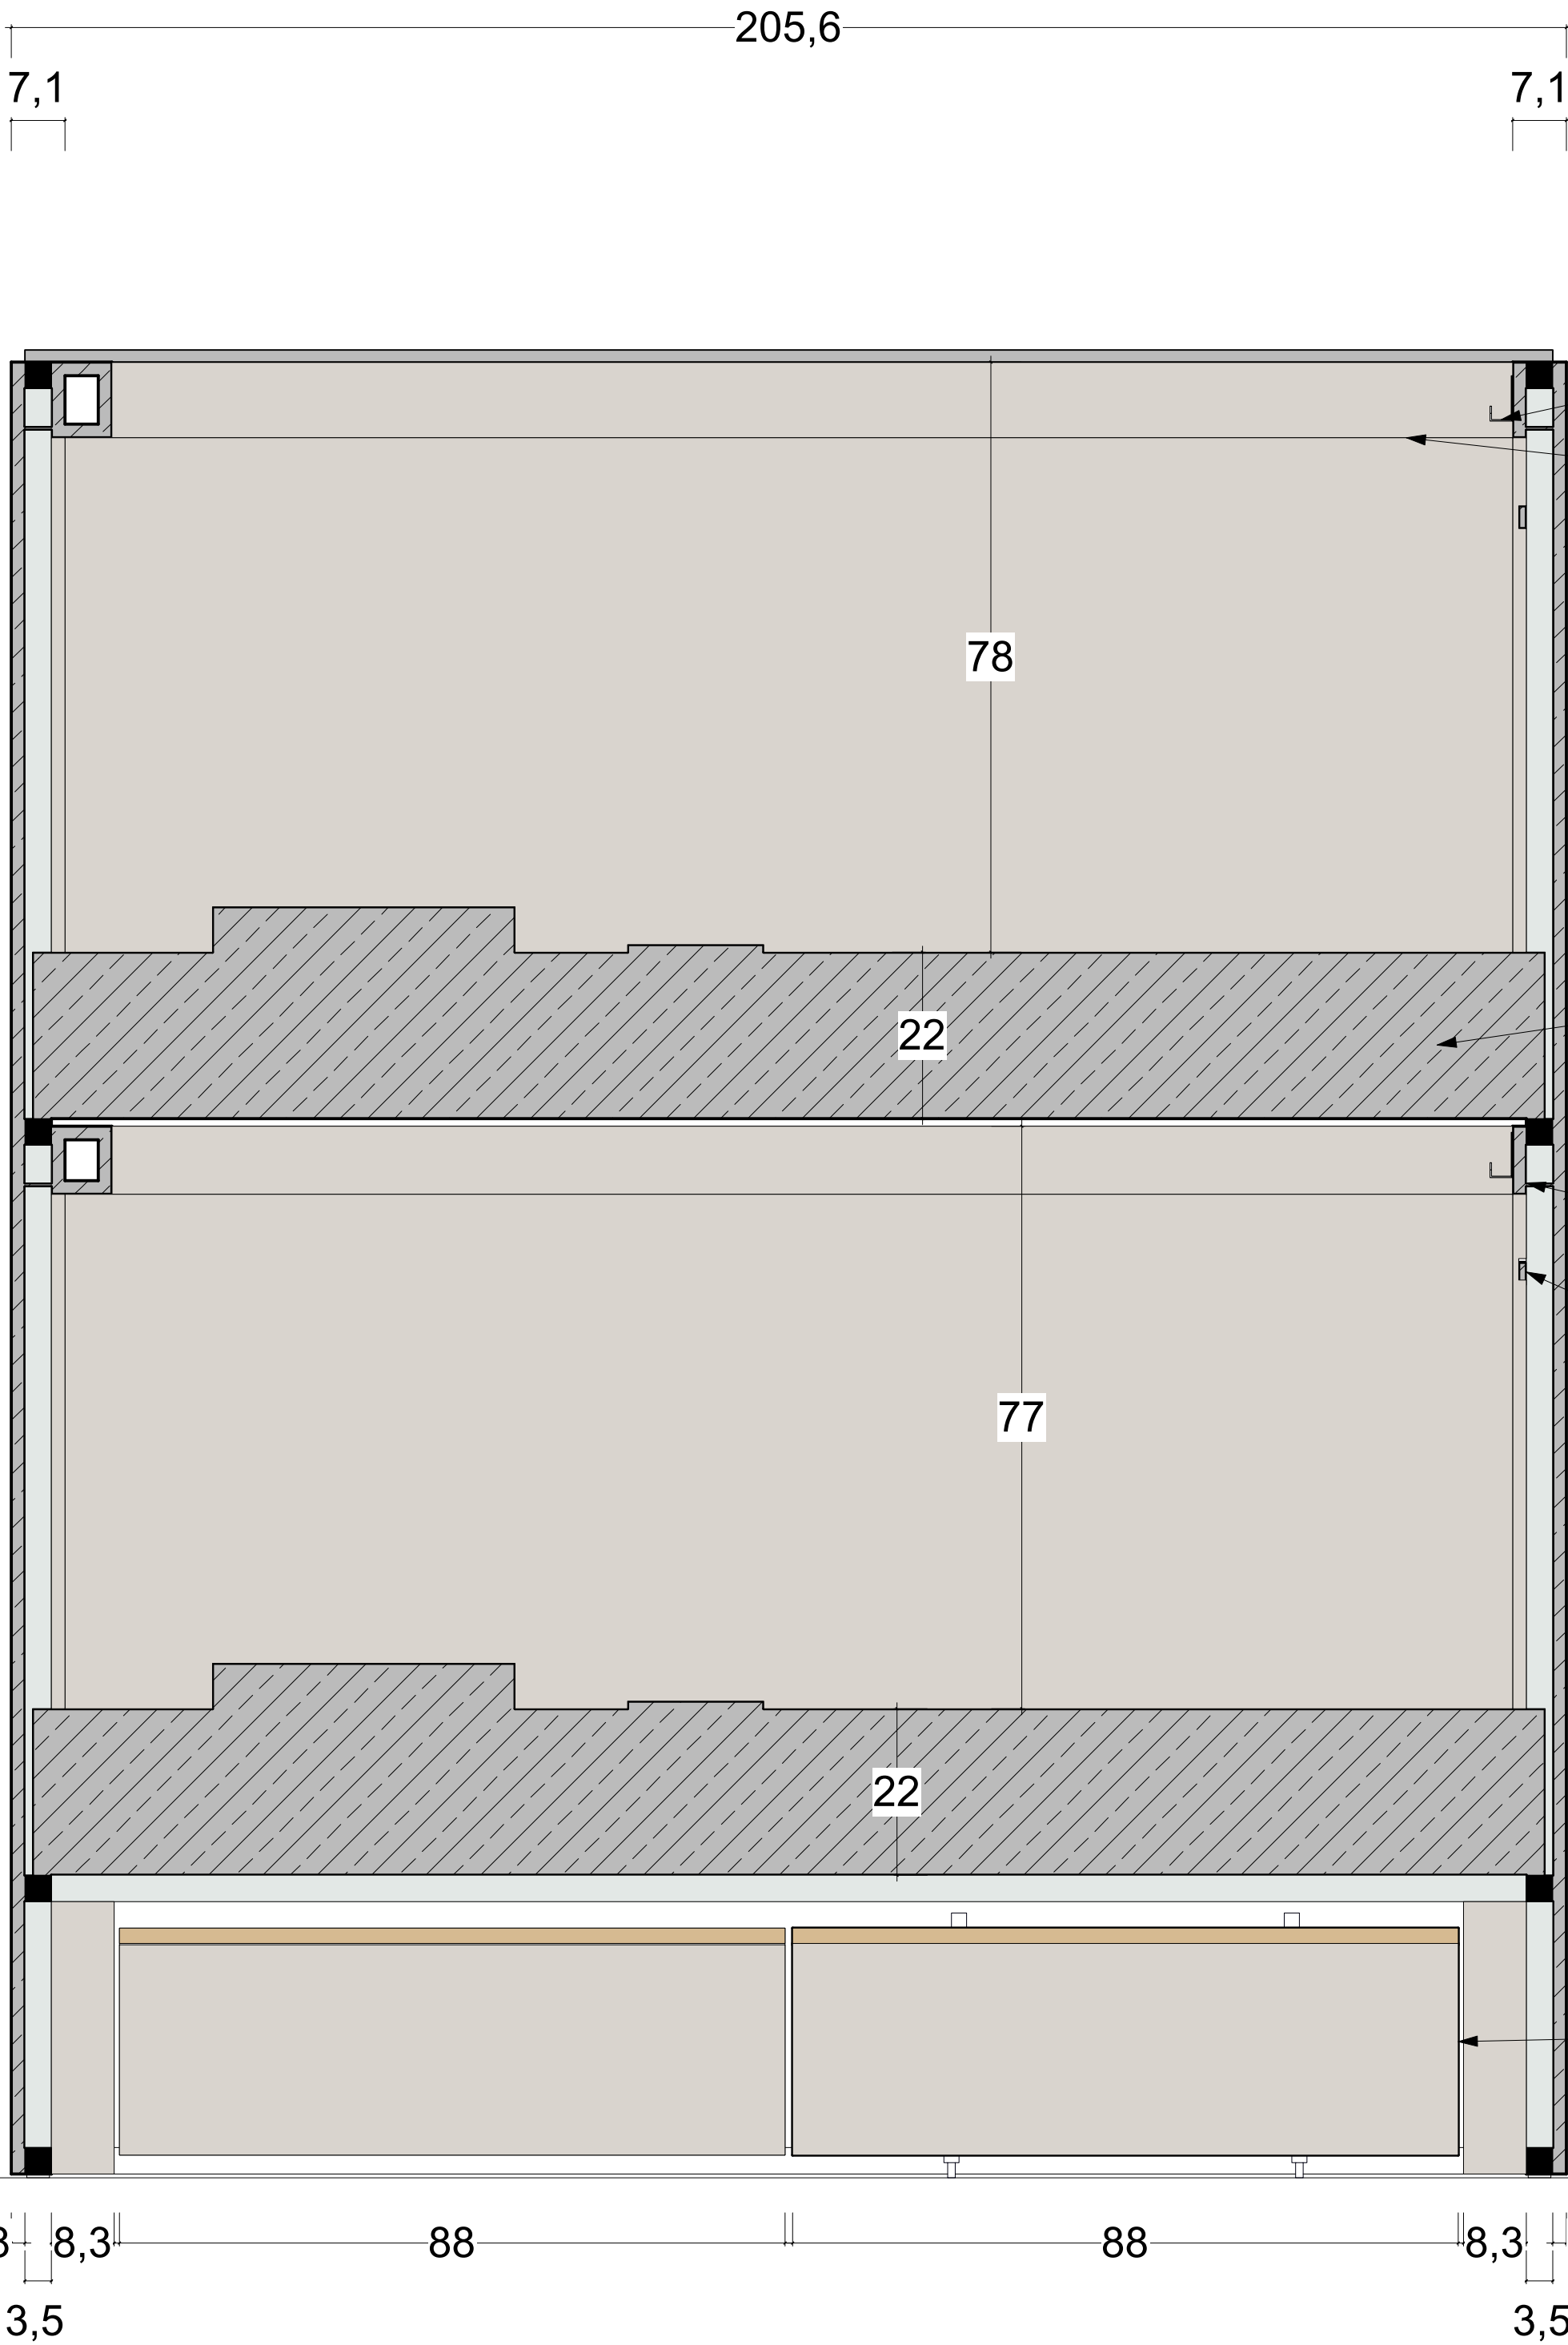

AA-H01
HOOKS 02-BUNKBED 2-ABC
AA-H01 - Hooks - stainless steel powder-coated (art.2326 PB12)- RAL 3020 Red & RAL 4010 Rose (RAL colour to be confirmed by Clink)

CC-M01
CLADDING 019_BUNKBED 2-A
CC-M01/M02/M03/M04/M05/M06 Cladding - Laminated chipboard to match RAL 7044, Thickness 18m (RAL colour to be confirmed by Clink)

FF-M01
MATTRESS 02_BUNKBED 2-ABC
FF-M01 Mattress - 90x200x22cm - (Foam mattress - Fire retardant fabric and foam (Crib 5) - 100gr/m2 polyester - Reinforcement - Cover should be washable on 40 degrees) - Final height TBC (18/20/22 cm)



EE-L01
LED LIGHT 001_BUNKBED 2A
EE-L01/L02/L03/L04/L05/L06 LED light with light diffuser - LED stripes - 2000 Calvin - Warmwhite (in Al profile, recessed)

AA-R01
RACK 01_BUNKBED 2-ABC
AA-R01 TOWEL RACK - stainless steel - powder coated - The same colour as the metal frame, polished edges for safety reasons, to fit into the metal frame size - according to the drawing (RAL colour to be confirmed by Clink)

CC-L01
CLADDING 001_LOCKER 2-A
CC-L01 LOCKER - Panels - Laminated chipboard to match RAL 7044, Thickness 18m (RAL colour to be confirmed by Clink)

S2 BUNKBED 2-A SECTION 2
Scale: 1:8

BUNKBEDS - TYPE 2-A - SECTION 3

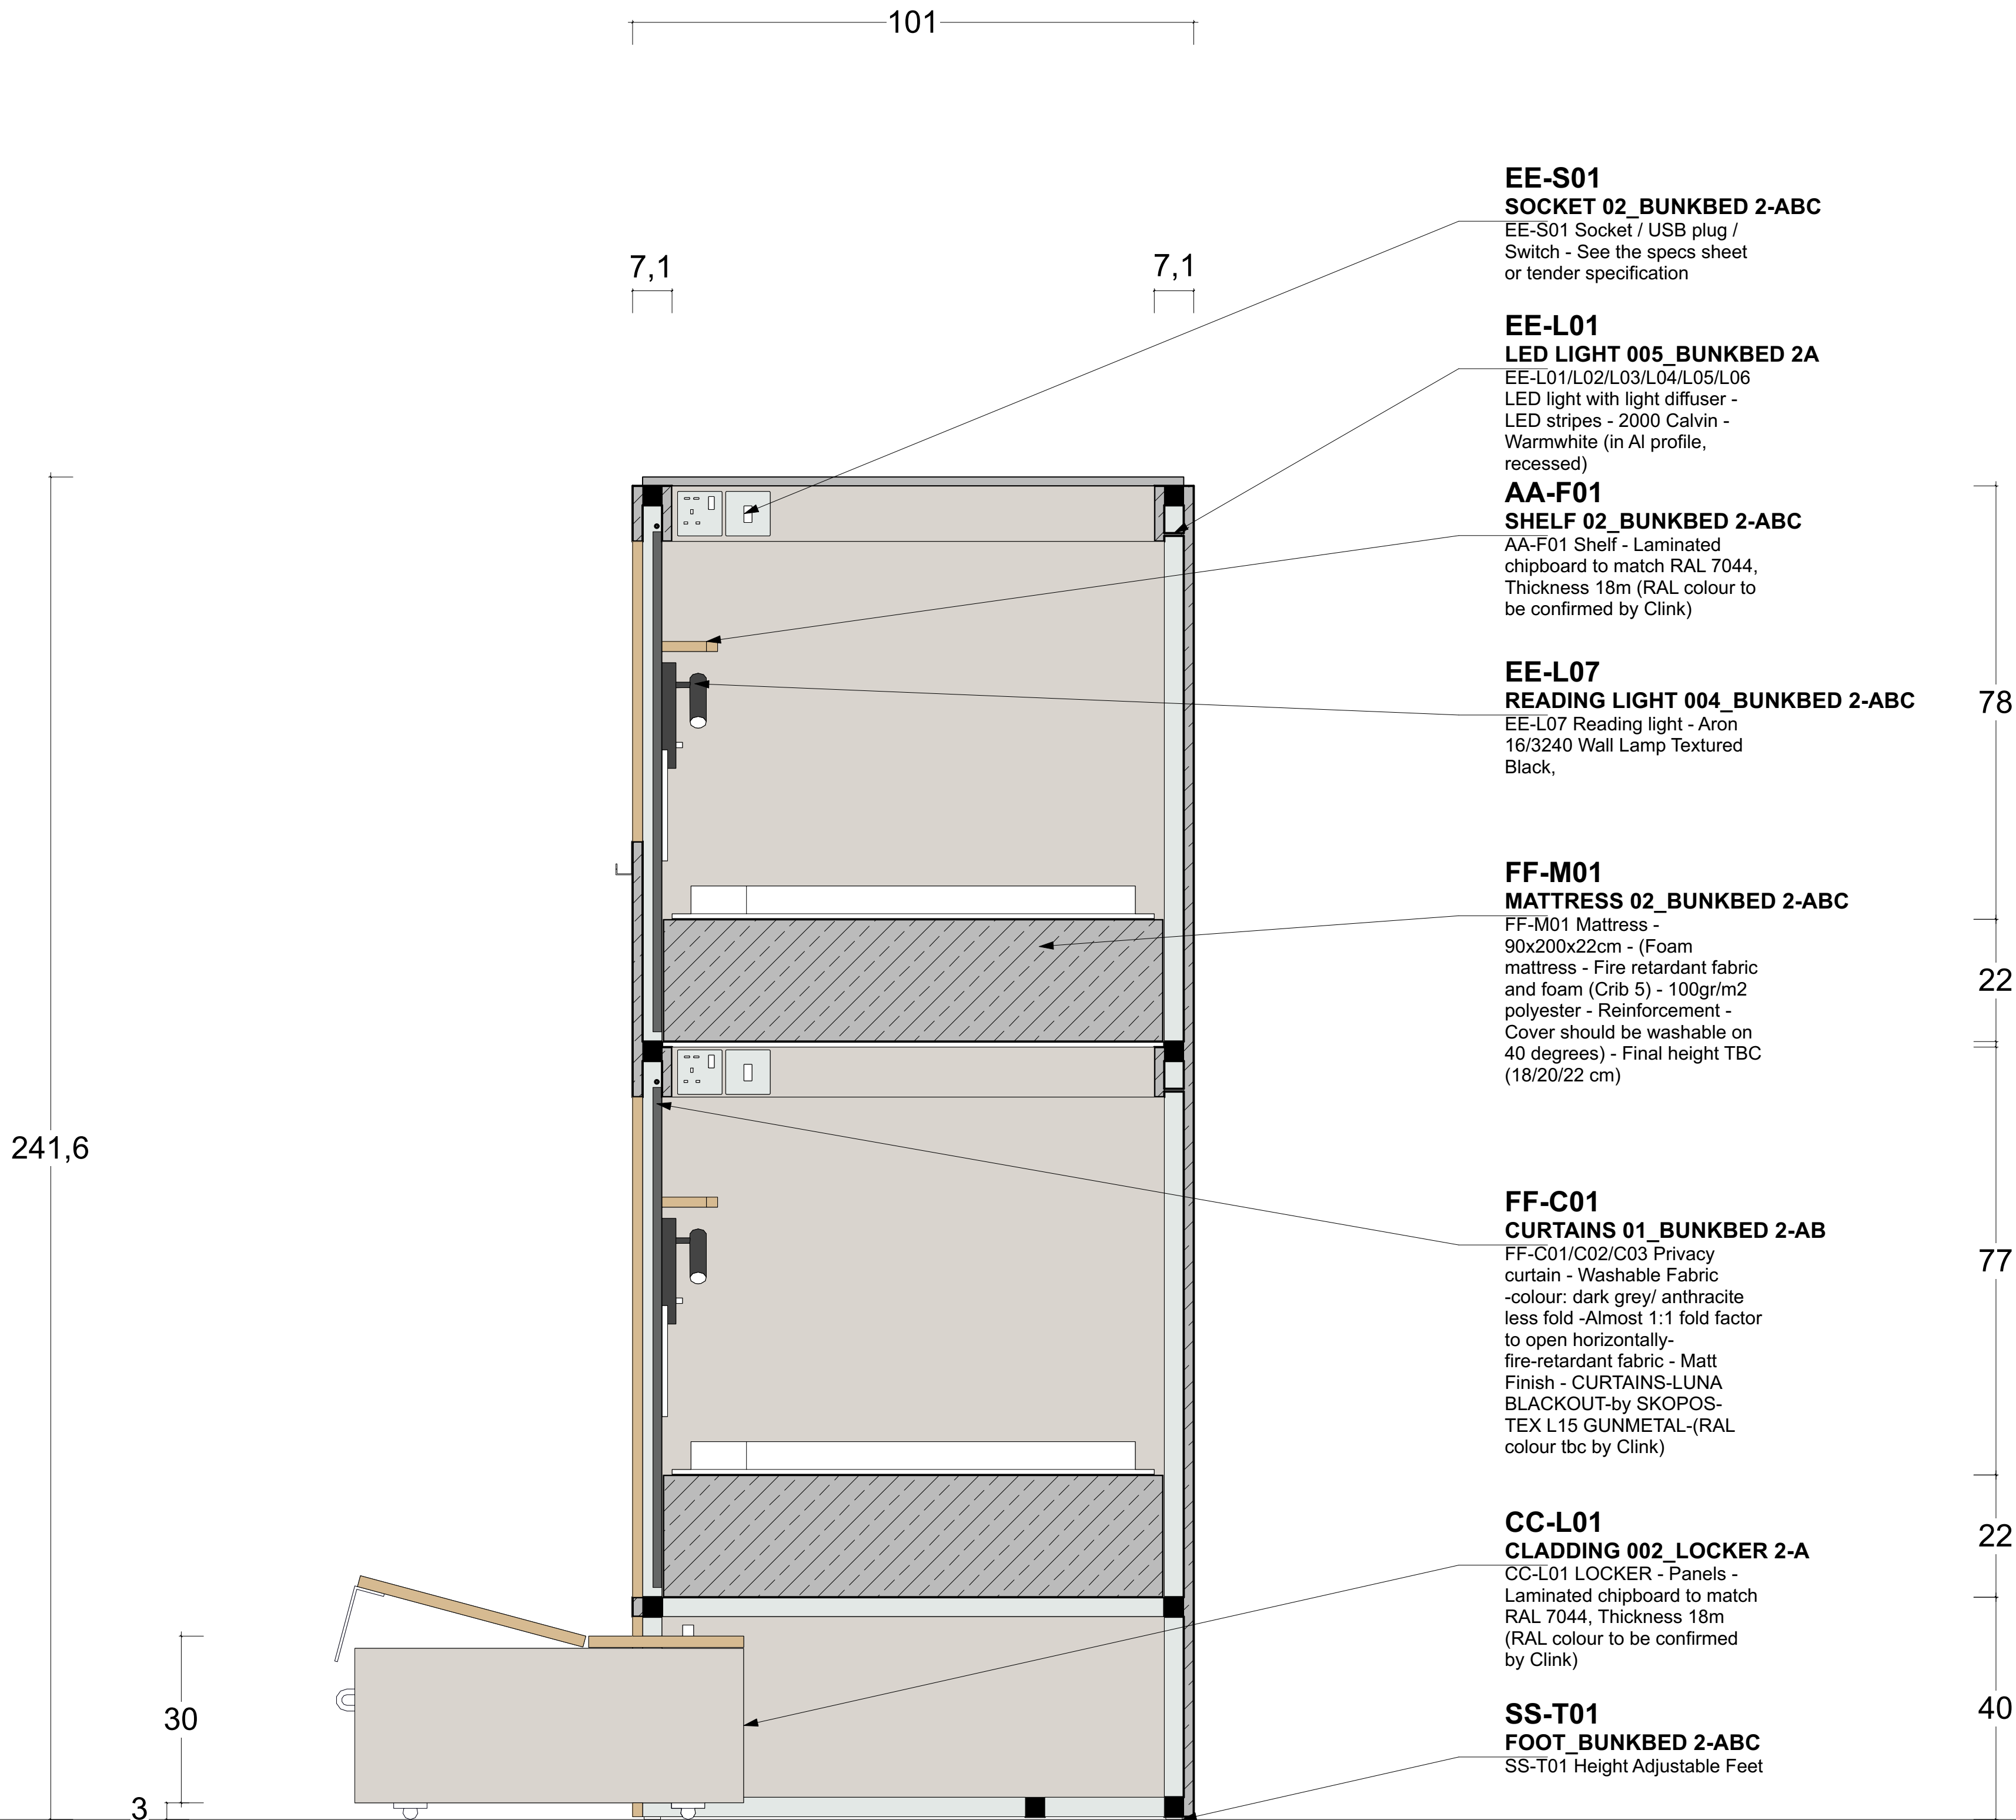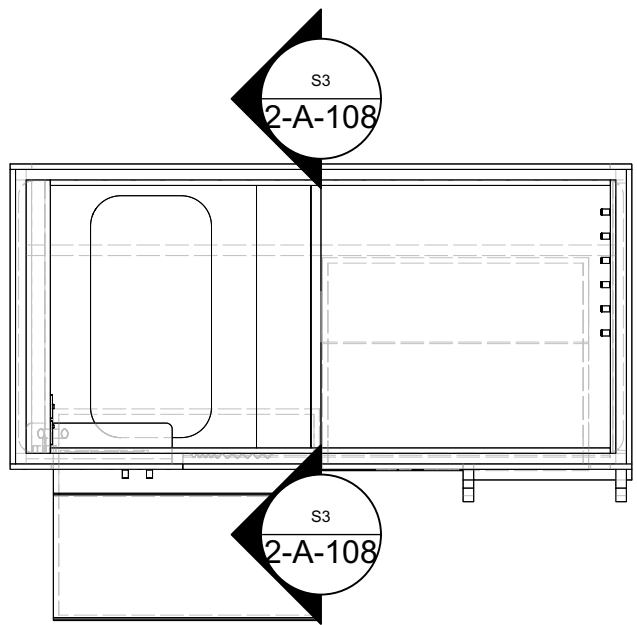

KEY

Index

A) 04.05.2026 Plan Set UP

All measurements have to be verified according to existing conditions by the contractor! Discrepancies must be reported immediately to the responsible project manager. The contractor has to produce fully dimensioned shop drawings prior to the start of the contract and they have to be approved by the client/ investor / interior designer

Project

CLINK 78 - BEDS

Logo



Project Address

CLINK 78
78 King's Cross Rd
London WC1X 9QG
United Kingdom

Client's Address

CLINK 78
78 King's Cross Rd
London WC1X 9QG
United Kingdom

Sheet Number 2-A-108		Total Sheets 82
Sheet Title BUNKBED 2-A SECTION 3		Level
File Name 260425_CLINK 78_BEDs AA DRAFT 03.vwx		




Date	Sheet Size	Scale	Signed
28.04.26	A1	1:8	AA

Stefanie Jaensch INTERIOR DESIGNS

Global Headquarter | Stefanie Jaensch c/o WeWork
Taubusanlage 8 | 60329 Frankfurt a.M.
E-Mail info@stefaniejaensch.de | DE +49 (0) 174 6756098
www.stefaniejaensch.de

Legal address | Stefanie Jaensch | Offenbacher Landstraße 434 | 60599 Frankfurt a.M.
© 2023 All Rights Reserved | Stefanie Jaensch

BUNKBEDS - TYPE 2-A - SECTION 4

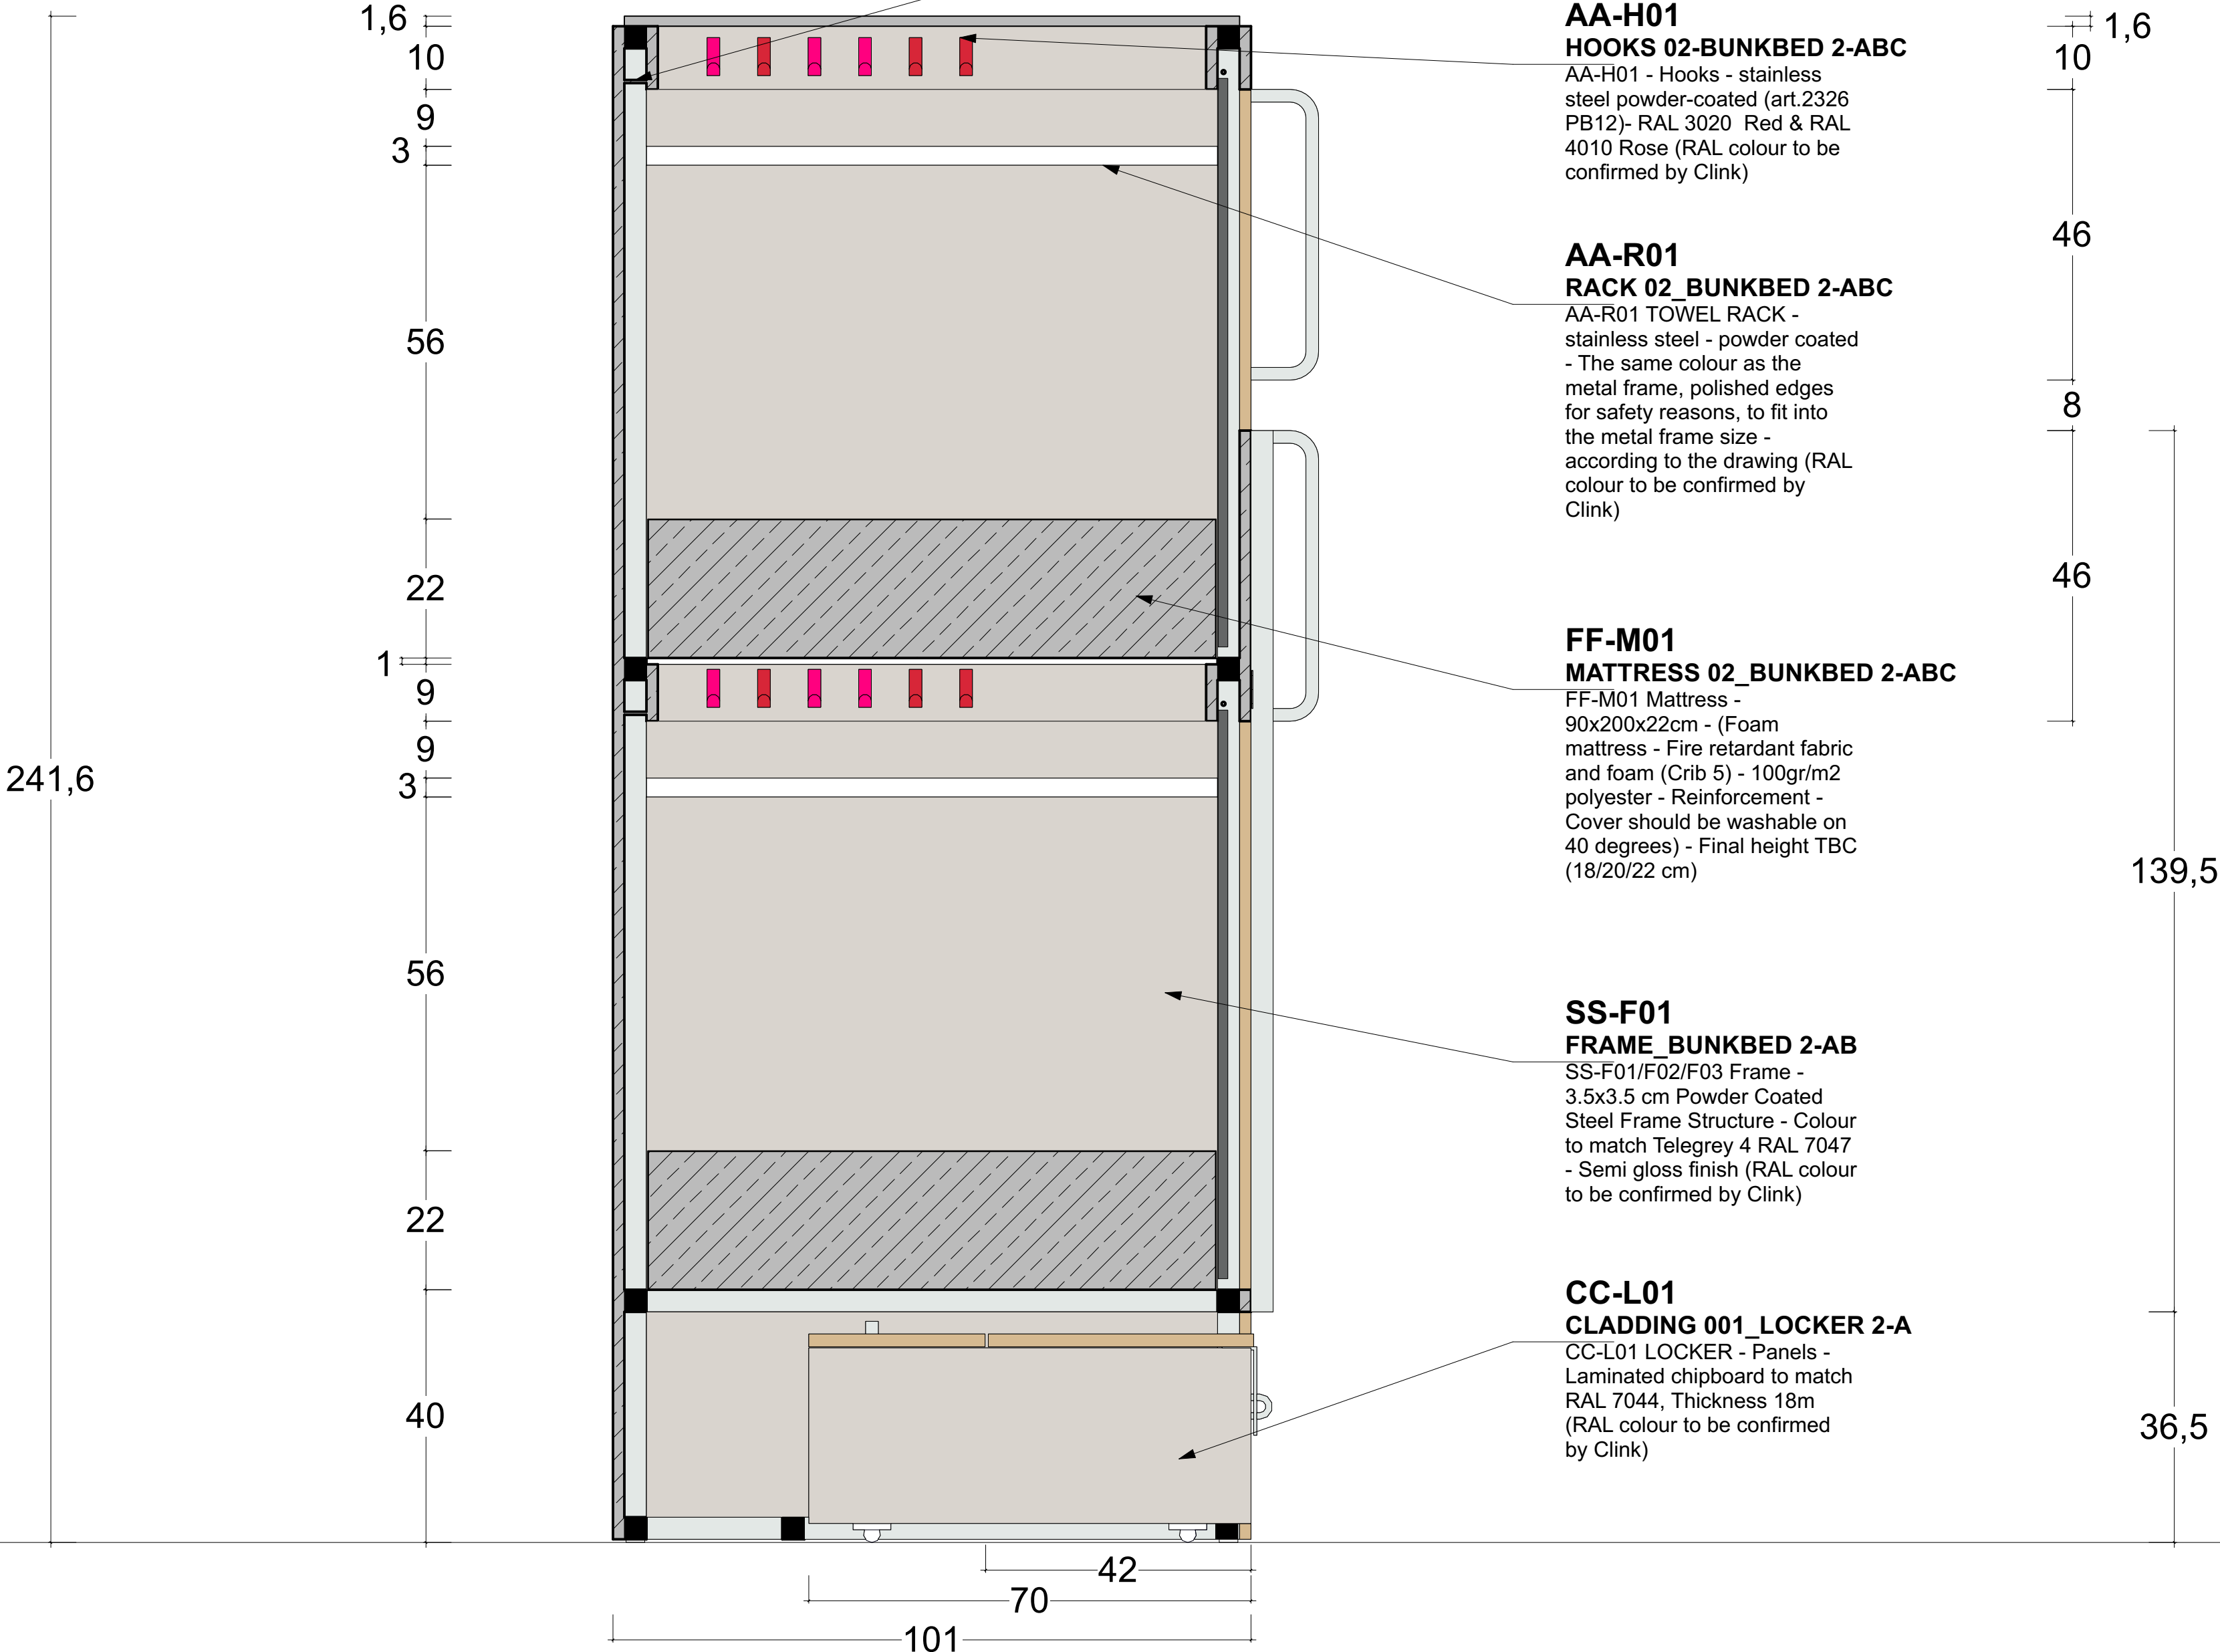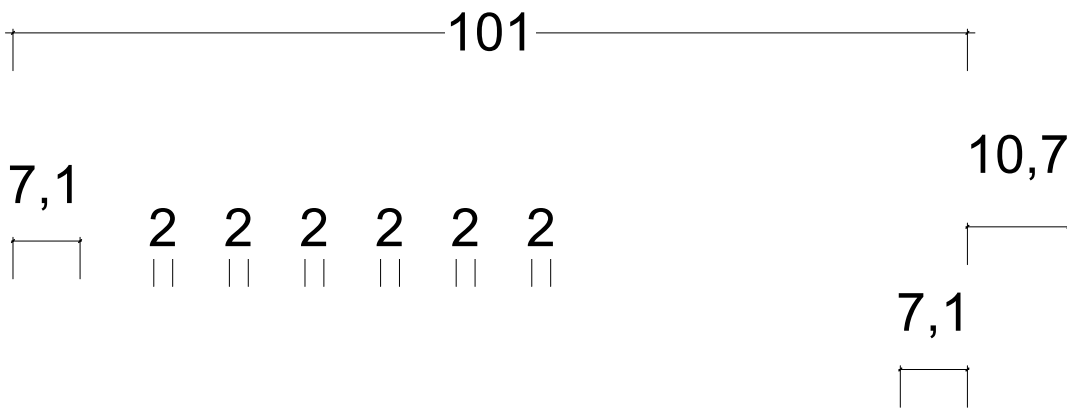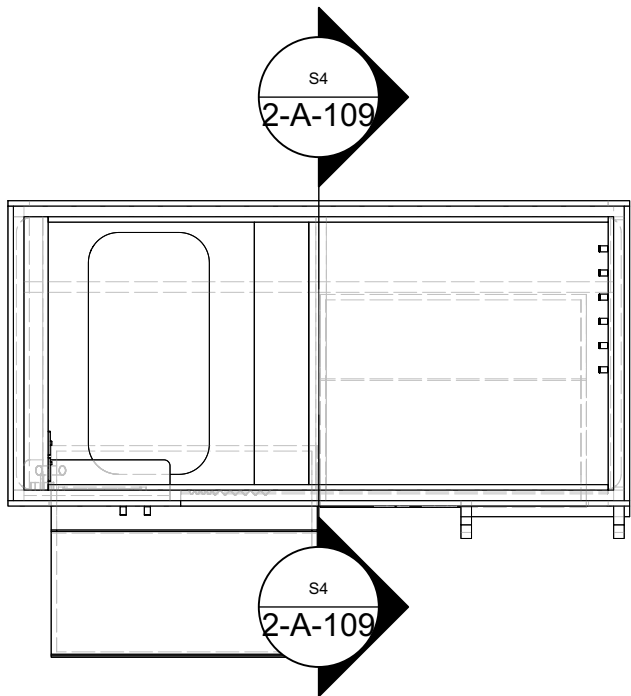

EE-L01
LED LIGHT 005_BUNKBED 2A
EE-L01/L02/L03/L04/L05/L06
LED light with light diffuser -
LED stripes - 2000 Calvin -
Warmwhite (in Al profile,
recessed)

AA-H01
HOOKS 02-BUNKBED 2-ABC
AA-H01 - Hooks - stainless
steel powder-coated (art.2326
PB12)- RAL 3020 Red & RAL
4010 Rose (RAL colour to be
confirmed by Clink)

AA-R01
RACK 02_BUNKBED 2-ABC
AA-R01 TOWEL RACK -
stainless steel - powder coated
- The same colour as the
metal frame, polished edges
for safety reasons, to fit into
the metal frame size -
according to the drawing (RAL
colour to be confirmed by
Clink)

FF-M01
MATTRESS 02_BUNKBED 2-ABC
FF-M01 Mattress -
90x200x22cm - (Foam
mattress - Fire retardant fabric
and foam (Crib 5) - 100gr/m2
polyester - Reinforcement -
Cover should be washable on
40 degrees) - Final height TBC
(18/20/22 cm)

SS-F01
FRAME_BUNKBED 2-AB
SS-F01/F02/F03 Frame -
3.5x3.5 cm Powder Coated
Steel Frame Structure - Colour
to match Telegrey 4 RAL 7047
- Semi gloss finish (RAL colour
to be confirmed by Clink)

CC-L01
CLADDING 001_LOCKER 2-A
CC-L01 LOCKER - Panels -
Laminated chipboard to match
RAL 7044, Thickness 18m
(RAL colour to be confirmed
by Clink)



KEY

Index

A) 04.05.2026 Plan Set UP

All measurements have to be verified according to existing conditions by the contractor! Discrepancies must be reported immediately to the responsible project manager. The contractor has to produce fully dimensioned shop drawings prior to the start of the contract and they have to be approved by the client/ investor / interior designer

Project
CLINK 78 - BEDS




Project Address
CLINK 78
78 King's Cross Rd
London WC1X 9QG
United Kingdom

Client's Address
CLINK 78
78 King's Cross Rd
London WC1X 9QG
United Kingdom

Sheet Number	2-A-109	Total Sheets	82
Sheet Title	BUNKBED 2-A SECTION 4	Level	
File Name			
260425_CLINK 78_BEDs AA DRAFT 03.vwx			
Date	Sheet Size	Scale	Signed
28.04.26	A1	1:8	AA


Stefanie Jaensch INTERIOR DESIGNS
Global Headquarter | Stefanie Jaensch c/o WeWork
Taubusanlage 8 | 60329 Frankfurt a.M.
E-Mail info@stefaniejaensch.de | DE +49 (0) 174 6756098
www.stefaniejaensch.de
Legal address | Stefanie Jaensch | Offenbacher Landstraße 434 | 60599 Frankfurt a.M.
© 2023 All Rights Reserved | Stefanie Jaensch

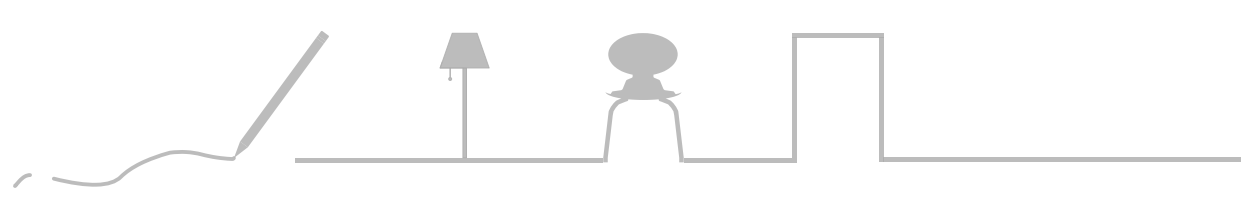

For



2-C1

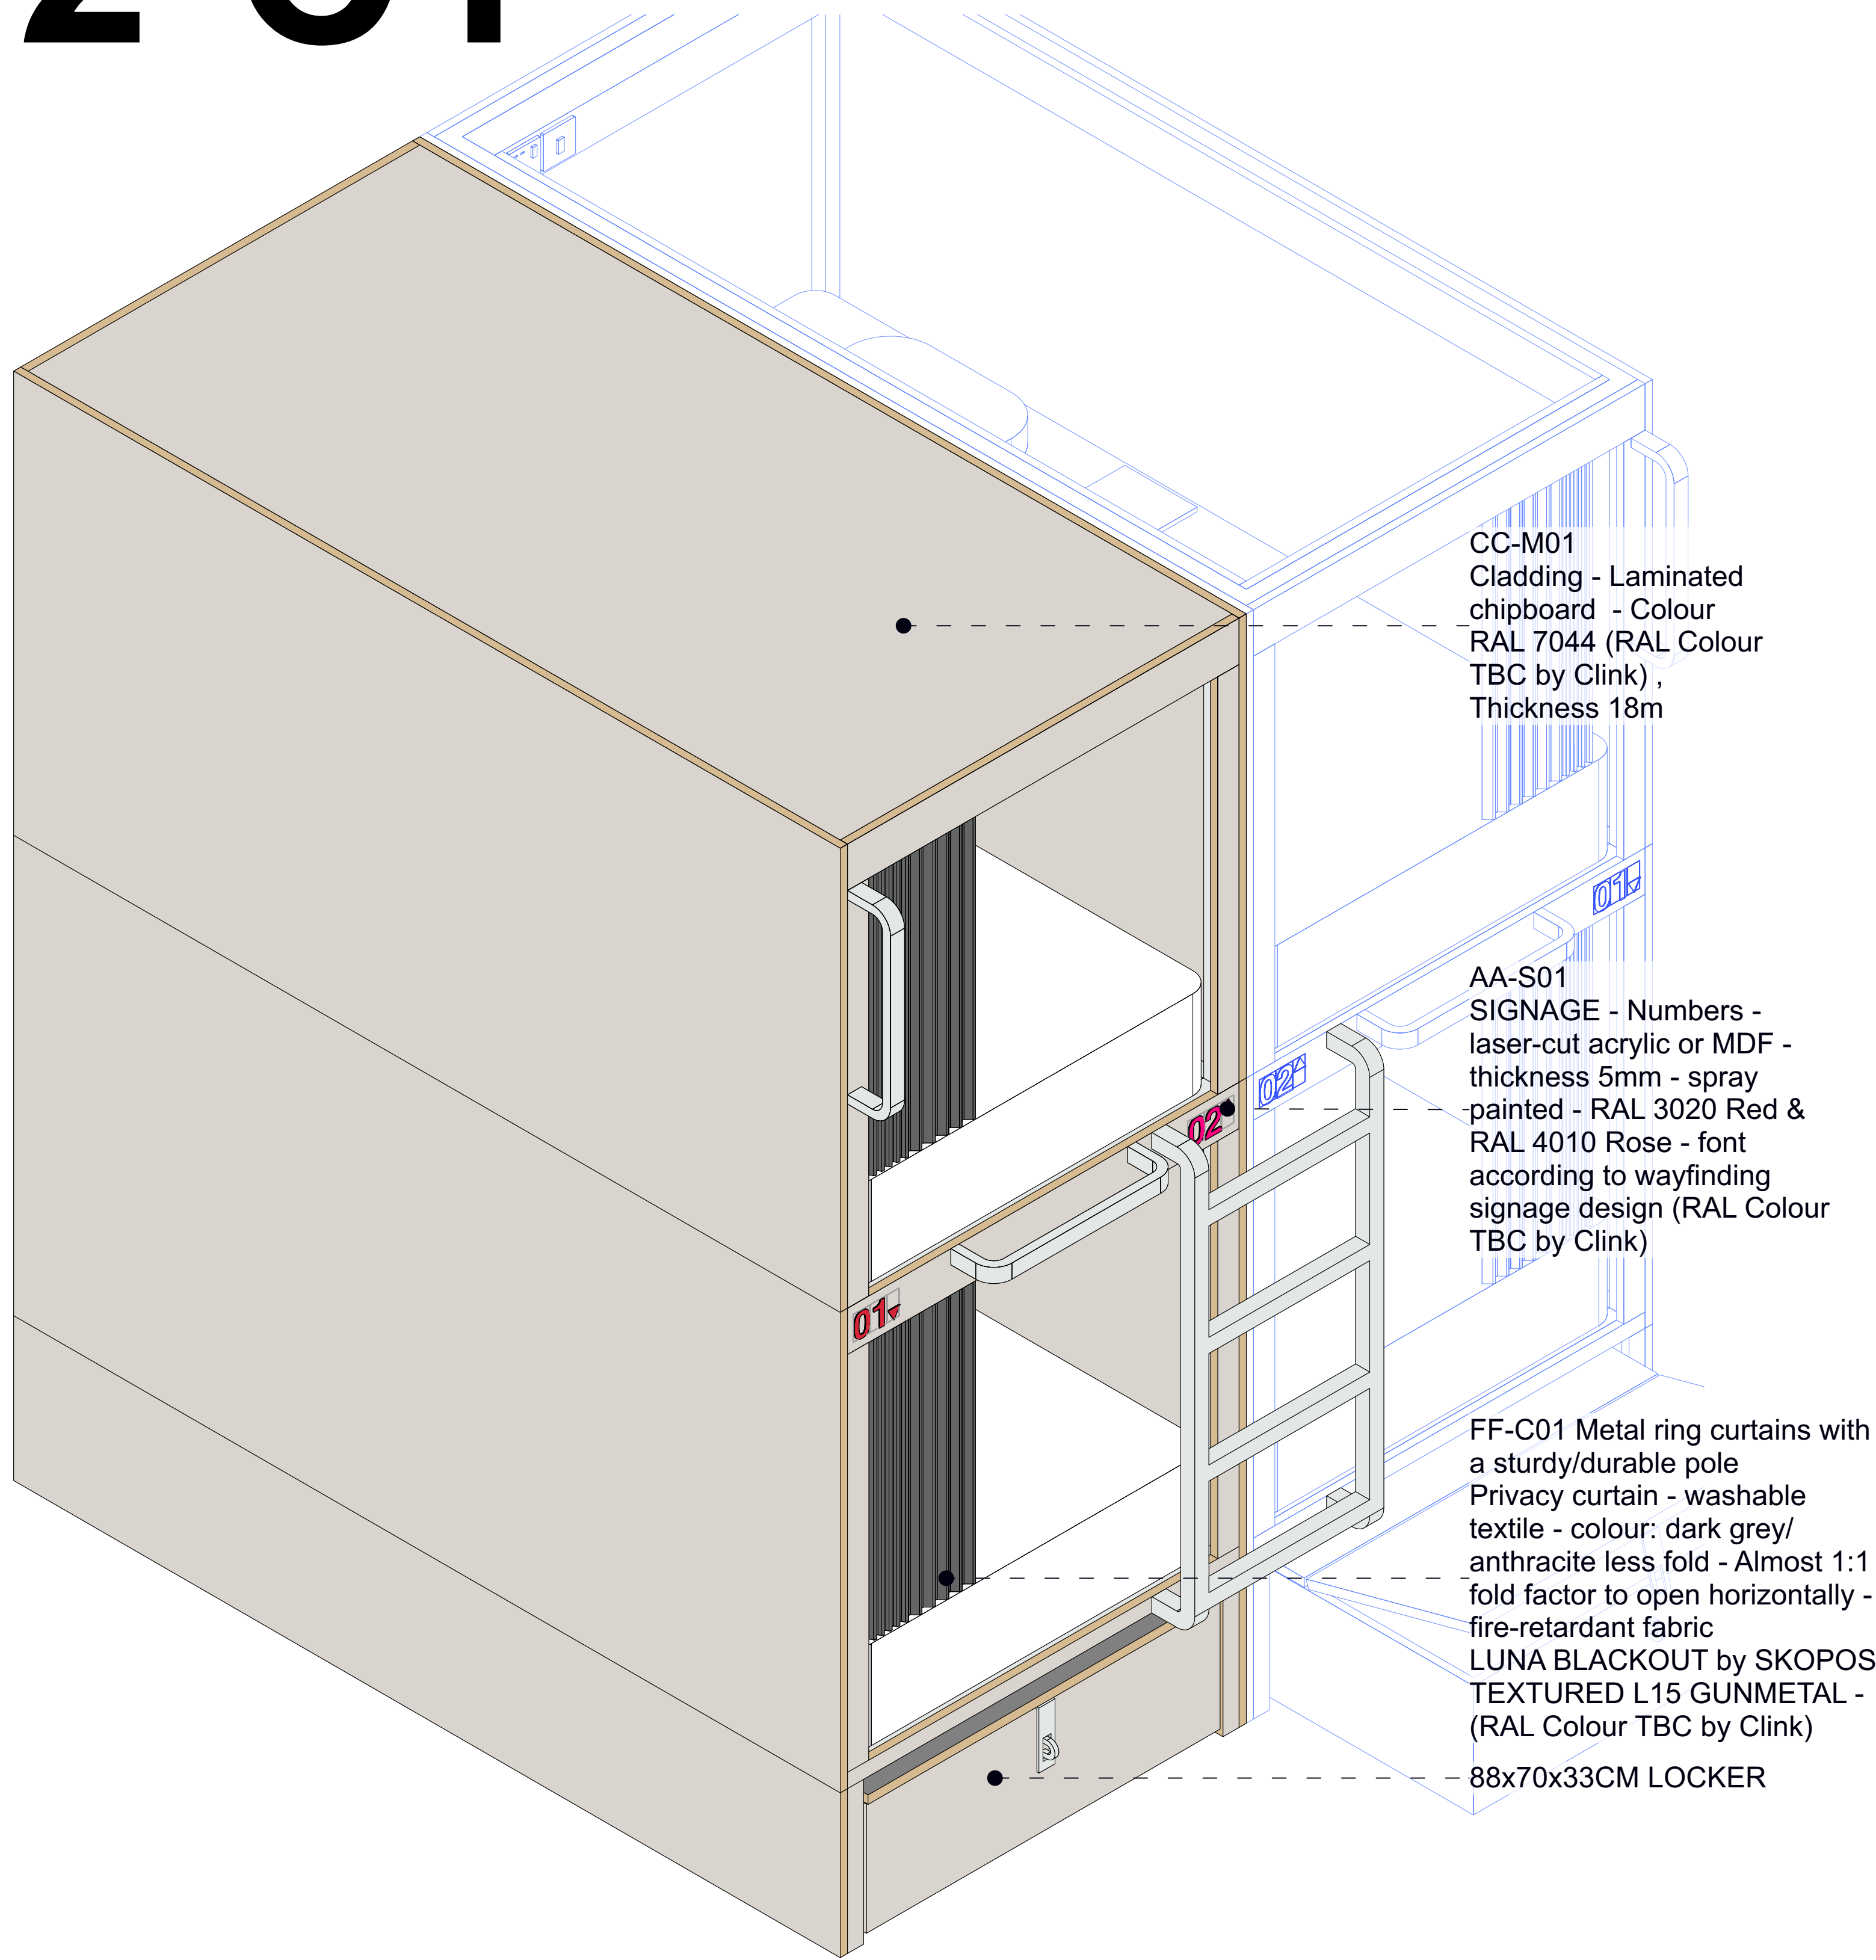


CC-M01
Cladding - Laminated
chipboard - Colour
RAL 7044 (RAL Colour
TBC by Clink) ,
Thickness 18m

AA-S01
SIGNAGE - Numbers -
laser-cut acrylic or MDF -
thickness 5mm - spray
painted - RAL 3020 Red &
RAL 4010 Rose - font
according to wayfinding
signage design (RAL Colour
TBC by Clink)

FF-C01 Metal ring curtains with
a sturdy/durable pole
Privacy curtain - washable
textile - colour: dark grey/
anthracite less fold - Almost 1:1
fold factor to open horizontally -
fire-retardant fabric
LUNA BLACKOUT by SKOPOS
TEXTURED L15 GUNMETAL -
(RAL Colour TBC by Clink)

88x70x33CM LOCKER

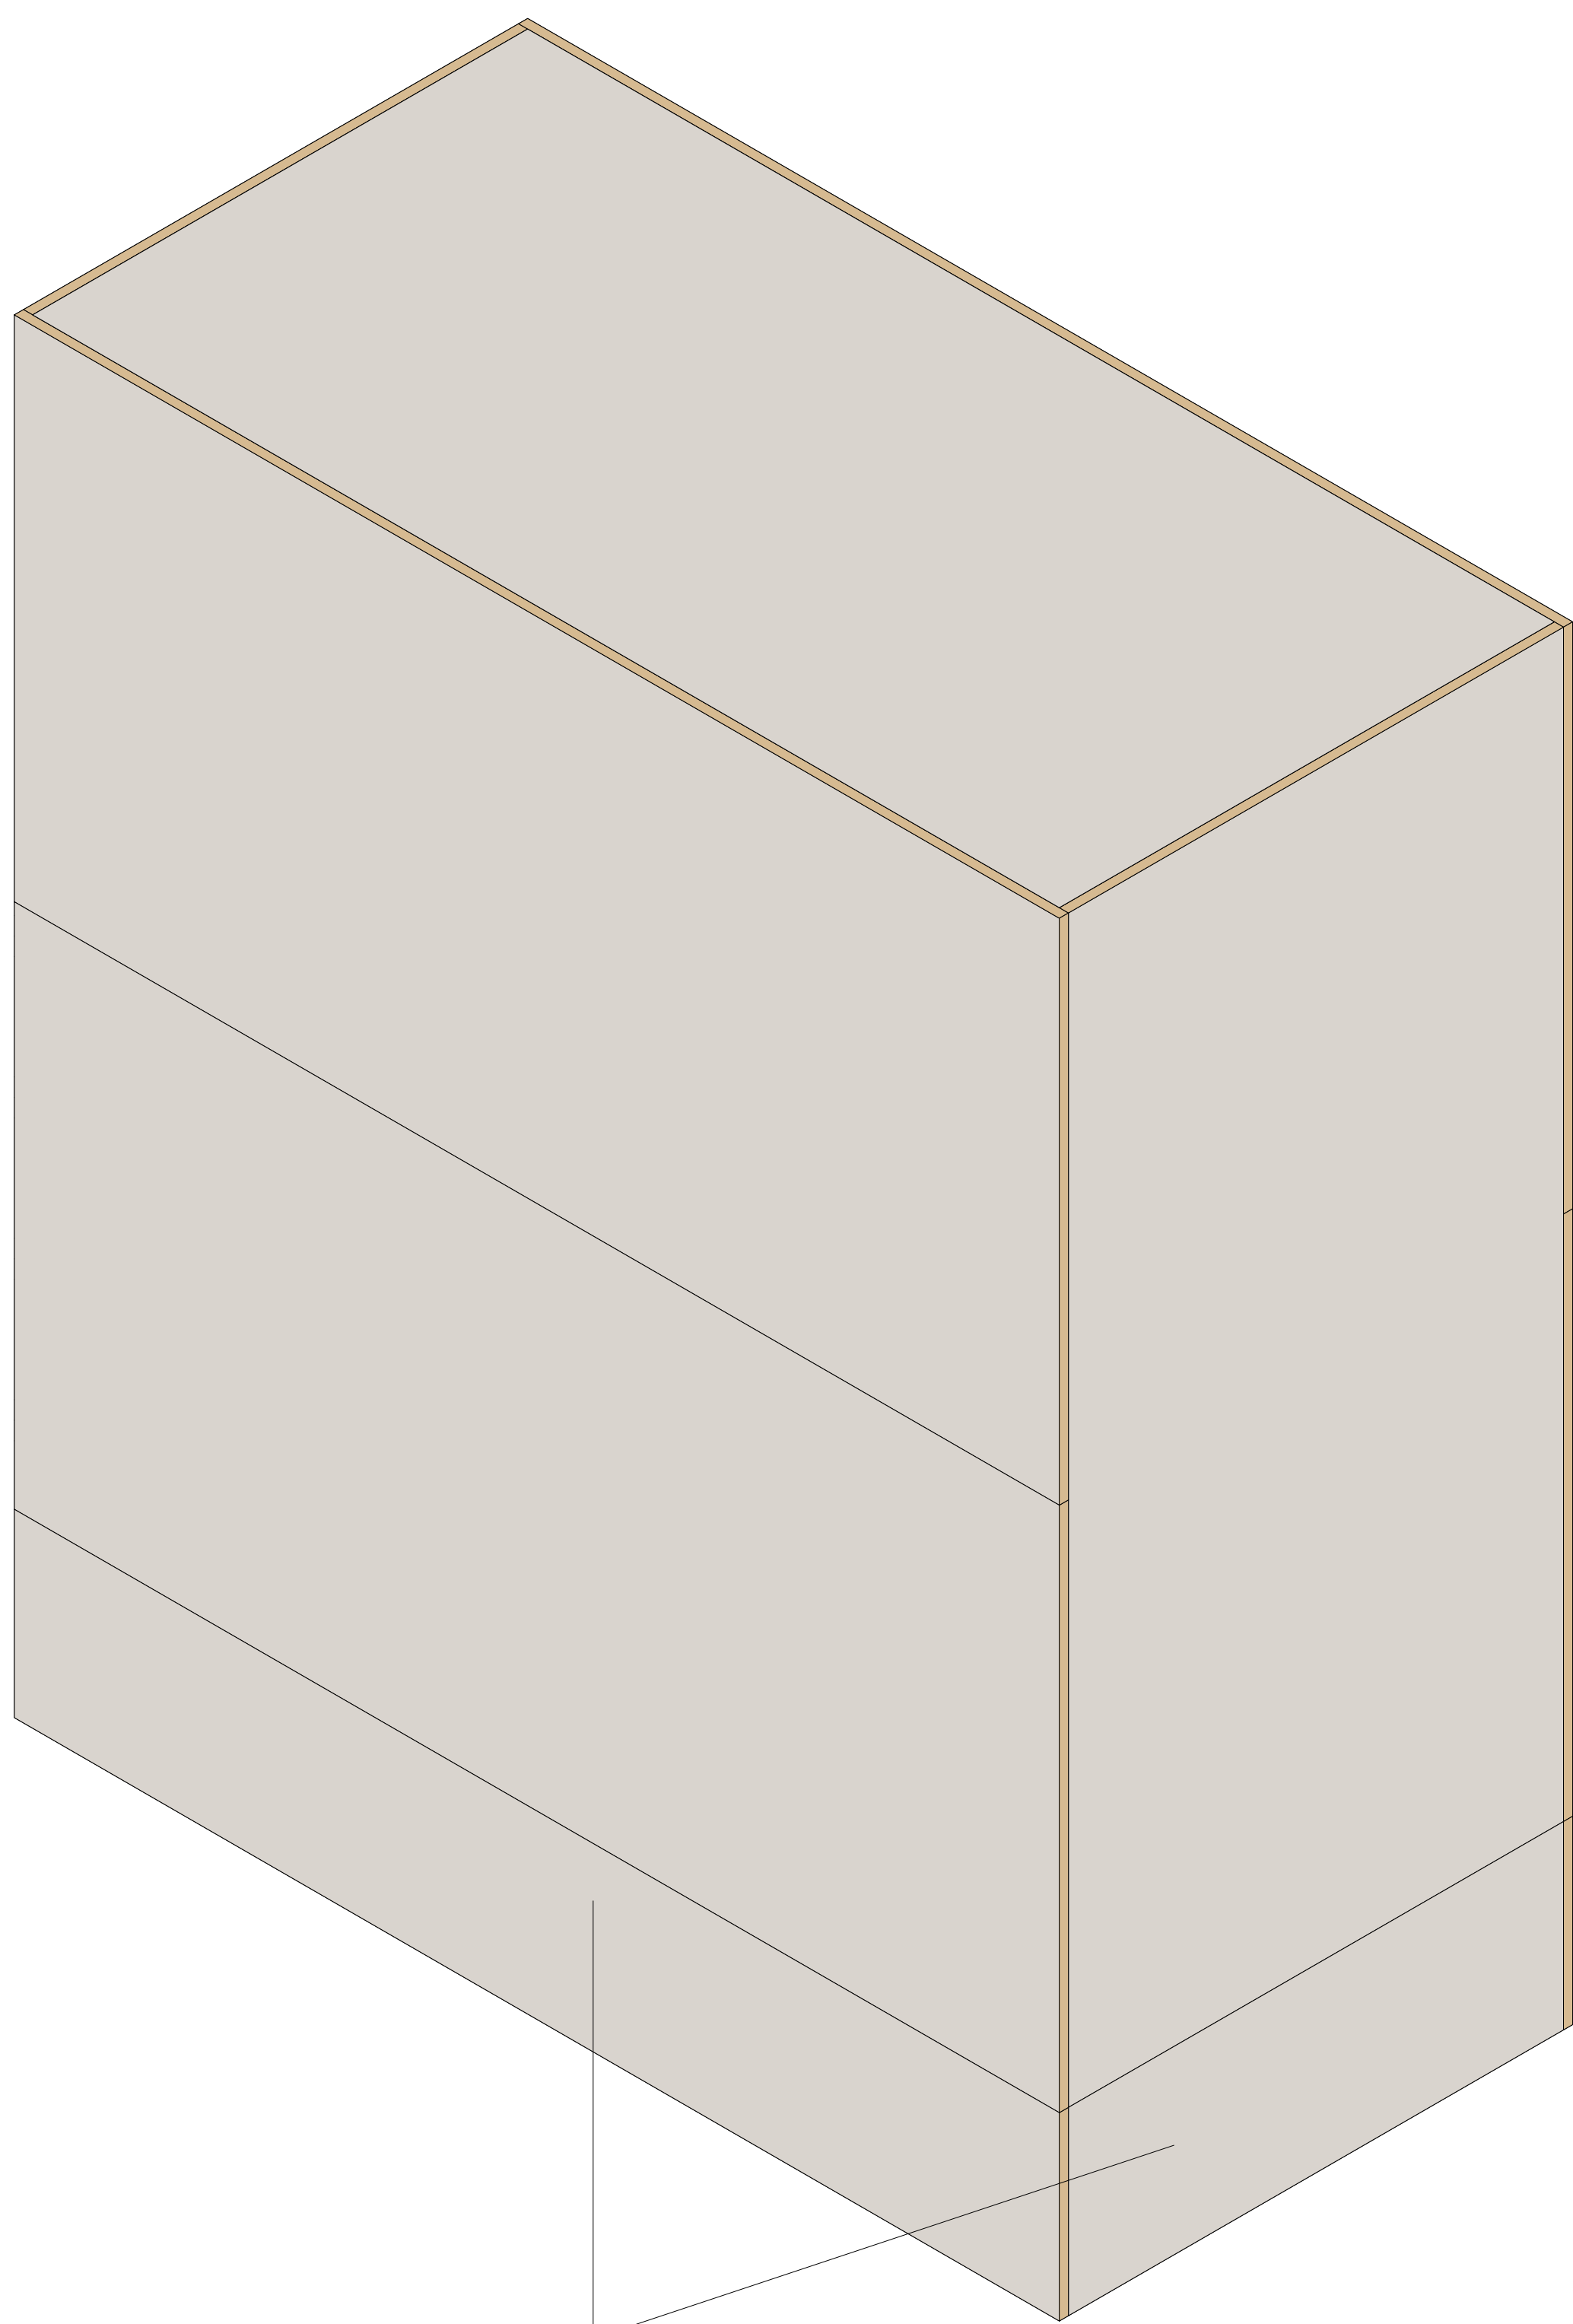


DRAFT

DIMENSIONS

101 x 205.6 x 241.6 (WxLxH)cm

Lower side panels may be removed to allow cable connections.

BUNKBEDS - TYPE 2-C1 - GA PLAN

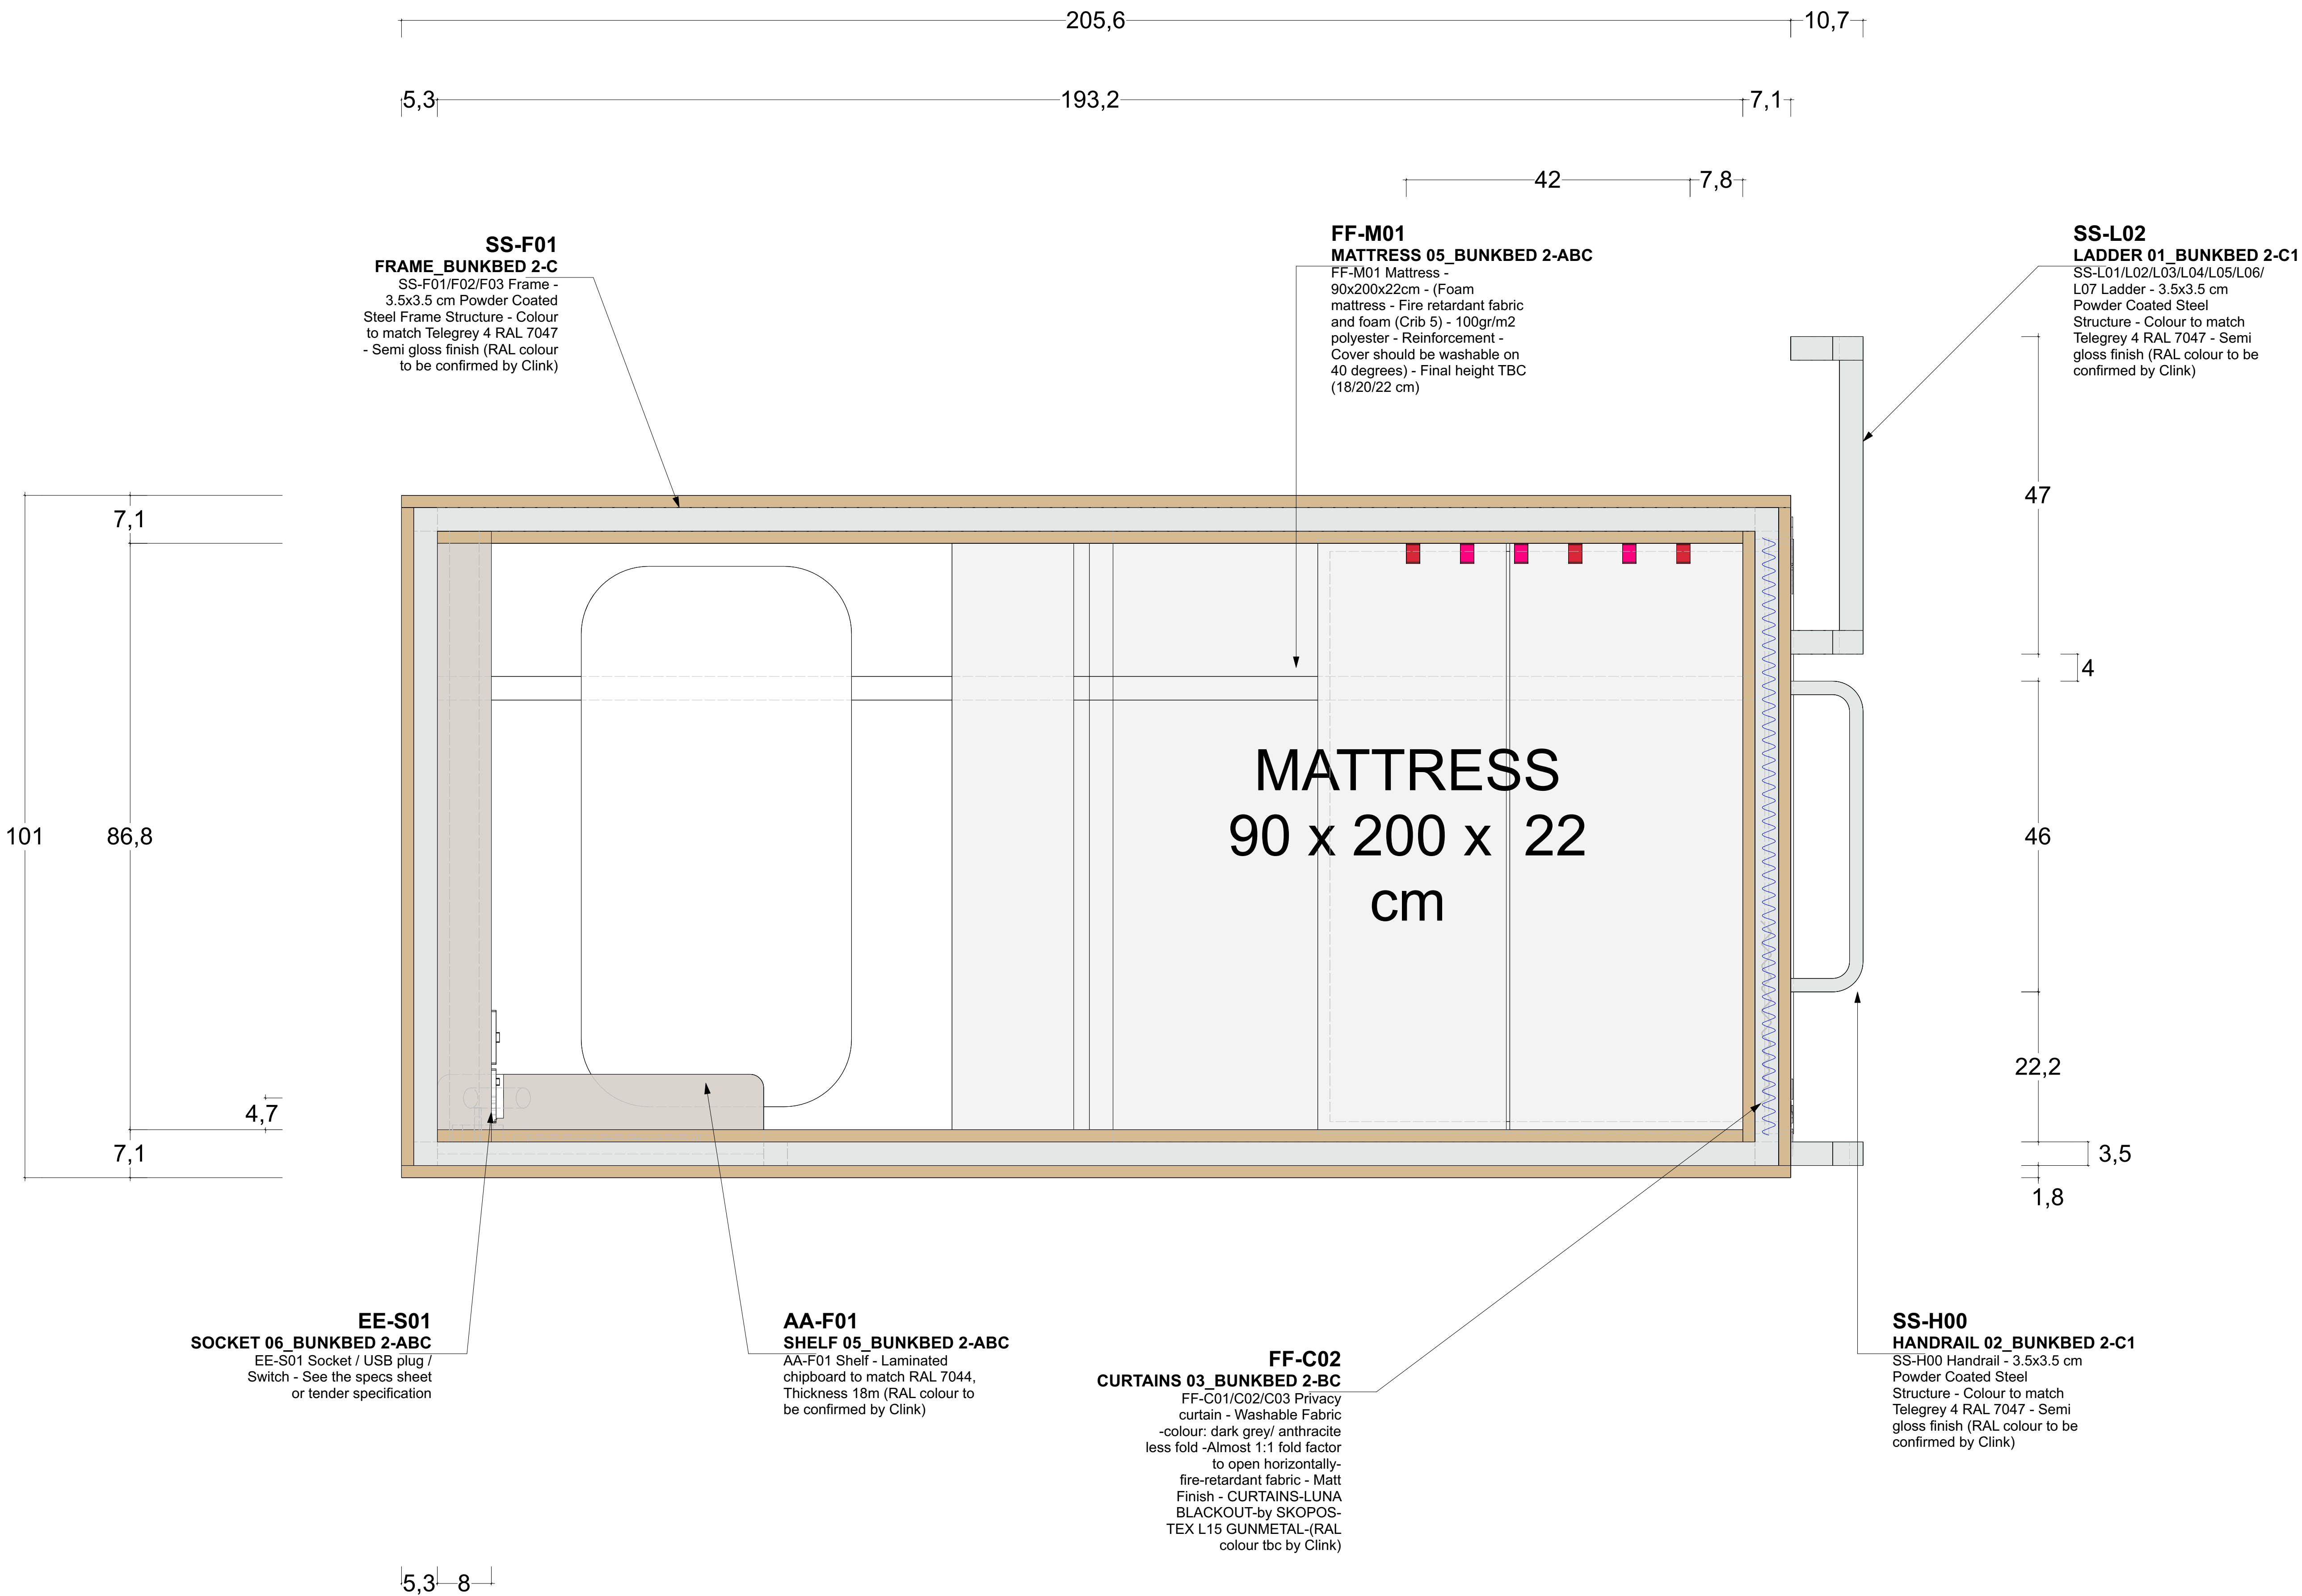

KEY

Index
A) 04.05.2026 Plan Set UP

All measurements have to be verified according to existing conditions by the contractor! Discrepancies must be reported immediately to the responsible project manager. The contractor has to produce fully dimensioned shop drawings prior to the start of the contract and they have to be approved by the client/ investor / interior designer

Project
CLINK 78 - BEDS

Logo


Project Address
CLINK 78
78 King's Cross Rd
London WC1X 9QG
United Kingdom

Client's Address
CLINK 78
78 King's Cross Rd
London WC1X 9QG
United Kingdom

Sheet Number 2-C1-301	Total Sheets 82		
Sheet Title BUNKBED 2-C1 GA	Level		
File Name 260425_CLINK 78_BEDs AA DRAFT 03.vwx			
Date 28.04.26	Sheet Size A1	Scale 1:5	Signed AA

Stefanie Jaensch INTERIOR DESIGNS
Global Headquarter | Stefanie Jaensch c/o WeWork
Taubusanlage 8 | 60329 Frankfurt a.M.
E-Mail info@stefaniejaensch.de | DE +49 (0) 174 6756098
www.stefaniejaensch.de
Legal address | Stefanie Jaensch | Offenbacher Landstraße 434 | 60599 Frankfurt a.M.
© 2023 All Rights Reserved | Stefanie Jaensch

BUNKBEDS - TYPE 2-C1 - FRONT ELEVATION

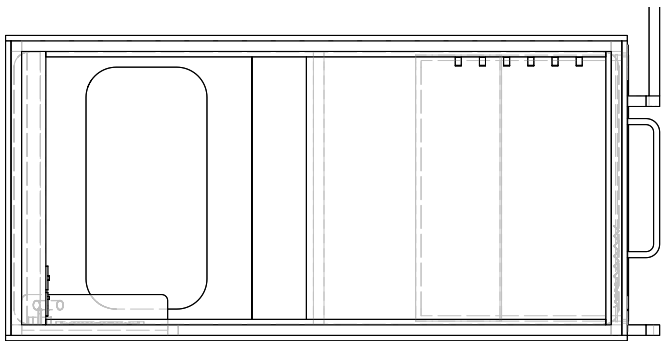

E1
2-C1-302



KEY

Index

A) 04.05.2026 Plan Set UP

All measurements have to be verified according to existing conditions by the contractor! Discrepancies must be reported immediately to the responsible project manager. The contractor has to produce fully dimensioned shop drawings prior to the start of the contract and they have to be approved by the client/ investor / interior designer

Project
CLINK 78 - BEDS



Project Address
CLINK 78
78 King's Cross Rd
London WC1X 9QG
United Kingdom

Client's Address
CLINK 78
78 King's Cross Rd
London WC1X 9QG
United Kingdom

Sheet Number	2-C1-302	Total Sheets	82
--------------	----------	--------------	----

Sheet Title	BUNKBED 2-C1 FRONT ELEVATION	Level	
-------------	------------------------------	-------	--


File Name	260425_CLINK 78_BEDs AA DRAFT 03.vwx
-----------	--------------------------------------

Date	Sheet Size	Scale	Signed
28.04.26	A1	1:8	AA



Stefanie Jaensch INTERIOR DESIGNS

Global Headquarter | Stefanie Jaensch c/o WeWork
Taubusanlage 8 | 60329 Frankfurt a.M.
E-Mail info@stefaniejaensch.de | DE +49 (0) 174 6756098
www.stefaniejaensch.de

Legal address | Stefanie Jaensch | Offenbacher Landstraße 434 | 60599 Frankfurt a.M.
© 2023 All Rights Reserved | Stefanie Jaensch

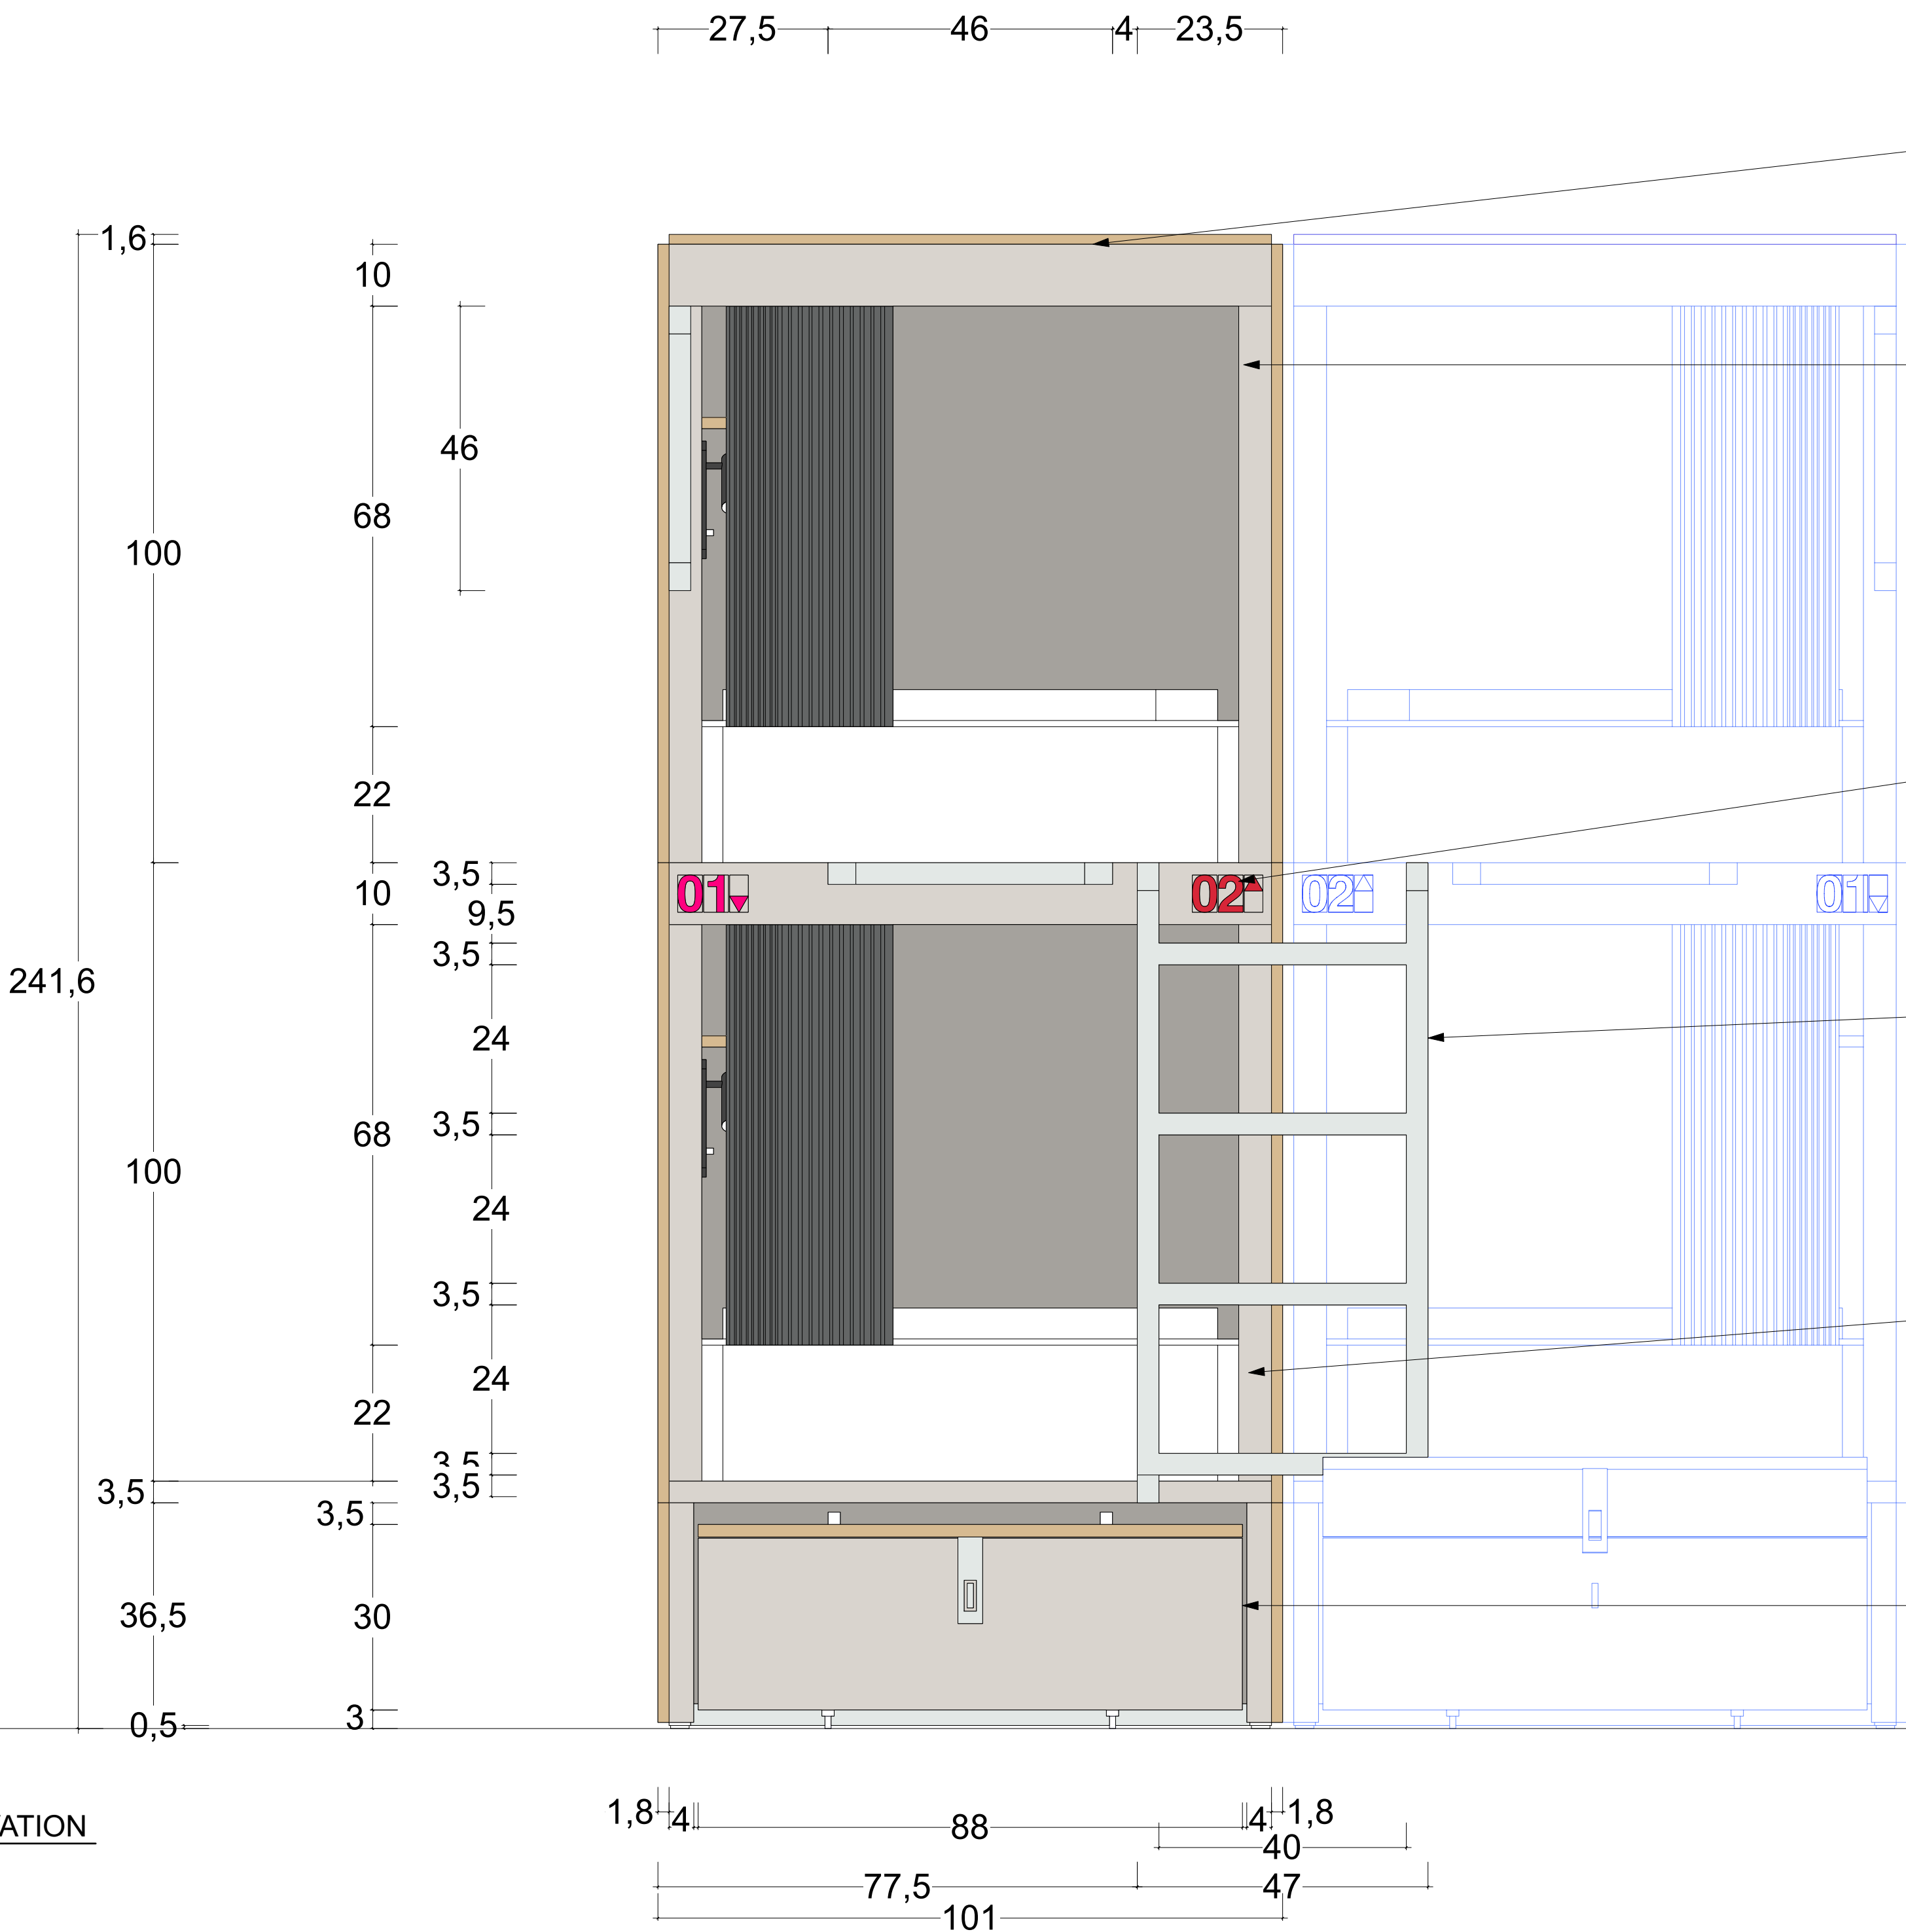

BUNKBEDS - TYPE 2-C1 - BACK ELEVATION

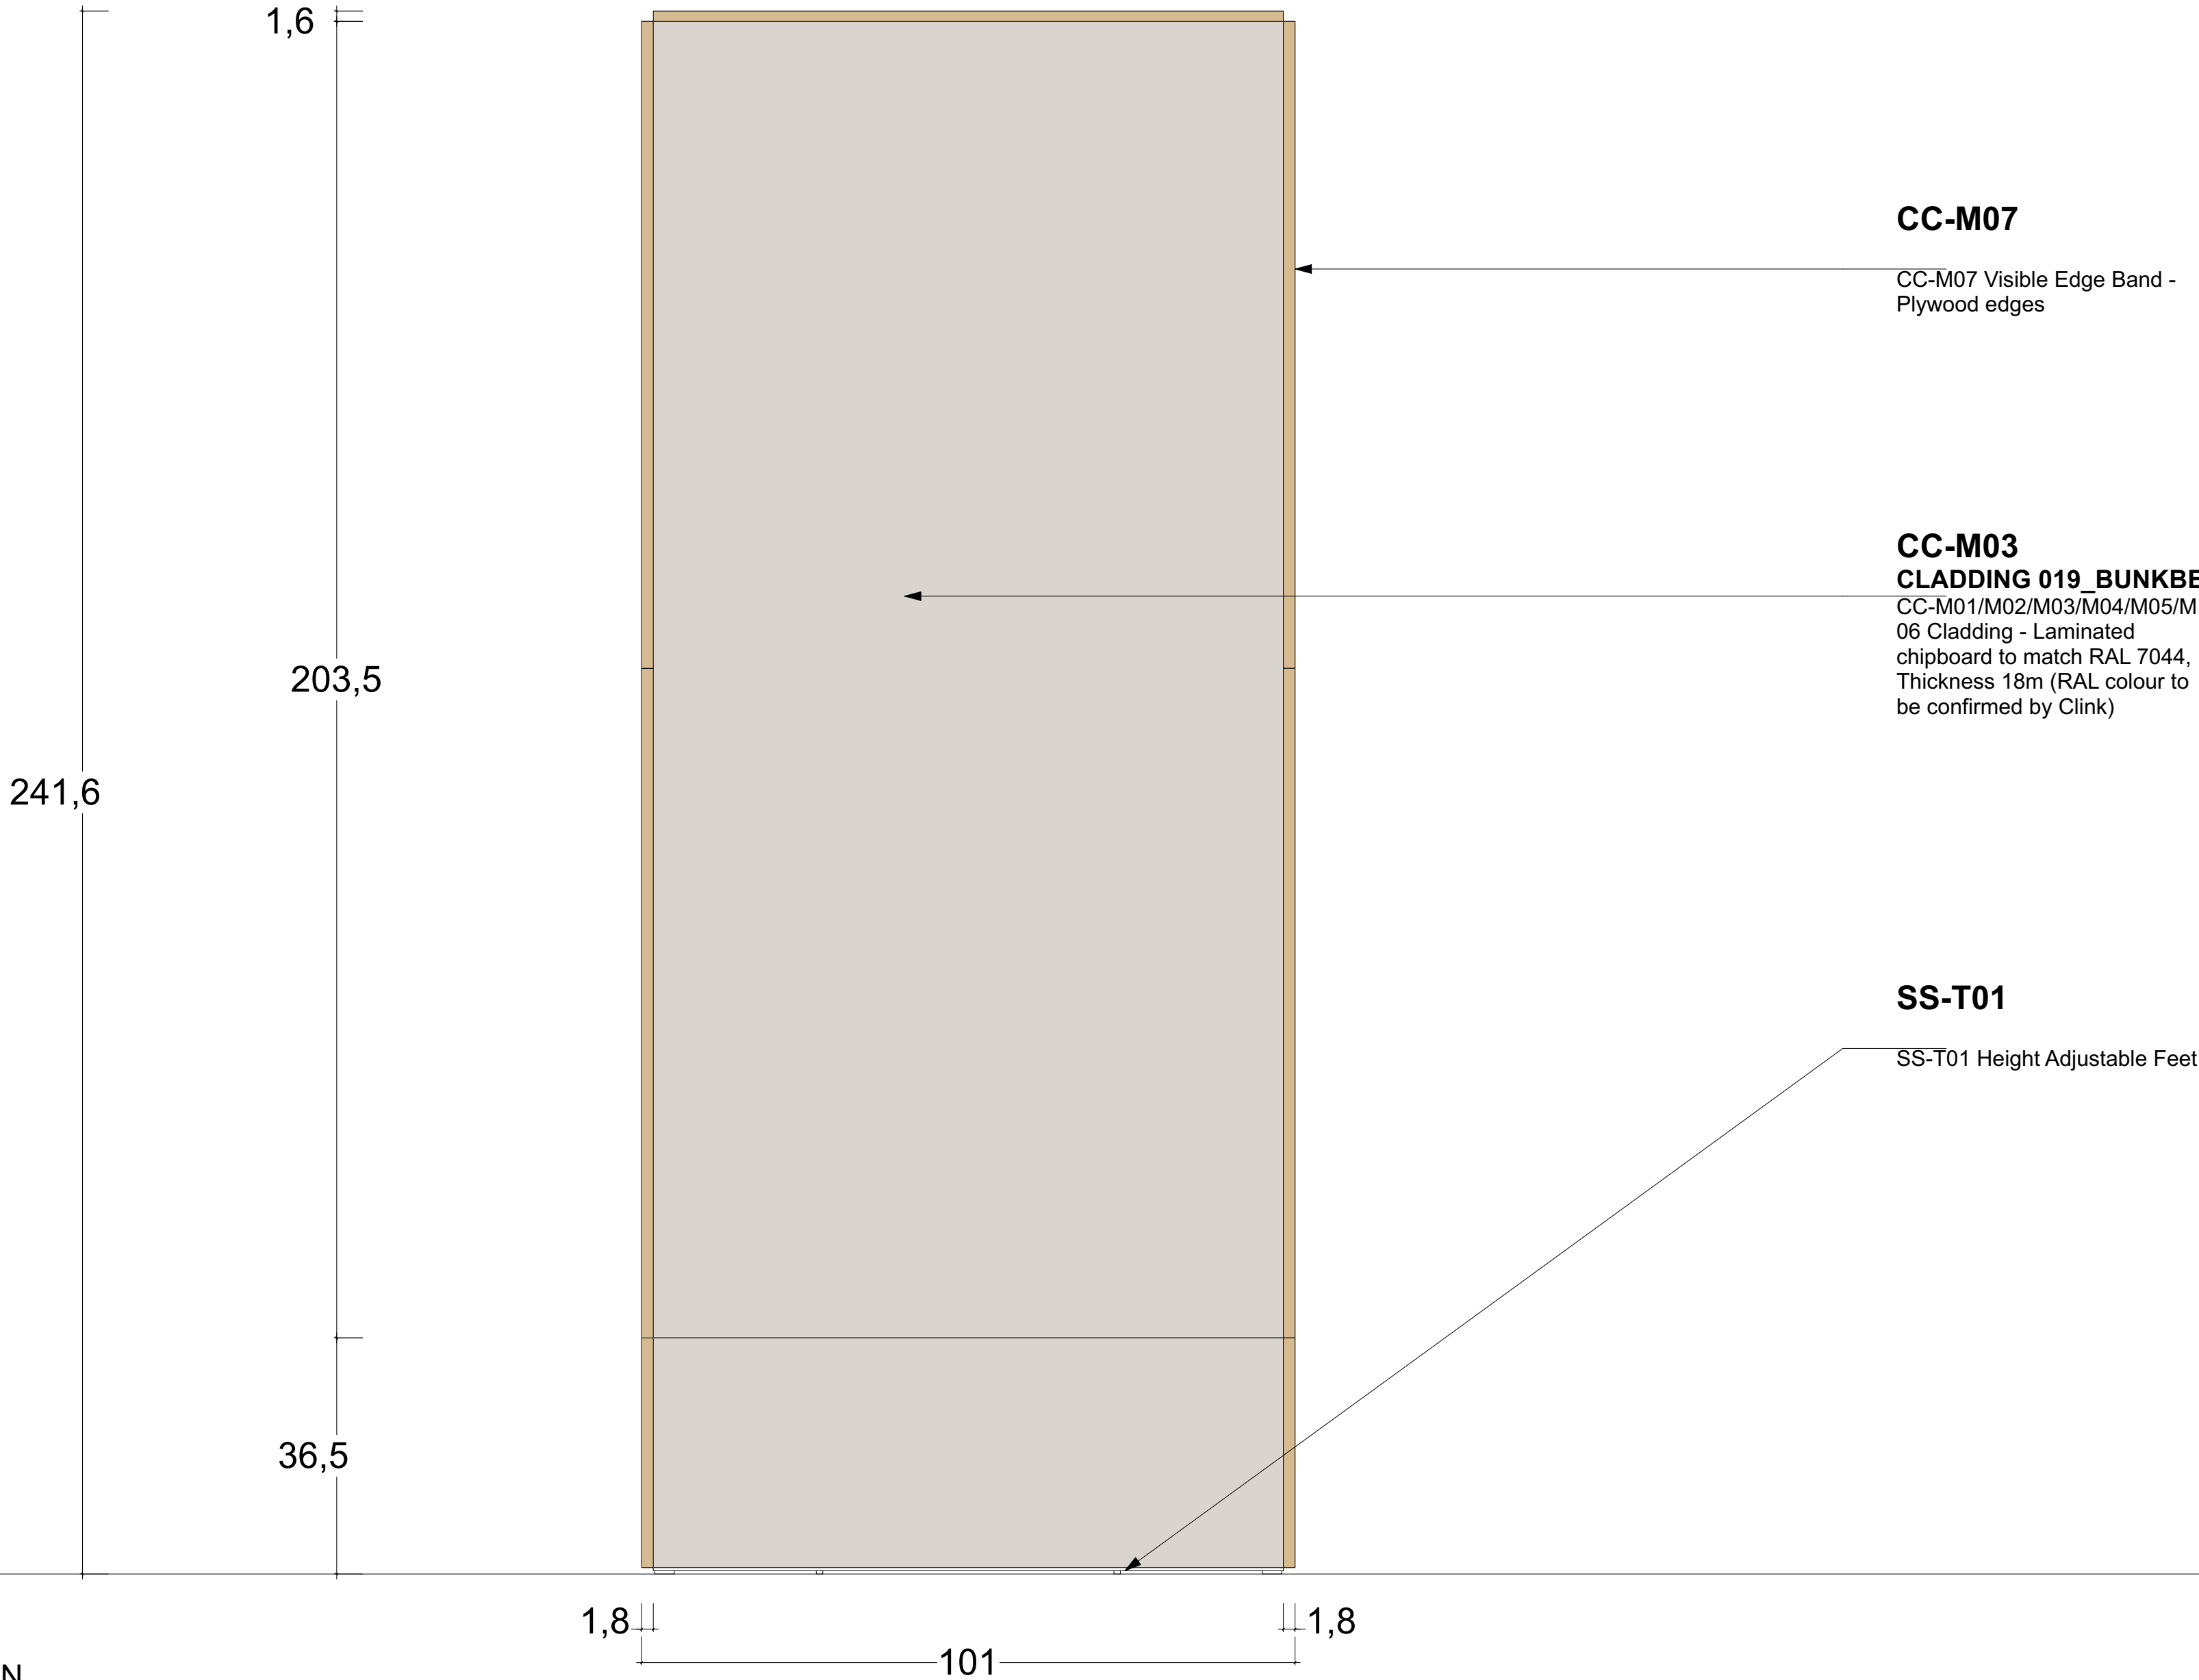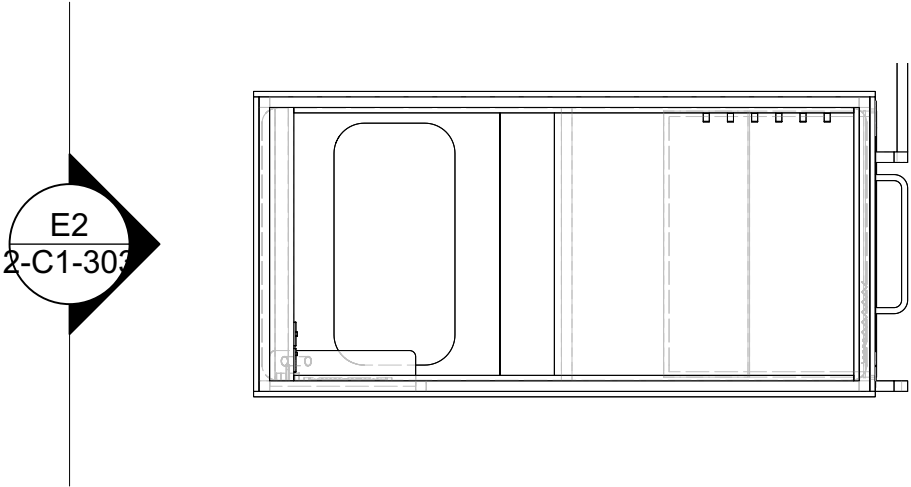

KEY

Index

A) 04.05.2026 Plan Set UP

All measurements have to be verified according to existing conditions by the contractor! Discrepancies must be reported immediately to the responsible project manager. The contractor has to produce fully dimensioned shop drawings prior to the start of the contract and they have to be approved by the client/ investor / interior designer

Project

CLINK 78 - BEDS

Logo



Project Address

CLINK 78
78 King's Cross Rd
London WC1X 9QG
United Kingdom



Client's Address

CLINK 78
78 King's Cross Rd
London WC1X 9QG
United Kingdom

Sheet Number 2-C1-303		Total Sheets 82
Sheet Title BUNKBED 2-C1 BACK ELEVATION		Level
File Name 260425_CLINK 78_BEDs AA DRAFT 03.vwx		

Date	Sheet Size	Scale	Signed
28.04.26	A1	1:8	AA

BUNKBEDS - TYPE 2-C1 - RIGHT ELEVATION

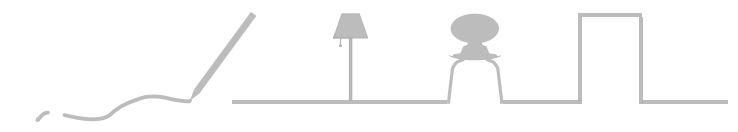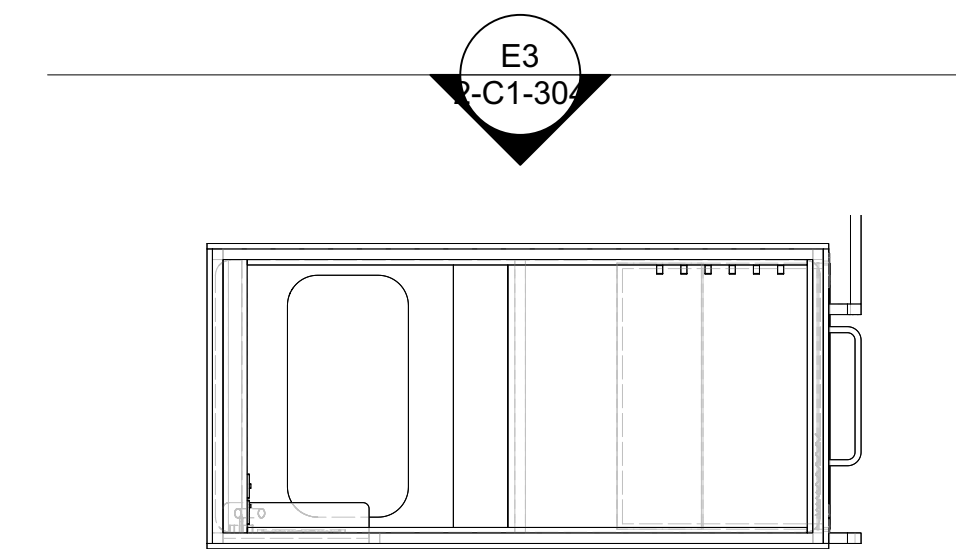

KEY

Index

A) 04.05.2026 Plan Set UP

All measurements have to be verified according to existing conditions by the contractor! Discrepancies must be reported immediately to the responsible project manager. The contractor has to produce fully dimensioned shop drawings prior to the start of the contract and they have to be approved by the client/investor / interior designer

Project	
---------	--

CLINK 78 - BEDS

Logo



Project Address

CLINK 78
78 King's Cross Rd
London WC1X 9QG
United Kingdom

Client's Address

CLINK 78
78 King's Cross Rd
London WC1X 9QG
United Kingdom

Sheet Number 2-C1-304			Total Sheets 82
Sheet Title <i>BUNKBED 2-C1 RIGHT ELEVATION</i>			Level
File Name <i>260425_CLINK 78_BEDs AA DRAFT 03.vwx</i>			
Date 28.04.26	Sheet Size A1	Scale 1:8	Signed AA

Stefanie Jaensch INTERIOR DESIGNS


Global Headquarter | Stefanie Jaensch c/o WeWork

Taunusanlage 8 | 60329 Frankfurt a.M.



www.stefaniejaensch.de

Legal address | Stefanie Jaensch | Offenbacher Landstraße 434 | 60599 Frankfurt a.M.

© 2023 All Rights Reserved | Stefanie Jaensch

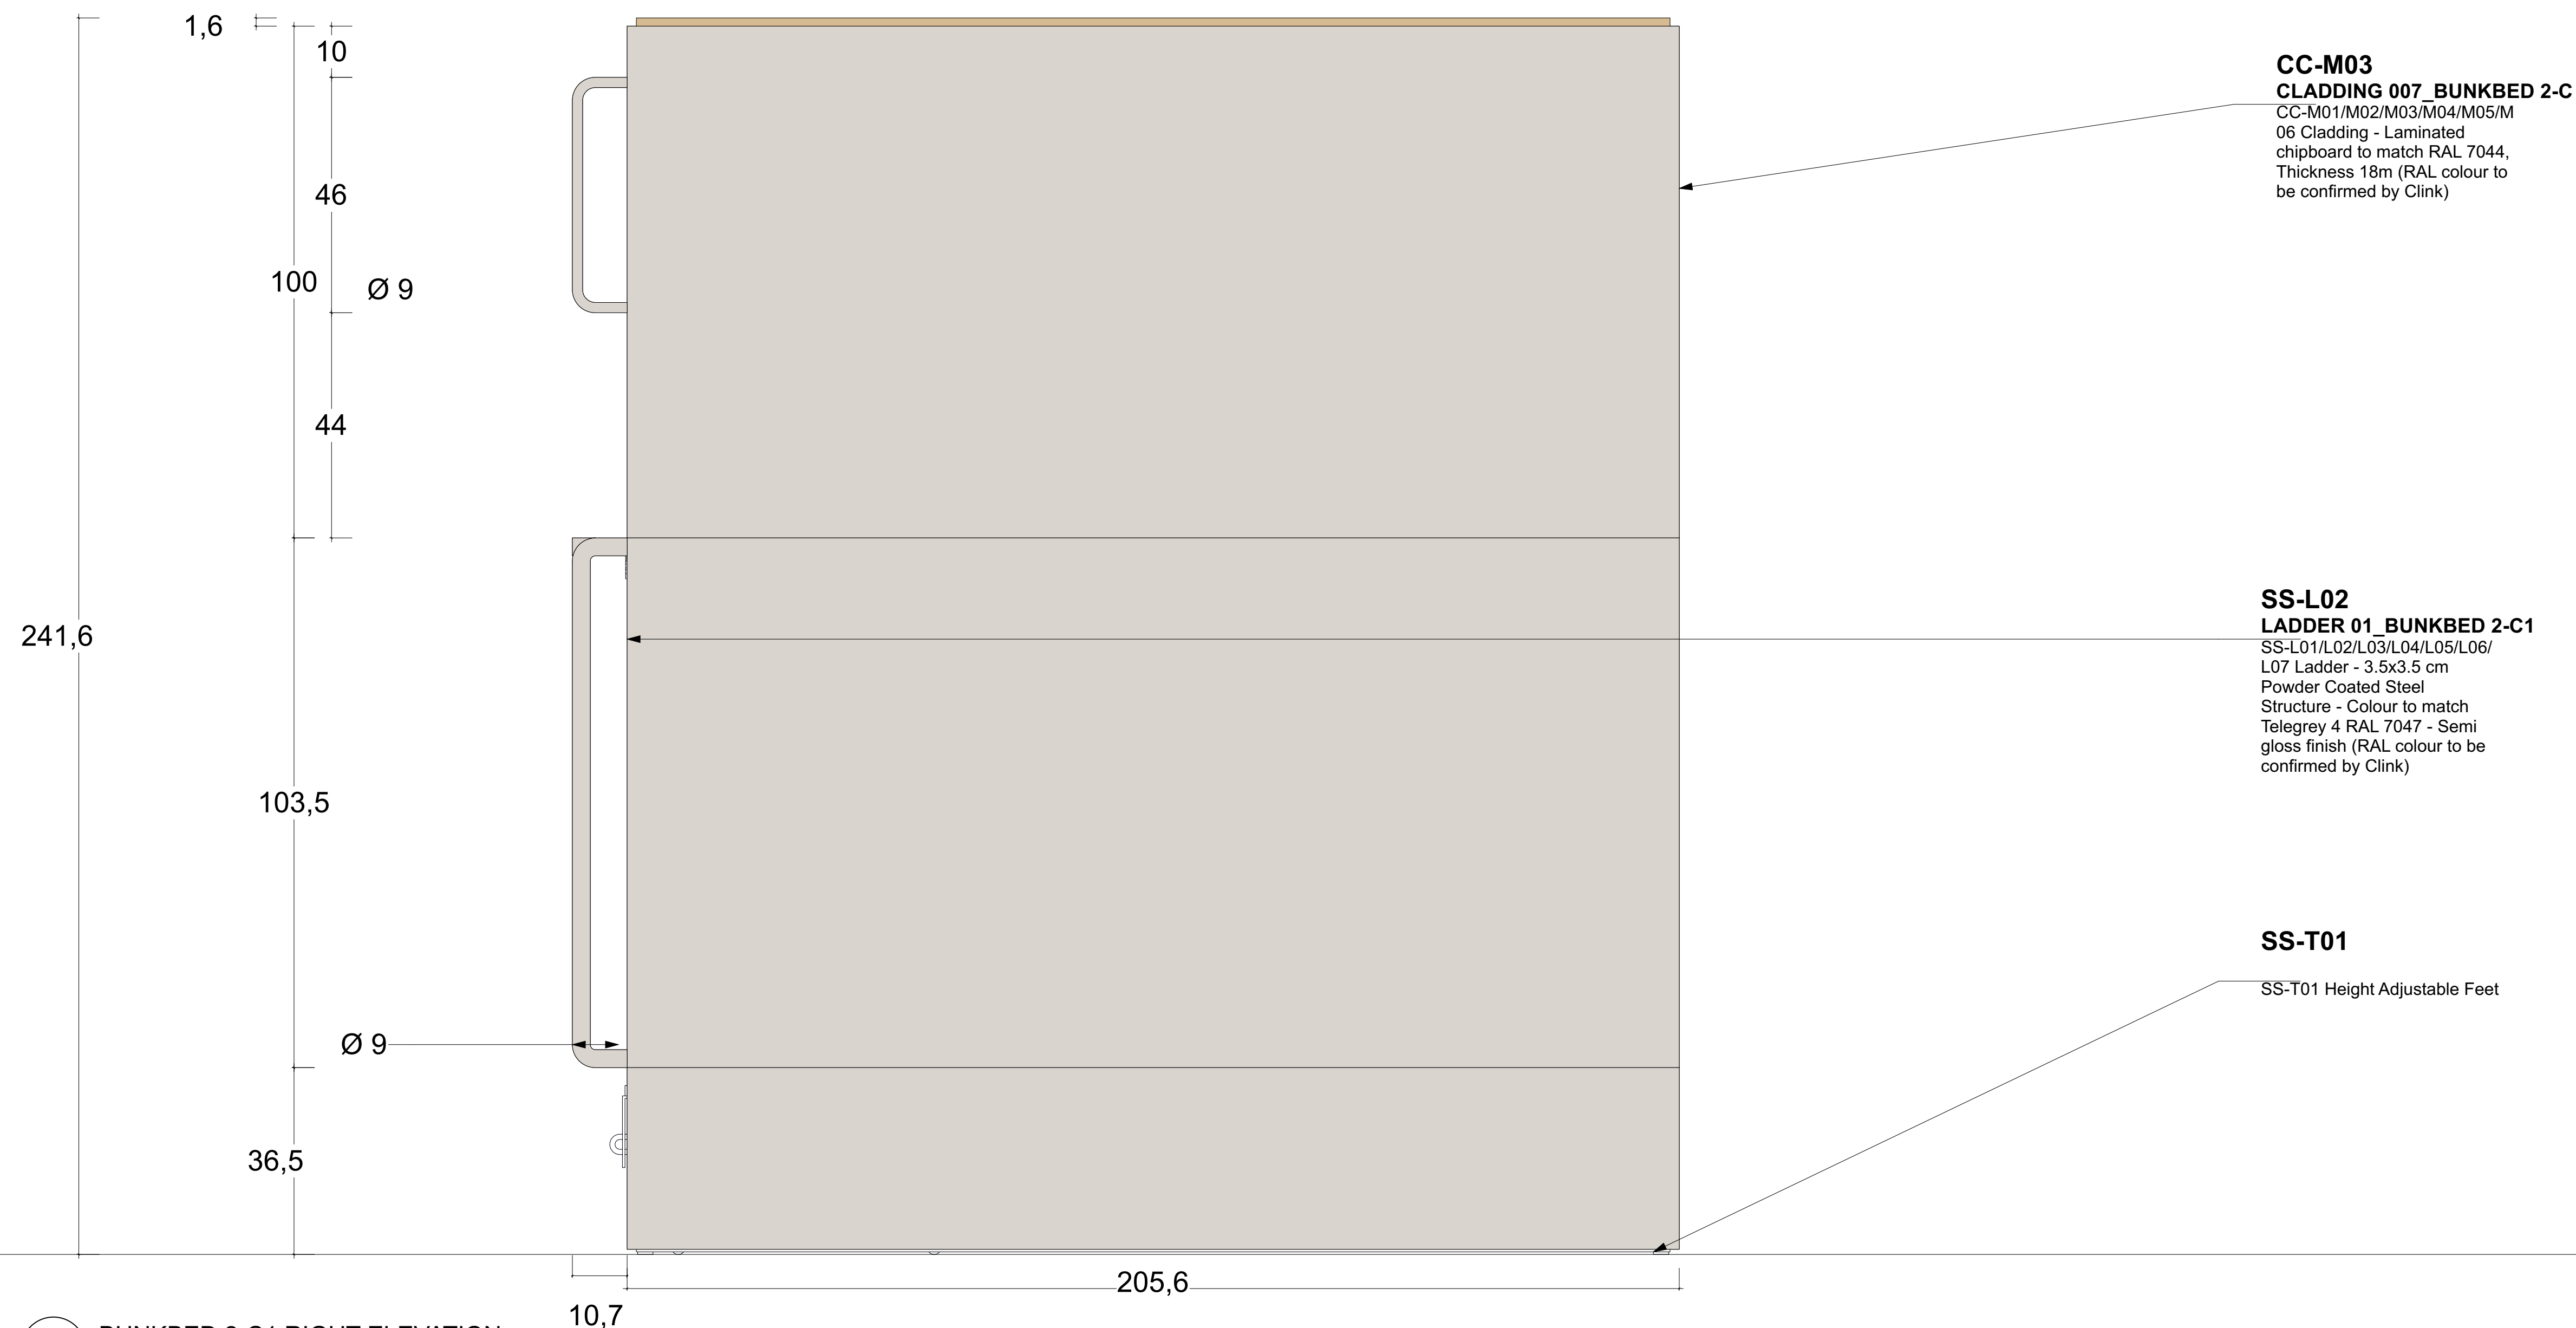

BUNKBEDS - TYPE 2-C1 - LEFT ELEVATION

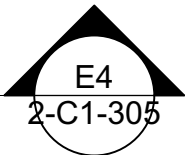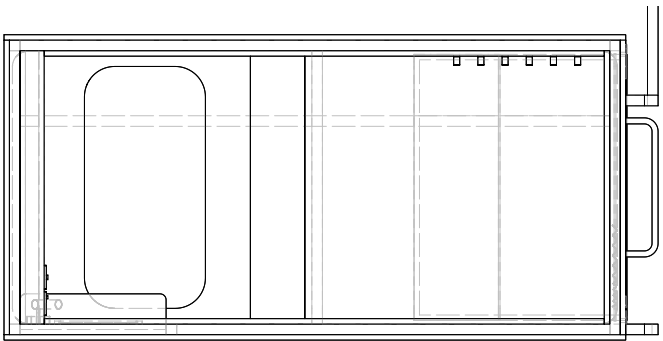

KEY

Index

A) 04.05.2026 Plan Set UP

All measurements have to be verified according to existing conditions by the contractor! Discrepancies must be reported immediately to the responsible project manager. The contractor has to produce fully dimensioned shop drawings prior to the start of the contract and they have to be approved by the client/ investor / interior designer

Project

CLINK 78 - BEDS

Logo



Project Address

CLINK 78
78 King's Cross Rd
London WC1X 9QG
United Kingdom


Client's Address

CLINK 78
78 King's Cross Rd
London WC1X 9QG
United Kingdom


Sheet Number 2-C1-305		Total Sheets 82
Sheet Title BUNKBED 2-C1 LEFT ELEVATION		Level
File Name 260425_CLINK 78_BEDs AA DRAFT 03.vwx		

Date	Sheet Size	Scale	Signed
28.04.26	A1	1:8	AA

Stefanie Jaensch INTERIOR DESIGNS
Global Headquarter | Stefanie Jaensch c/o WeWork
Taunusanlage 8 | 60329 Frankfurt a.M.
E-Mail info@stefaniejaensch.de | DE +49 (0) 174 6756098
www.stefaniejaensch.de
Legal address | Stefanie Jaensch | Offenbacher Landstraße 434 | 60599 Frankfurt a.M.
© 2023 All Rights Reserved | Stefanie Jaensch

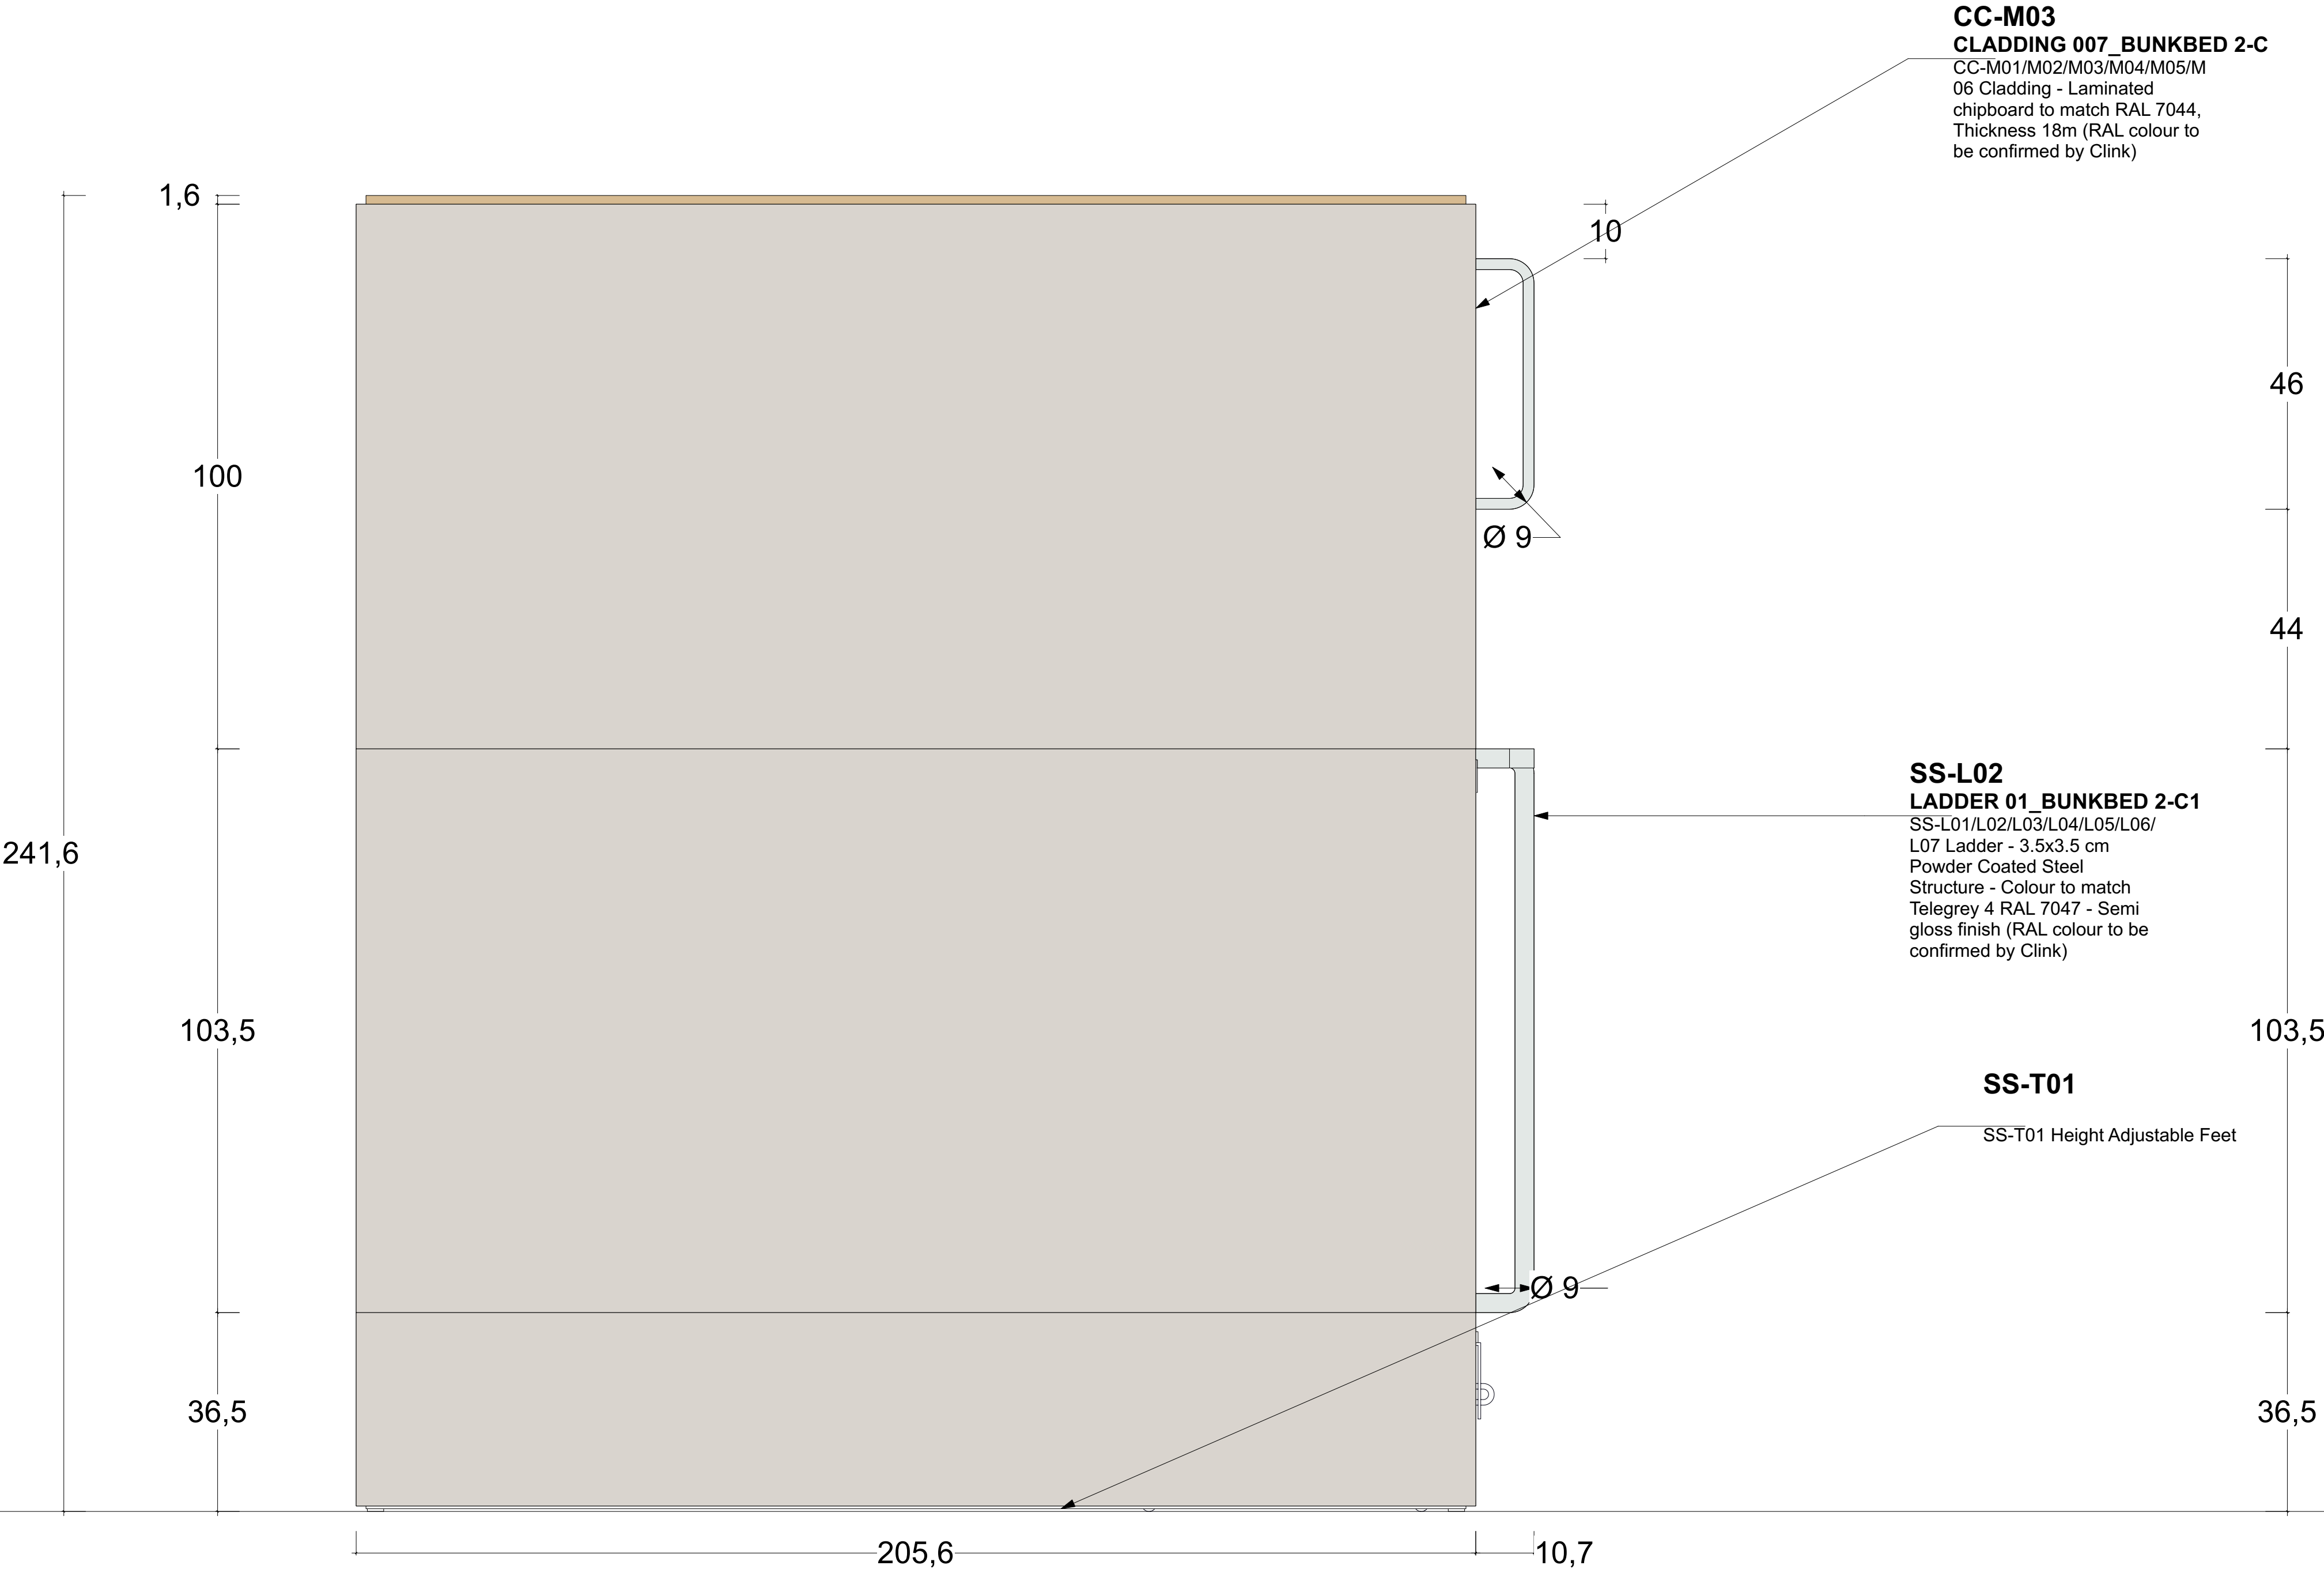

BUNKBEDS - TYPE 2-C1 - SECTION 1

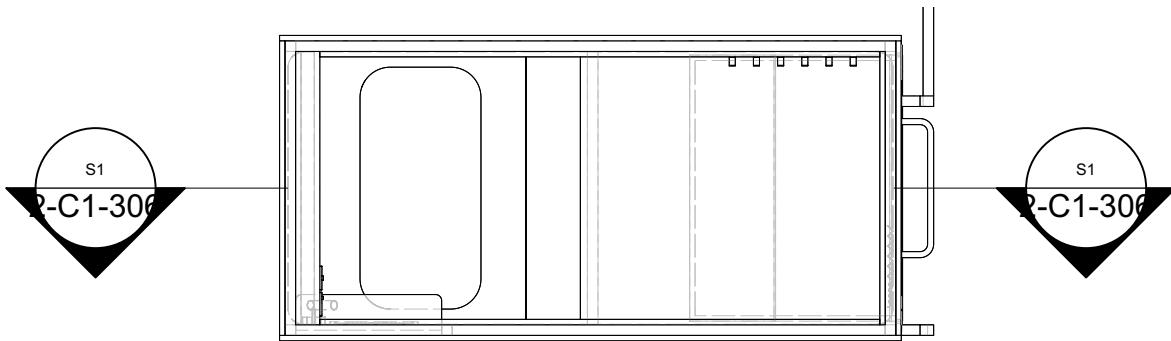

KEY

Index

A) 04.05.2026 Plan Set UP

All measurements have to be verified according to existing conditions by the contractor! Discrepancies must be reported immediately to the responsible project manager. The contractor has to produce fully dimensioned shop drawings prior to the start of the contract and they have to be approved by the client/ investor / interior designer

Project
CLINK 78 - BEDS




Project Address
CLINK 78
78 King's Cross Rd
London WC1X 9QG
United Kingdom

Client's Address
CLINK 78
78 King's Cross Rd
London WC1X 9QG
United Kingdom

Sheet Number	2-C1-306	Total Sheets	82
Sheet Title	BUNKBED 2-C1 SECTION 1	Level	
File Name			
260425_CLINK 78_BEDs AA DRAFT 03.vwx			

Date	Sheet Size	Scale	Signed
28.04.26	A1	1:8	AA

Stefanie Jaensch INTERIOR DESIGNS
Global Headquarter | Stefanie Jaensch c/o WeWork
Taunusanlage 8 | 60329 Frankfurt a.M.
E-Mail info@stefaniejaensch.de | DE +49 (0) 174 6756098
www.stefaniejaensch.de
Legal address | Stefanie Jaensch | Offenbacher Landstraße 434 | 60599 Frankfurt a.M.
© 2023 All Rights Reserved | Stefanie Jaensch

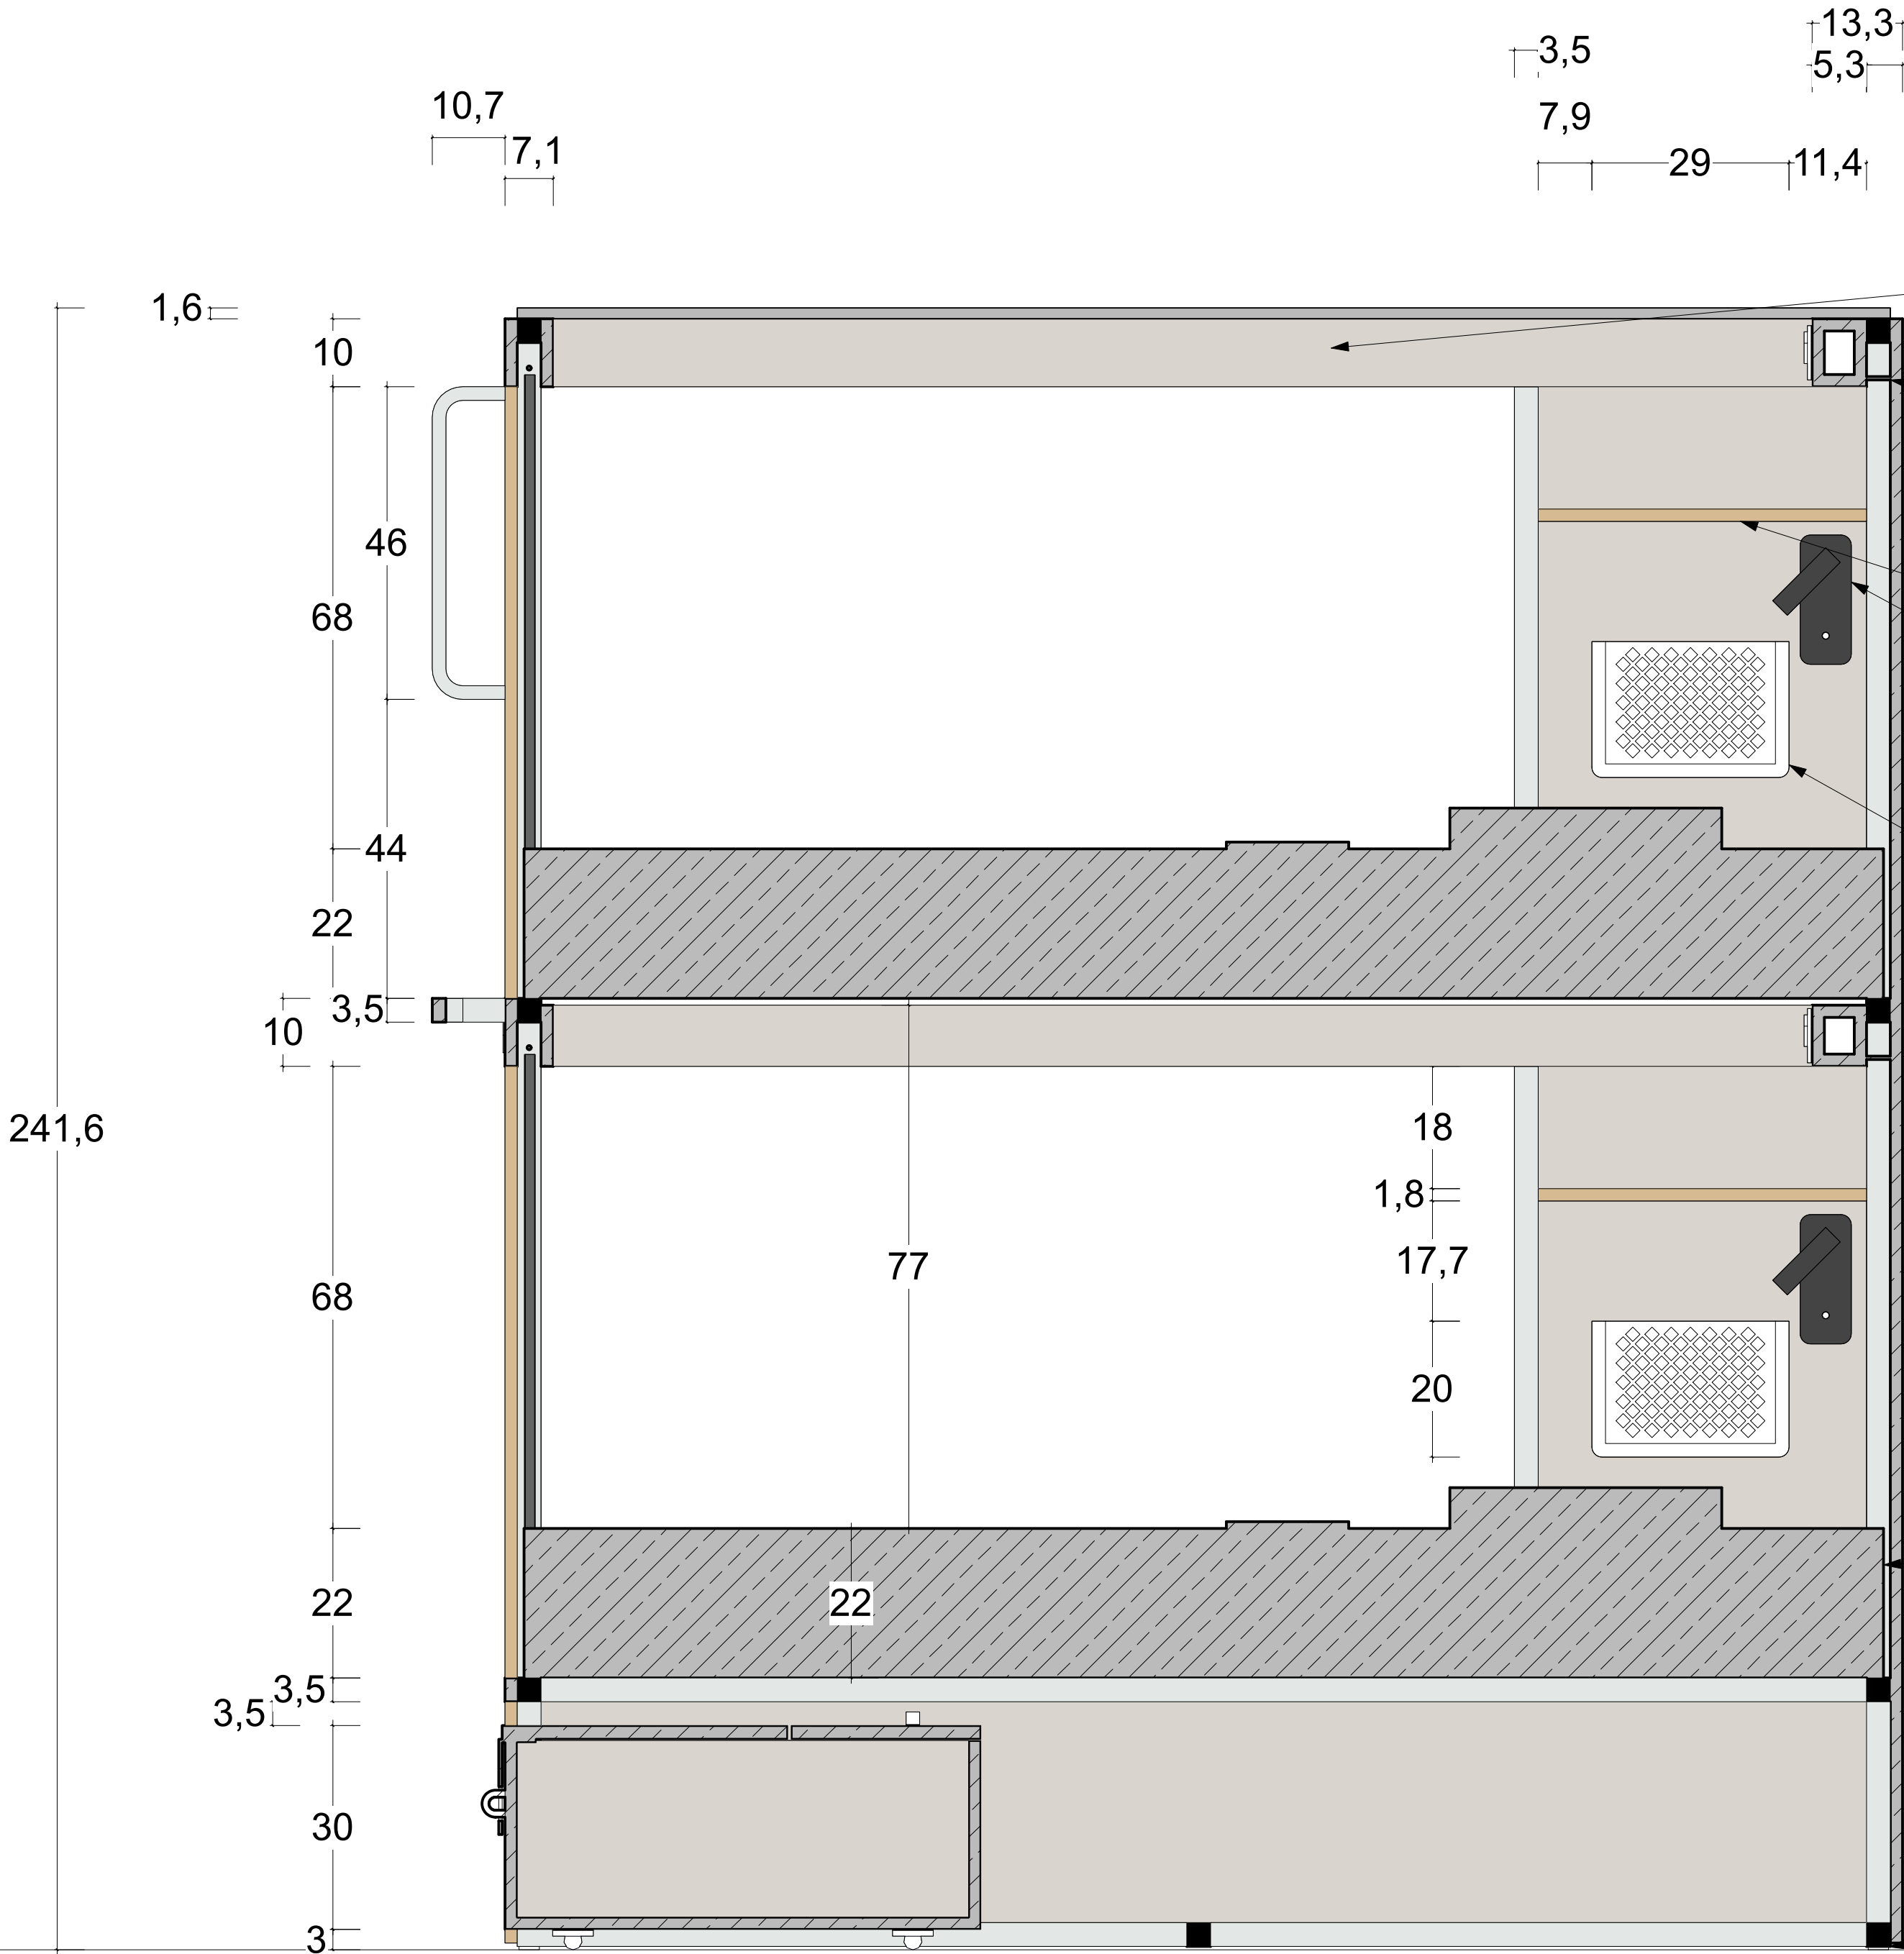

CC-M03
CLADDING 007_BUNKBED 2-C
CC-M01/M02/M03/M04/M05/M
06 Cladding - Laminated
chipboard to match RAL 7044,
Thickness 18m (RAL colour to
be confirmed by Clink)

EE-L03
LED LIGHT 005_BUNKBED 2C
EE-L01/L02/L03/L04/L05/L06
LED light with light diffuser -
LED stripes - 2000 Calvin -
Warmwhite (in Al profile,
recessed)

AA-F01
SHELF 06_BUNKBED 2-ABC
AA-F01 Shelf - Laminated
chipboard to match RAL 7044,
Thickness 18m (RAL colour to
be confirmed by Clink)


EE-L07
READING LIGHT 006_BUNKBED 2-ABC
EE-L07 Reading light - Aron
16/3240 Wall Lamp Textured
Black,

AA-M01
MESH POCKET 006_BUNKBED 2-ABC
AA-M01 Mesh pocket
30x20cm frame: white - net:
white - 2 pc. per bunk bed
(final colour to be confirmed by
Clink)

FF-M01
MATTRESS 05_BUNKBED 2-ABC
FF-M01 Mattress -
90x200x22cm - (Foam
mattress - Fire retardant fabric
and foam (Crib 5) - 100gr/m2
polyester - Reinforcement -
Cover should be washable on
40 degrees) - Final height TBC
(18/20/22 cm)

SS-T01
SS-T01 Height Adjustable Feet

BUNKBEDS - TYPE 2-C1 - SECTION 2

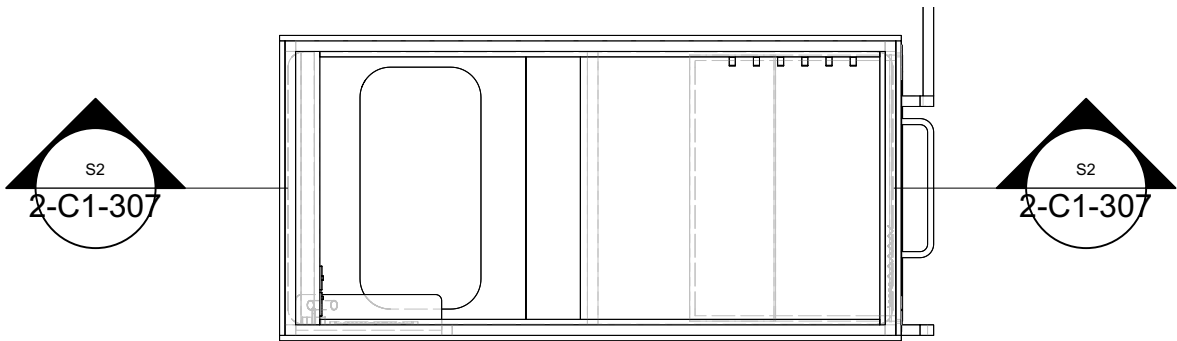

KEY

Index

A) 04.05.2026 Plan Set UP

All measurements have to be verified according to existing conditions by the contractor! Discrepancies must be reported immediately to the responsible project manager. The contractor has to produce fully dimensioned shop drawings prior to the start of the contract and they have to be approved by the client/ investor / interior designer

Project
CLINK 78 - BEDS




Project Address
CLINK 78
78 King's Cross Rd
London WC1X 9QG
United Kingdom

Client's Address
CLINK 78
78 King's Cross Rd
London WC1X 9QG
United Kingdom

Sheet Number 2-C1-307		Total Sheets 82	
Sheet Title BUNKBED 2-C1 SECTION 2		Level	
File Name 260425_CLINK 78_BEDs AA DRAFT 03.vwx			
Date 28.04.26	Sheet Size A1	Scale 1:8	Signed AA

Stefanie Jaensch INTERIOR DESIGNS
Global Headquarter | Stefanie Jaensch c/o WeWork
Taunusanlage 8 | 60329 Frankfurt a.M.
E-Mail info@stefaniejaensch.de | DE +49 (0) 174 6756098
www.stefaniejaensch.de
Legal address | Stefanie Jaensch | Offenbacher Landstraße 434 | 60599 Frankfurt a.M.
© 2023 All Rights Reserved | Stefanie Jaensch

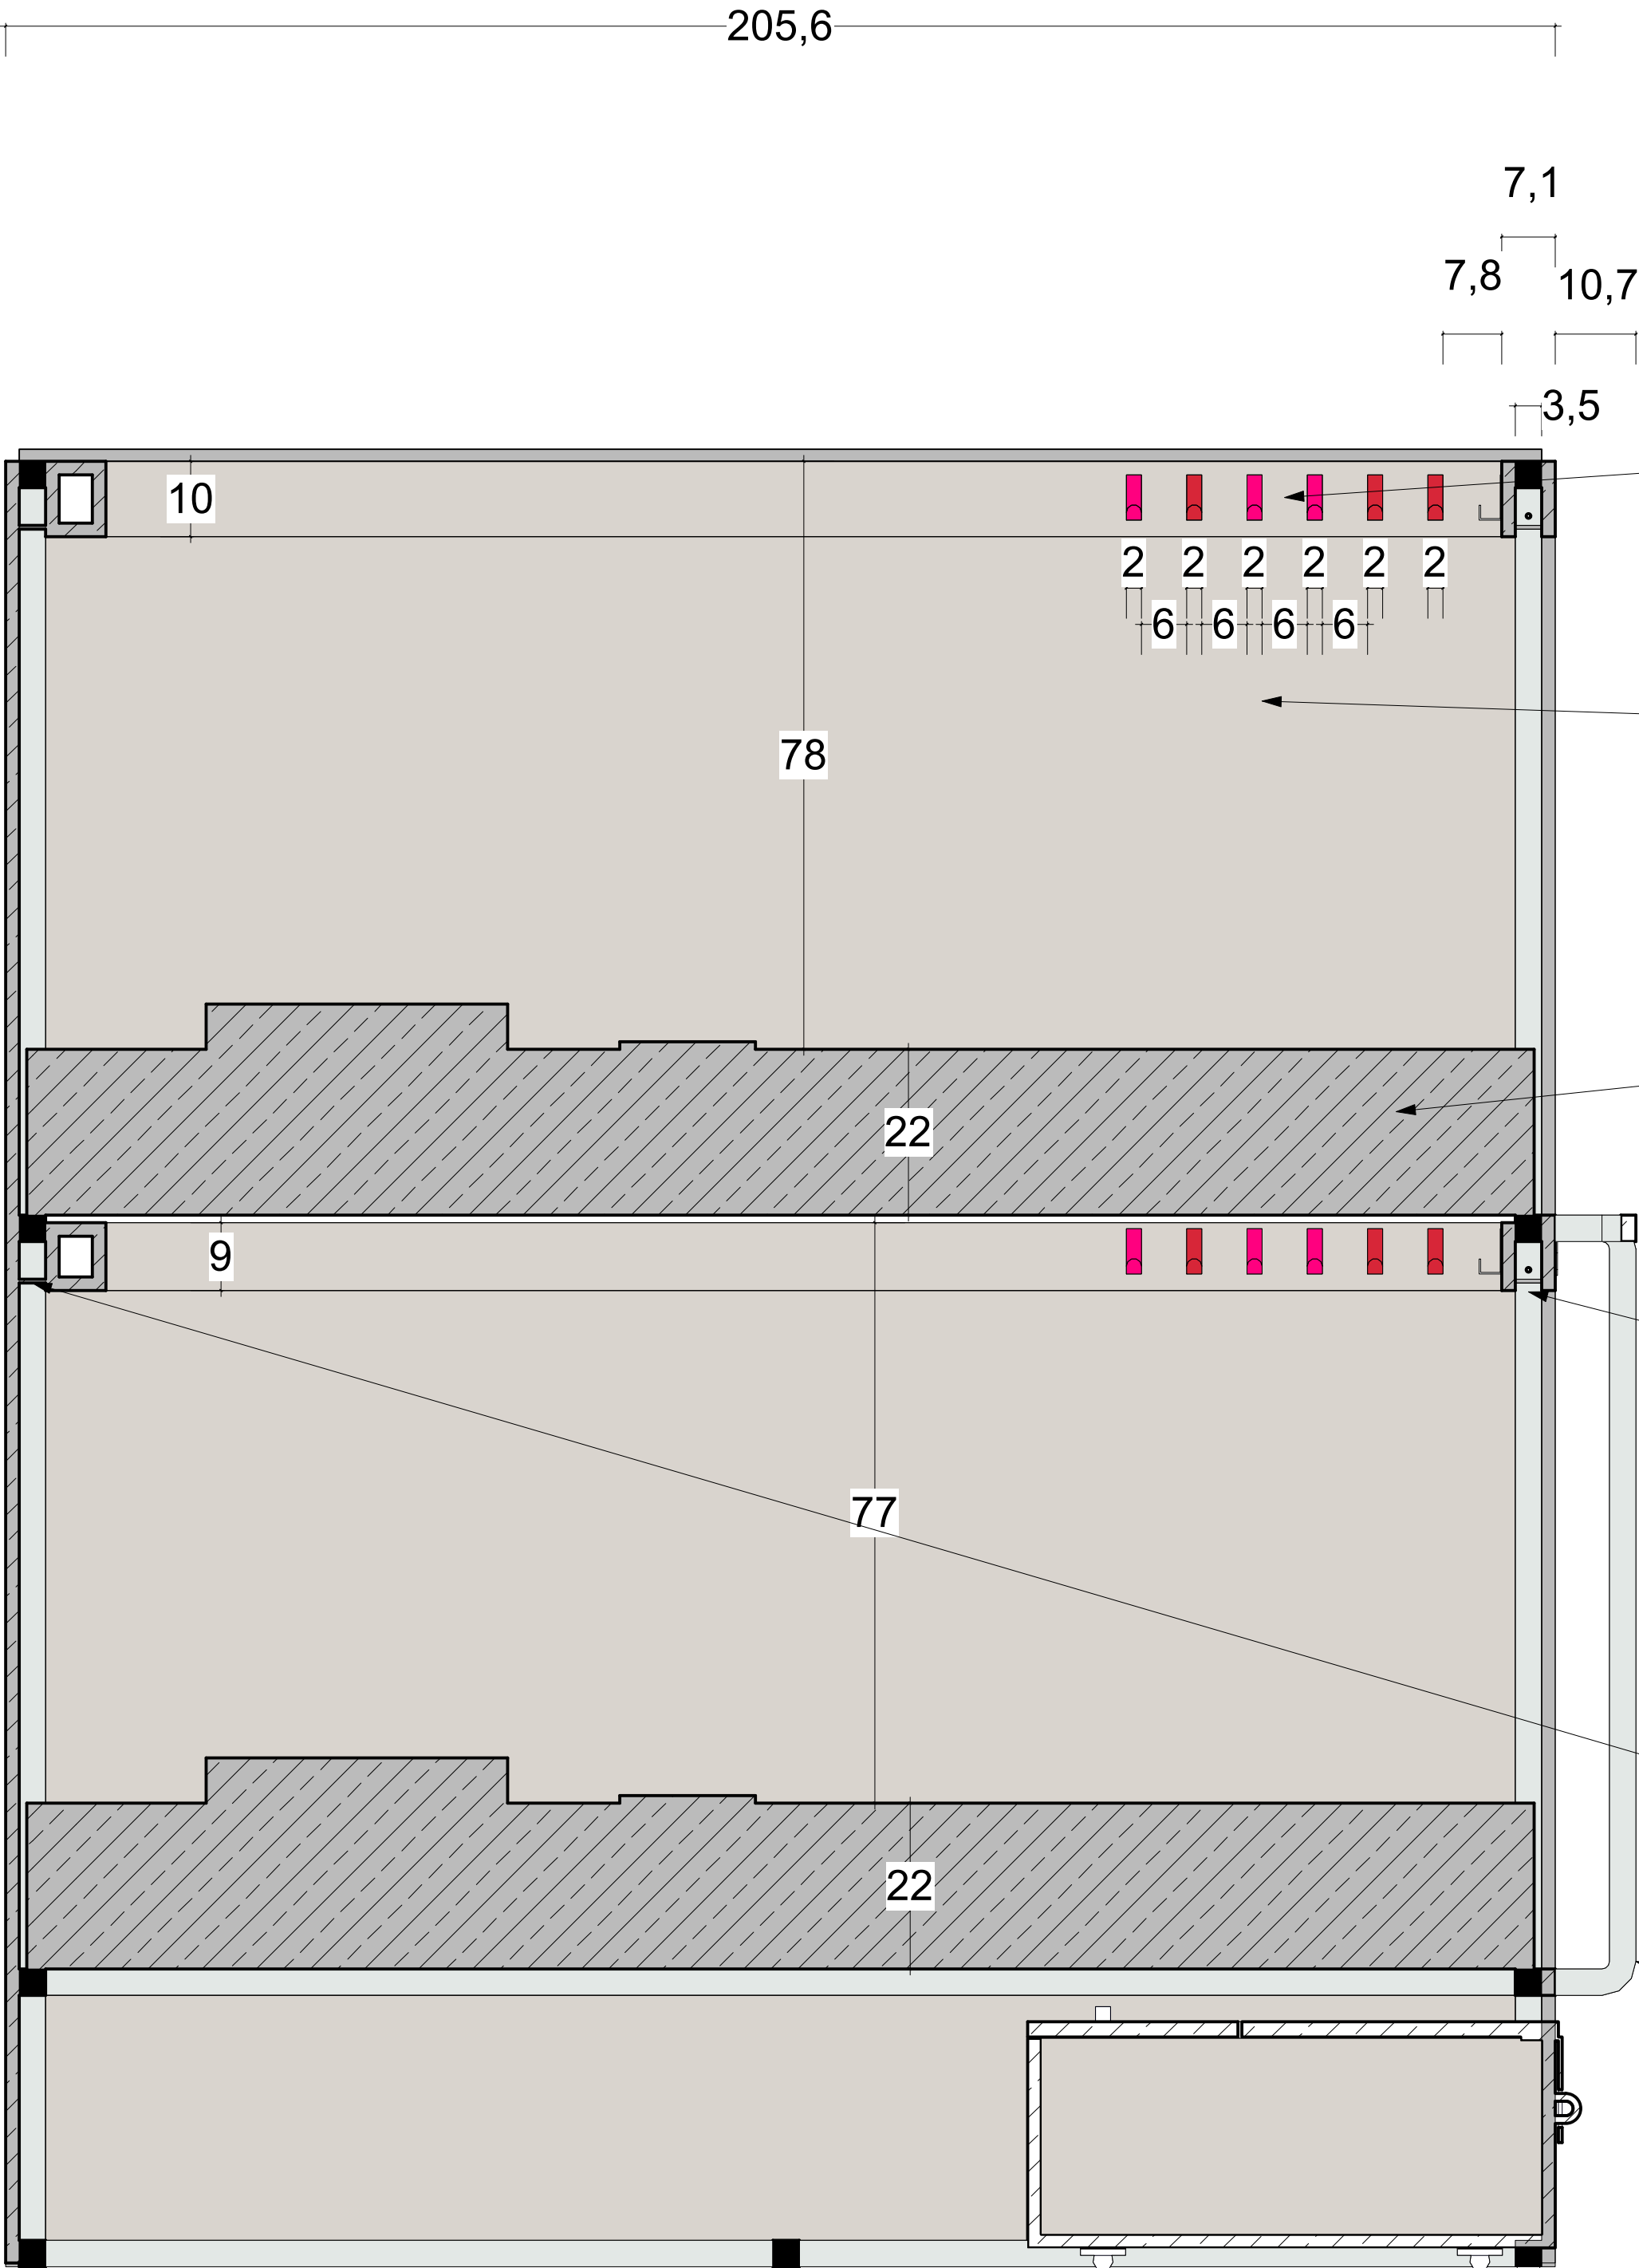

AA-H01
HOOKS 06-BUNKBED 2-ABC
AA-H01 - Hooks - stainless steel powder-coated (art.2326 PB12)- RAL 3020 Red & RAL 4010 Rose (RAL colour to be confirmed by Clink)

CC-M03
CLADDING 019_BUNKBED 2-C
CC-M01/M02/M03/M04/M05/M06 Cladding - Laminated chipboard to match RAL 7044, Thickness 18m (RAL colour to be confirmed by Clink)



FF-M01
MATTRESS 06_BUNKBED 2-ABC
FF-M01 Mattress - 90x200x22cm - (Foam mattress - Fire retardant fabric and foam (Crib 5) - 100gr/m2 polyester - Reinforcement - Cover should be washable on 40 degrees) - Final height TBC (18/20/22 cm)

FF-C02
CURTAINS 02_BUNKBED 2-BC
FF-C01/C02/C03 Privacy curtain - Washable Fabric -colour: dark grey/ anthracite less fold -Almost 1:1 fold factor to open horizontally- fire-retardant fabric - Matt Finish - CURTAINS-LUNA BLACKOUT-by SKOPOS-TEX L15 GUNMETAL-(RAL colour tbc by Clink)

EE-L03
LED LIGHT 003_BUNKBED 2C
EE-L01/L02/L03/L04/L05/L06 LED light with light diffuser - LED stripes - 2000 Calvin - Warmwhite (in Al profile, recessed)

SS-L02
LADDER 01_BUNKBED 2-C1
SS-L01/L02/L03/L04/L05/L06/L07 Ladder - 3.5x3.5 cm Powder Coated Steel Structure - Colour to match Telegrey 4 RAL 7047 - Semi gloss finish (RAL colour to be confirmed by Clink)

BUNKBEDS - TYPE 2-C1 - SECTION 3

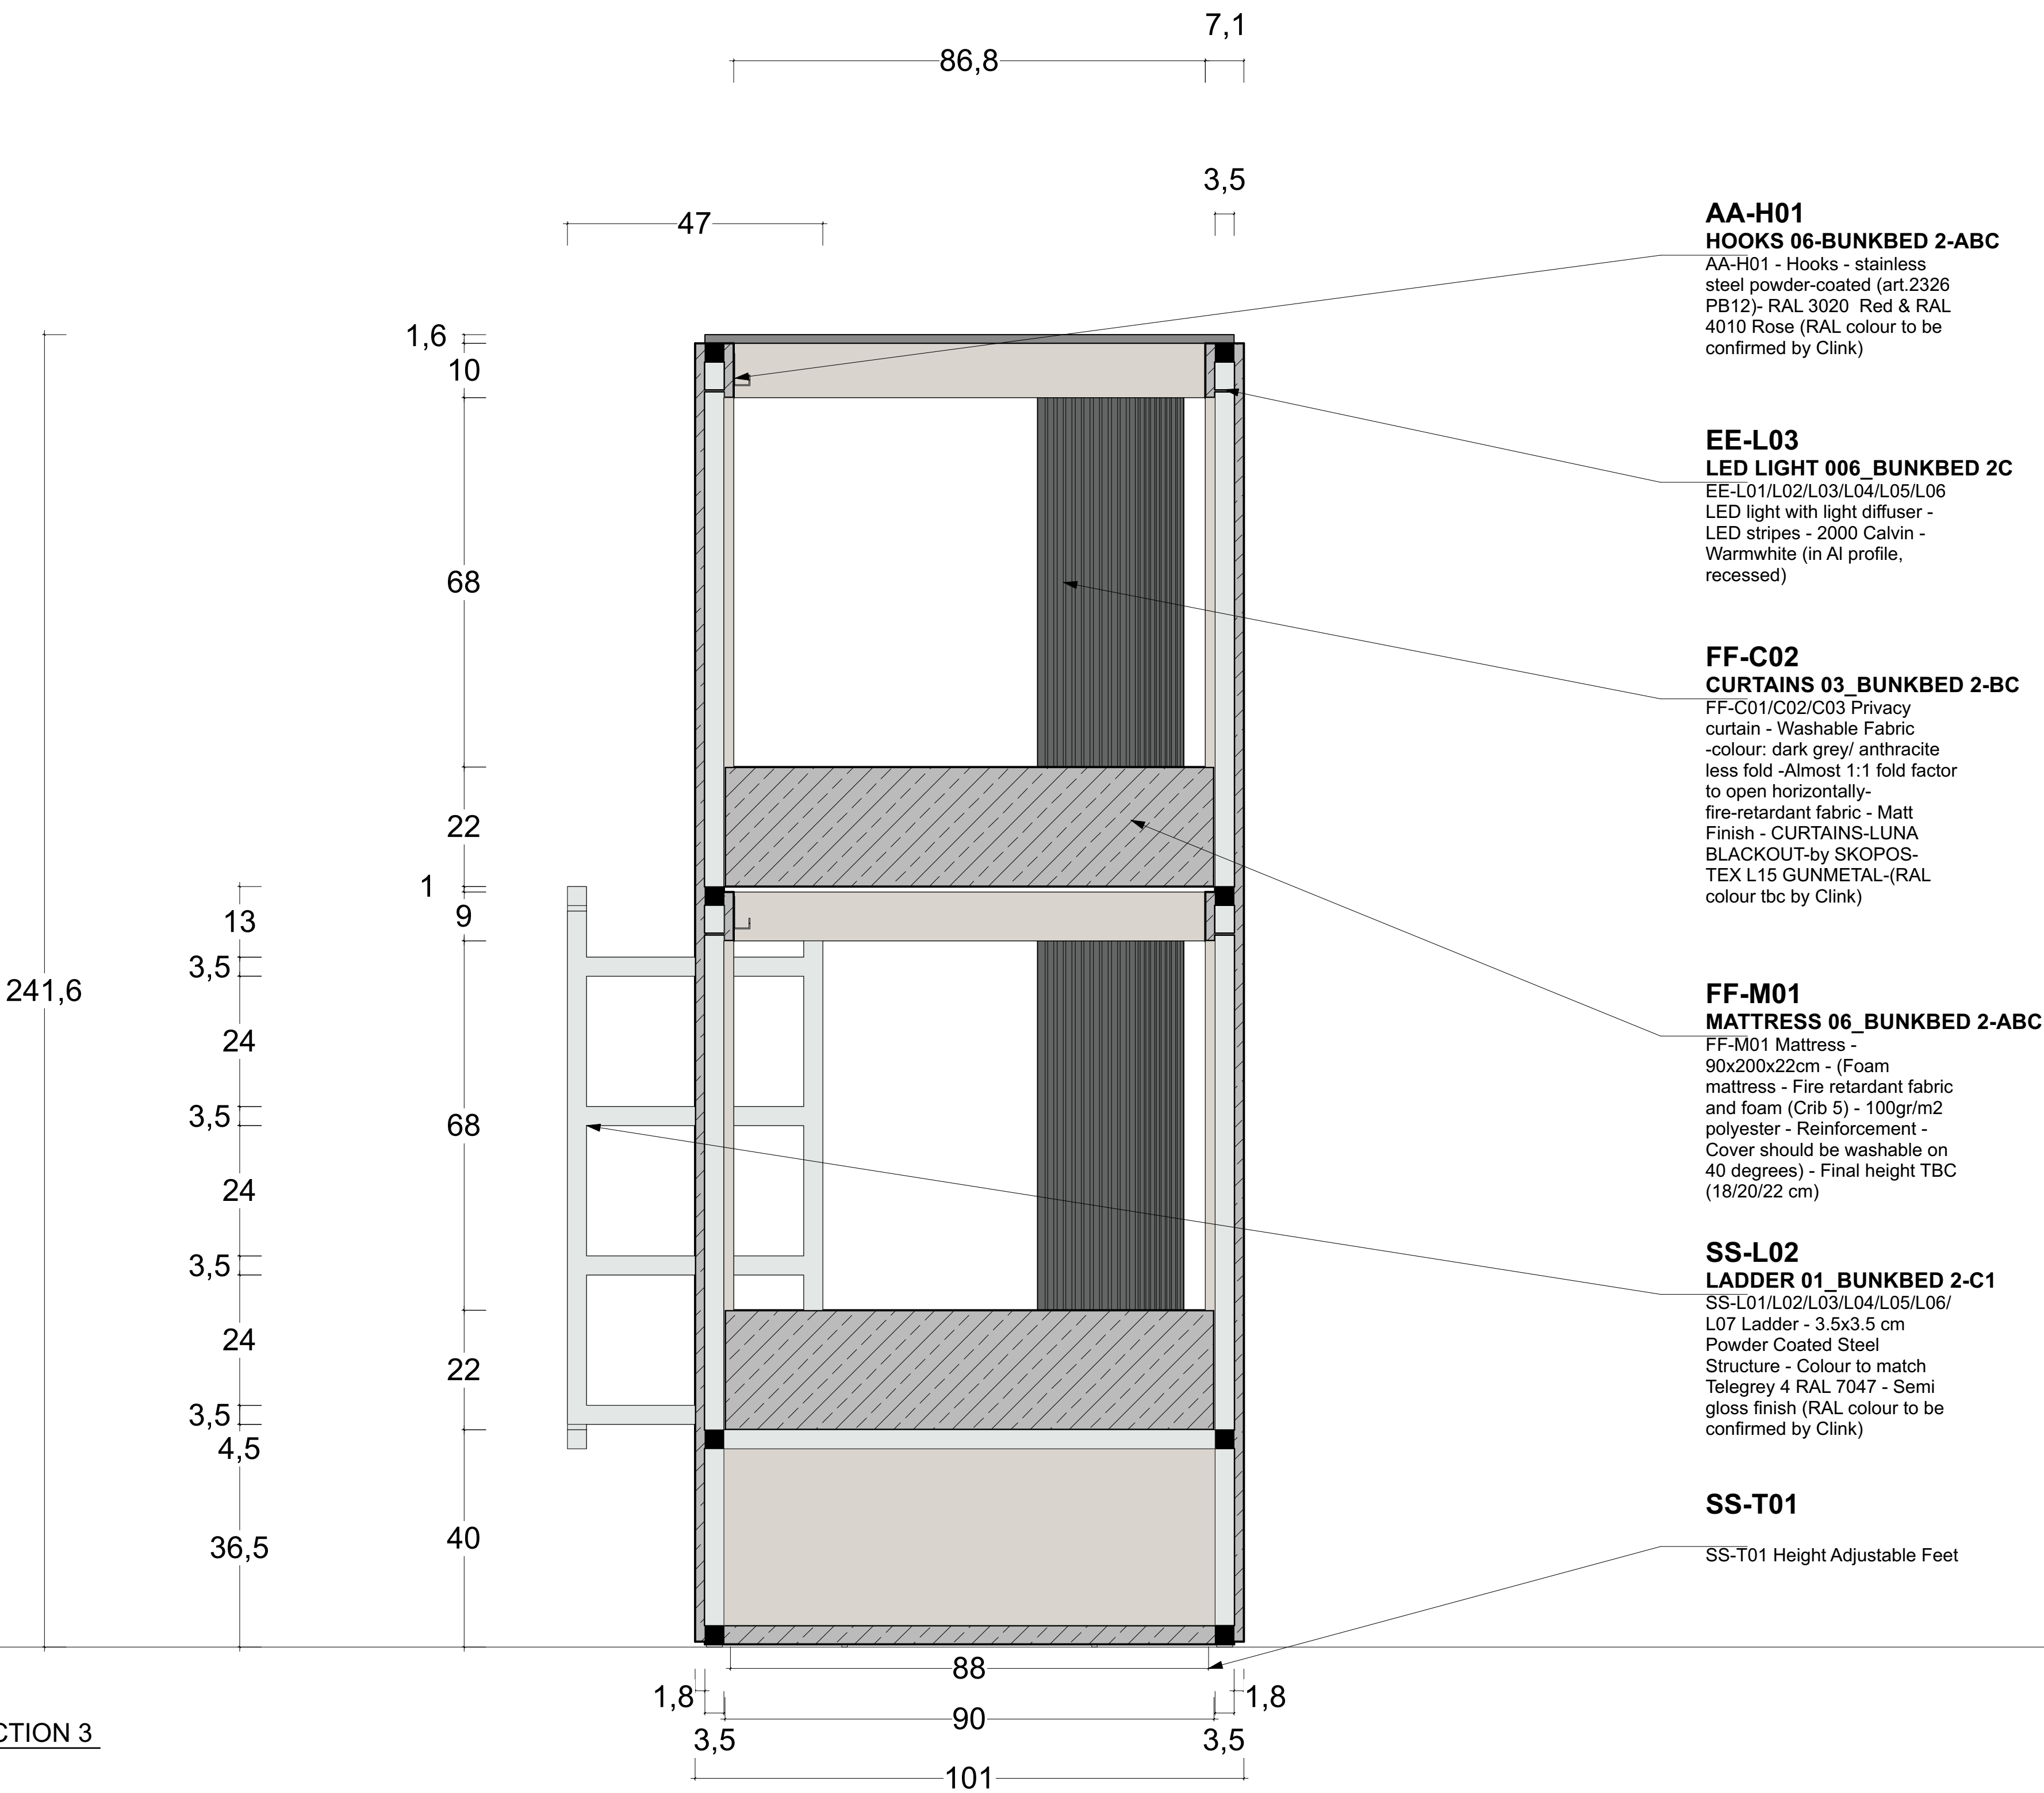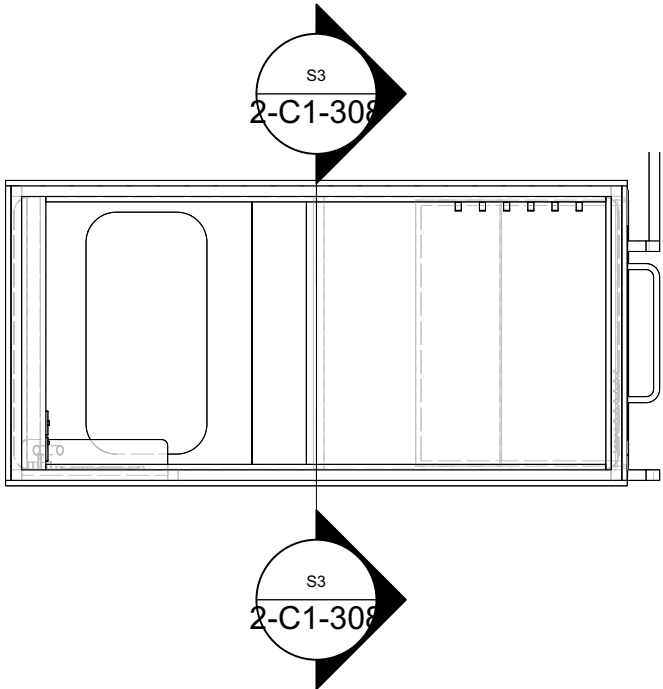

KEY

Index

A) 04.05.2026 Plan Set UP

All measurements have to be verified according to existing conditions by the contractor! Discrepancies must be reported immediately to the responsible project manager. The contractor has to produce fully dimensioned shop drawings prior to the start of the contract and they have to be approved by the client/ investor / interior designer

Project
CLINK 78 - BEDS





Project Address
CLINK 78
78 King's Cross Rd
London WC1X 9QG
United Kingdom

Client's Address
CLINK 78
78 King's Cross Rd
London WC1X 9QG
United Kingdom

Sheet Number	2-C1-308	Total Sheets	82
Sheet Title	BUNKBED 2-C1 SECTION 3	Level	
File Name			
260425_CLINK 78_BEDs AA DRAFT 03.vwx			

Date	Sheet Size	Scale	Signed
28.04.26	A1	1:8	AA

BUNKBEDS - TYPE 2-C1 - SECTION 4

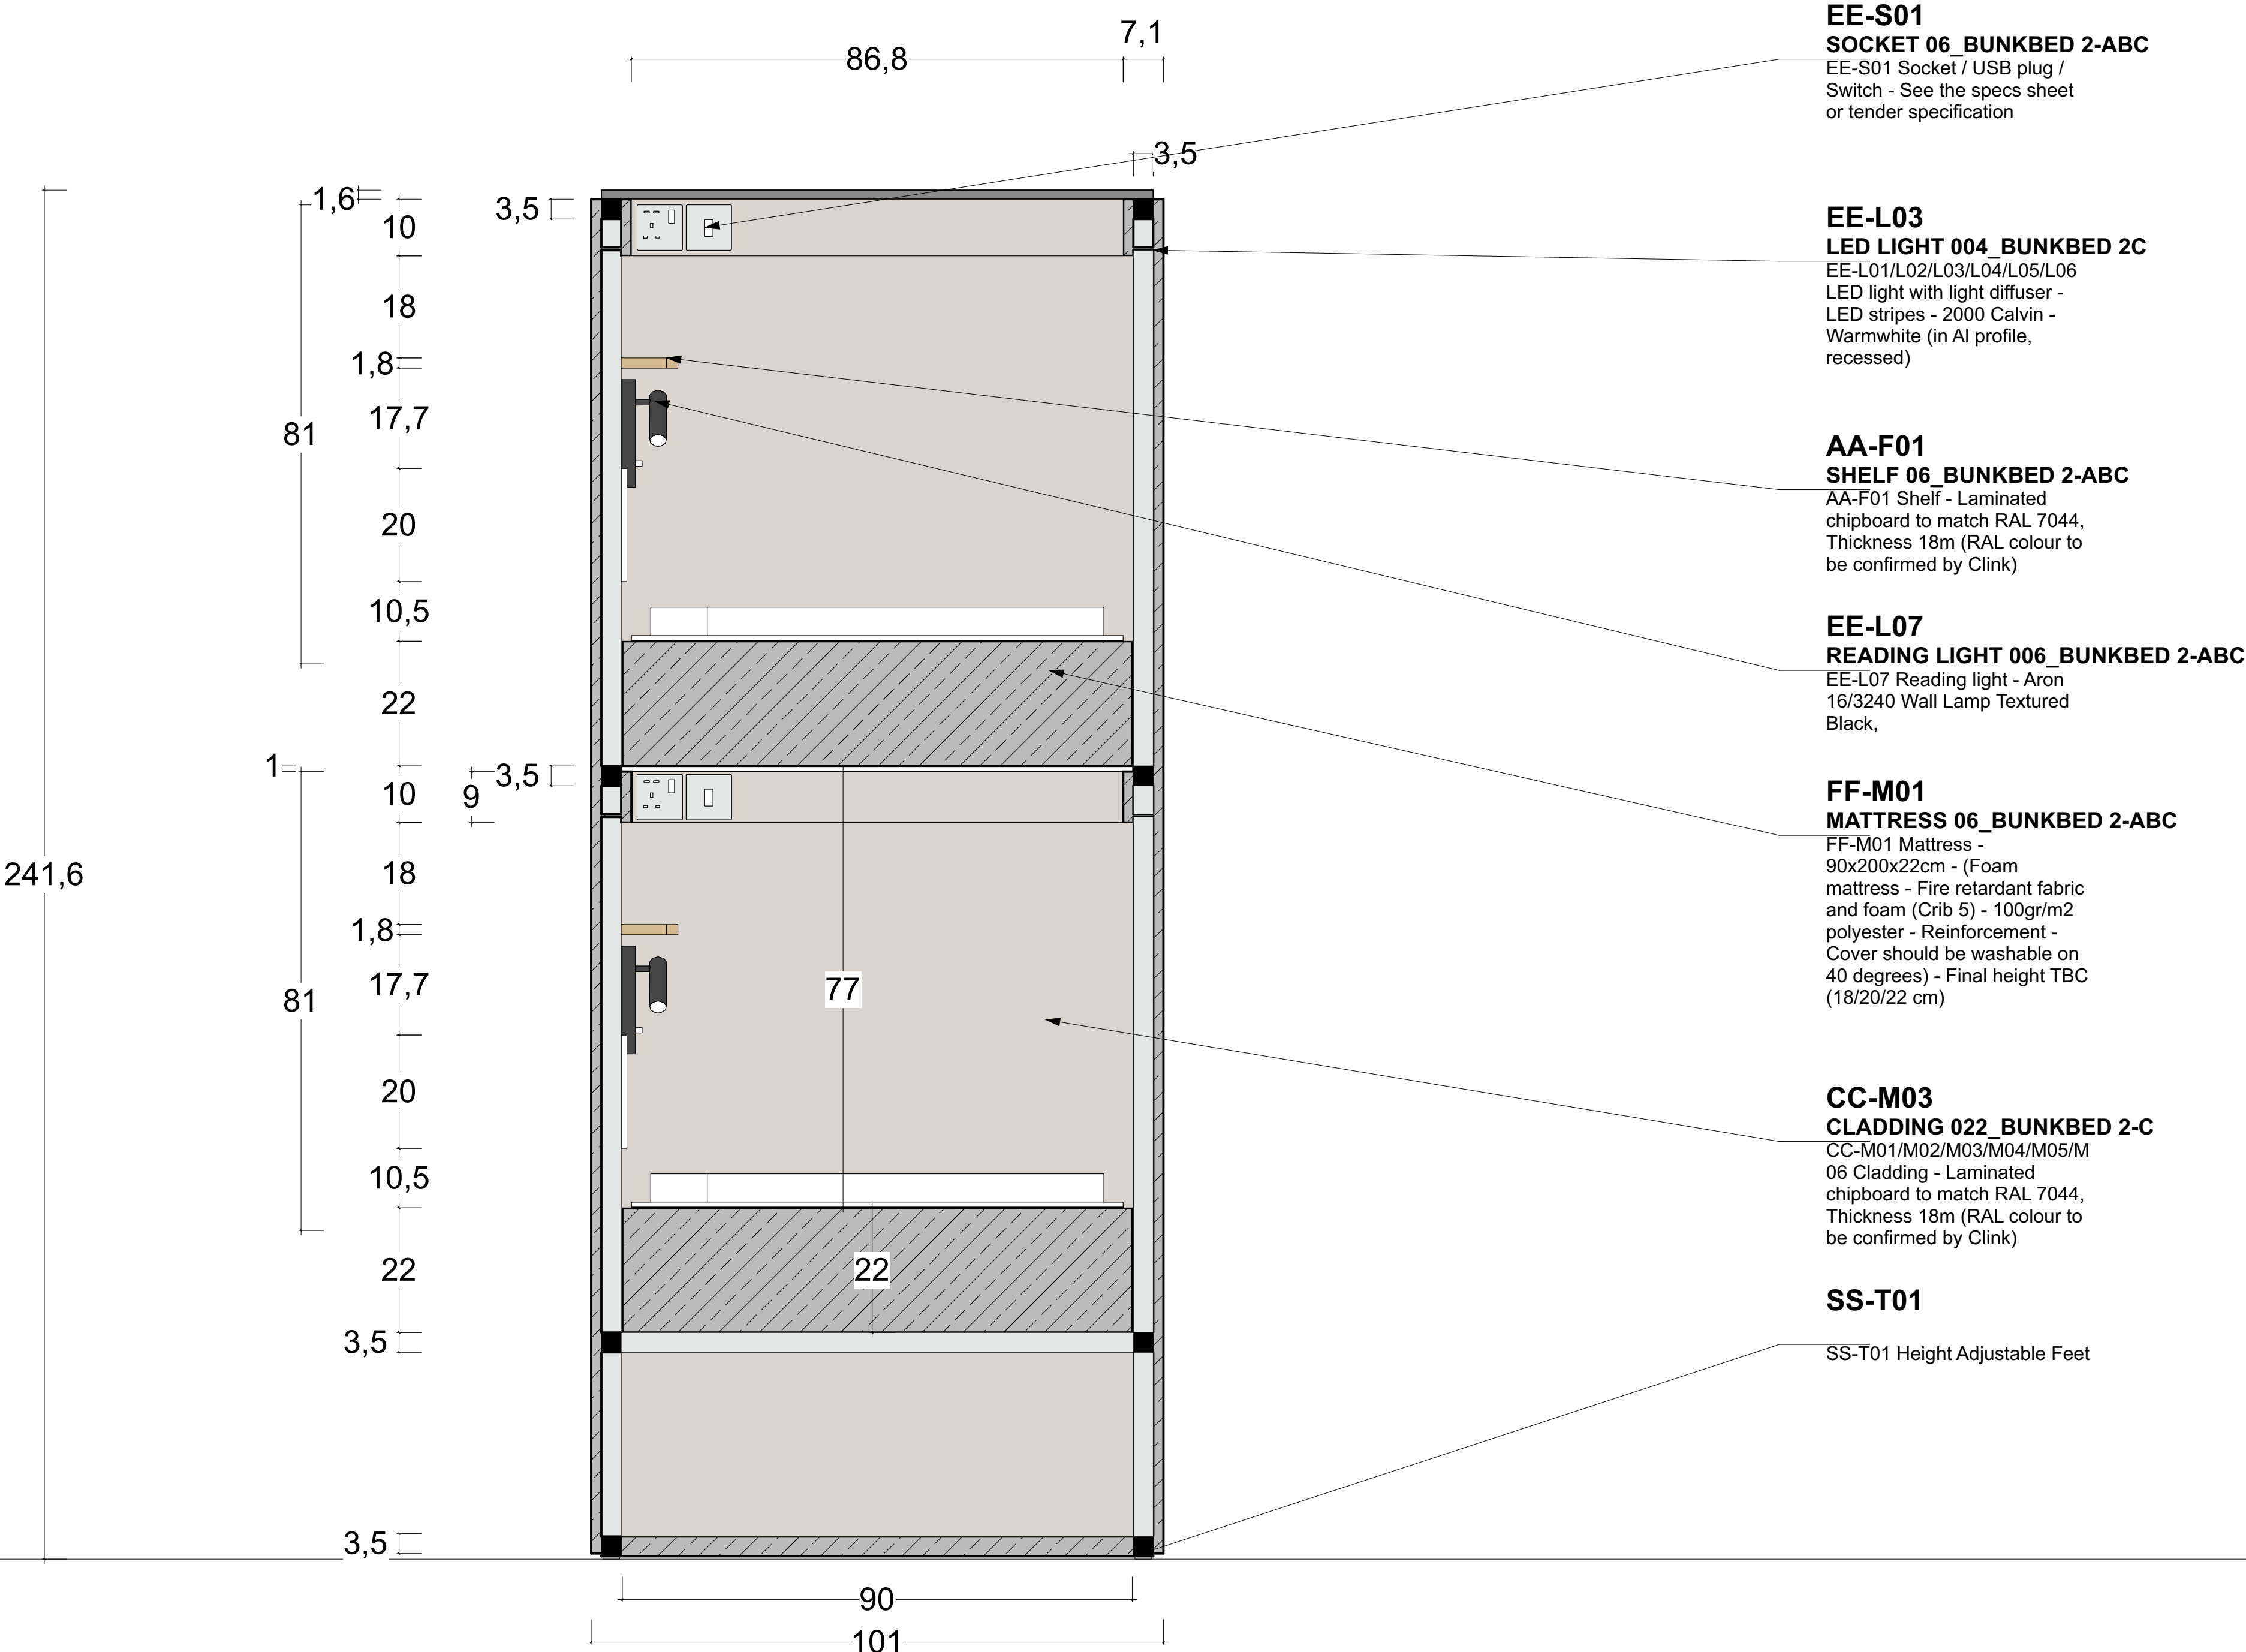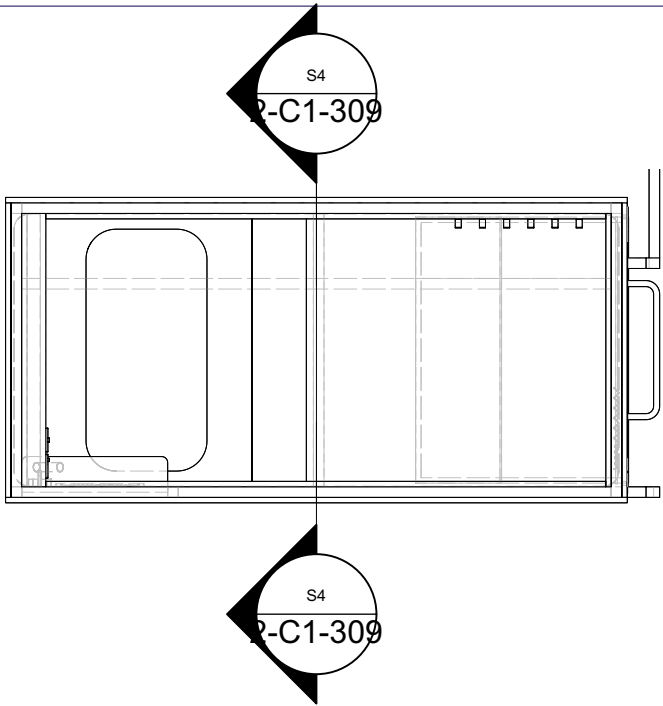

KEY

Index

A) 04.05.2026 Plan Set UP

All measurements have to be verified according to existing conditions by the contractor! Discrepancies must be reported immediately to the responsible project manager. The contractor has to produce fully dimensioned shop drawings prior to the start of the contract and they have to be approved by the client/ investor / interior designer

Project

CLINK 78 - BEDS

Logo



Project Address

CLINK 78
78 King's Cross Rd
London WC1X 9QG
United Kingdom


Client's Address

CLINK 78
78 King's Cross Rd
London WC1X 9QG
United Kingdom

Sheet Number 2-C1-309		Total Sheets 82
Sheet Title BUNKBED 2-C1 SECTION 4		Level
File Name 260425_CLINK 78_BEDs AA DRAFT 03.vwx		

Date	Sheet Size	Scale	Signed
28.04.26	A1	1:8	AA


Stefanie Jaensch INTERIOR DESIGNS
Global Headquarter | Stefanie Jaensch c/o WeWork
Taubusanlage 8 | 60329 Frankfurt a.M.
E-Mail info@stefaniejaensch.de | DE +49 (0) 174 6756098
www.stefaniejaensch.de
Legal address | Stefanie Jaensch | Offenbacher Landstraße 434 | 60599 Frankfurt a.M.
© 2023 All Rights Reserved | Stefanie Jaensch

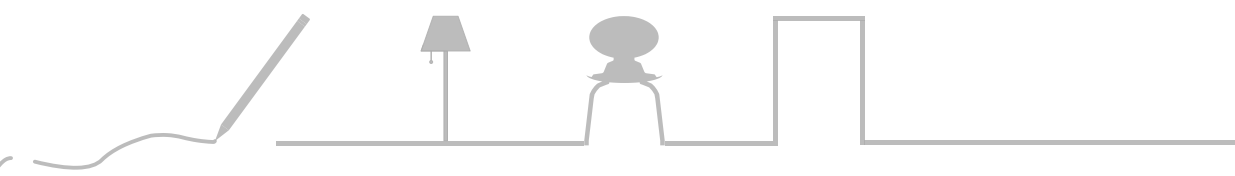

For



2-C2

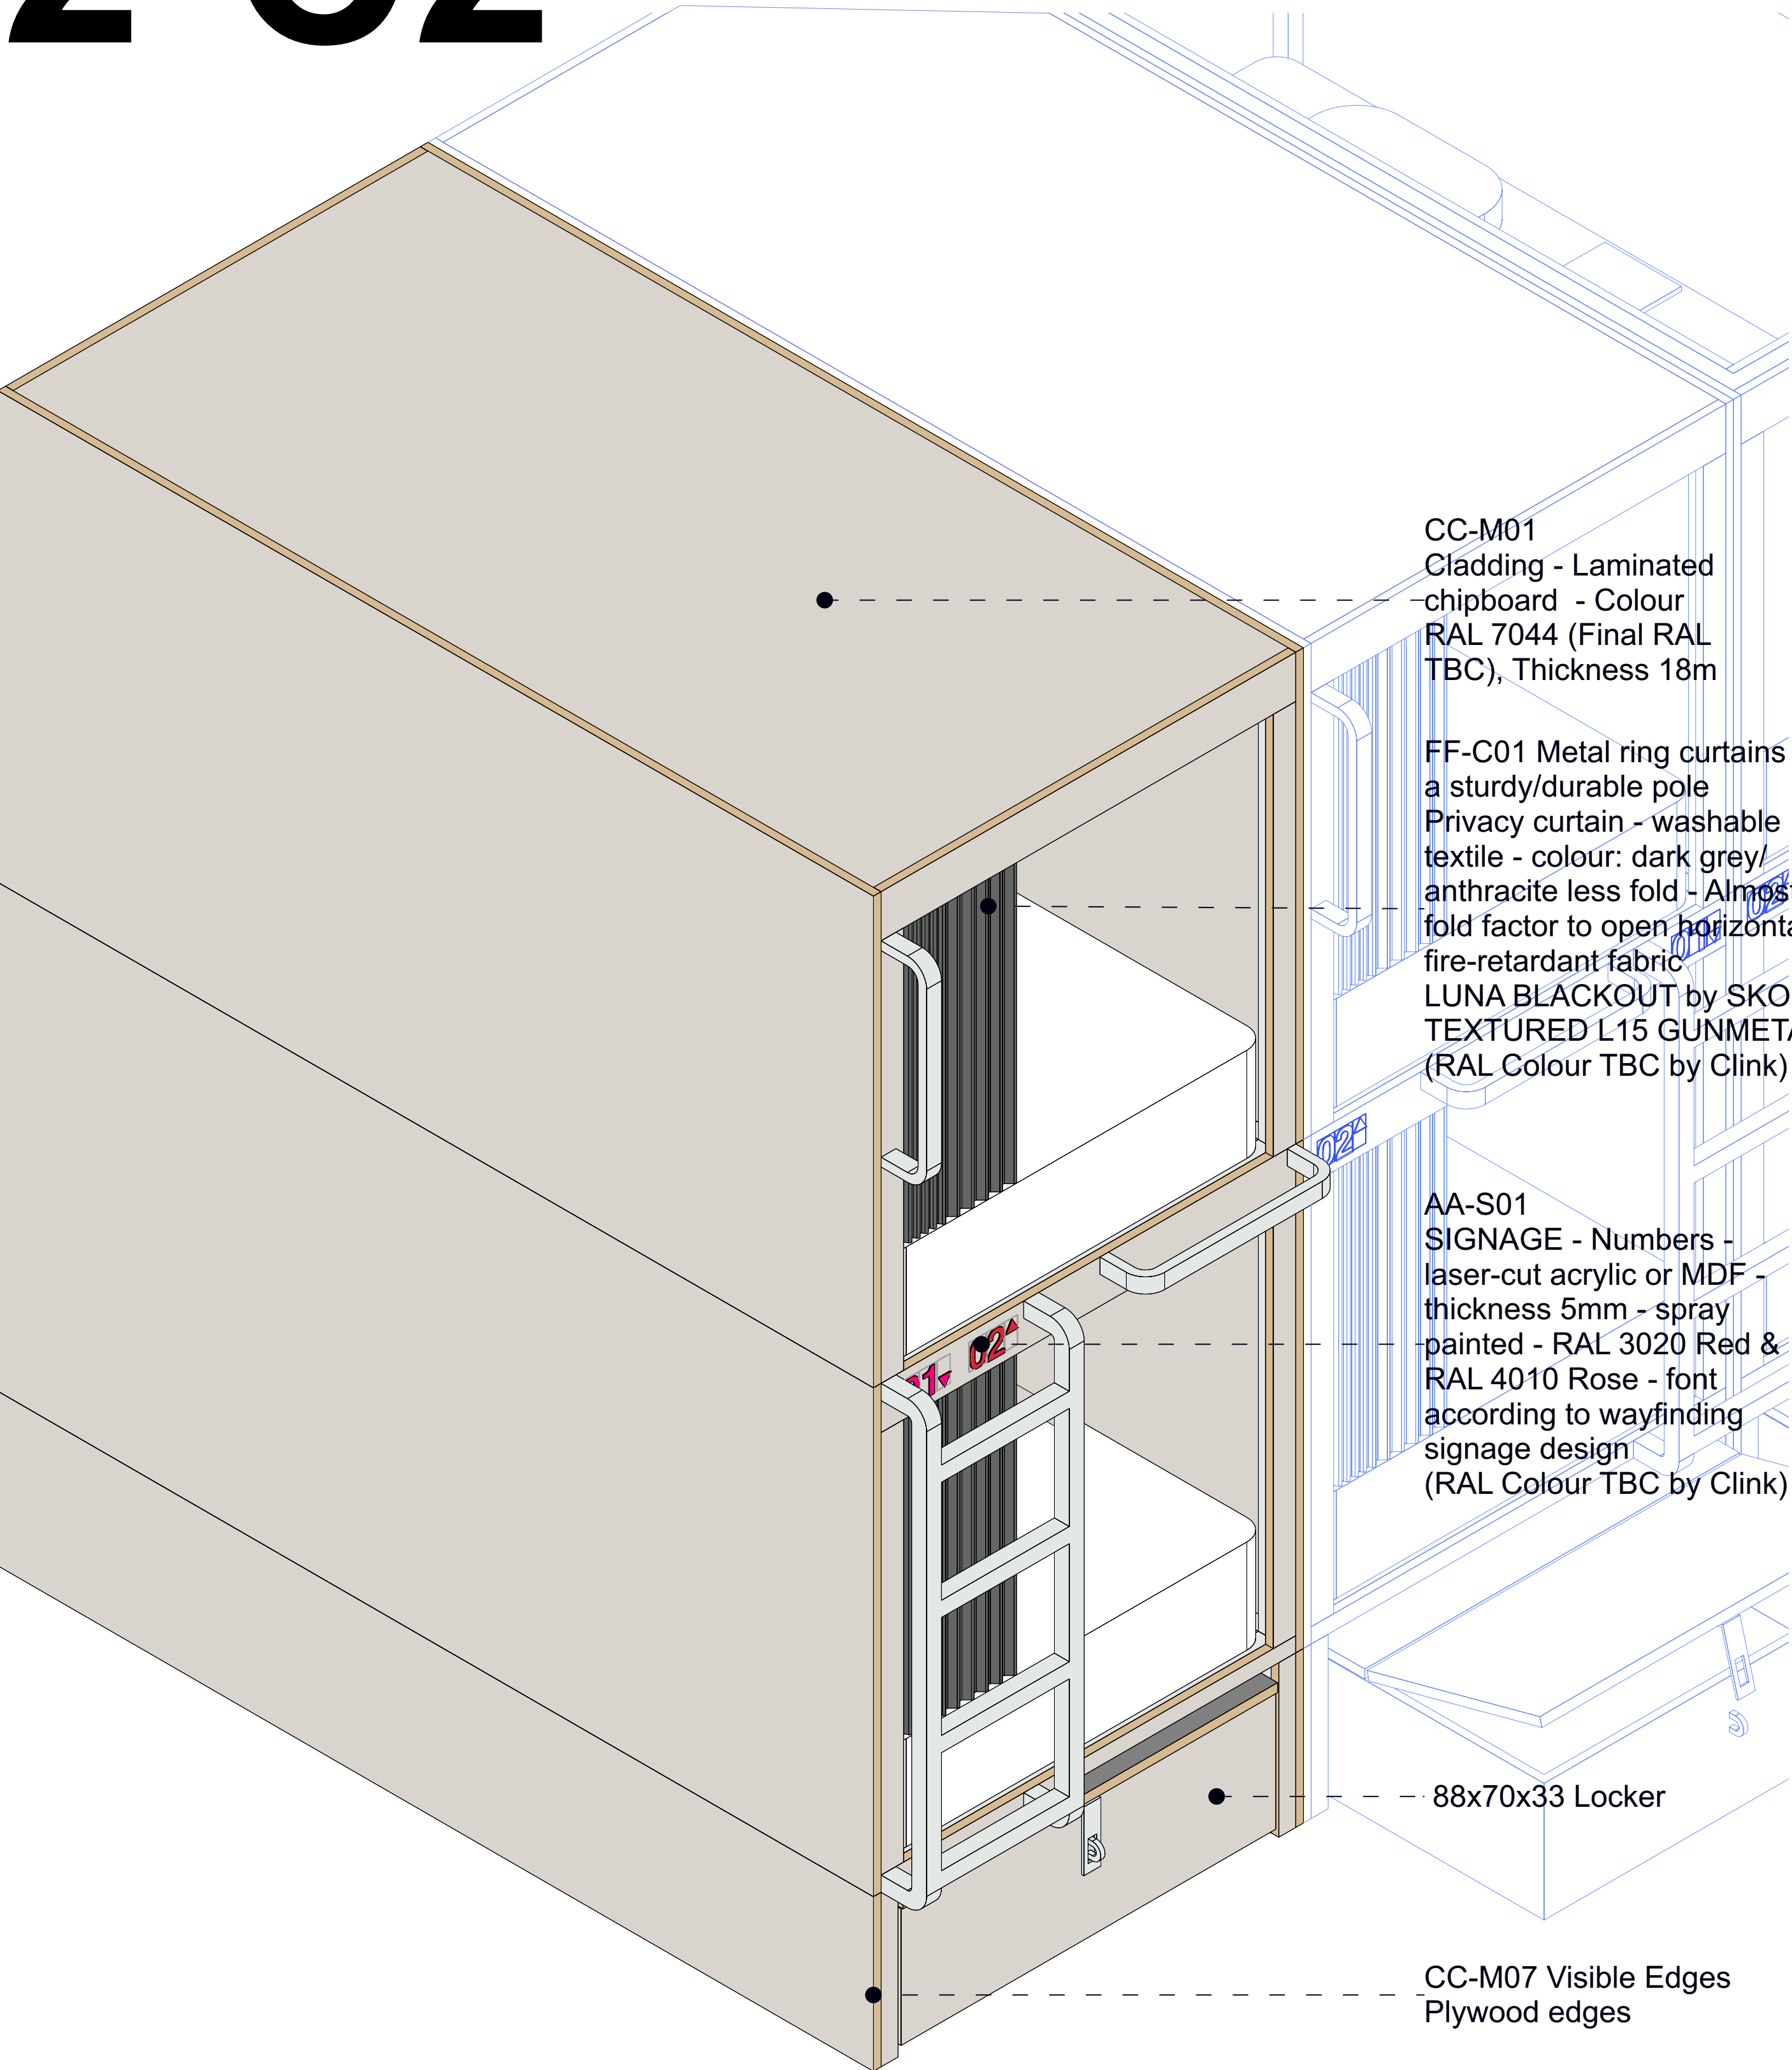


CC-M01
Cladding - Laminated
chipboard - Colour
RAL 7044 (Final RAL
TBC), Thickness 18m

FF-C01 Metal ring curtains with
a sturdy/durable pole
Privacy curtain - washable
textile - colour: dark grey/
anthracite less fold - Almost 1:1
fold factor to open horizontally -
fire-retardant fabric
LUNA BLACKOUT by SKOPOS
TEXTURED L15 GUNMETAL
(RAL Colour TBC by Clink)

AA-S01
SIGNAGE - Numbers -
laser-cut acrylic or MDF -
thickness 5mm - spray
painted - RAL 3020 Red &
RAL 4010 Rose - font
according to wayfinding
signage design
(RAL Colour TBC by Clink)

88x70x33 Locker

CC-M07 Visible Edges
Plywood edges

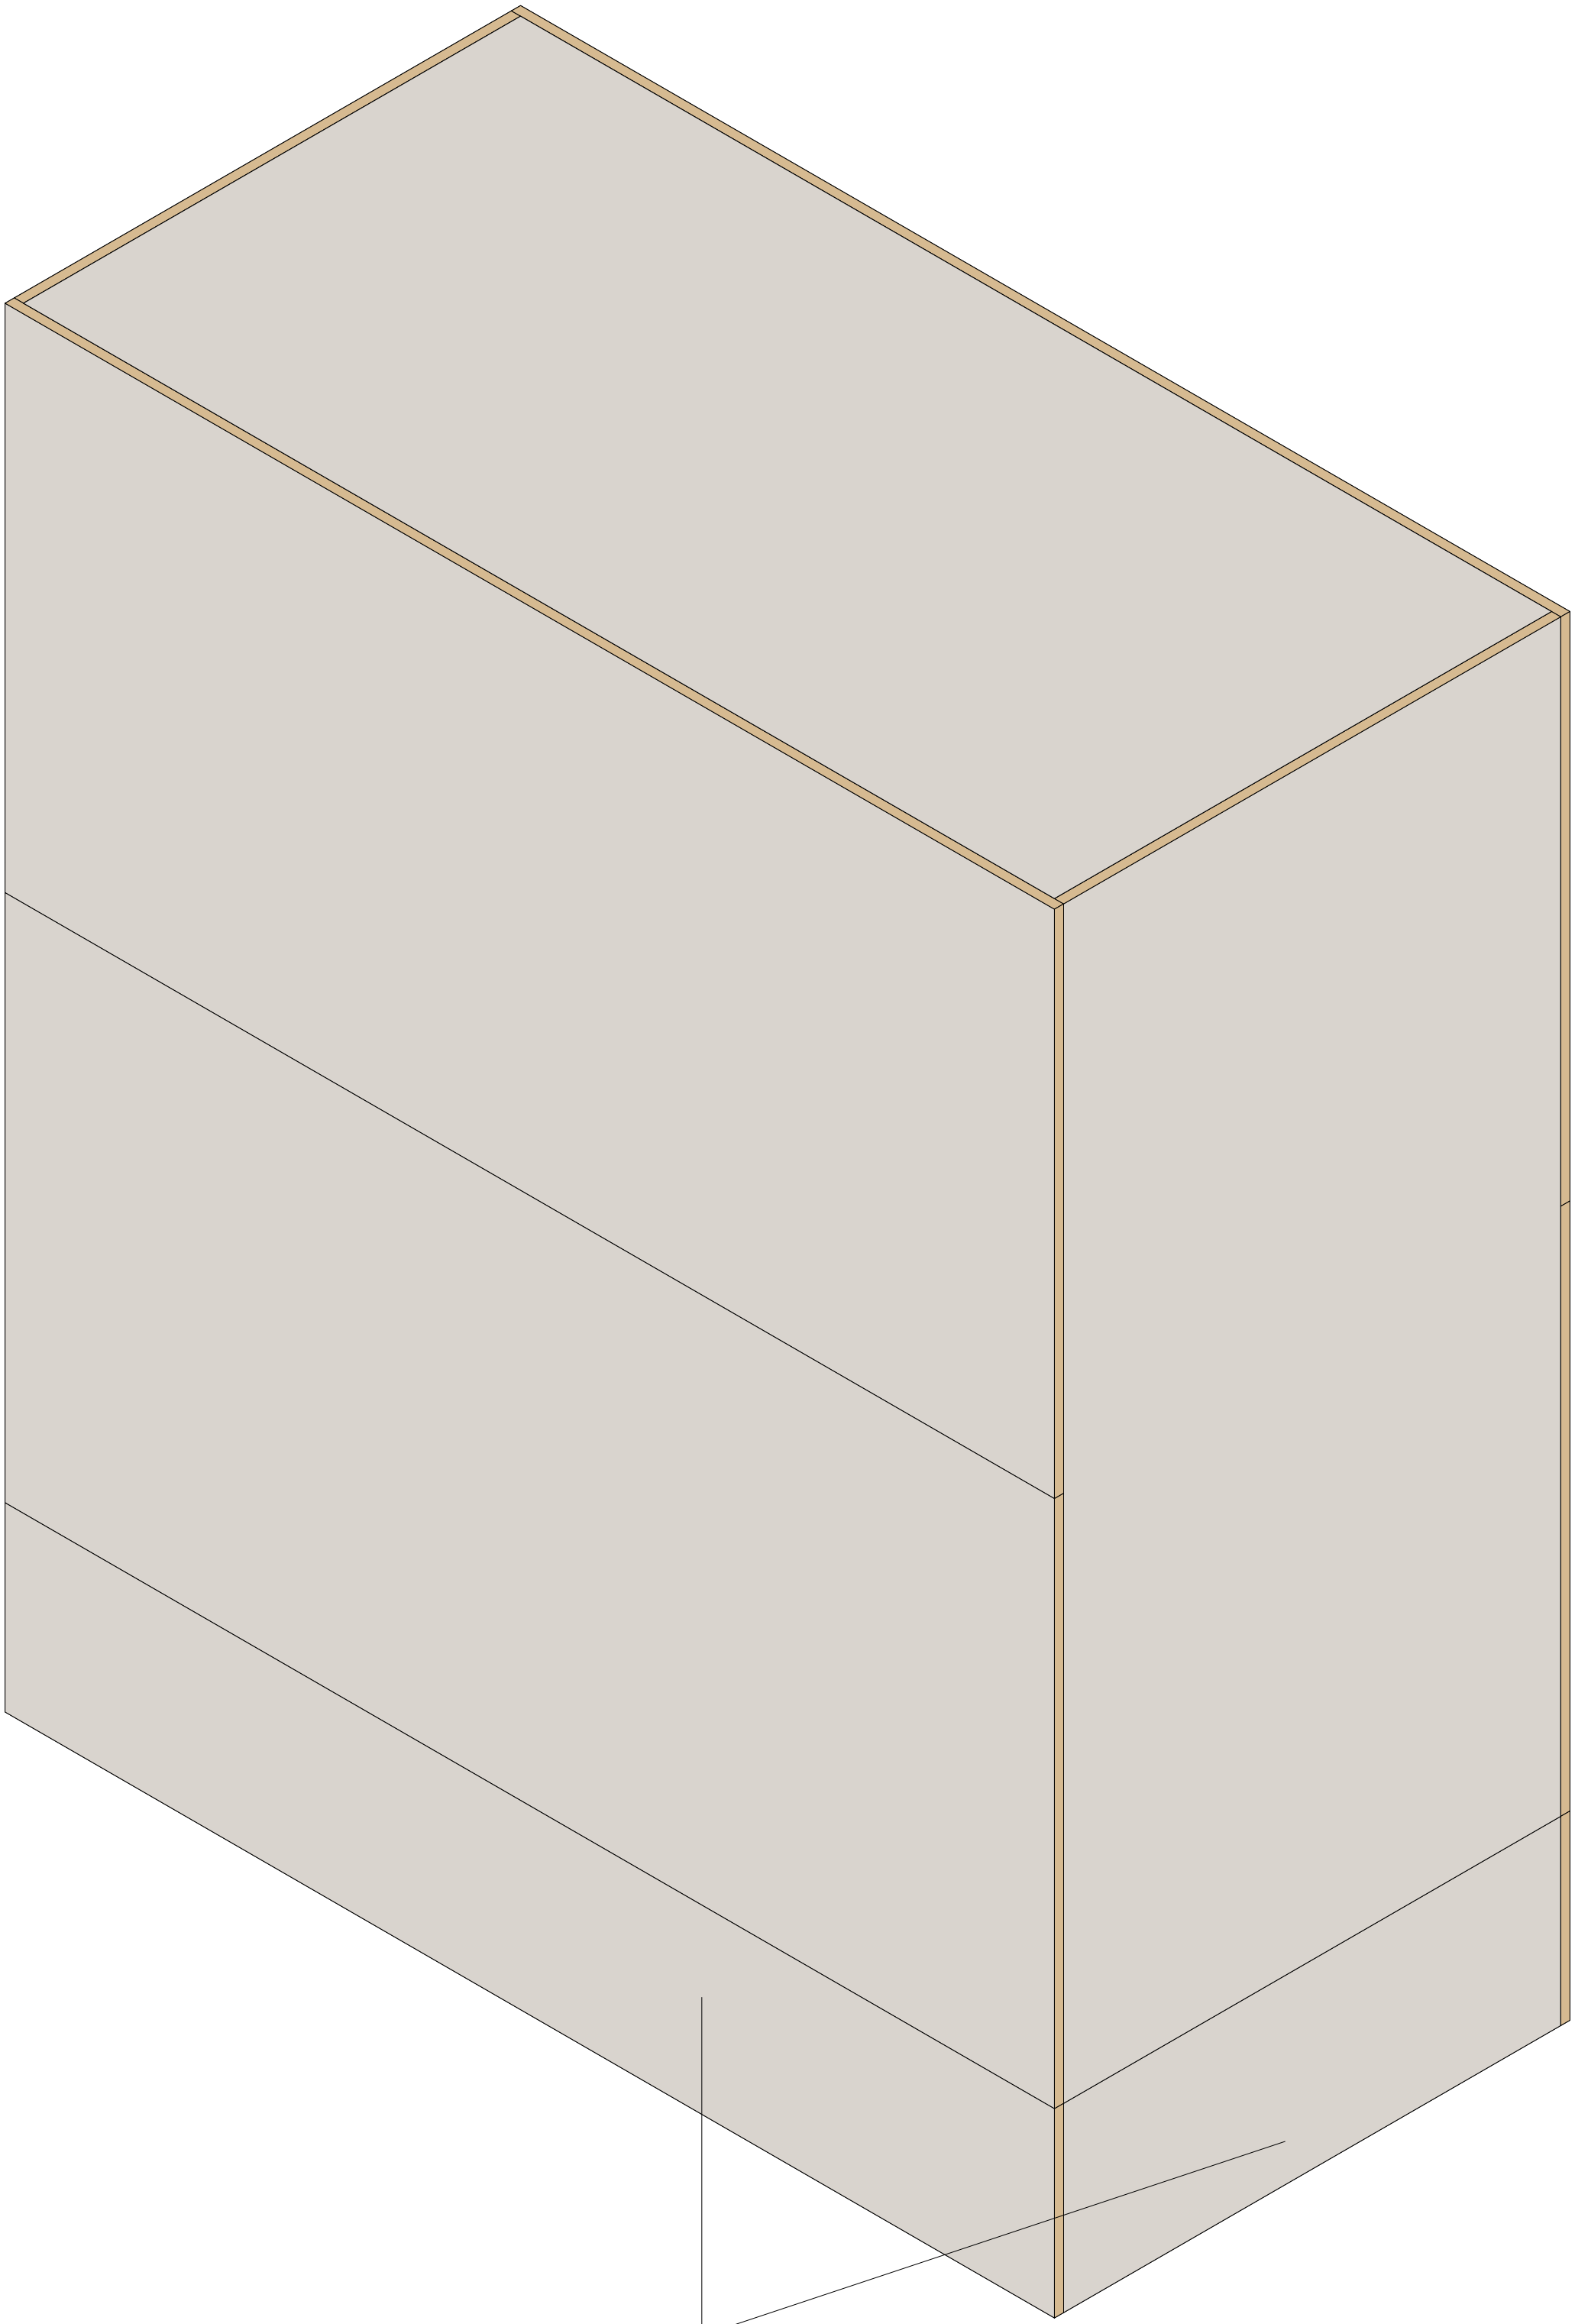


Lower side panels may be
removed to allow cable
connections.

DIMENSIONS

101 x 205.6 x 241.6 (WxLxH)cm

DRAFT

BUNKBEDS - TYPE 2-C2 - GA PLAN

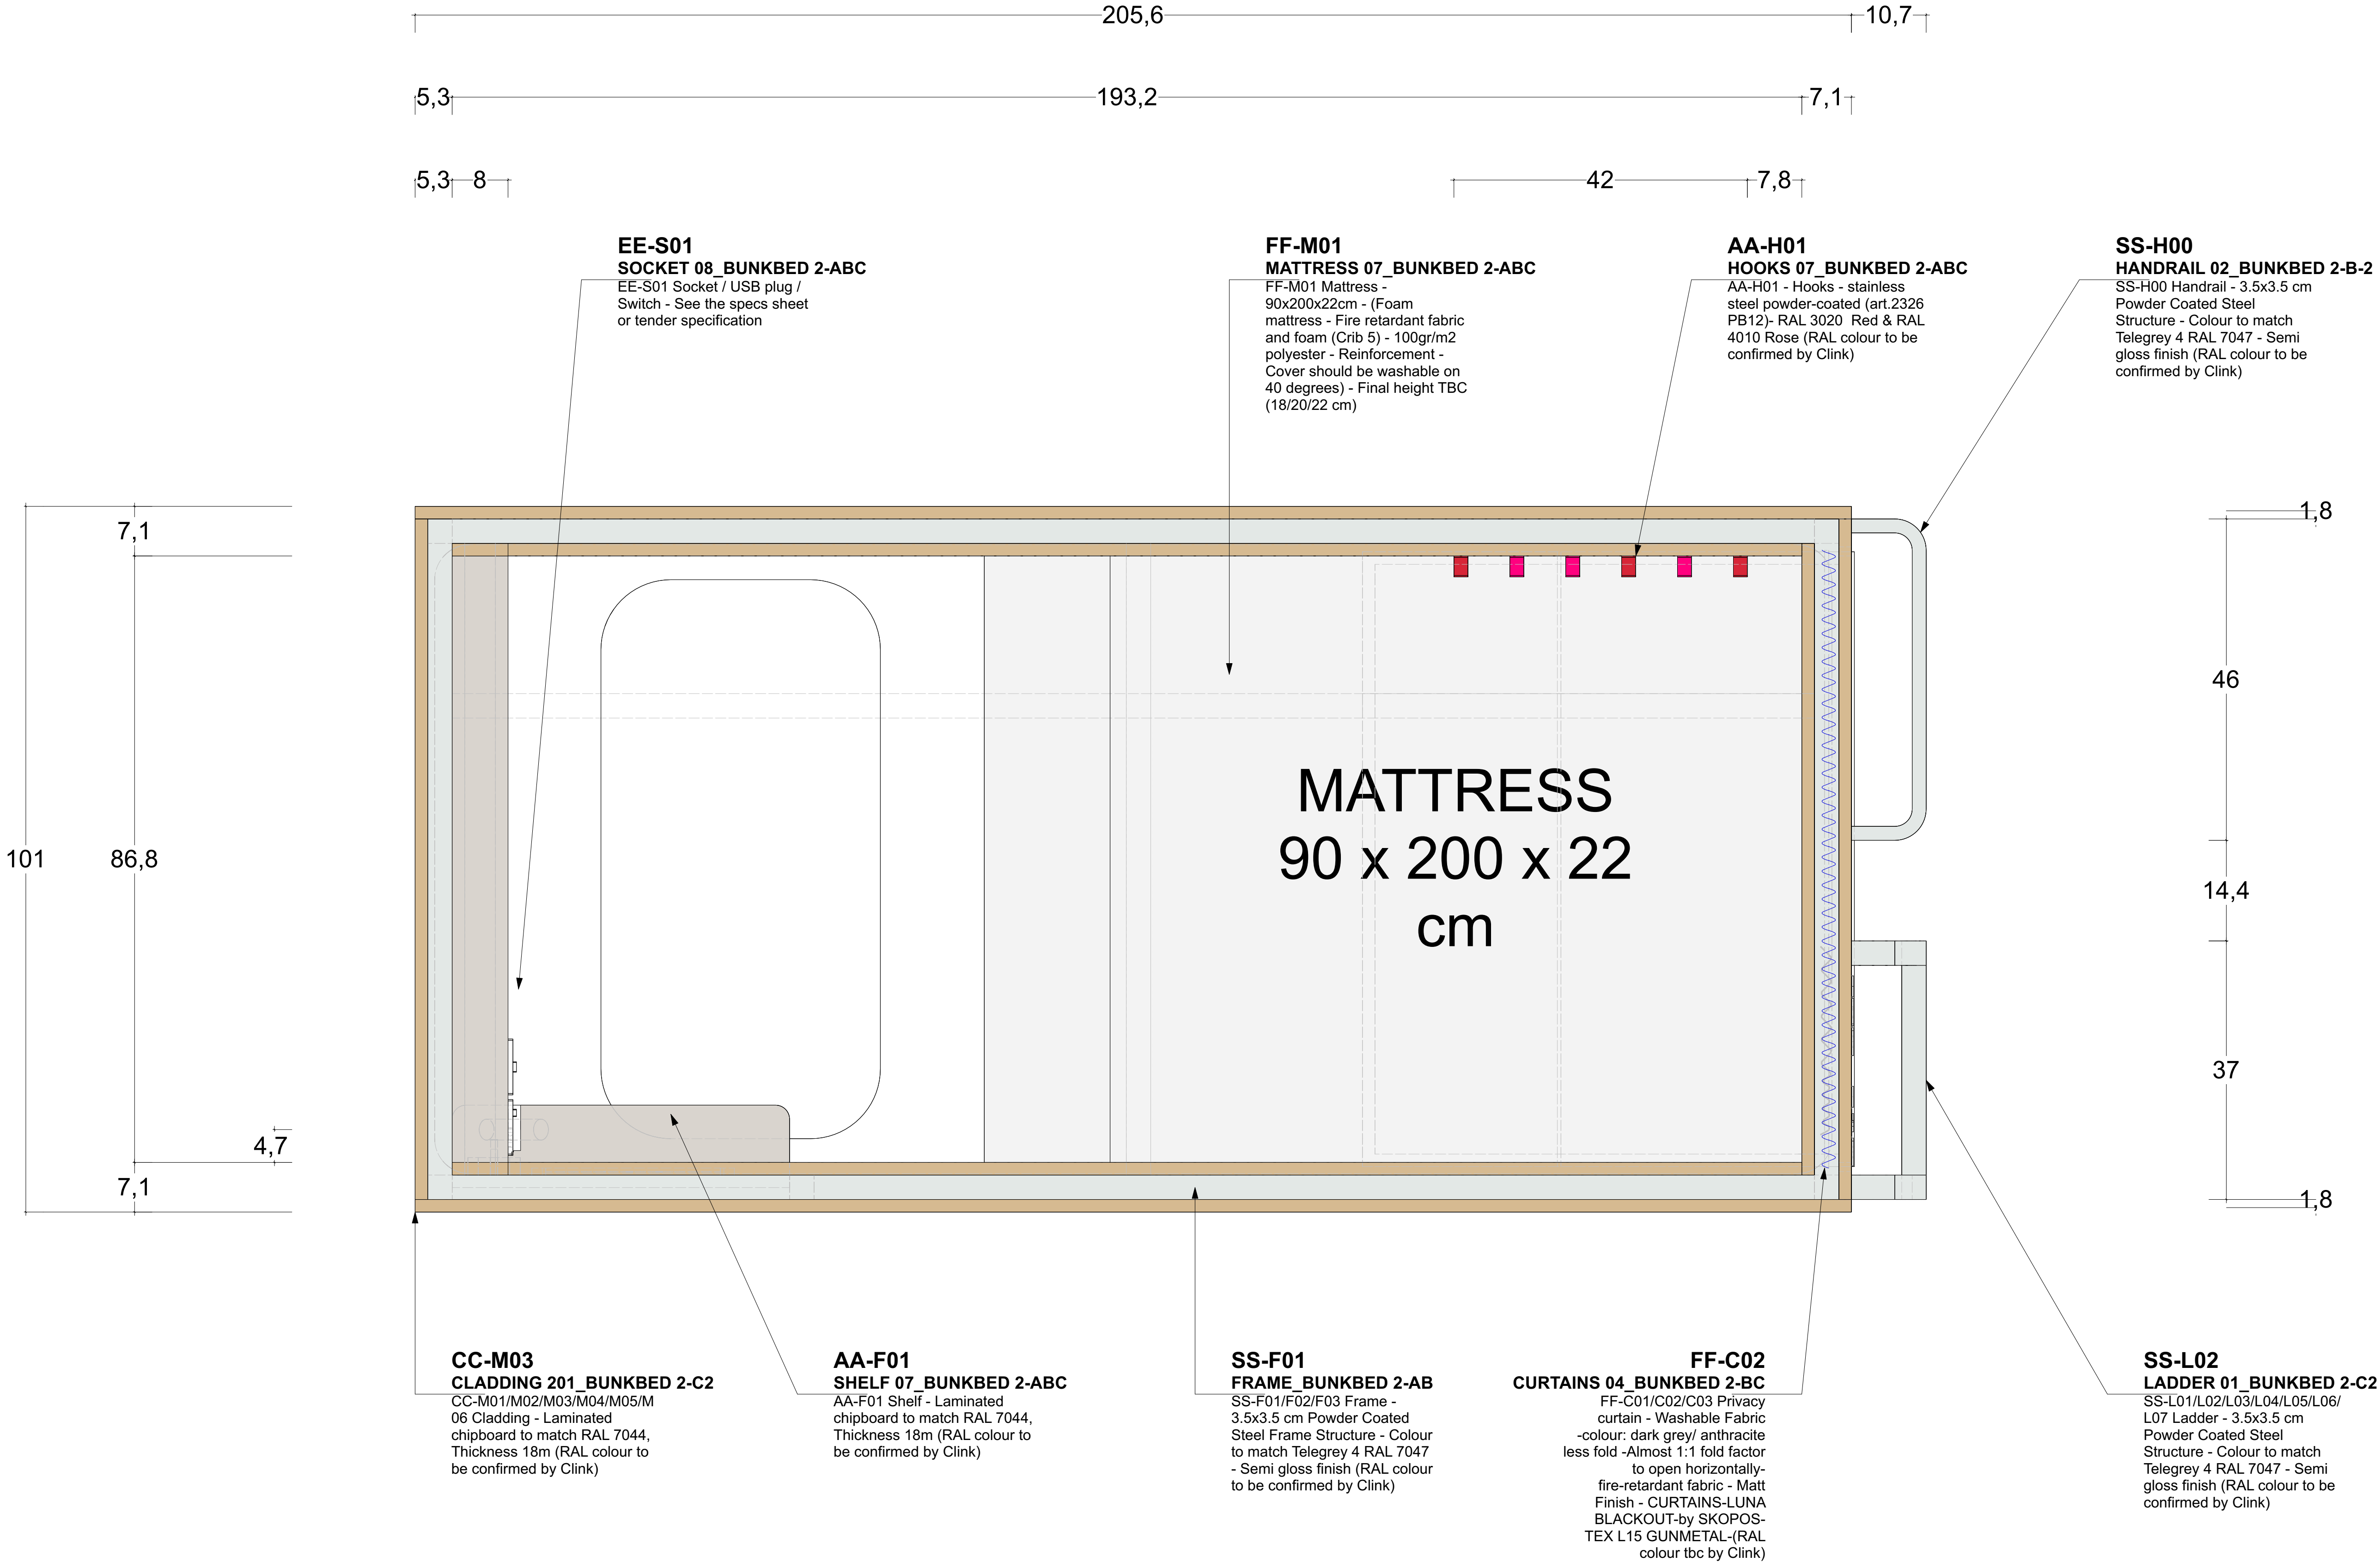

KEY

Index

A) 04.05.2026 Plan Set UP

All measurements have to be verified according to existing conditions by the contractor! Discrepancies must be reported immediately to the responsible project manager. The contractor has to produce fully dimensioned shop drawings prior to the start of the contract and they have to be approved by the client/ investor / interior designer

Project
CLINK 78 - BEDS

Logo
CLINK
HOSTELS

Project Address
CLINK 78
78 King's Cross Rd
London WC1X 9QG
United Kingdom


Client's Address
CLINK 78
78 King's Cross Rd
London WC1X 9QG
United Kingdom

Sheet Number	2-C2-401	Total Sheets	82
Sheet Title	BUNKBED 2-C2 GA	Level	
File Name 260425_CLINK 78_BEDs AA DRAFT 03.vwx			
Date	28.04.26	Sheet Size	A1
Scale	1:5	Signed	AA

Stefanie Jaensch **INTERIOR DESIGNS**

Global Headquarter | Stefanie Jaensch c/o WeWork
Taubusanlage 8 | 60329 Frankfurt a.M.
E-Mail info@stefaniejaensch.de | DE +49 (0) 174 6756098
www.stefaniejaensch.de
Legal address | Stefanie Jaensch | Offenbacher Landstraße 434 | 60599 Frankfurt a.M.
© 2023 All Rights Reserved | Stefanie Jaensch

BUNKBEDS - TYPE 2-C2 - FRONT ELEVATION

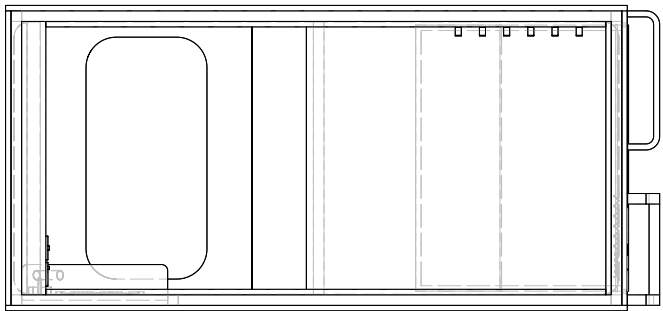

E1
2-C2-402



KEY

Index

A) 04.05.2026 Plan Set UP

All measurements have to be verified according to existing conditions by the contractor! Discrepancies must be reported immediately to the responsible project manager. The contractor has to produce fully dimensioned shop drawings prior to the start of the contract and they have to be approved by the client/ investor / interior designer

Project

CLINK 78 - BEDS

Logo



Project Address

CLINK 78
78 King's Cross Rd
London WC1X 9QG
United Kingdom

Client's Address

CLINK 78
78 King's Cross Rd
London WC1X 9QG
United Kingdom


Sheet Number	2-C2-402	Total Sheets	82
Sheet Title	BUNKBED 2-C2 FRONT ELEVATION	Level	
File Name			
260425_CLINK 78_BEDs AA DRAFT 03.vwx			

Date	Sheet Size	Scale	Signed
28.04.26	A1	1:8	AA

Stefanie Jaensch INTERIOR DESIGNS

Global Headquarter | Stefanie Jaensch c/o WeWork
Taubusanlage 8 | 60329 Frankfurt a.M.
E-Mail info@stefaniejaensch.de | DE +49 (0) 174 6756098
www.stefaniejaensch.de

Legal address | Stefanie Jaensch | Offenbacher Landstraße 434 | 60599 Frankfurt a.M.
© 2023 All Rights Reserved | Stefanie Jaensch

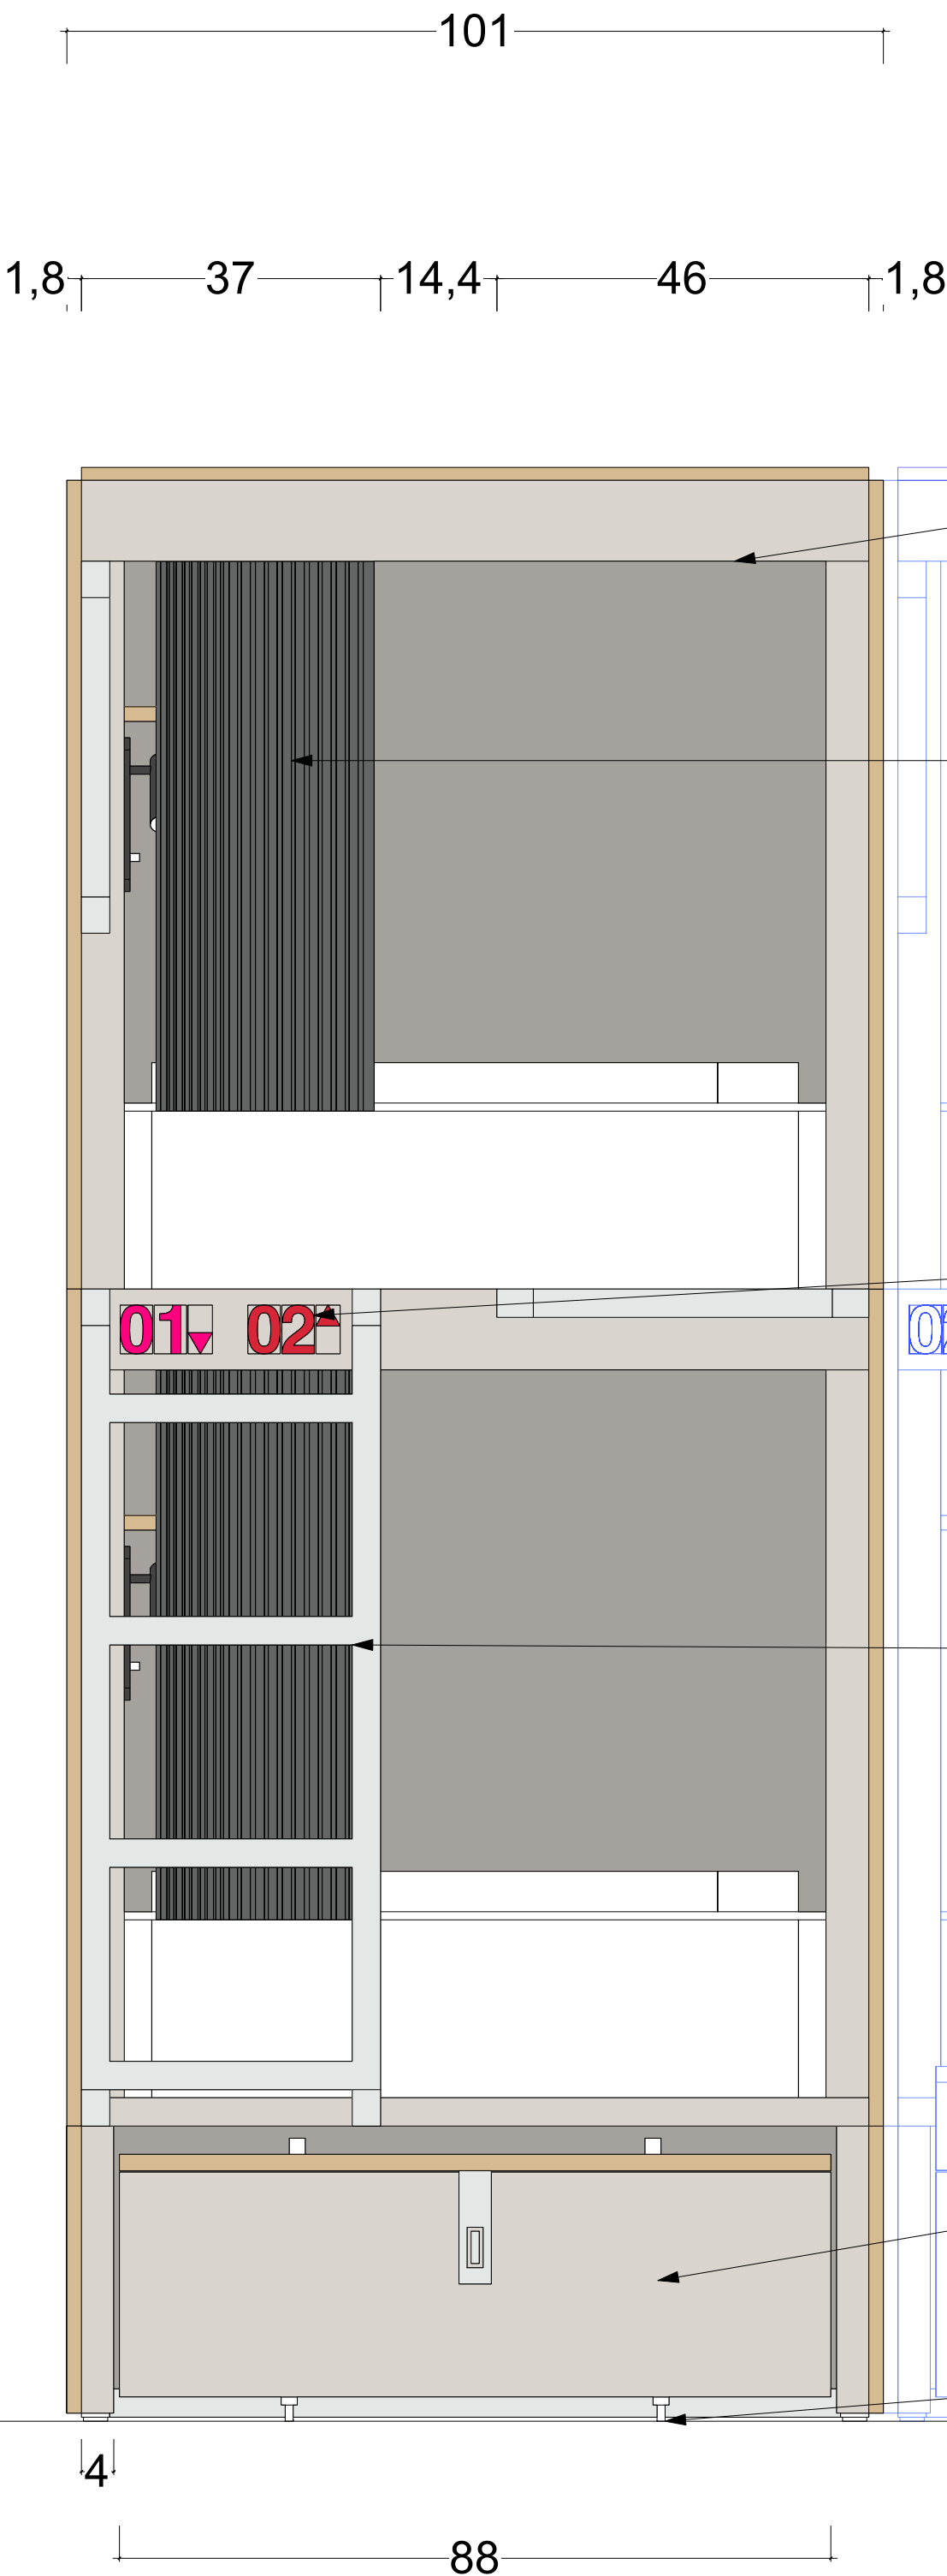

CC-M04
CLADDING 220_BUNKBED 2-C
CC-M01/M02/M03/M04/M05/M06 Cladding - Laminated chipboard to match RAL 7044, Thickness 18mm (RAL colour to be confirmed by Clink)

FF-C02
CURTAINS 05_BUNKBED 2-BC
FF-C01/C02/C03 Privacy curtain - Washable Fabric -colour: dark grey/ anthracite less fold -Almost 1:1 fold factor to open horizontally- fire-retardant fabric - Matt Finish - CURTAINS-LUNA BLACKOUT-by SKOPOS-TEX L15 GUNMETAL-(RAL colour tbc by Clink)


AA-S01
SIGNAGE 08_BUNKBED 2-ABC
AA-S01 SIGNAGE - Numbers - laser-cut acrylic or MDF - thickness 5mm - spray painted - RAL 3020 Red & RAL 4010 Rose - font according to wayfinding signage design (RAL colour to be confirmed by Clink)

SS-L02
LADDER 01_BUNKBED 2-C2
SS-L01/L02/L03/L04/L05/L06/L07 Ladder - 3.5x3.5 cm Powder Coated Steel Structure - Colour to match Telegrey 4 RAL 7047 - Semi gloss finish (RAL colour to be confirmed by Clink)

CC-L01
CLADDING 001_LOCKER 2-C2
CC-L01 LOCKER - Panels - Laminated chipboard to match RAL 7044, Thickness 18mm (RAL colour to be confirmed by Clink)

SS-T01
SS-T01 Height Adjustable Feet

BUNKBEDS - TYPE 2-C2 - BACK ELEVATION

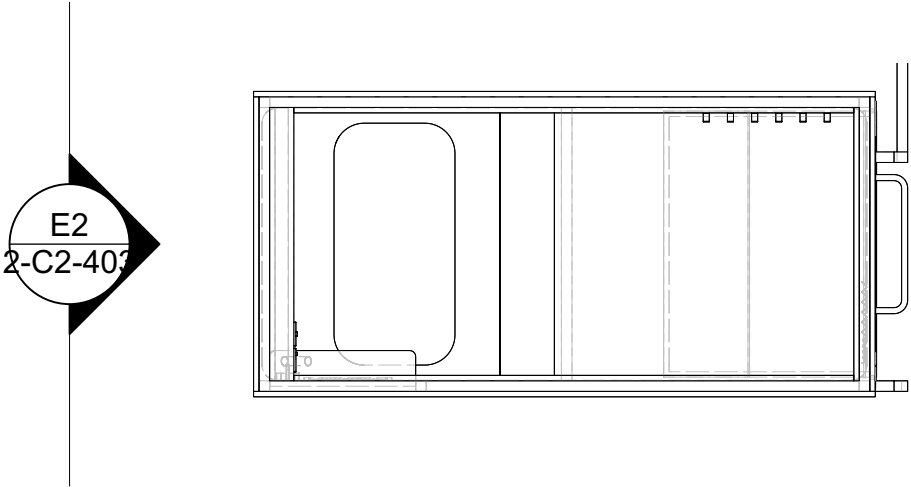

CC-M03
CLADDING 207_BUNKBED 2-C2
CC-M01/M02/M03/M04/M05/M06 Cladding - Laminated chipboard to match RAL 7044, Thickness 18m (RAL colour to be confirmed by Clink)

CC-M07
CC-M07 Visible Edge Band - Plywood edges

SS-T01
SS-T01 Height Adjustable Feet



KEY

Index
A) 04.05.2026 Plan Set UP

All measurements have to be verified according to existing conditions by the contractor! Discrepancies must be reported immediately to the responsible project manager. The contractor has to produce fully dimensioned shop drawings prior to the start of the contract and they have to be approved by the client/ investor / interior designer

Project
CLINK 78 - BEDS



Project Address
CLINK 78
78 King's Cross Rd
London WC1X 9QG
United Kingdom



Client's Address
CLINK 78
78 King's Cross Rd
London WC1X 9QG
United Kingdom

Sheet Number 2-C2-403		Total Sheets 82
Sheet Title BUNKBED 2-C2 BACK ELEVATION		Level
File Name 260425_CLINK 78_BEDs AA DRAFT 03.vwx		

Date	Sheet Size	Scale	Signed
28.04.26	A1	1:8	AA

Stefanie Jaensch INTERIOR DESIGNS
Global Headquarter | Stefanie Jaensch c/o WeWork
Taubusanlage 8 | 60329 Frankfurt a.M.
E-Mail info@stefaniejaensch.de | DE +49 (0) 174 6756098
www.stefaniejaensch.de
Legal address | Stefanie Jaensch | Offenbacher Landstraße 434 | 60599 Frankfurt a.M.
© 2023 All Rights Reserved | Stefanie Jaensch

BUNKBEDS - TYPE 2-C2 - RIGHT ELEVATION

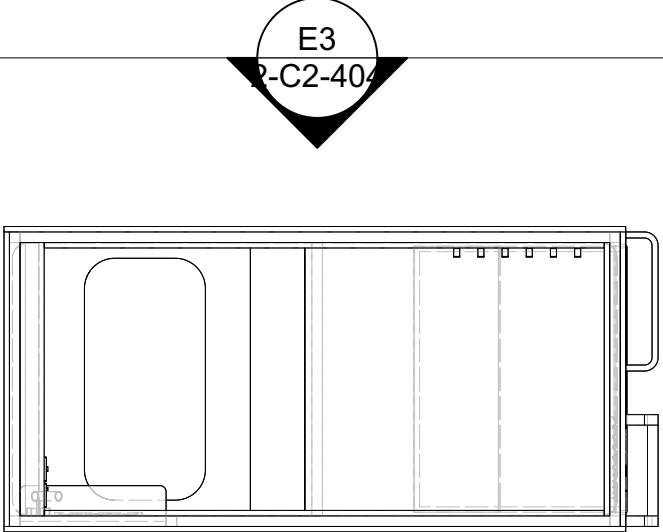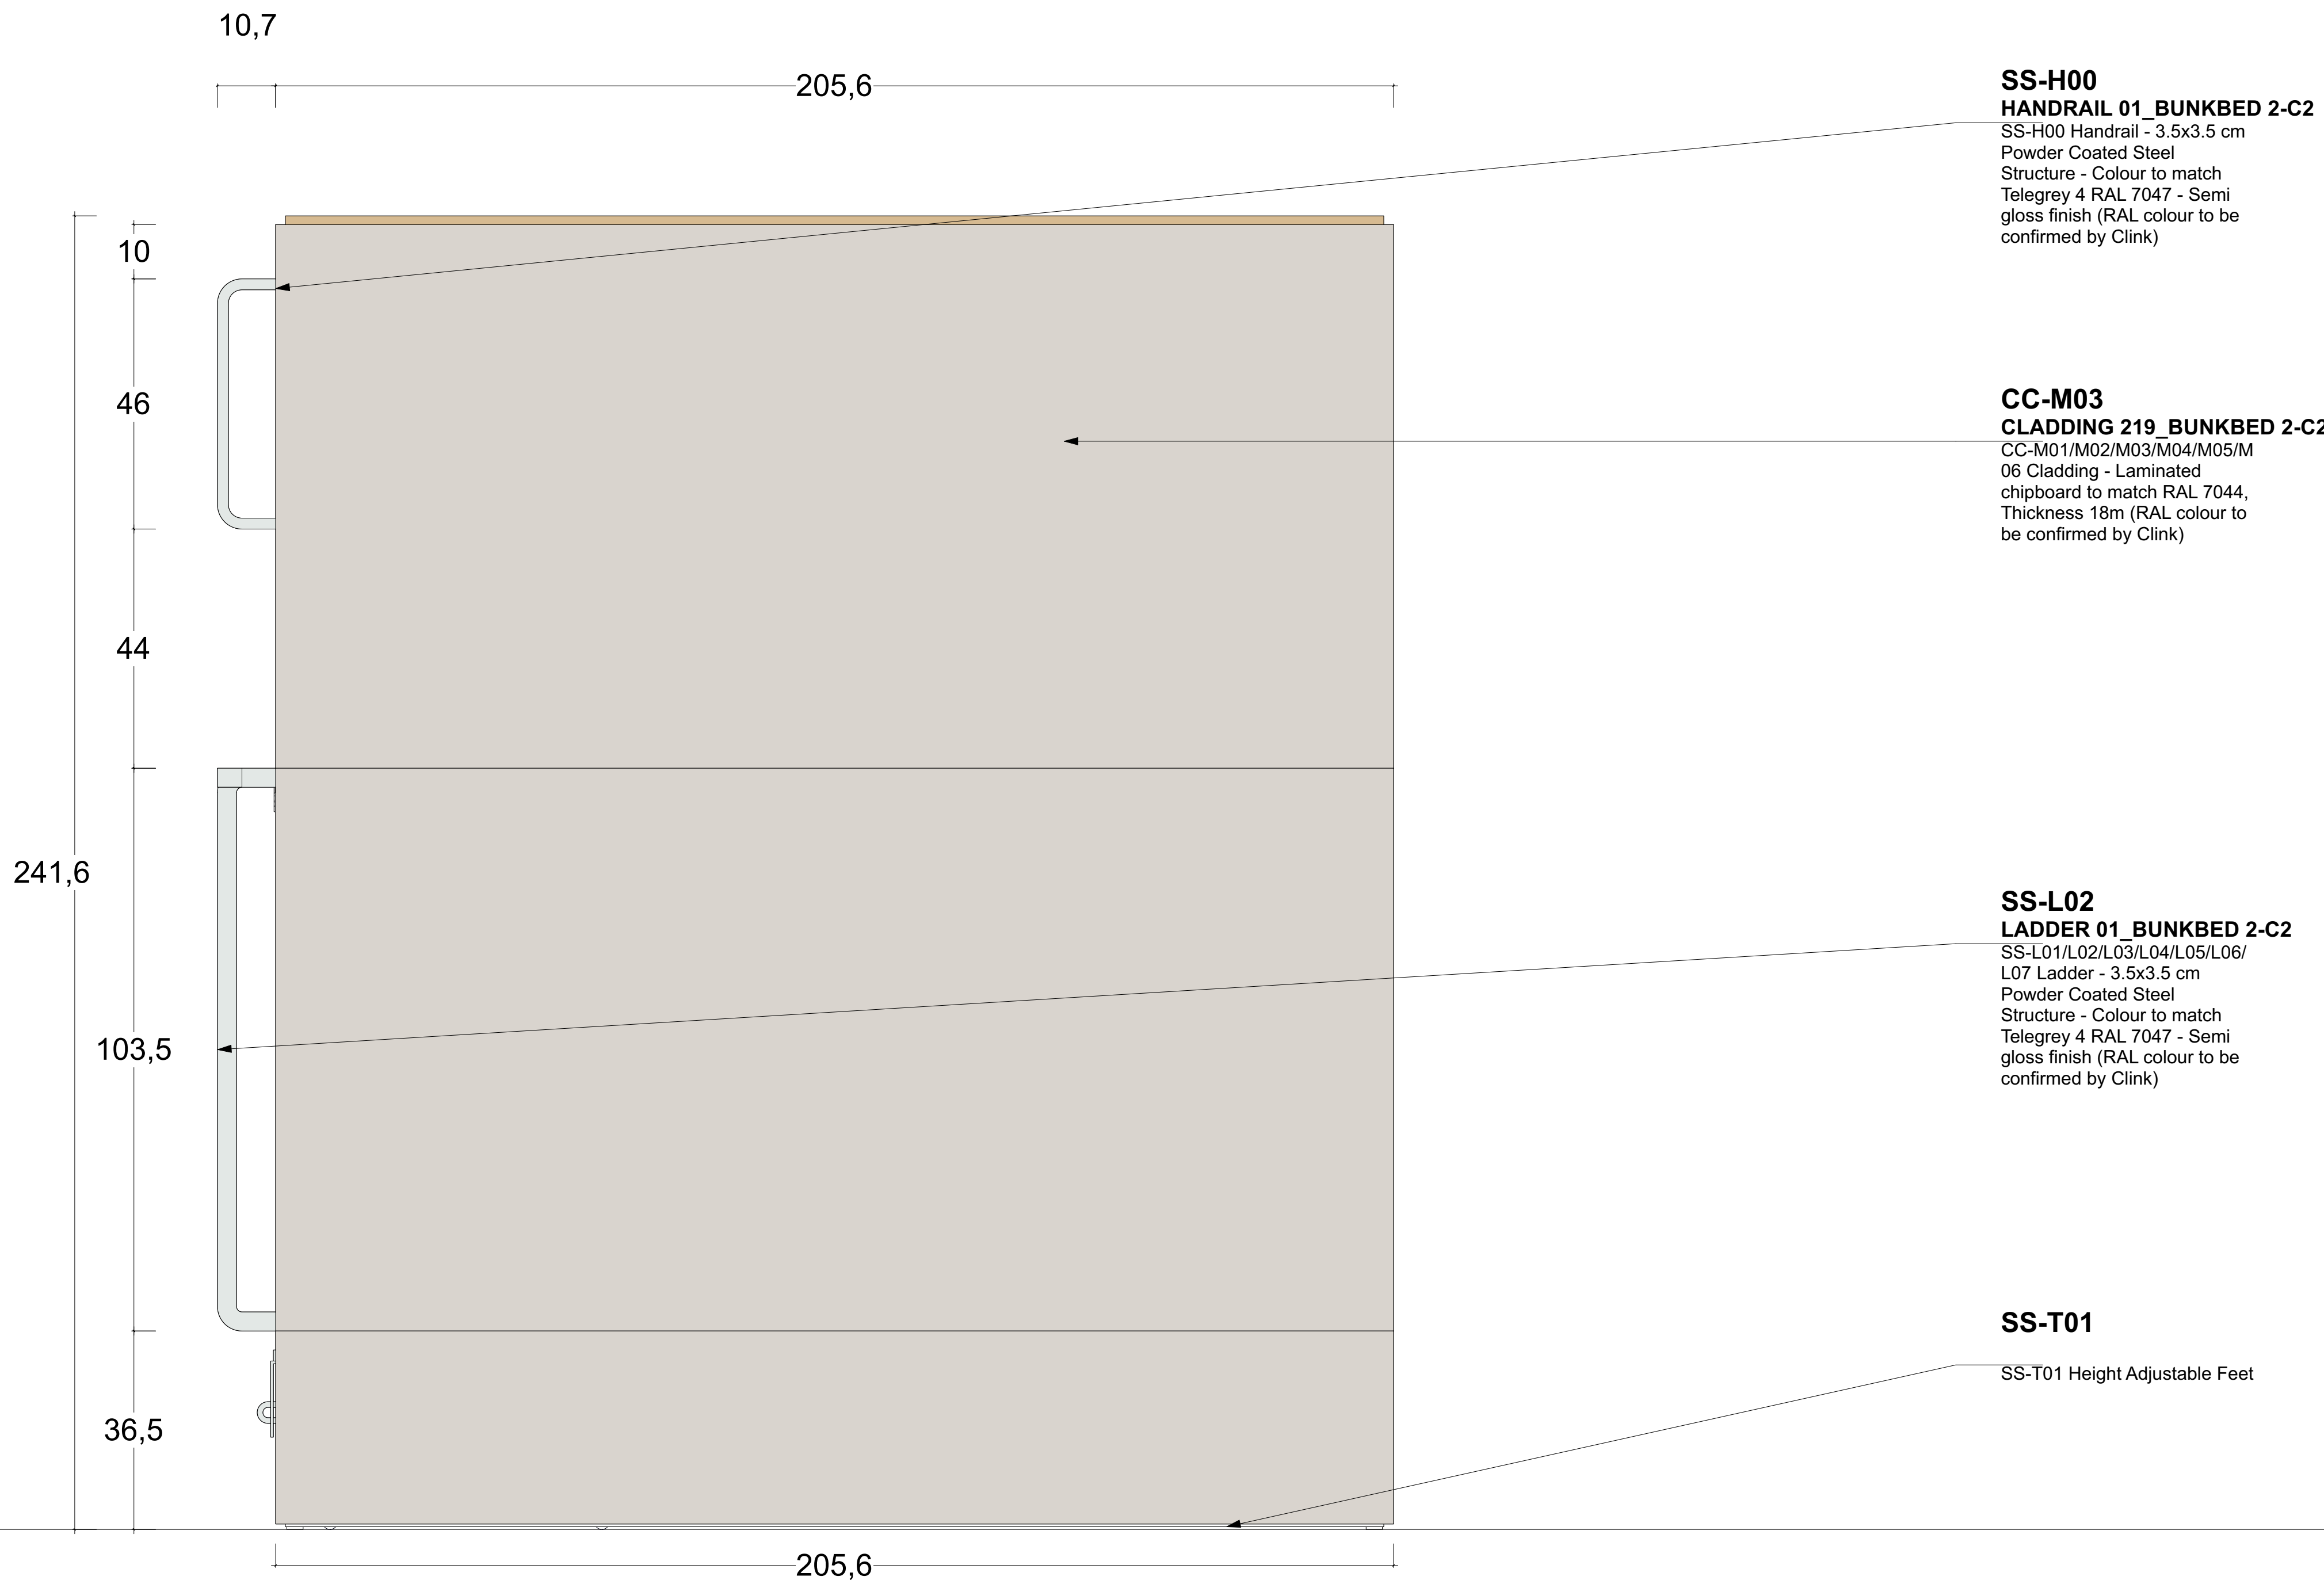

KEY

Index

A) 04.05.2026 Plan Set UP

All measurements have to be verified according to existing conditions by the contractor! Discrepancies must be reported immediately to the responsible project manager. The contractor has to produce fully dimensioned shop drawings prior to the start of the contract and they have to be approved by the client/ investor / interior designer

Project

CLINK 78 - BEDS

Logo



Project Address

CLINK 78
78 King's Cross Rd
London WC1X 9QG
United Kingdom

Client's Address

CLINK 78
78 King's Cross Rd
London WC1X 9QG
United Kingdom

Sheet Number 2-C2-404		Total Sheets 82
Sheet Title BUNKBED 2-C2 RIGHT ELEVATION		Level
File Name 260425_CLINK 78_BEDs AA DRAFT 03.vwx		

Date	Sheet Size	Scale	Signed
28.04.26	A1	1:8	AA

Stefanie Jaensch INTERIOR DESIGNS

Global Headquarter | Stefanie Jaensch c/o WeWork

Taunusanlage 8 | 60329 Frankfurt a.M.



E-Mail info@stefaniejaensch.de | DE +49 (0) 174 6756098

www.stefaniejaensch.de

Legal address | Stefanie Jaensch | Offenbacher Landstraße 434 | 60599 Frankfurt a.M.

© 2023 All Rights Reserved | Stefanie Jaensch

BUNKBEDS - TYPE 2-C2 - LEFT ELEVATION

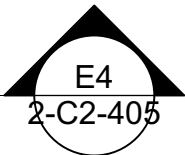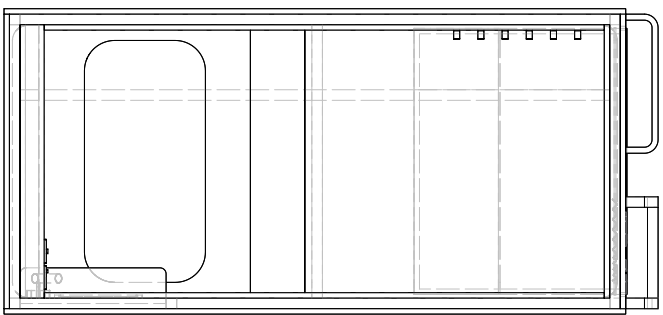

KEY

Index

A) 04.05.2026 Plan Set UP

All measurements have to be verified according to existing conditions by the contractor! Discrepancies must be reported immediately to the responsible project manager. The contractor has to produce fully dimensioned shop drawings prior to the start of the contract and they have to be approved by the client/ investor / interior designer

Project

CLINK 78 - BEDS

Logo



Project Address

CLINK 78
78 King's Cross Rd
London WC1X 9QG
United Kingdom

Client's Address

CLINK 78
78 King's Cross Rd
London WC1X 9QG
United Kingdom

Sheet Number 2-C2-405		Total Sheets 82
Sheet Title BUNKBED 2-C2 LEFT ELEVATION		Level
File Name 260425_CLINK 78_BEDs AA DRAFT 03.vwx		

Date	Sheet Size	Scale	Signed
28.04.26	A1	1:8	AA

Stefanie Jaensch INTERIOR DESIGNS


Global Headquarter | Stefanie Jaensch c/o WeWork
Taunusanlage 8 | 60329 Frankfurt a.M.

E-Mail info@stefaniejaensch.de | DE +49 (0) 174 6756098


www.stefaniejaensch.de

Legal address | Stefanie Jaensch | Offenbacher Landstraße 434 | 60599 Frankfurt a.M.

© 2023 All Rights Reserved | Stefanie Jaensch

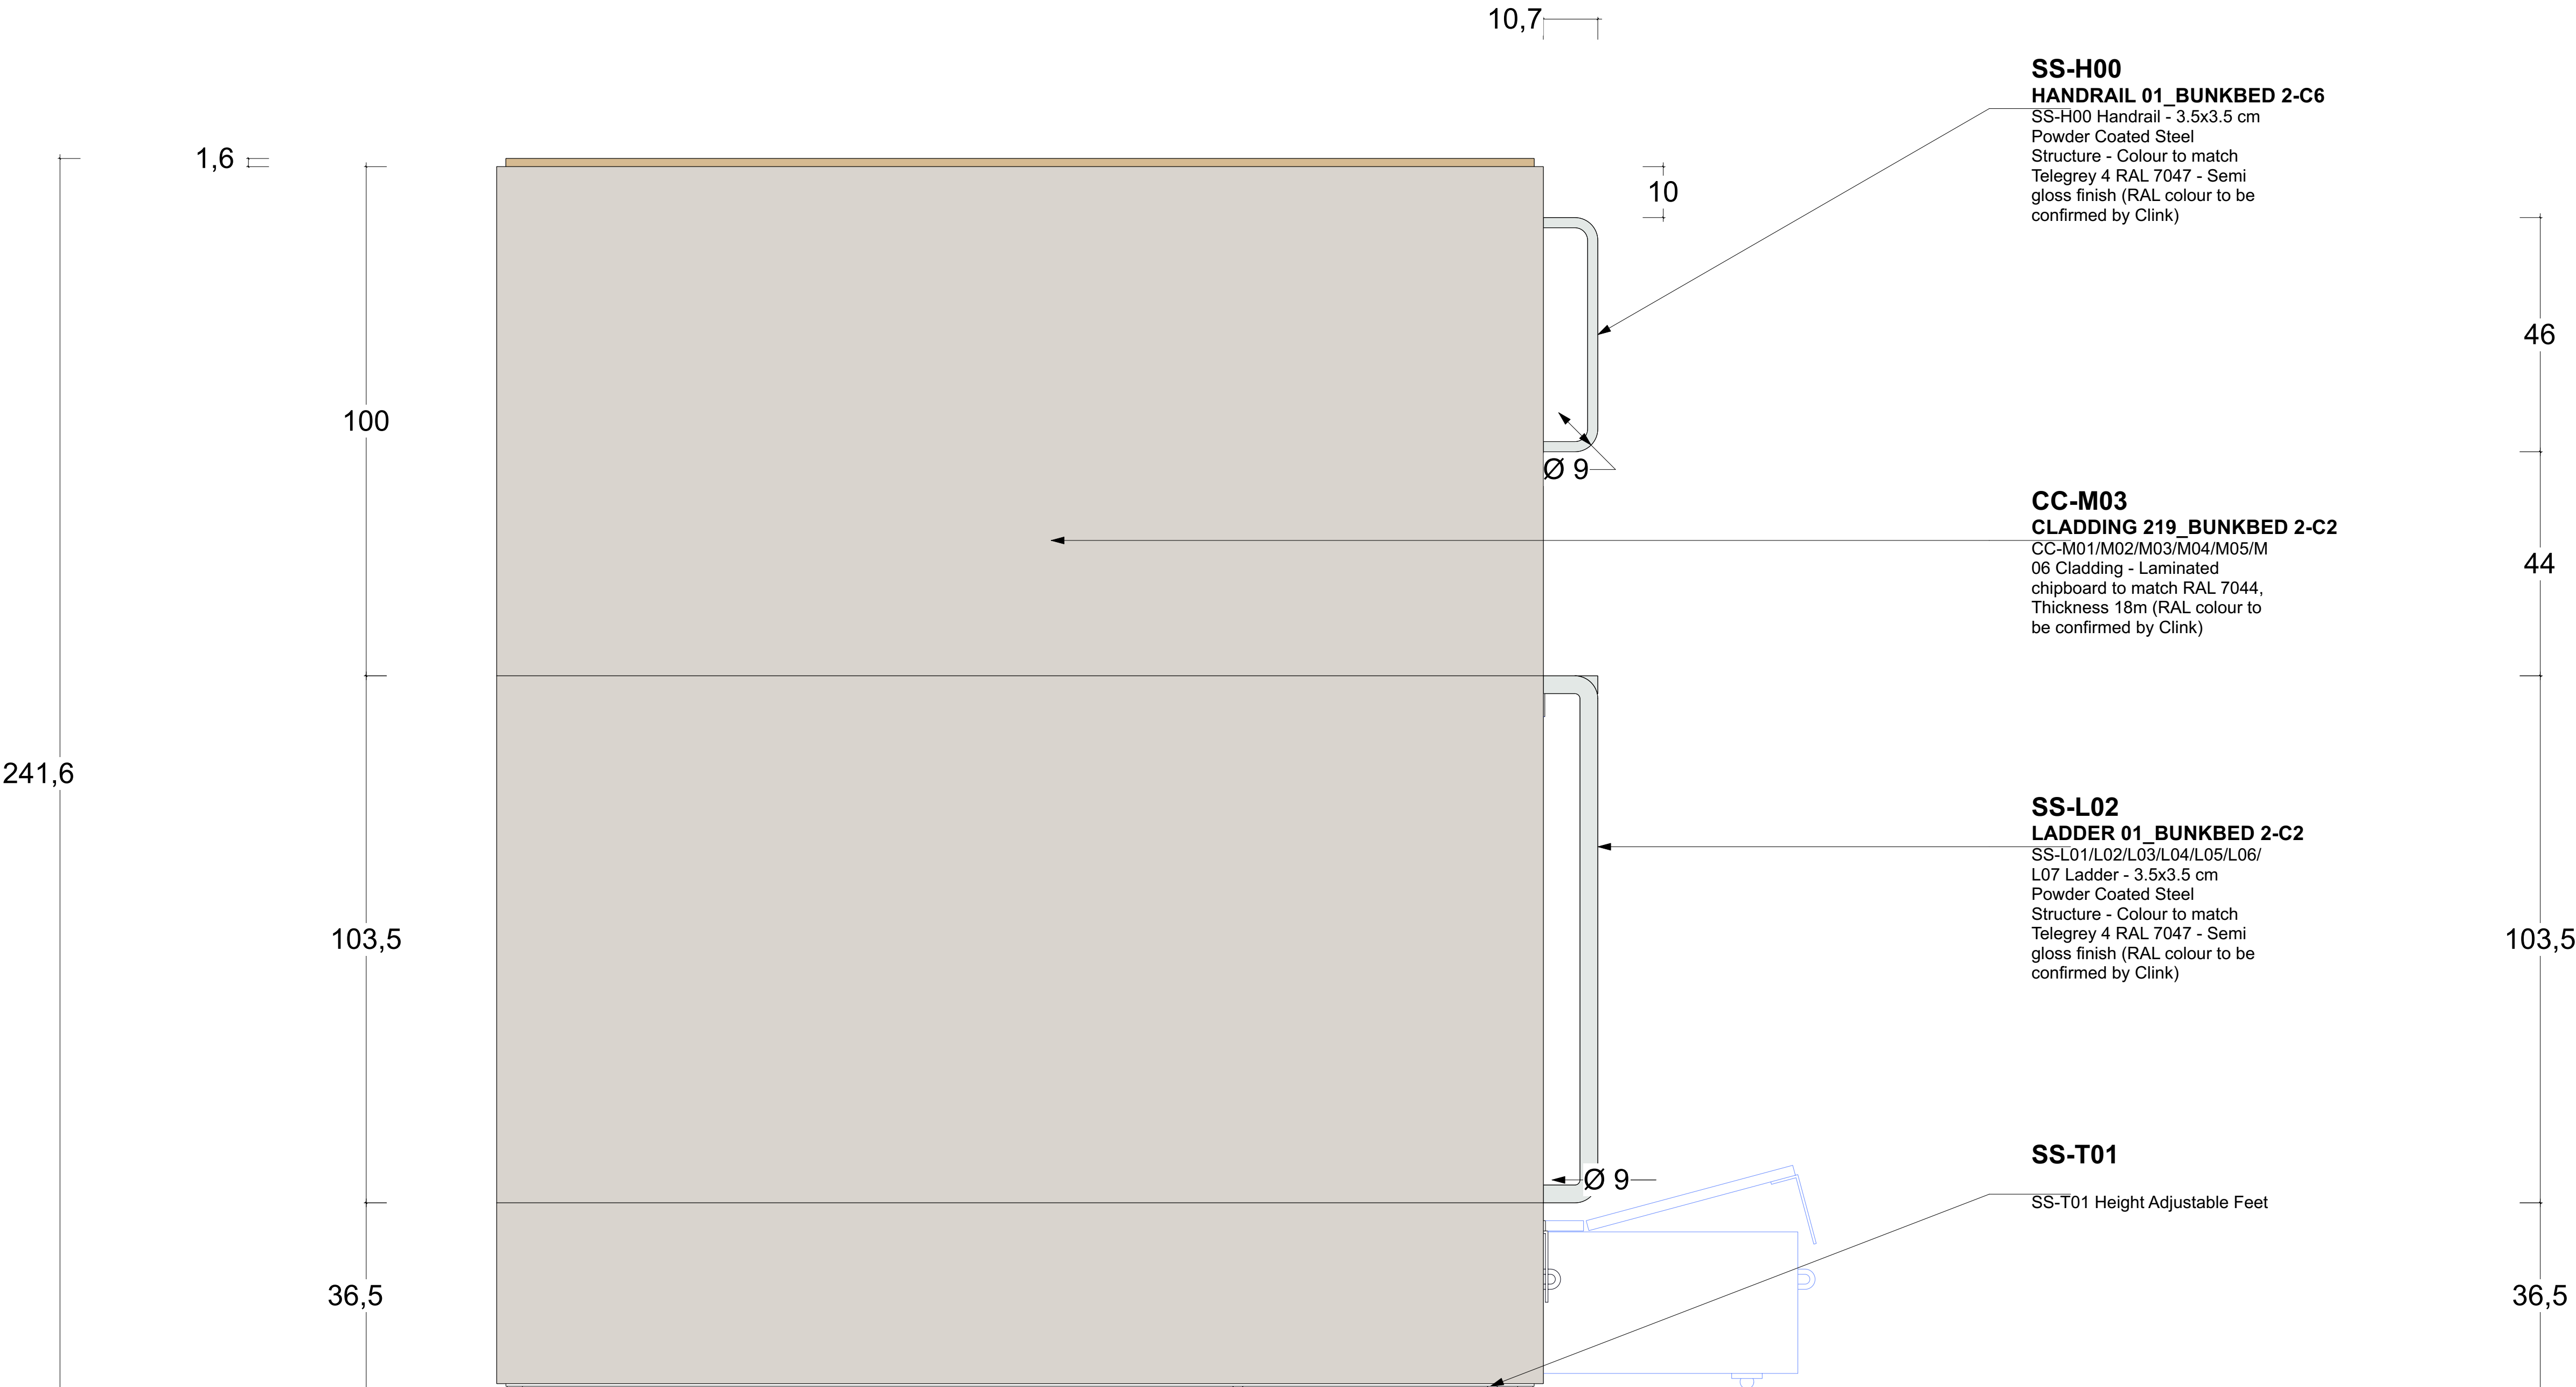

BUNKBEDS - TYPE 2-C2 - SECTION 1

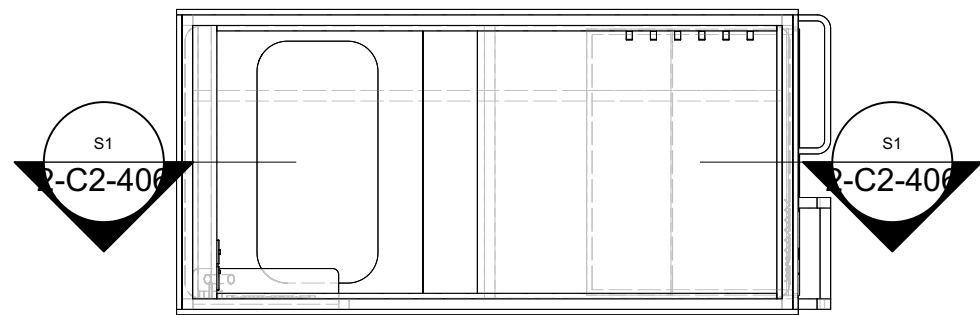

KEY

Index

A) 04.05.2026 Plan Set UP

All measurements have to be verified according to existing conditions by the contractor! Discrepancies must be reported immediately to the responsible project manager. The contractor has to produce fully dimensioned shop drawings prior to the start of the contract and they have to be approved by the client/ investor / interior designer

Project

CLINK 78 - BEDS

Logo



Project Address

CLINK 78
78 King's Cross Rd
London WC1X 9QG
United Kingdom

Client's Address

CLINK 78
78 King's Cross Rd
London WC1X 9QG
United Kingdom

Sheet Number 2-C2-406

Total Sheets

82

Sheet Title
BUNKBED 2-C2 SECTION 1

Level

File Name

260425_CLINK 78_BEDs AA DRAFT 03.vwx

Date	Sheet Size	Scale	Signed
28.04.26	A1	1:8	AA

Stefanie Jaensch INTERIOR DESIGNS

Global Headquarter | Stefanie Jaensch c/o WeWork


Taunusanlage 8 | 60329 Frankfurt a.M.

E-Mail info@stefaniejaensch.de | DE +49 (0) 174 6756098



www.stefaniejaensch.de

Legal address | Stefanie Jaensch | Offenbacher Landstraße 434 | 60599 Frankfurt a.M.

© 2023 All Rights Reserved | Stefanie Jaensch

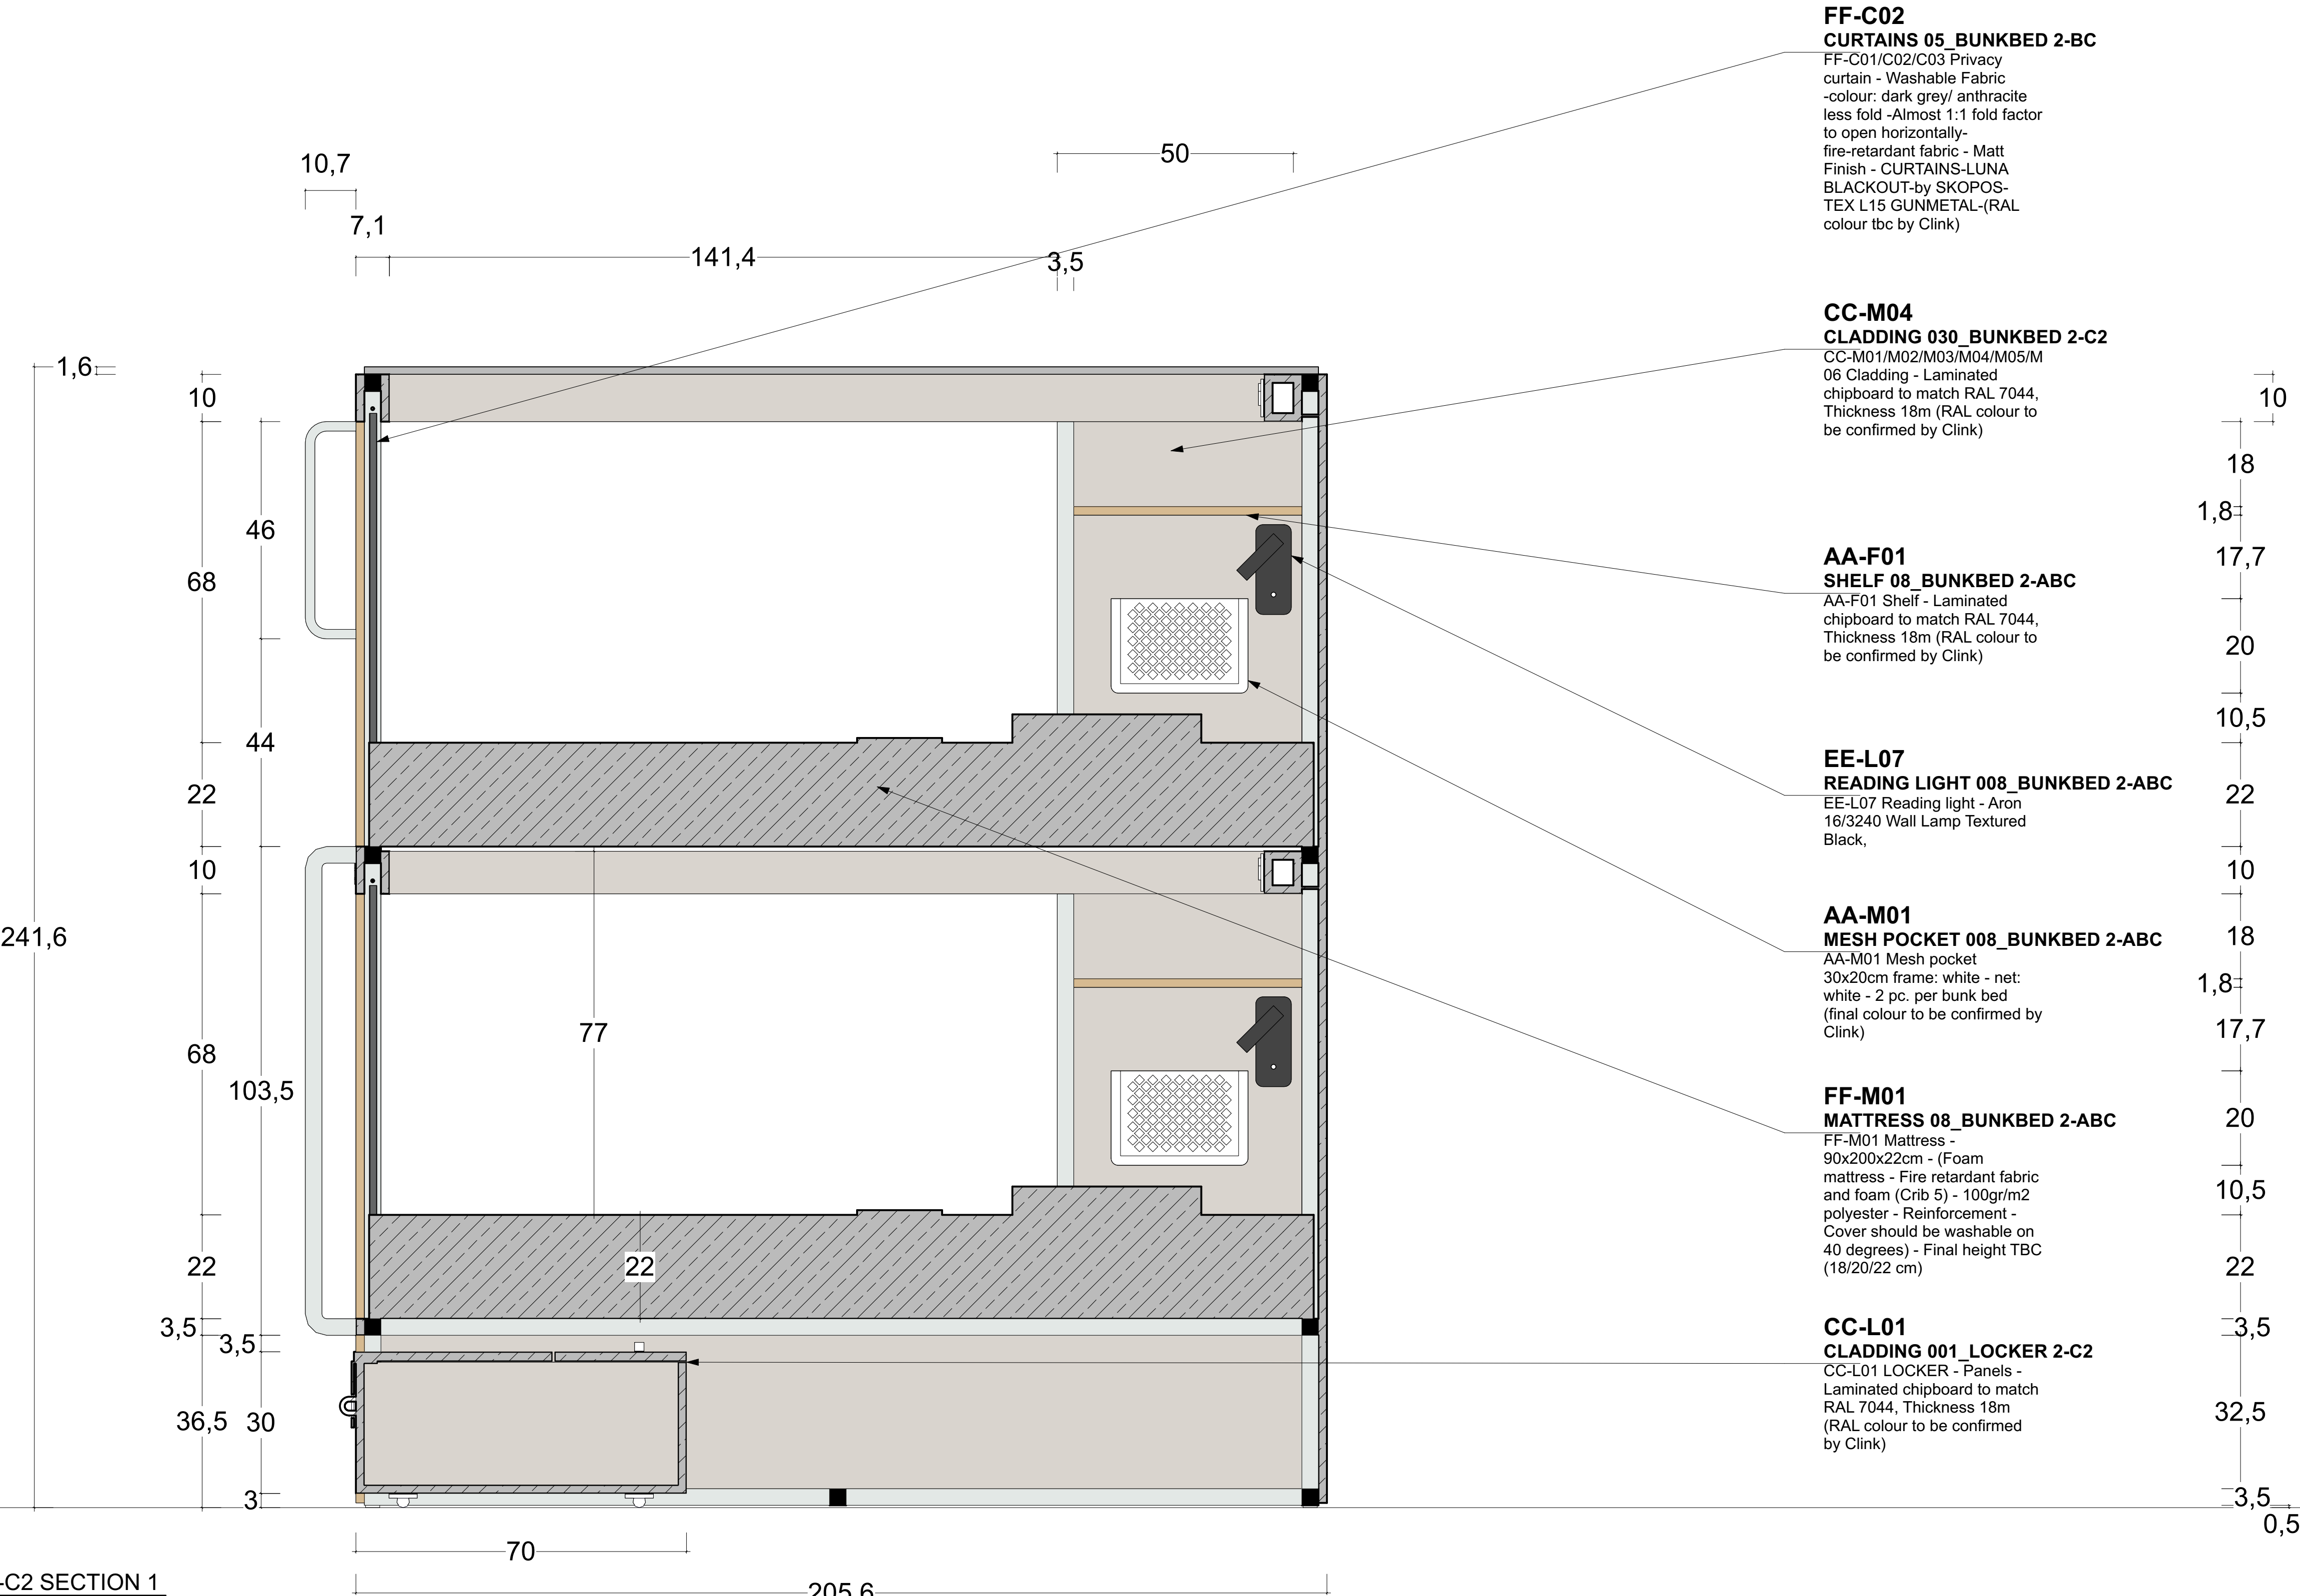

BUNKBEDS - TYPE 2-C2 - SECTION 2

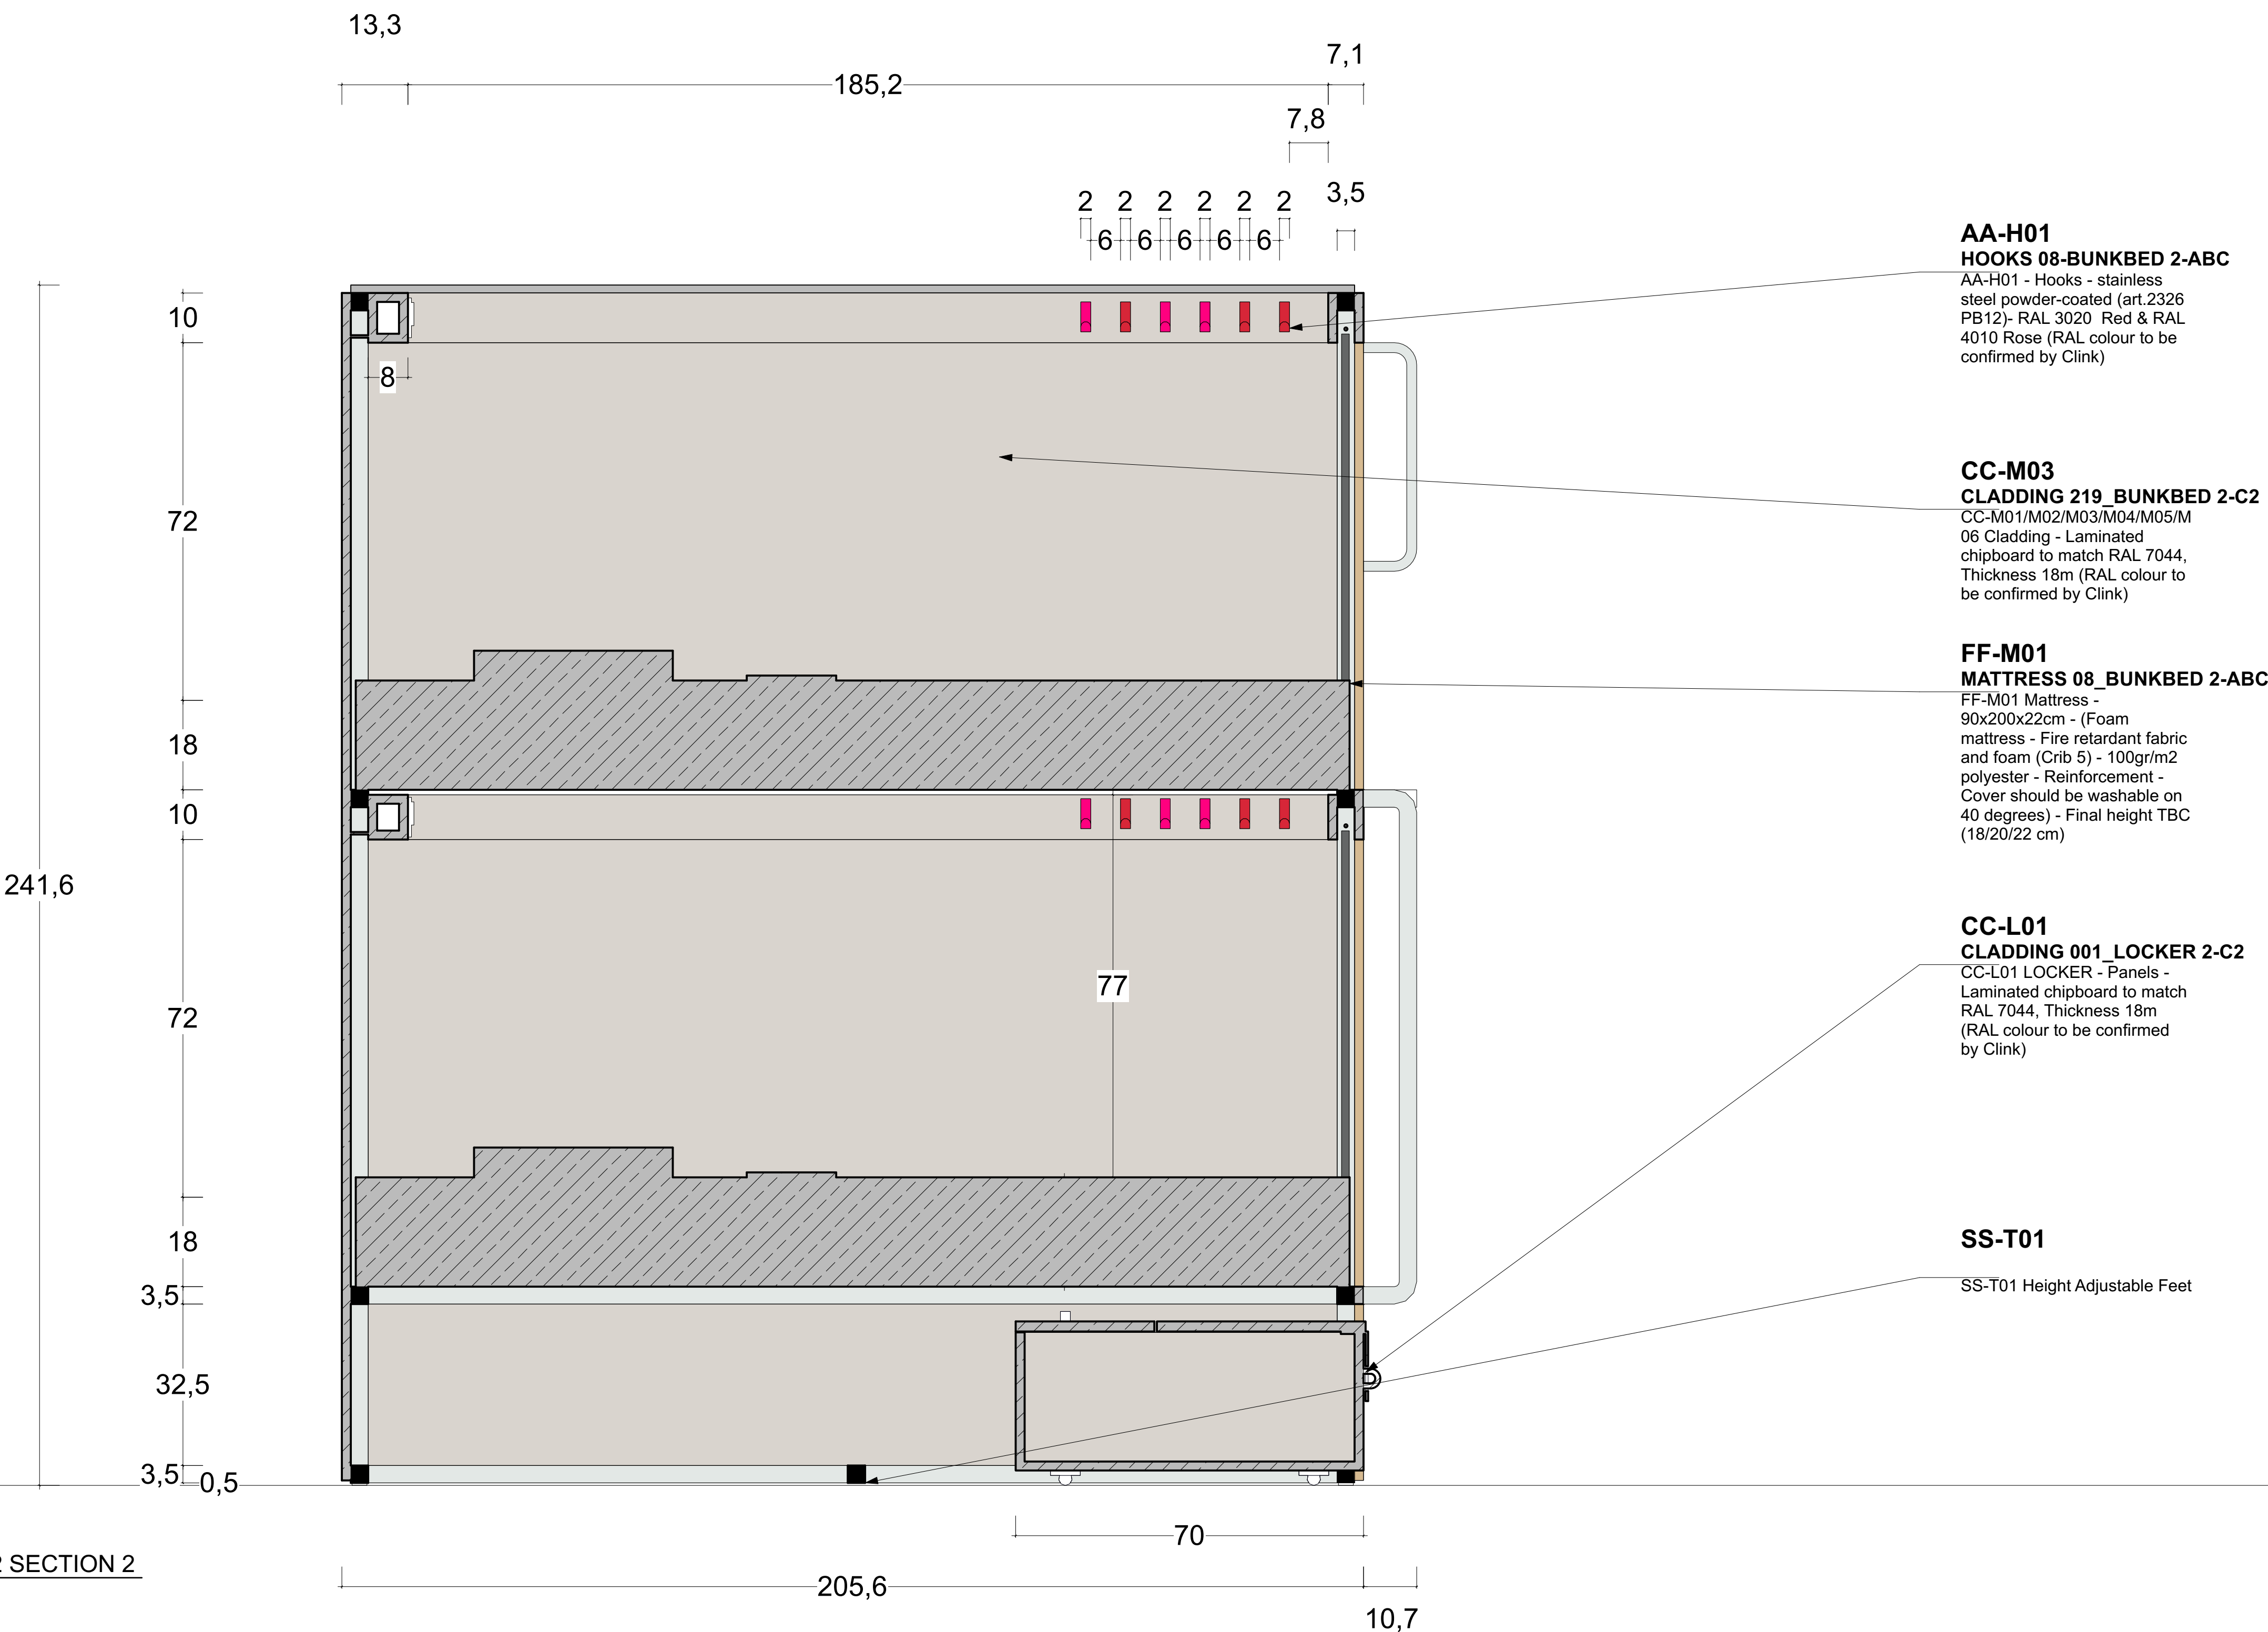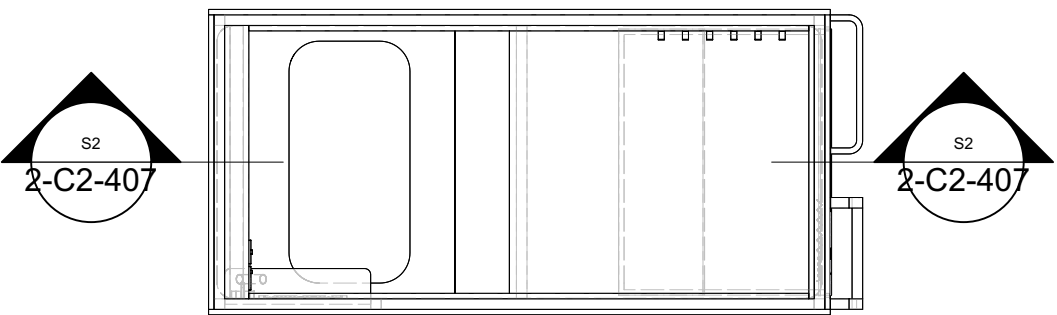

KEY

Index

A) 04.05.2026 Plan Set UP

All measurements have to be verified according to existing conditions by the contractor! Discrepancies must be reported immediately to the responsible project manager. The contractor has to produce fully dimensioned shop drawings prior to the start of the contract and they have to be approved by the client/ investor / interior designer

Project
CLINK 78 - BEDS





Project Address
CLINK 78
78 King's Cross Rd
London WC1X 9QG
United Kingdom

Client's Address
CLINK 78
78 King's Cross Rd
London WC1X 9QG
United Kingdom

Sheet Number 2-C2-407		Total Sheets 82
Sheet Title BUNKBED 2-C2 SECTION 2		Level
File Name 260425_CLINK 78_BEDs AA DRAFT 03.vwx		
Date 28.04.26	Sheet Size A1	Scale 1:8
		Signed AA

Stefanie Jaensch INTERIOR DESIGNS
Global Headquarter | Stefanie Jaensch c/o WeWork
Taunusanlage 8 | 60329 Frankfurt a.M.
E-Mail info@stefaniejaensch.de | DE +49 (0) 174 6756098
www.stefaniejaensch.de
Legal address | Stefanie Jaensch | Offenbacher Landstraße 434 | 60599 Frankfurt a.M.
© 2023 All Rights Reserved | Stefanie Jaensch

BUNKBEDS - TYPE 2-C2 - SECTION 3

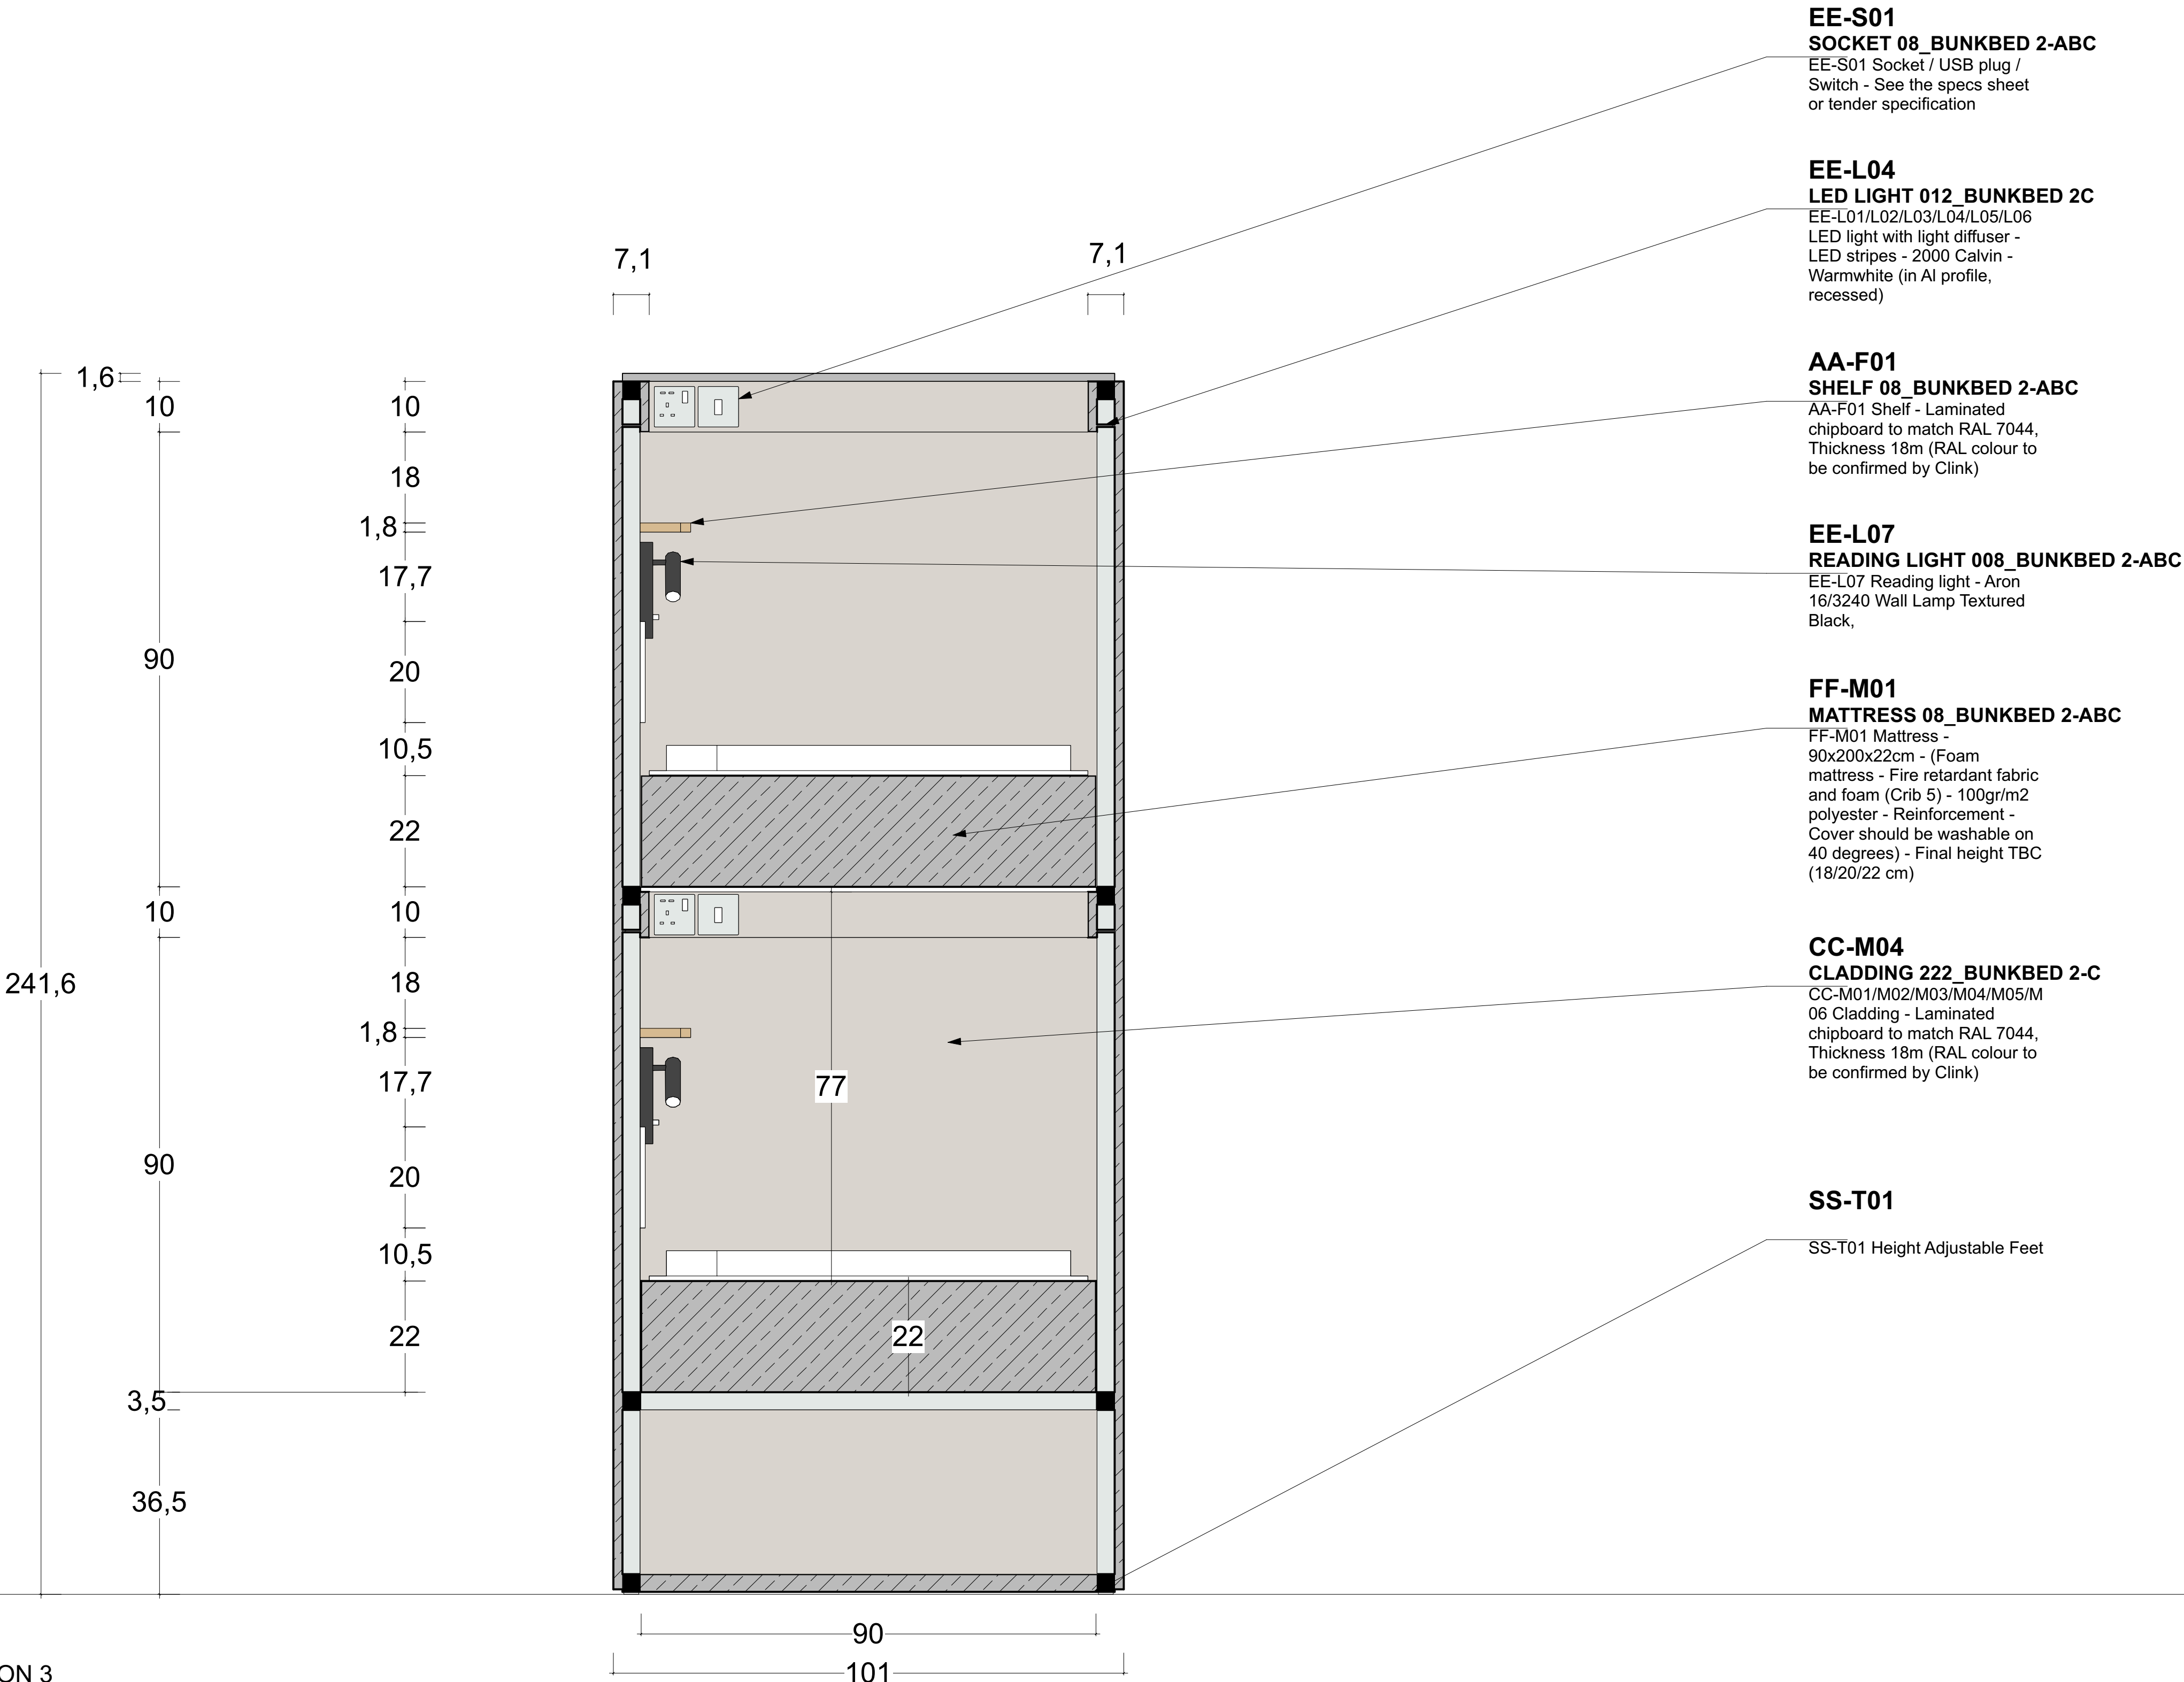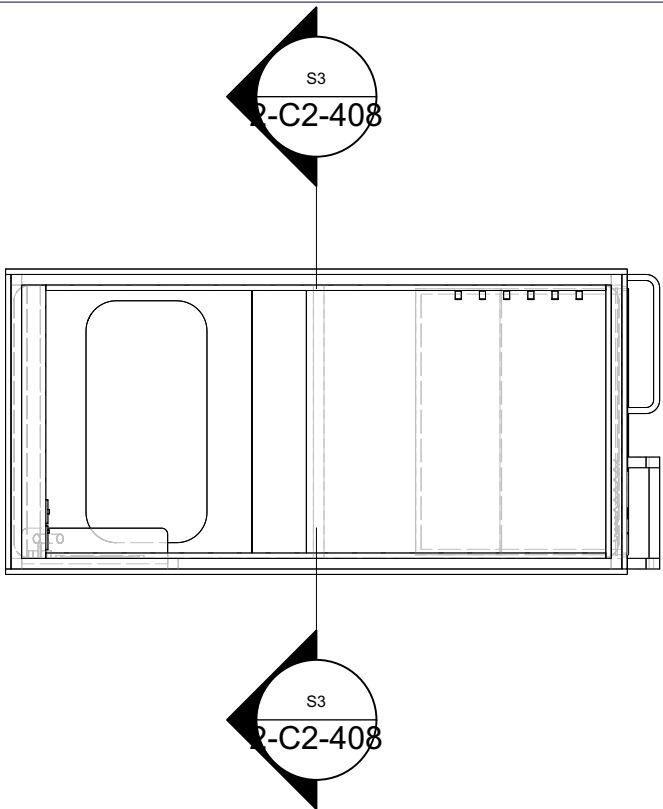

KEY

Index

A) 04.05.2026 Plan Set UP

All measurements have to be verified according to existing conditions by the contractor! Discrepancies must be reported immediately to the responsible project manager. The contractor has to produce fully dimensioned shop drawings prior to the start of the contract and they have to be approved by the client/ investor / interior designer

Project

CLINK 78 - BEDS

Logo



Project Address

CLINK 78
78 King's Cross Rd
London WC1X 9QG
United Kingdom

Client's Address

CLINK 78
78 King's Cross Rd
London WC1X 9QG
United Kingdom



Sheet Number 2-C2-408		Total Sheets 82
Sheet Title BUNKBED 2-C2 SECTION 3		Level
File Name 260425_CLINK 78_BEDs AA DRAFT 03.vwx		
Date 28.04.26	Sheet Size A1	Scale 1:8
		Signed AA

Stefanie Jaensch INTERIOR DESIGNS

Global Headquarter | Stefanie Jaensch c/o WeWork
Taubusanlage 8 | 60329 Frankfurt a.M.
E-Mail info@stefaniejaensch.de | DE +49 (0) 174 6756098
www.stefaniejaensch.de

Legal address | Stefanie Jaensch | Offenbacher Landstraße 434 | 60599 Frankfurt a.M.
© 2023 All Rights Reserved | Stefanie Jaensch

BUNKBEDS - TYPE 2-C2 - SECTION 4

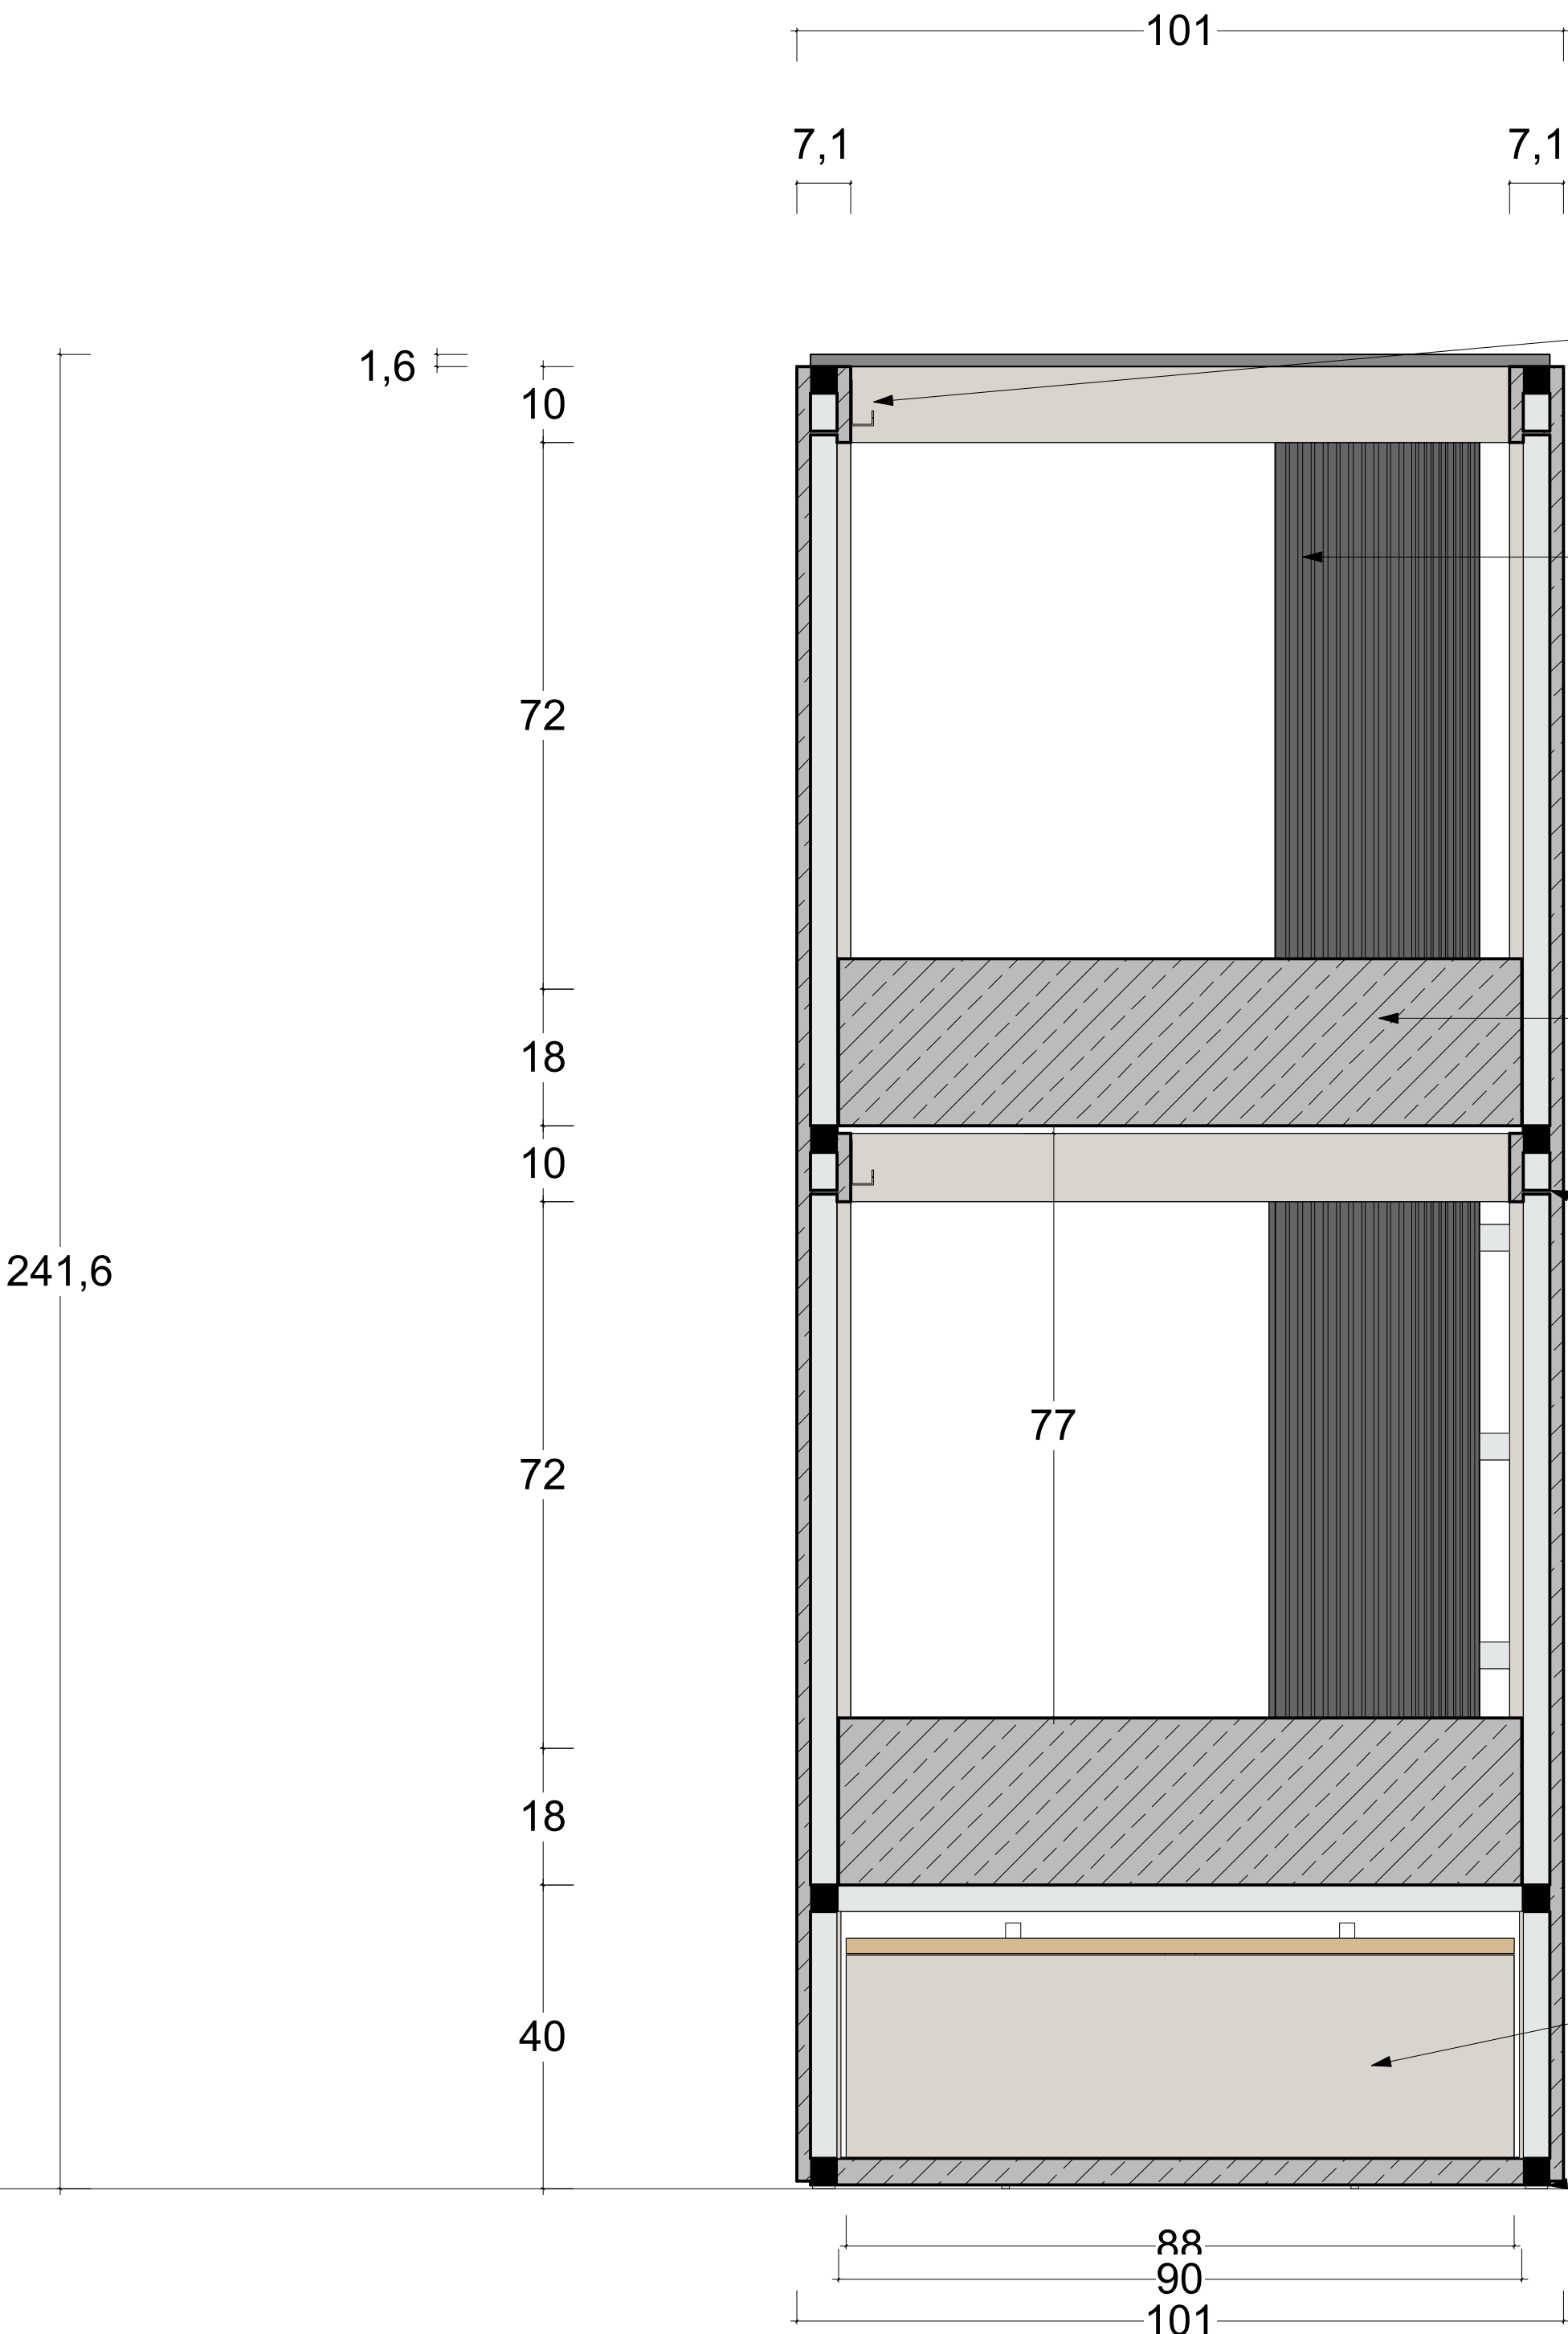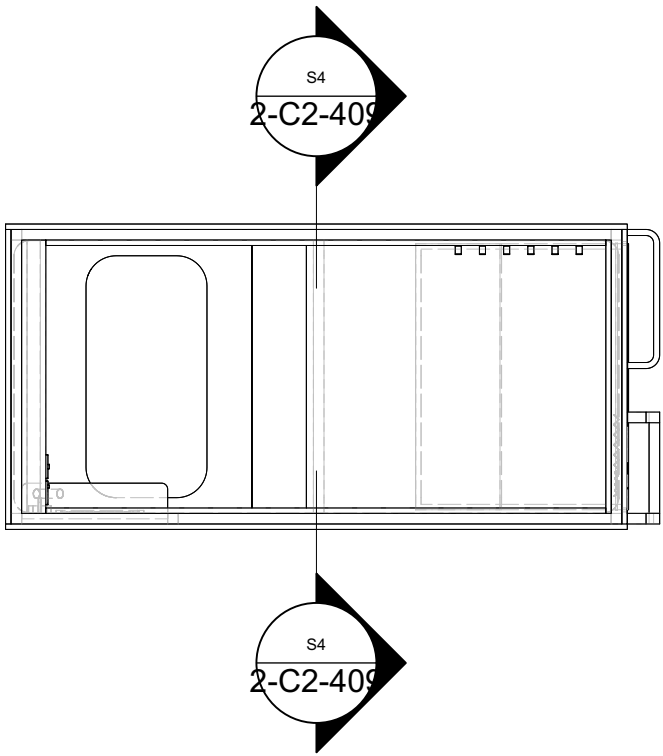

AA-H01
HOOKS 08-BUNKBED 2-ABC
AA-H01 - Hooks - stainless steel powder-coated (art.2326 PB12)- RAL 3020 Red & RAL 4010 Rose (RAL colour to be confirmed by Clink)

FF-C02
CURTAINS 05_BUNKBED 2-BC
FF-C01/C02/C03 Privacy curtain - Washable Fabric -colour: dark grey/ anthracite less fold -Almost 1:1 fold factor to open horizontally- fire-retardant fabric - Matt Finish - CURTAINS-LUNA BLACKOUT-by SKOPOS-TEX L15 GUNMETAL-(RAL colour tbc by Clink)

FF-M01
MATTRESS 08_BUNKBED 2-ABC
FF-M01 Mattress - 90x200x22cm - (Foam mattress - Fire retardant fabric and foam (Crib 5) - 100gr/m2 polyester - Reinforcement - Cover should be washable on 40 degrees) - Final height TBC (18/20/22 cm)

EE-L04
LED LIGHT 007_BUNKBED 2C
EE-L01/L02/L03/L04/L05/L06 LED light with light diffuser - LED stripes - 2000 Calvin - Warmwhite (in AI profile, recessed)

CC-L01
CLADDING 001_LOCKER 2-C2
CC-L01 LOCKER - Panels - Laminated chipboard to match RAL 7044, Thickness 18m (RAL colour to be confirmed by Clink)

SS-T01
SS-T01 Height Adjustable Feet



KEY

Index

A) 04.05.2026 Plan Set UP

All measurements have to be verified according to existing conditions by the contractor! Discrepancies must be reported immediately to the responsible project manager.The contractor has to produce fully dimensioned shop drawings prior to the start of the contract and they have to be approved by the client/ investor / interior designer

Project

CLINK 78 - BEDS

Logo



Project Address

CLINK 78
78 King's Cross Rd
London WC1X 9QG
United Kingdom

Client's Address

CLINK 78
78 King's Cross Rd
London WC1X 9QG
United Kingdom

Sheet Number	2-C2-409	Total Sheets	82
Sheet Title	BUNKBED 2-C2 SECTION 4	Level	
File Name			
260425_CLINK 78_BEDs AA DRAFT 03.vwx			

Date	Sheet Size	Scale	Signed
28.04.26	A1	1:8	AA

Stefanie Jaensch INTERIOR DESIGNS


Global Headquarter | Stefanie Jaensch c/o WeWork
Taunusanlage 8 | 60329 Frankfurt a.M.

E-Mail info@stefaniejaensch.de | DE +49 (0) 174 6756098

www.stefaniejaensch.de

Legal address | Stefanie Jaensch | Offenbacher Landstraße 434 | 60599 Frankfurt a.M.

© 2023 All Rights Reserved | Stefanie Jaensch

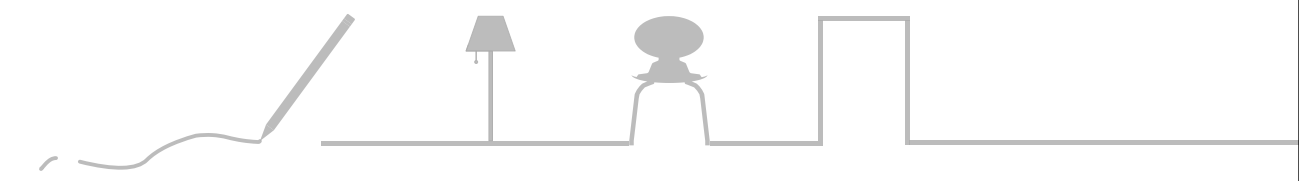


For

CLiNK
HOSTELS

PODS TYPE 2P

THE
DRAW

PODS TYPE 2P

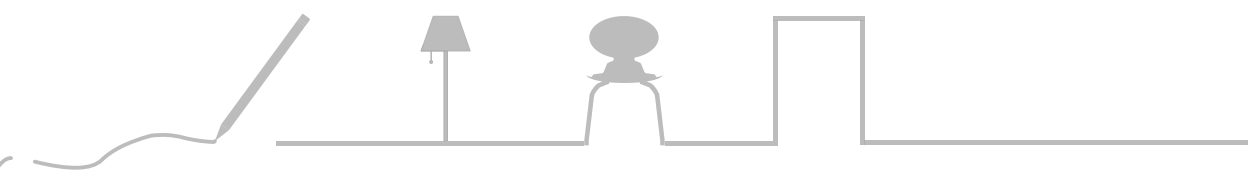


Stefanie Jaensch

INTERIOR DESIGNS

For




DRAFT

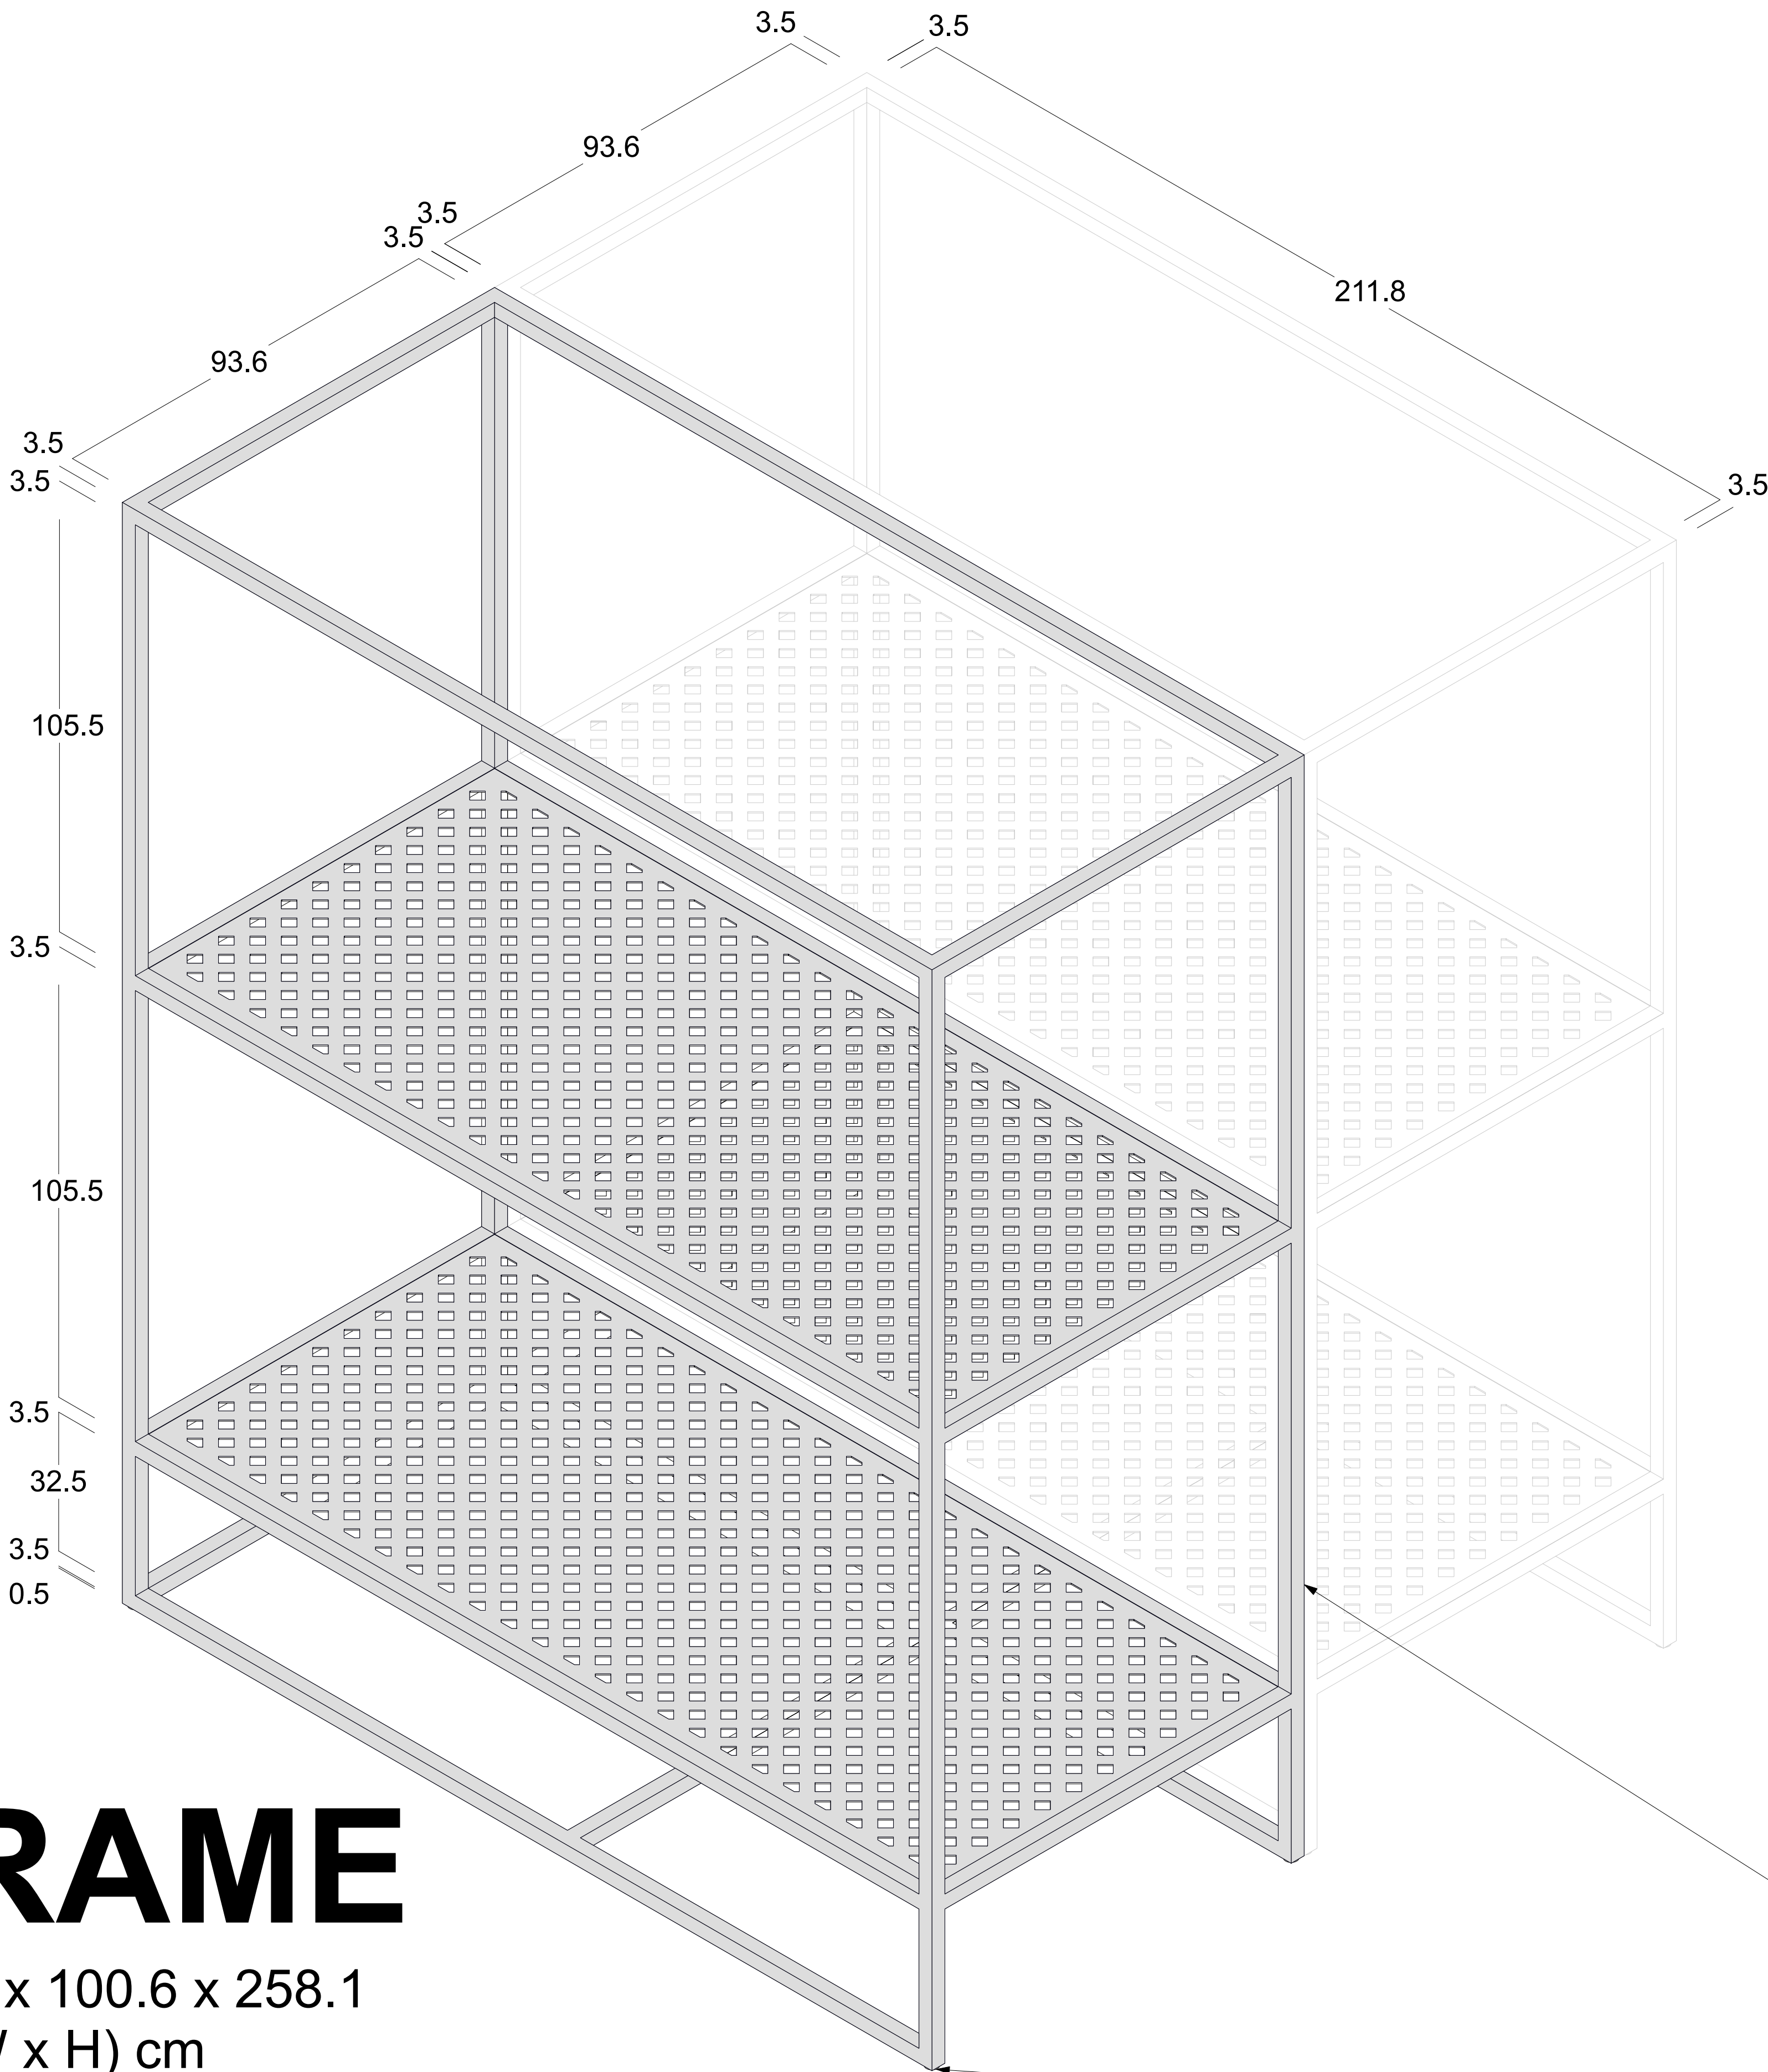

FRAME

218.8 x 100.6 x 258.1
(L x W x H) cm

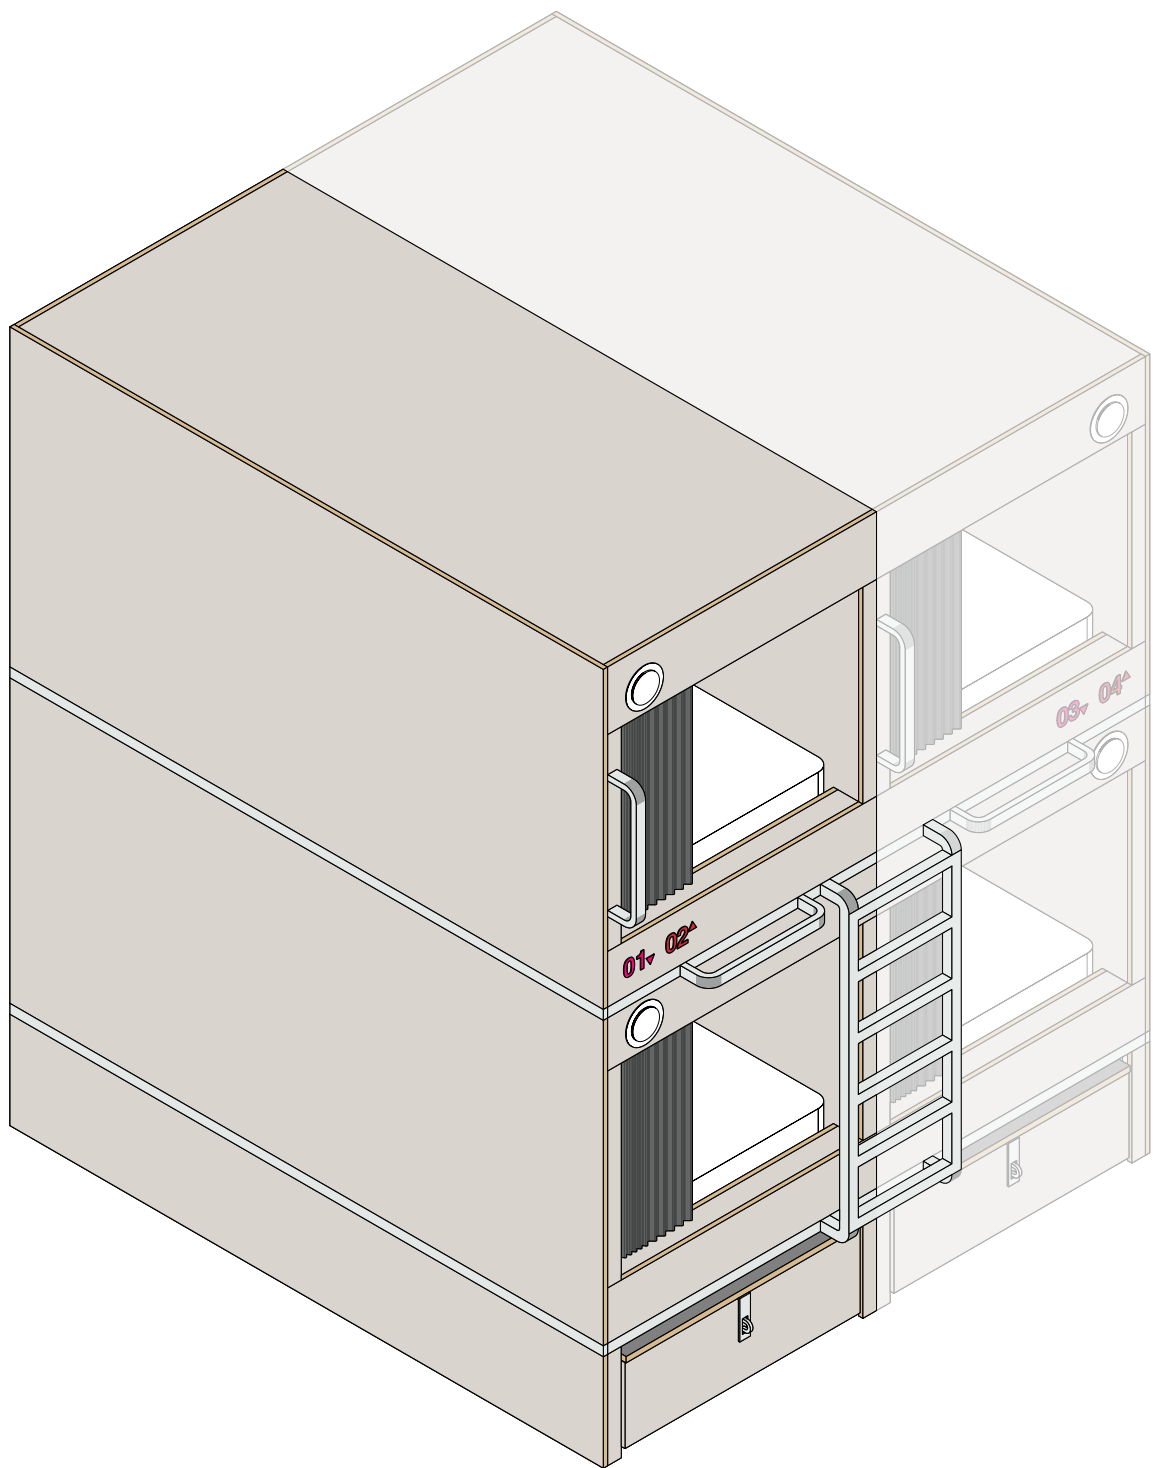


2-P

SS-F01
FRAME_BUNKBED 2-AB
SS-F01/F02/F03 Frame -
3.5x3.5 cm Powder Coated
Steel Frame Structure - Colour
to match Telegrey 4 RAL 7047
- Semi gloss finish (RAL colour
to be confirmed by Clink)

SS-T01
SS-T01 Height Adjustable Feet


PODS TYPE 2P

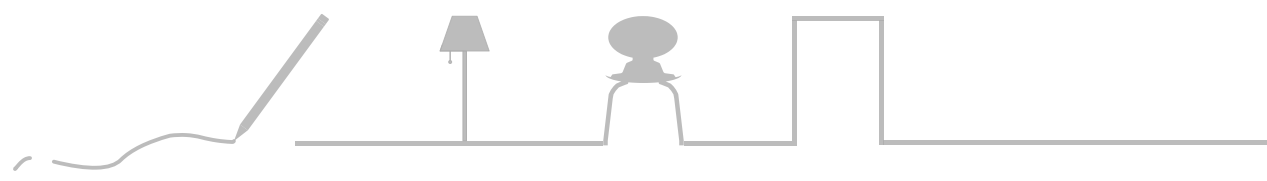

Stefanie Jaensch

INTERIOR DESIGNS

For

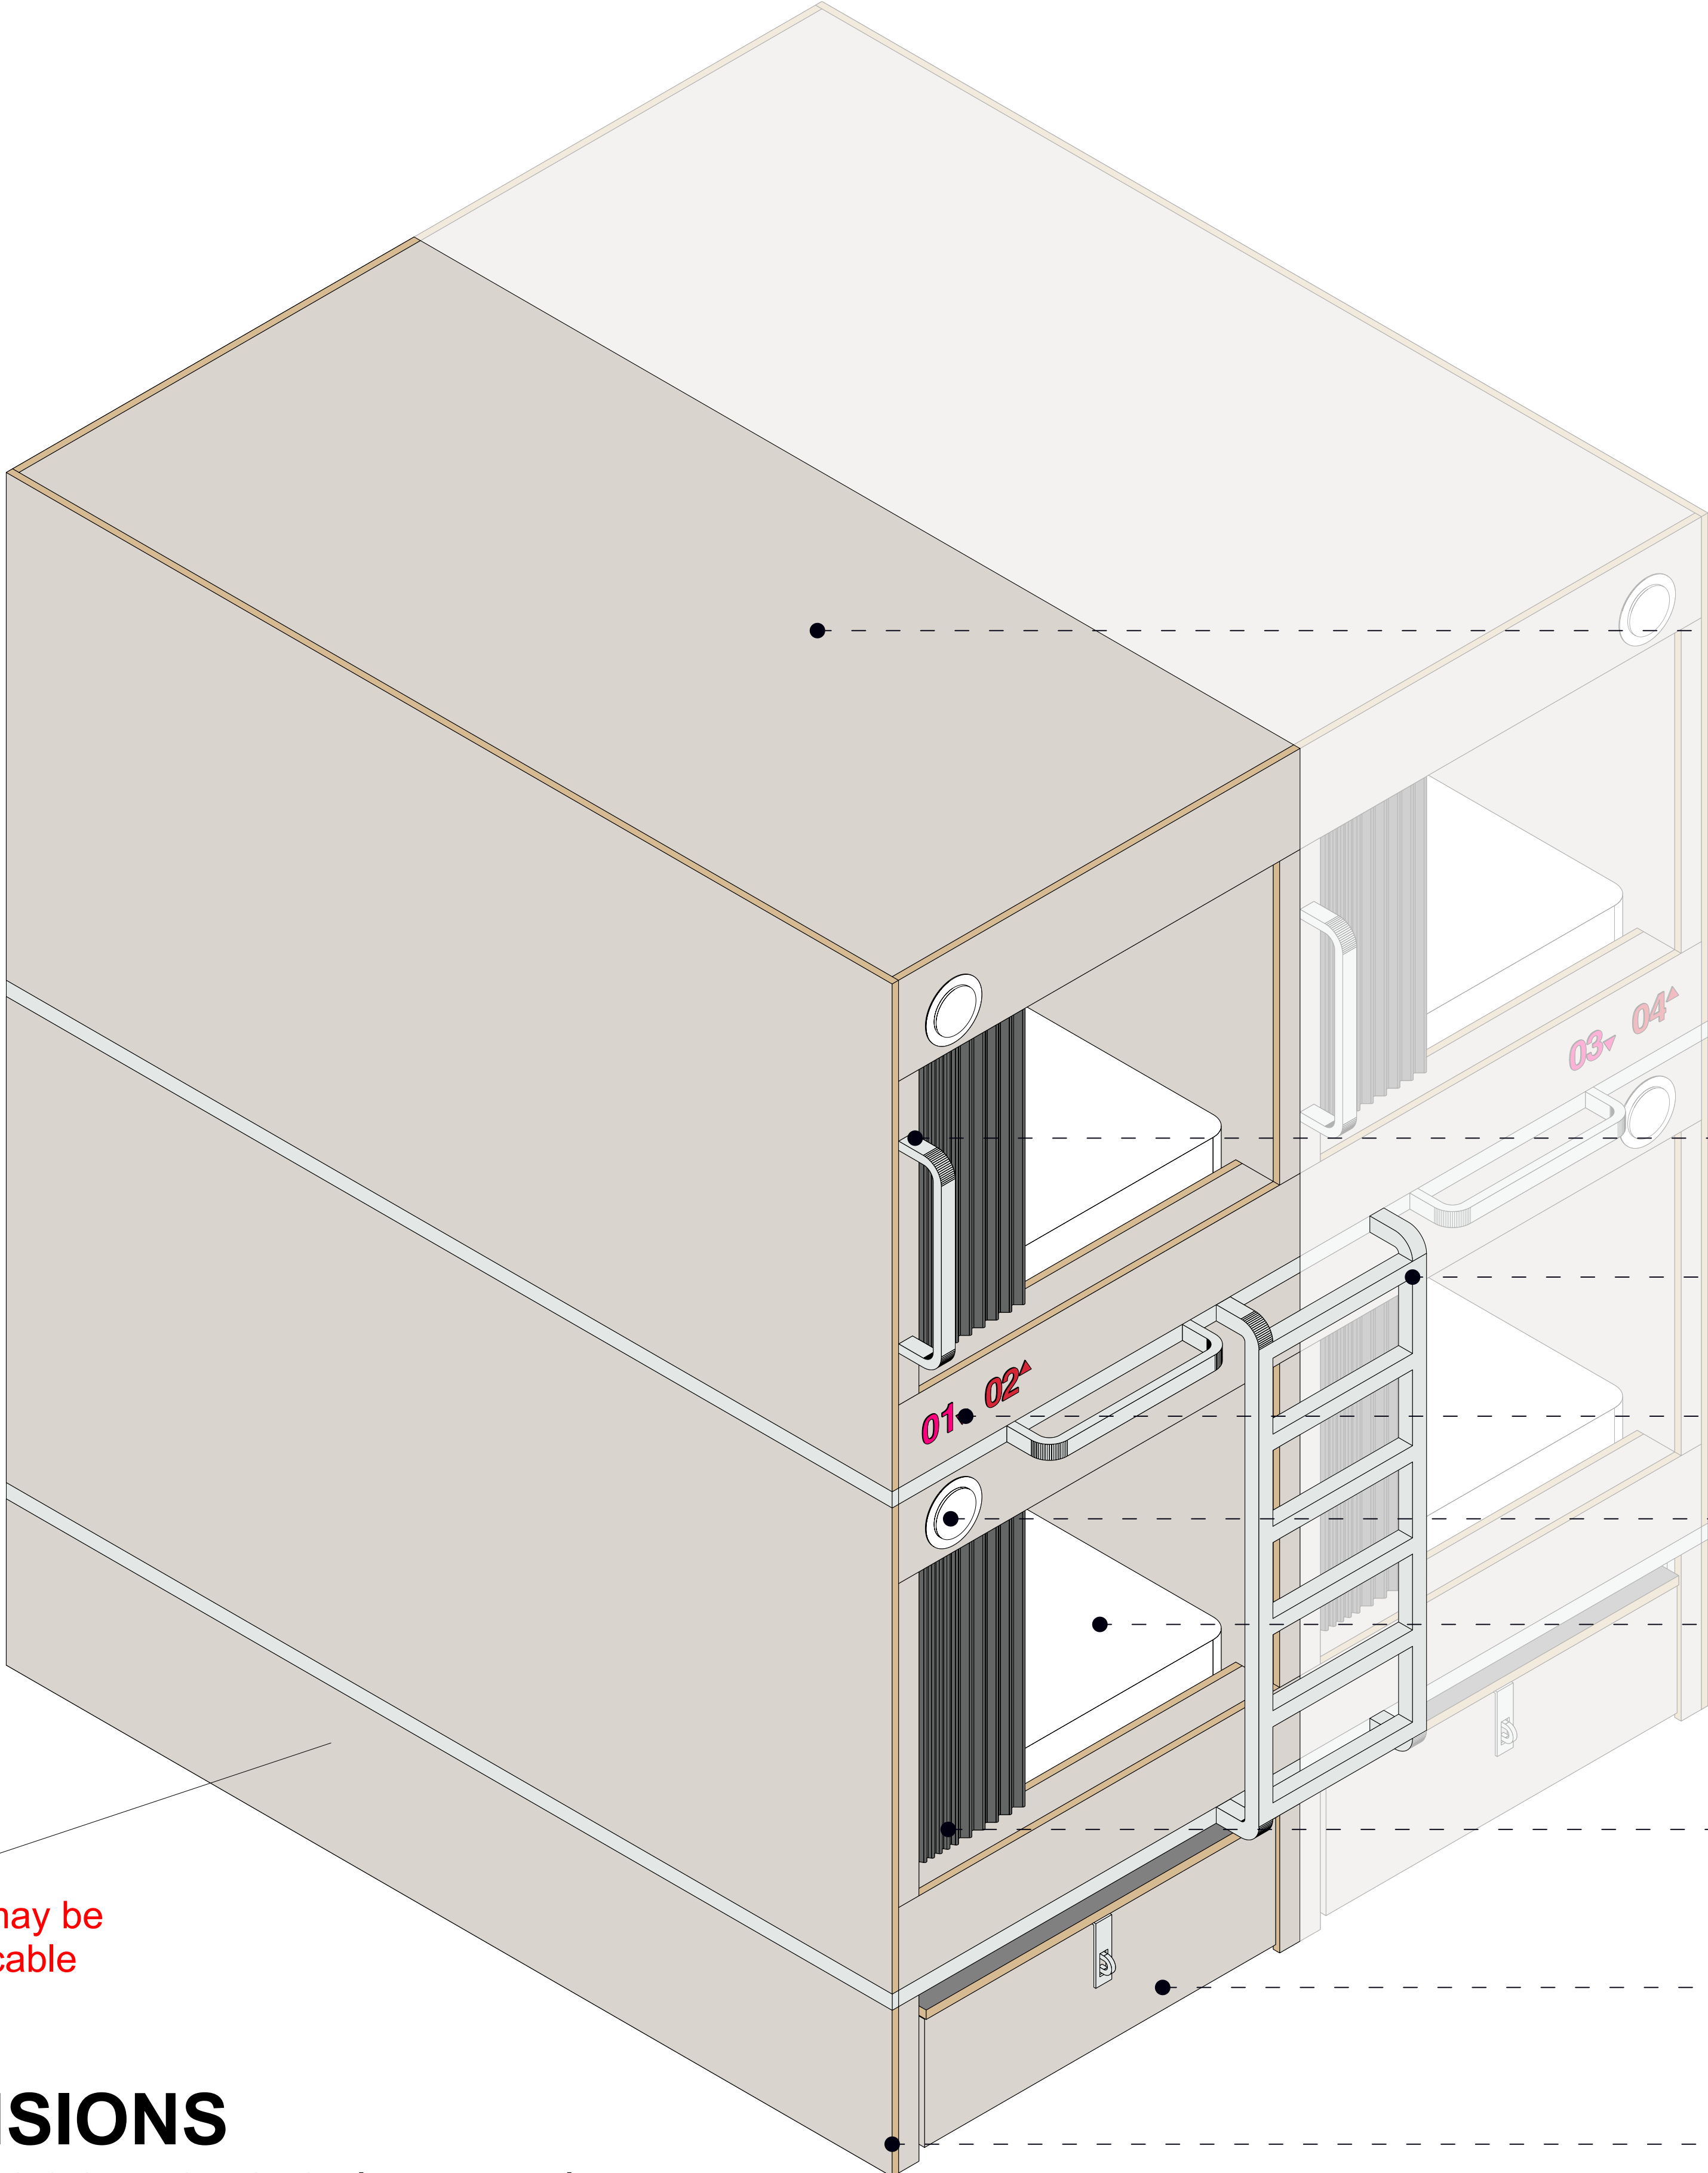

Lower side panels may be removed to allow cable connections.

DIMENSIONS
102.2 x 222 x 259.3 (WxLxH)cm

CC-M01

-Cladding - Laminated chipboard - Colour RAL 7044, Thickness 18m (RAL Colour TBC by Clink)

SS-F/L/G Handrail - 3.5x3.5 cm Powder Coated Steel Structure - Colour to match Telegrey RAL 7047 - Semi gloss finish (RAL Colour TBC by Clink)

SS-F/L/G Ladder - 3.5x3.5 cm Powder Coated Steel Structure - Colour to match Telegrey RAL 7047 - Semi gloss finish (RAL Colour TBC by Clink)

AA-S01 SIGNAGE - Numbers - laser-cut acrylic or MDF - thickness 5mm - spray painted - RAL 3020 Red & RAL 4010 Rose - font according to wayfinding signage design (RAL Colour TBC by Clink)

Ventilation system - Europlast NGA100


FF-M01 Mattress - 90x200x22cm - (Foam Mattress - Fire retardant fabric and foam (Crib 5) - 100gr/m2 polyester - Reinforcement - Cover should be washable on 40 degrees) FINAL MATTRESS HEIGHT TBC (18/20/22cm)

FF-C01 Metal ring curtains with a sturdy/durable pole
Privacy curtain - washable textile - colour: dark grey/ anthracite less fold - Almost 1:1 fold factor to open horizontally - fire-retardant fabric LUNA BLACKOUT by SKOPOS - TEXTURED L15 GUNMETAL (Colour TBC by Clink)

Lockers 70 x 88 x 33 (W x D x H)cm

CC-M07 Visible Edges
Plywood edges


PODS - TYPE 2-P - GA PLAN

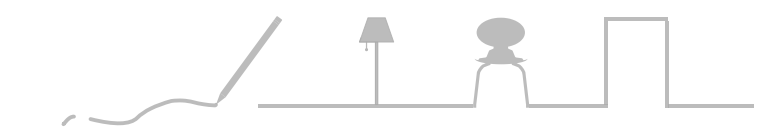

KEY

Index

A) 04.05.2026 Plan Set UP

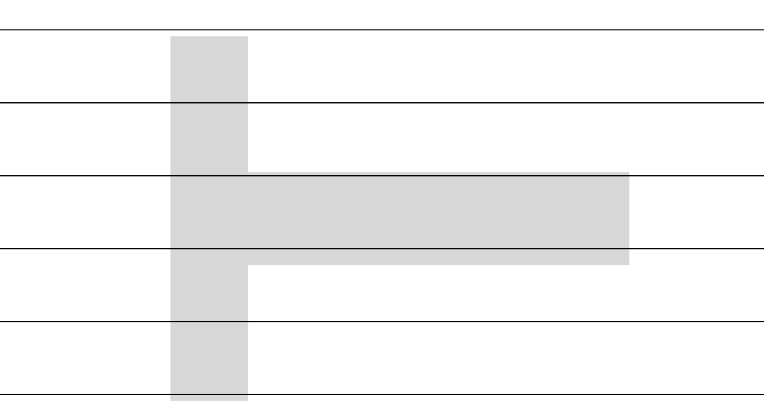

All measurements have to be verified according to existing conditions by the contractor! Discrepancies must be reported immediately to the responsible project manager. The contractor has to produce fully dimensioned shop drawings prior to the start of the contract and they have to be approved by the client/ investor / interior designer

Project
CLINK 78 - BEDS



Project Address
CLINK 78
78 King's Cross Rd
London WC1X 9QG
United Kingdom

Client's Address
CLINK 78
78 King's Cross Rd
London WC1X 9QG
United Kingdom

Sheet Number	2-P-501	Total Sheets	82
--------------	---------	--------------	----


Sheet Title	POD 2-P GA	Level	
-------------	------------	-------	--

File Name
260425_CLINK 78_BEDs AA DRAFT 03.vwx

Date	Sheet Size	Scale	Signed
28.04.26	A1	1:5	AA

Stefanie Jaensch INTERIOR DESIGNS
Global Headquarter | Stefanie Jaensch c/o WeWork
Taubusanlage 8 | 60329 Frankfurt a.M.
E-Mail info@stefaniejaensch.de | DE +49 (0) 174 6756098
www.stefaniejaensch.de
Legal address | Stefanie Jaensch | Offenbacher Landstraße 434 | 60599 Frankfurt a.M.
© 2023 All Rights Reserved | Stefanie Jaensch

PODS - TYPE 2-P - FRONT ELEVATION

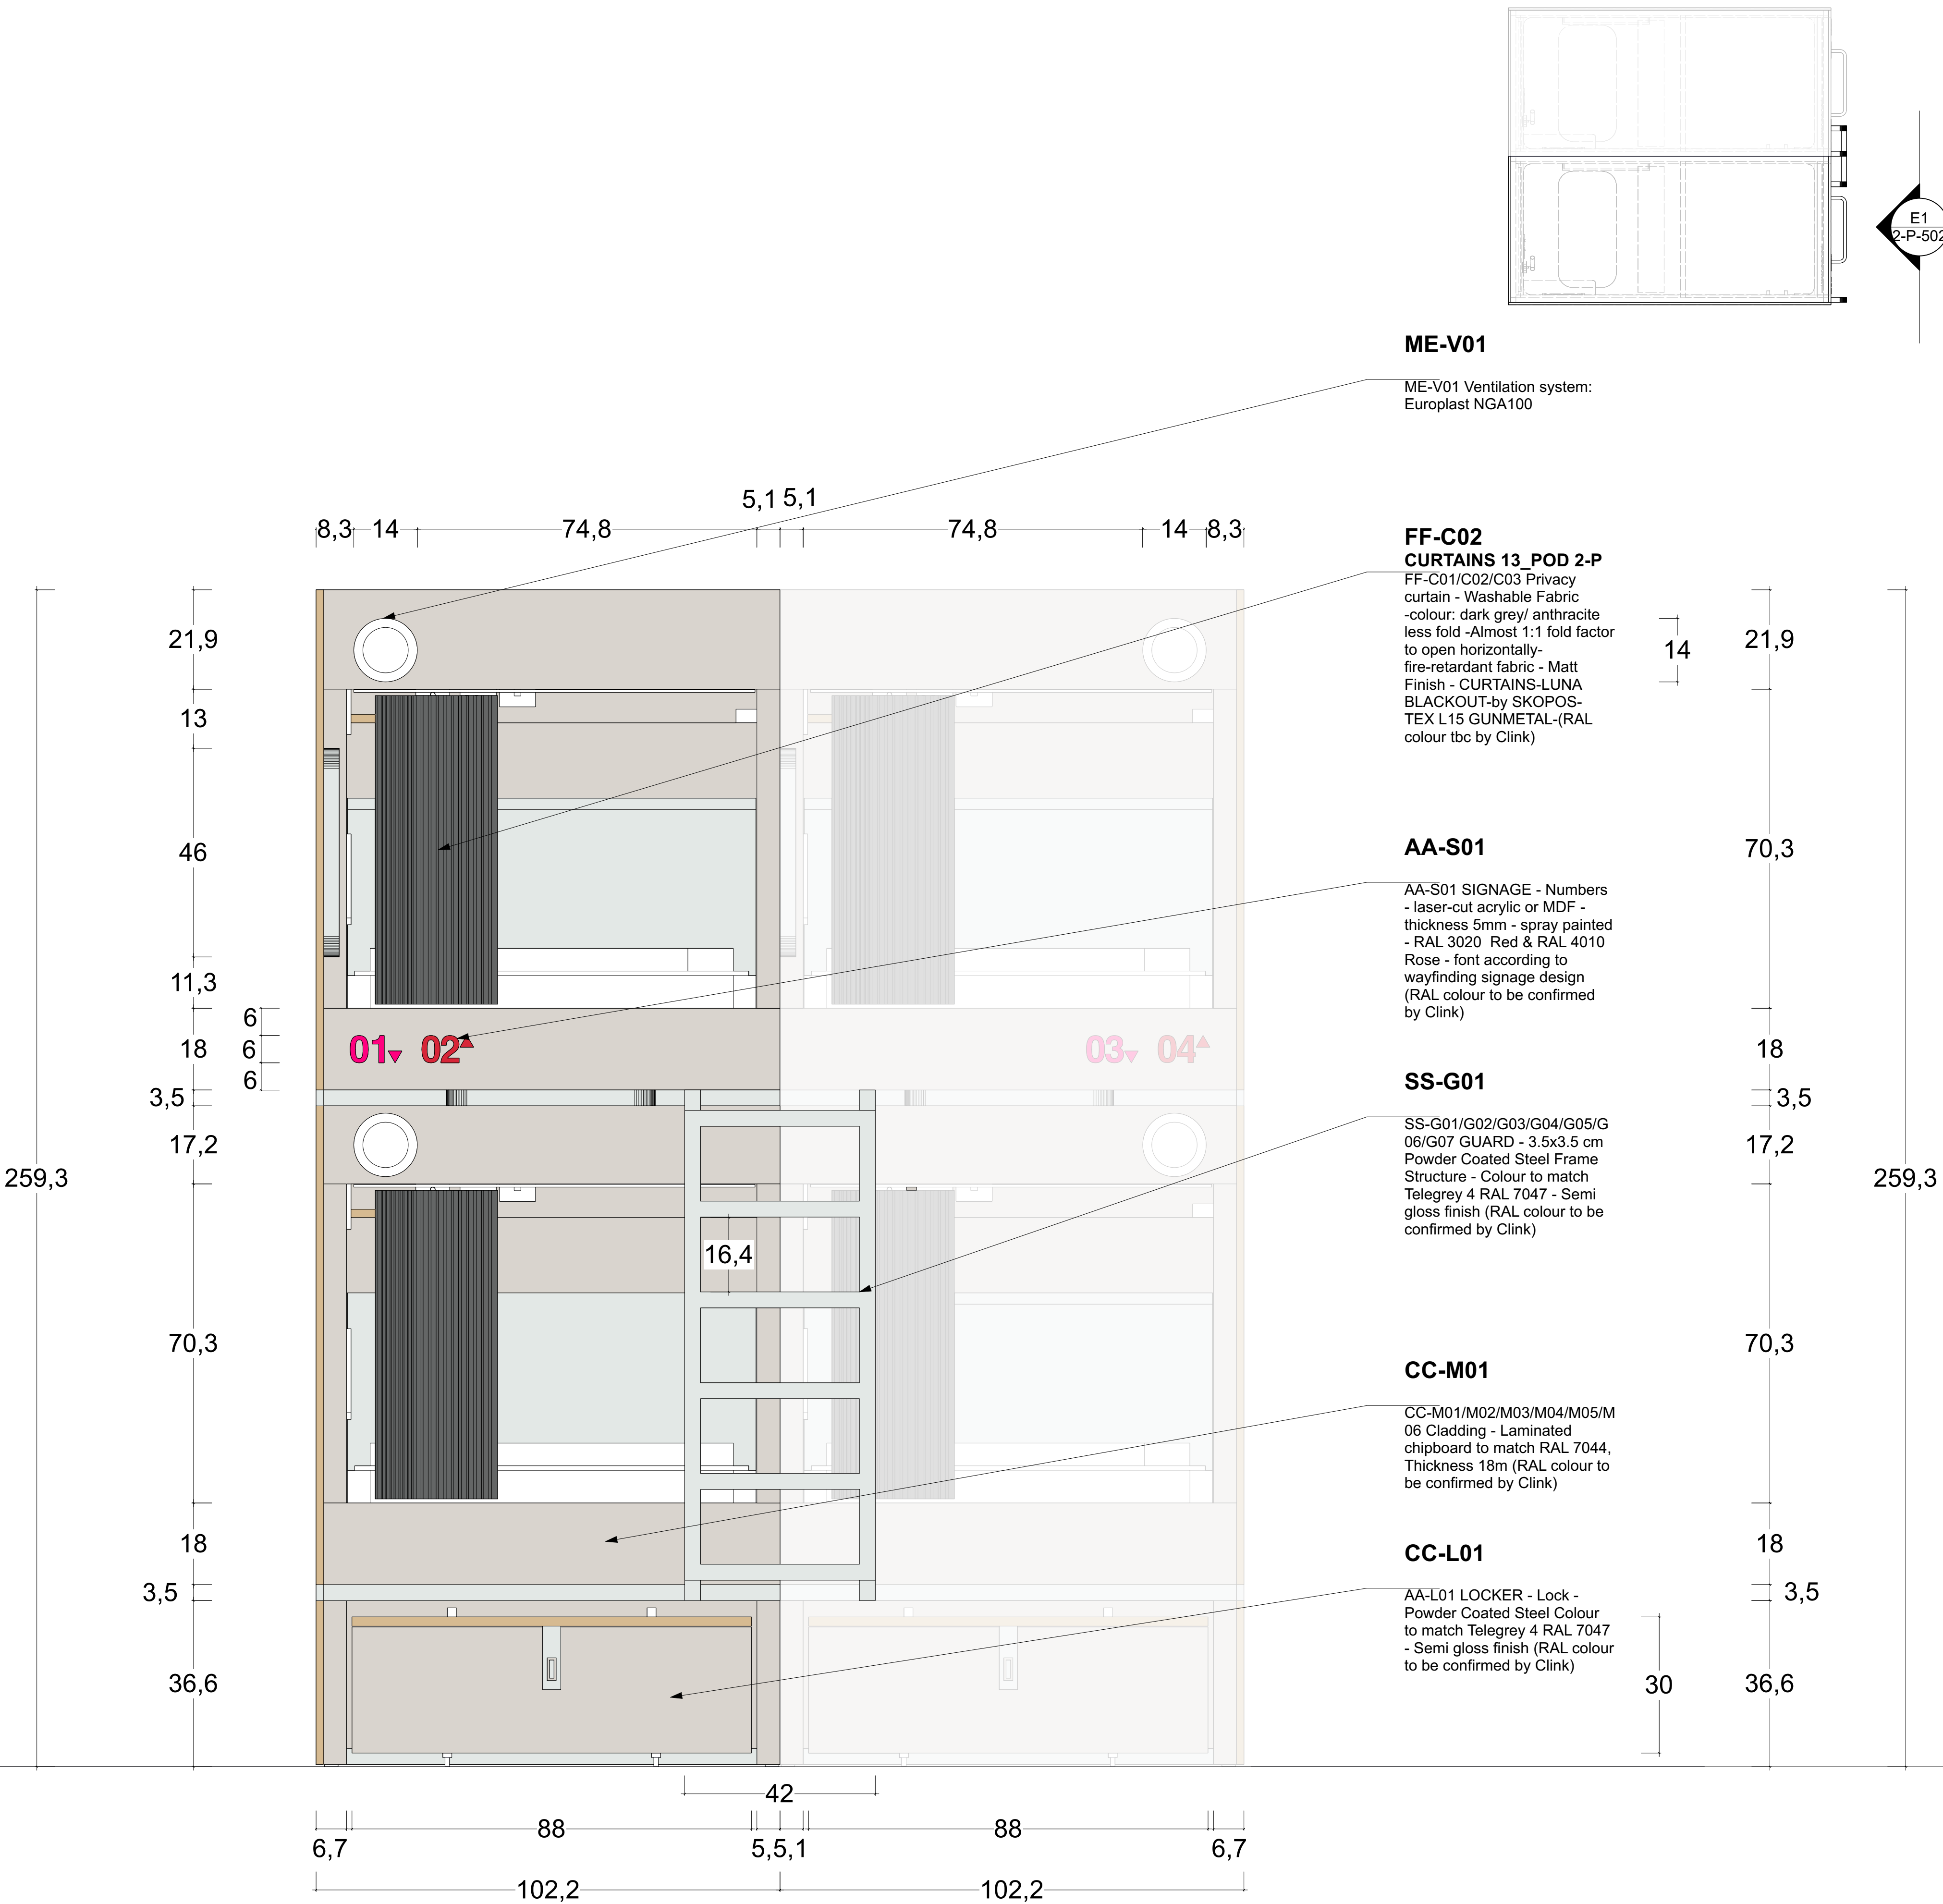

KEY

Index

A) 04.05.2026 Plan Set UP

All measurements have to be verified according to existing conditions by the contractor! Discrepancies must be reported immediately to the responsible project manager. The contractor has to produce fully dimensioned shop drawings prior to the start of the contract and they have to be approved by the client/ investor / interior designer

Project

CLINK 78 - BEDS

Logo



Project Address

CLINK 78
78 King's Cross Rd
London WC1X 9QG
United Kingdom

Client's Address

CLINK 78
78 King's Cross Rd
London WC1X 9QG
United Kingdom

Sheet Number 2-P-502

Total Sheets 82

Sheet Title
POD 2-P FRONT ELEVATION

Level

File Name

260425_CLINK 78_BEDs AA DRAFT 03.vwx

Date
28.04.26

Sheet Size
A1

Scale
1:8

Signed
AA

Stefanie Jaensch INTERIOR DESIGNS




Global Headquarter | Stefanie Jaensch c/o WeWork
Taubusanlage 8 | 60329 Frankfurt a.M.
E-Mail info@stefaniejaensch.de | DE +49 (0) 174 6756098
www.stefaniejaensch.de

Legal address | Stefanie Jaensch | Offenbacher Landstraße 434 | 60599 Frankfurt a.M.
© 2023 All Rights Reserved | Stefanie Jaensch

E1

POD 2-P FRONT ELEVATION
Scale: 1:8

PODS - TYPE 2-P - BACK ELEVATION

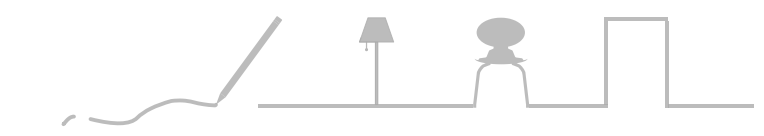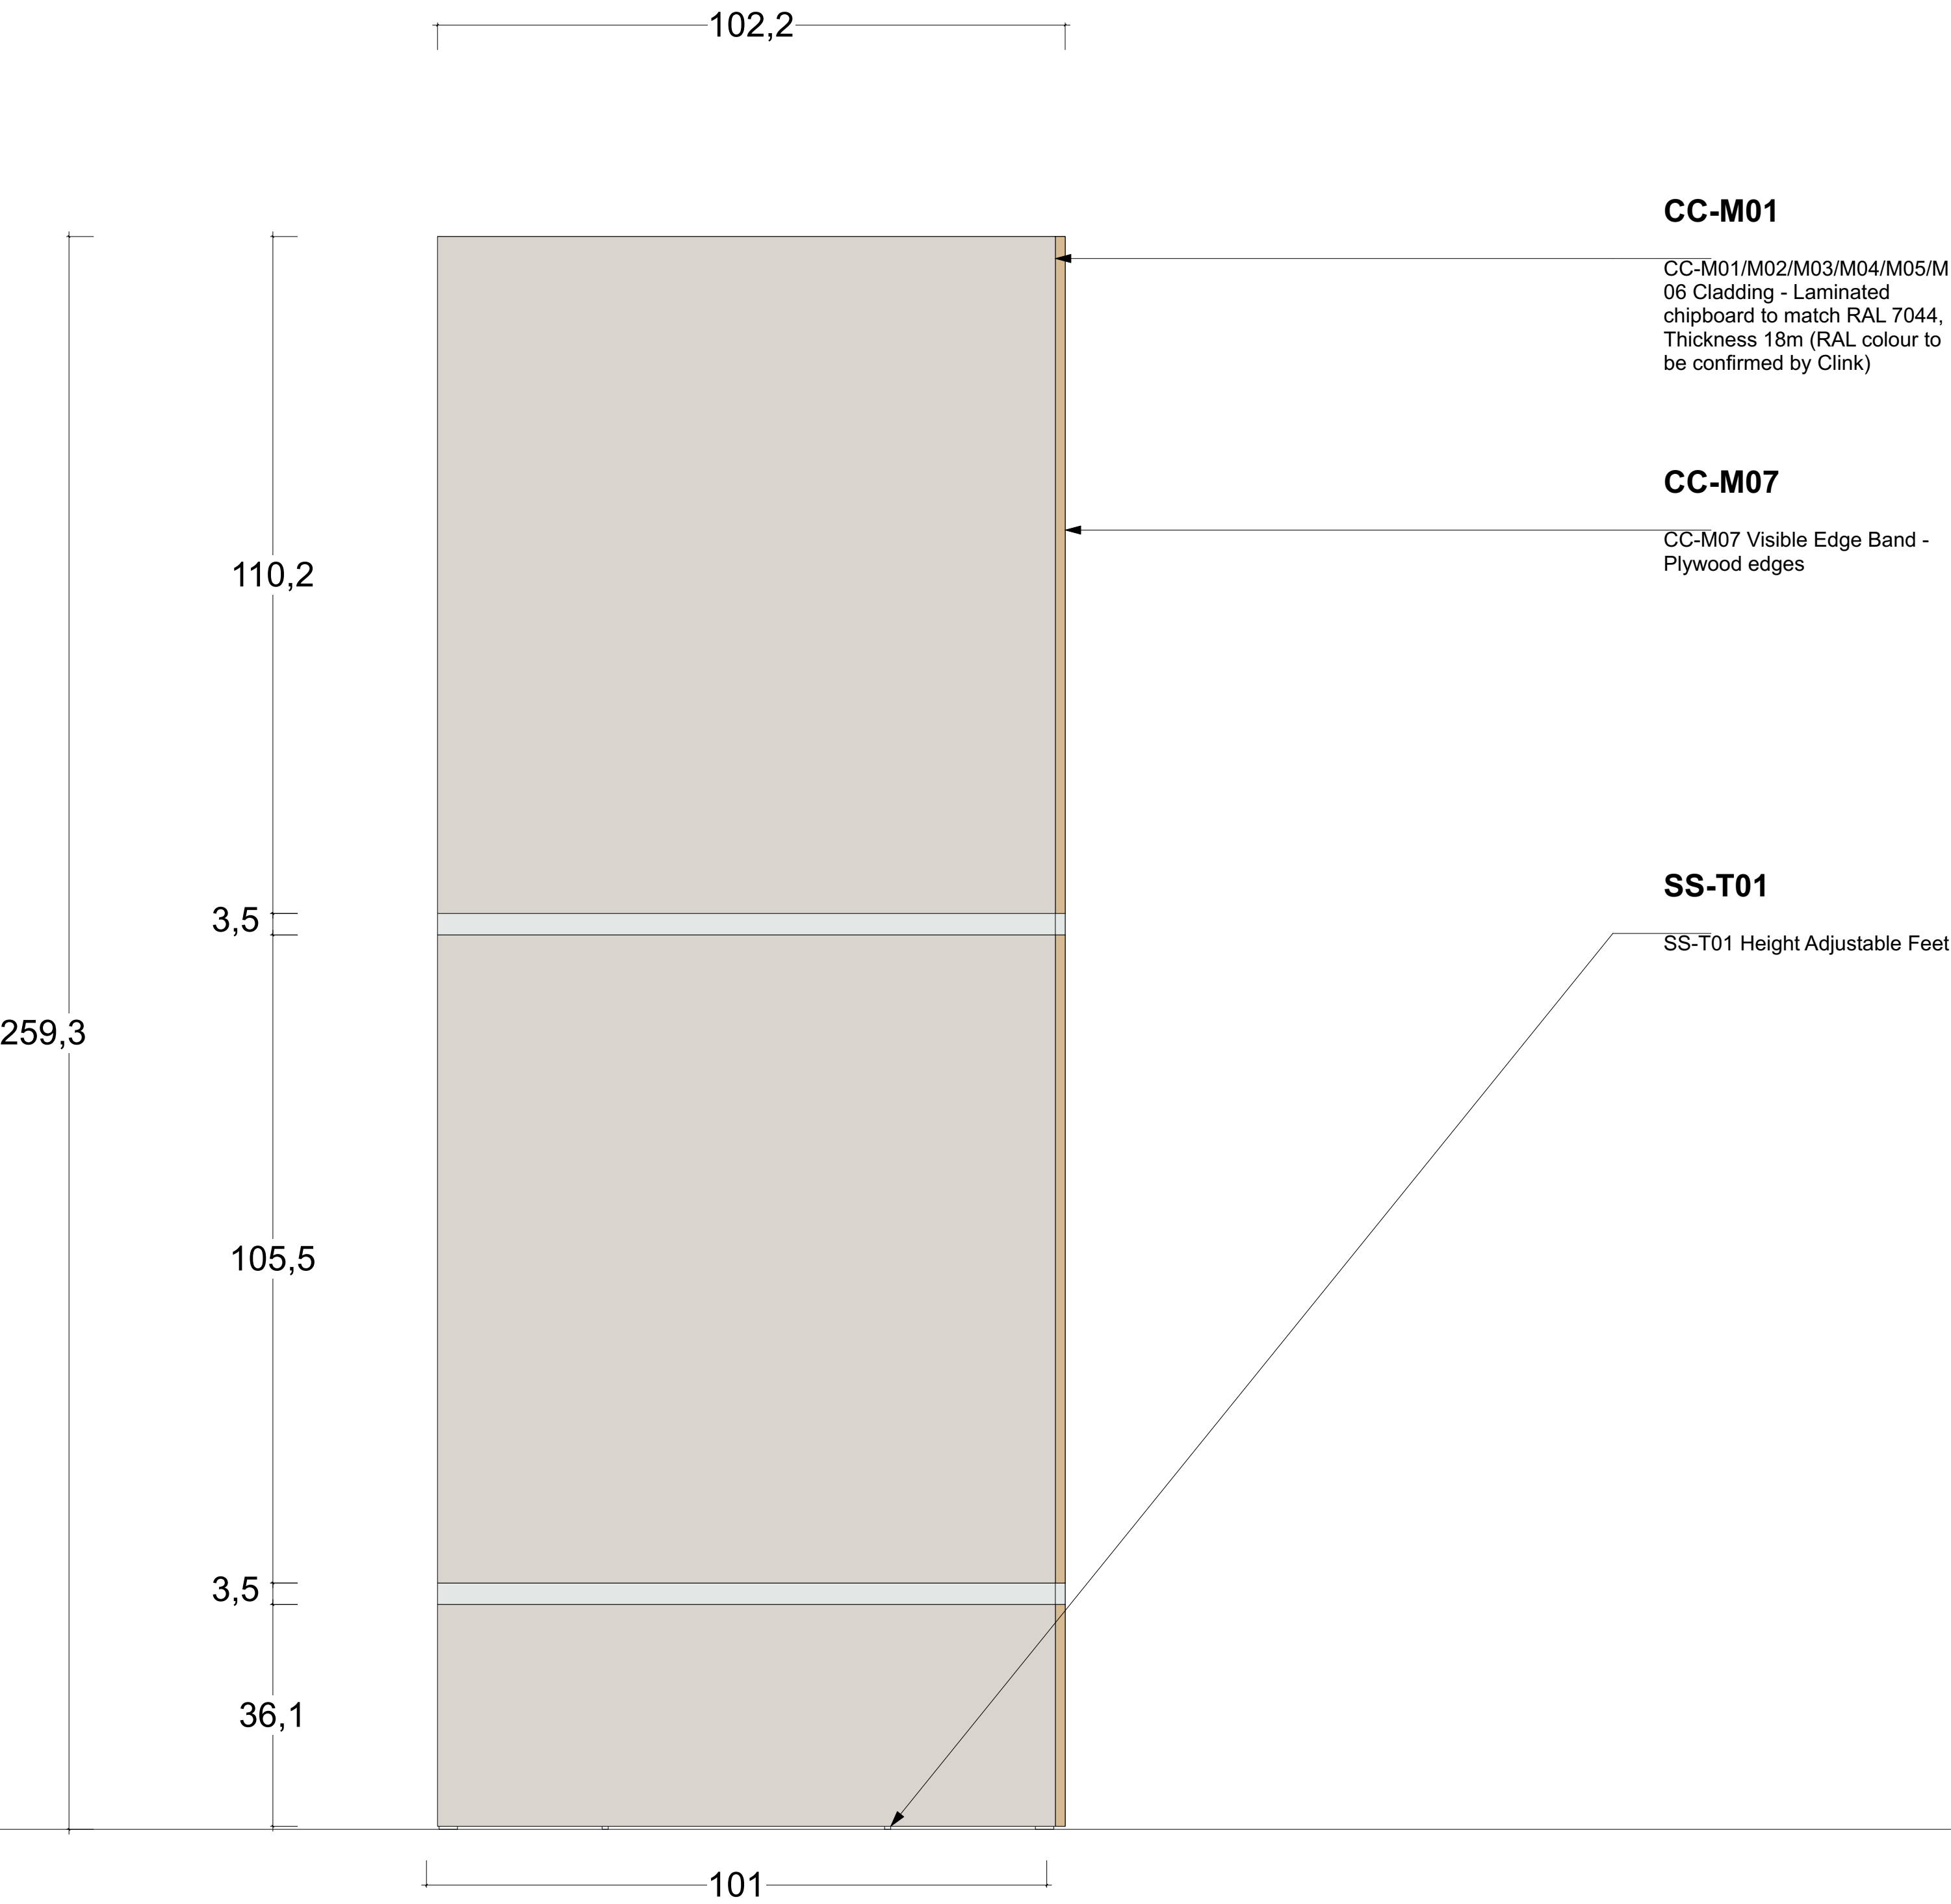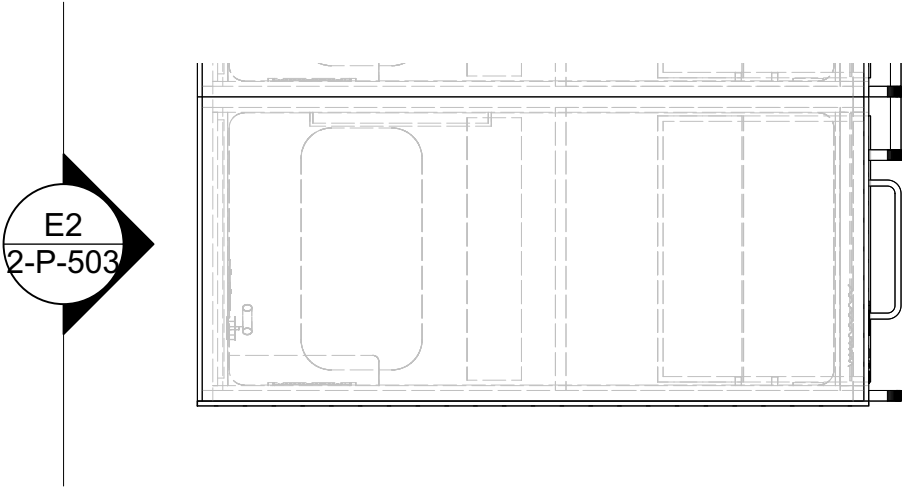

KEY

Index

A) 04.05.2026 Plan Set UP

All measurements have to be verified according to existing conditions by the contractor! Discrepancies must be reported immediately to the responsible project manager. The contractor has to produce fully dimensioned shop drawings prior to the start of the contract and they have to be approved by the client/ investor / interior designer

Project
CLINK 78 - BEDS



Project Address
CLINK 78
78 King's Cross Rd
London WC1X 9QG
United Kingdom

Client's Address
CLINK 78
78 King's Cross Rd
London WC1X 9QG
United Kingdom




Sheet Number	2-P-503	Total Sheets	82
--------------	---------	--------------	----

Sheet Title	Level
POD 2-P BACK ELEVATION	

File Name
260425_CLINK 78_BEDs AA DRAFT 03.vwx

Date	Sheet Size	Scale	Signed
28.04.26	A1	1:8	AA

PODS - TYPE 2-P - RIGHT ELEVATION

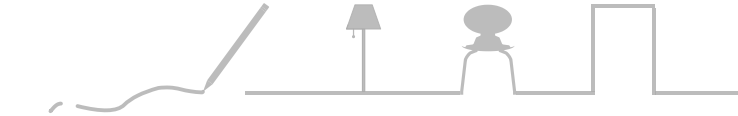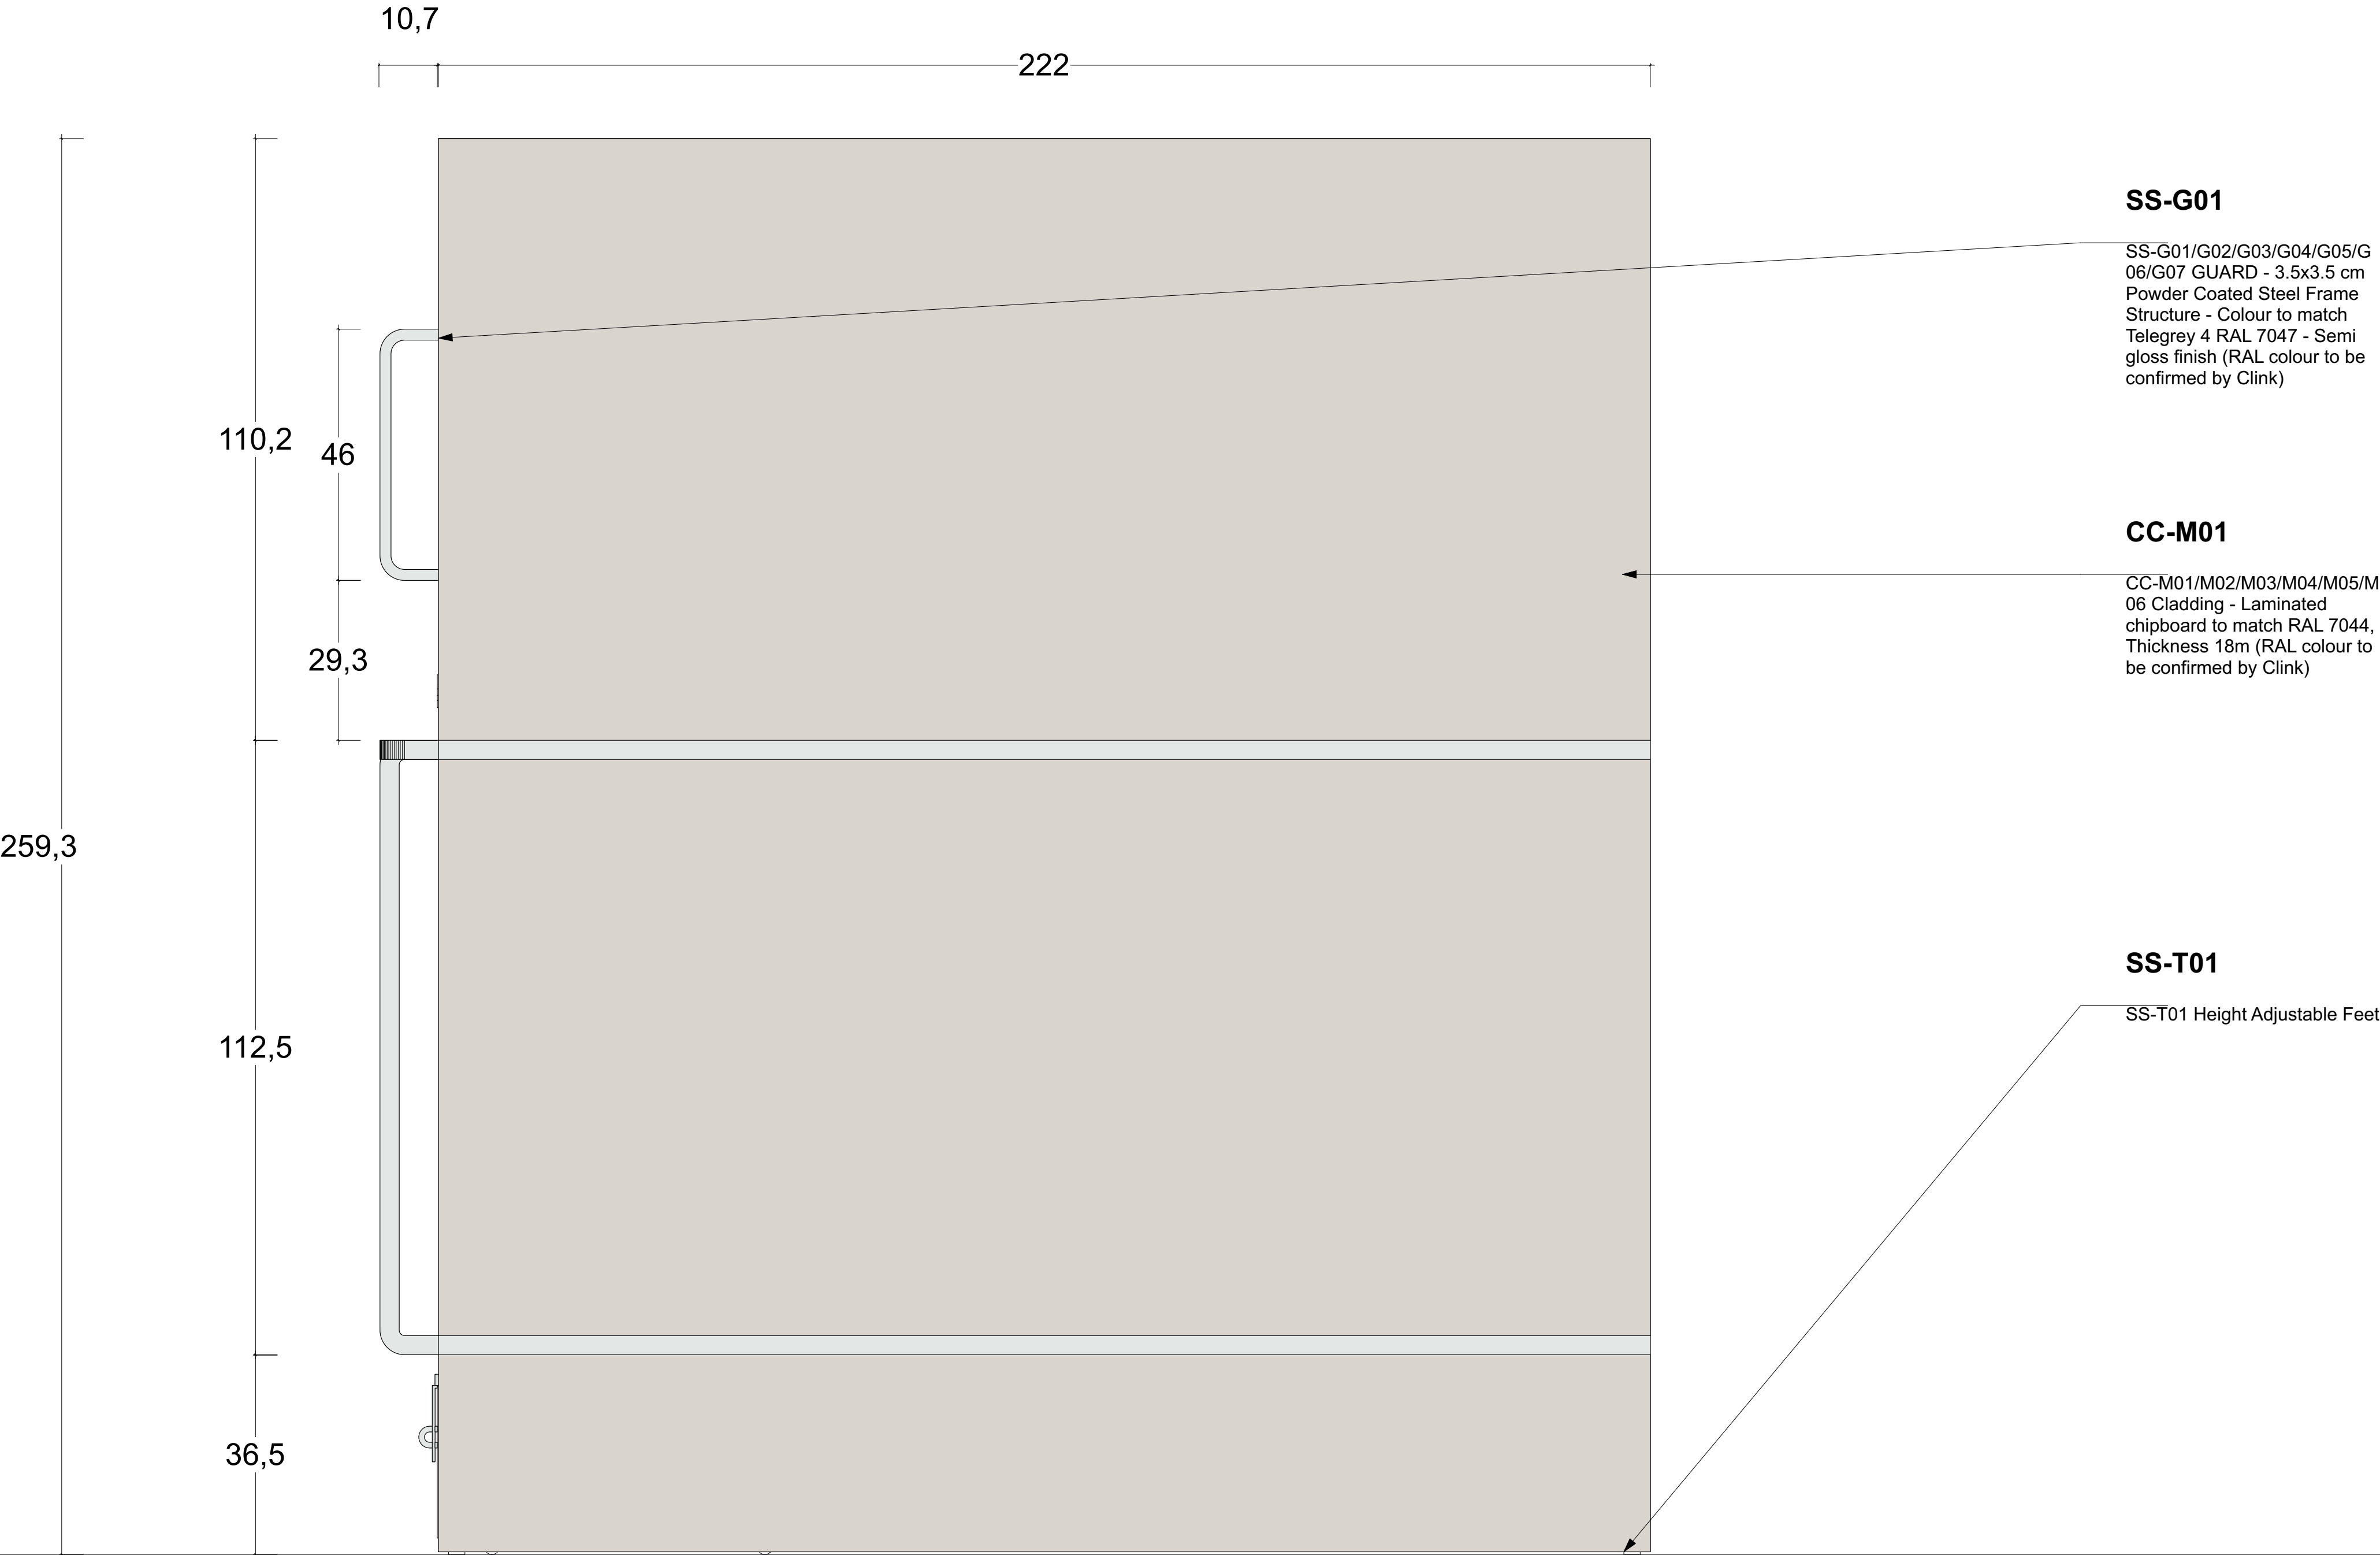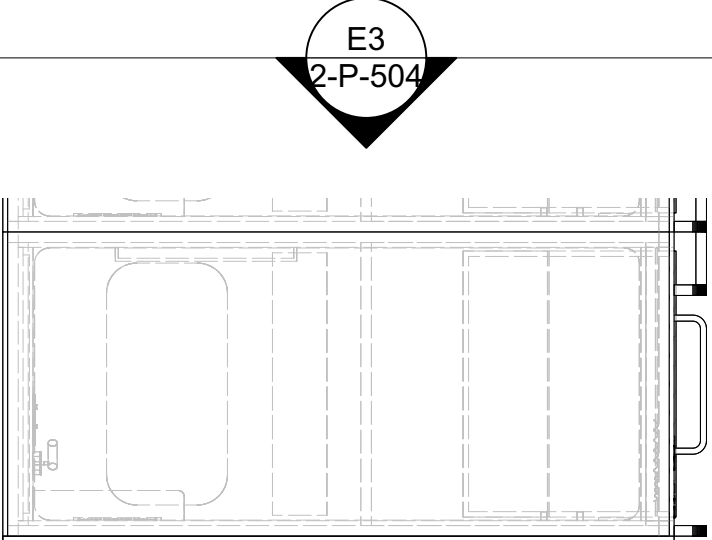

KEY

Index

A) 04.05.2026 Plan Set UP

All measurements have to be verified according to existing conditions by the contractor! Discrepancies must be reported immediately to the responsible project manager. The contractor has to produce fully dimensioned shop drawings prior to the start of the contract and they have to be approved by the client/ investor / interior designer

Project

CLINK 78 - BEDS

Logo



Project Address

CLINK 78
78 King's Cross Rd
London WC1X 9QG
United Kingdom

Client's Address



CLINK 78
78 King's Cross Rd
London WC1X 9QG
United Kingdom

Sheet Number 2-P-504		Total Sheets 82
Sheet Title POD 2-P RIGHT ELEVATION		Level
File Name 260425_CLINK 78_BEDs AA DRAFT 03.vwx		

Date	Sheet Size	Scale	Signed
28.04.26	A1	1:8	AA

Stefanie Jaensch INTERIOR DESIGNS
Global Headquarter | Stefanie Jaensch c/o WeWork
Taubusanlage 8 | 60329 Frankfurt a.M.
E-Mail info@stefaniejaensch.de | DE +49 (0) 174 6756098
www.stefaniejaensch.de
Legal address | Stefanie Jaensch | Offenbacher Landstraße 434 | 60599 Frankfurt a.M.
© 2023 All Rights Reserved | Stefanie Jaensch

PODS - TYPE 2-P - LEFT ELEVATION

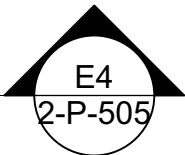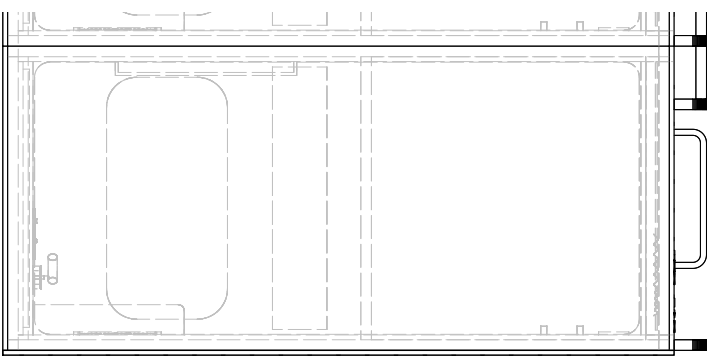

KEY

Index

A) 04.05.2026 Plan Set UP

All measurements have to be verified according to existing conditions by the contractor! Discrepancies must be reported immediately to the responsible project manager. The contractor has to produce fully dimensioned shop drawings prior to the start of the contract and they have to be approved by the client/ investor / interior designer

Project
CLINK 78 - BEDS




Project Address
CLINK 78
78 King's Cross Rd
London WC1X 9QG
United Kingdom


Client's Address
CLINK 78
78 King's Cross Rd
London WC1X 9QG
United Kingdom

Sheet Number 2-P-505		Total Sheets 82	
Sheet Title POD 2-P LEFT ELEVATION		Level	
File Name 260425_CLINK 78_BEDs AA DRAFT 03.vwx			
Date 28.04.26	Sheet Size A1	Scale 1:8	Signed AA

Stefanie Jaensch INTERIOR DESIGNS
Global Headquarter | Stefanie Jaensch c/o WeWork
Taubusanlage 8 | 60329 Frankfurt a.M.
E-Mail info@stefaniejaensch.de | DE +49 (0) 174 6756098
www.stefaniejaensch.de
Legal address | Stefanie Jaensch | Offenbacher Landstraße 434 | 60599 Frankfurt a.M.
© 2023 All Rights Reserved | Stefanie Jaensch

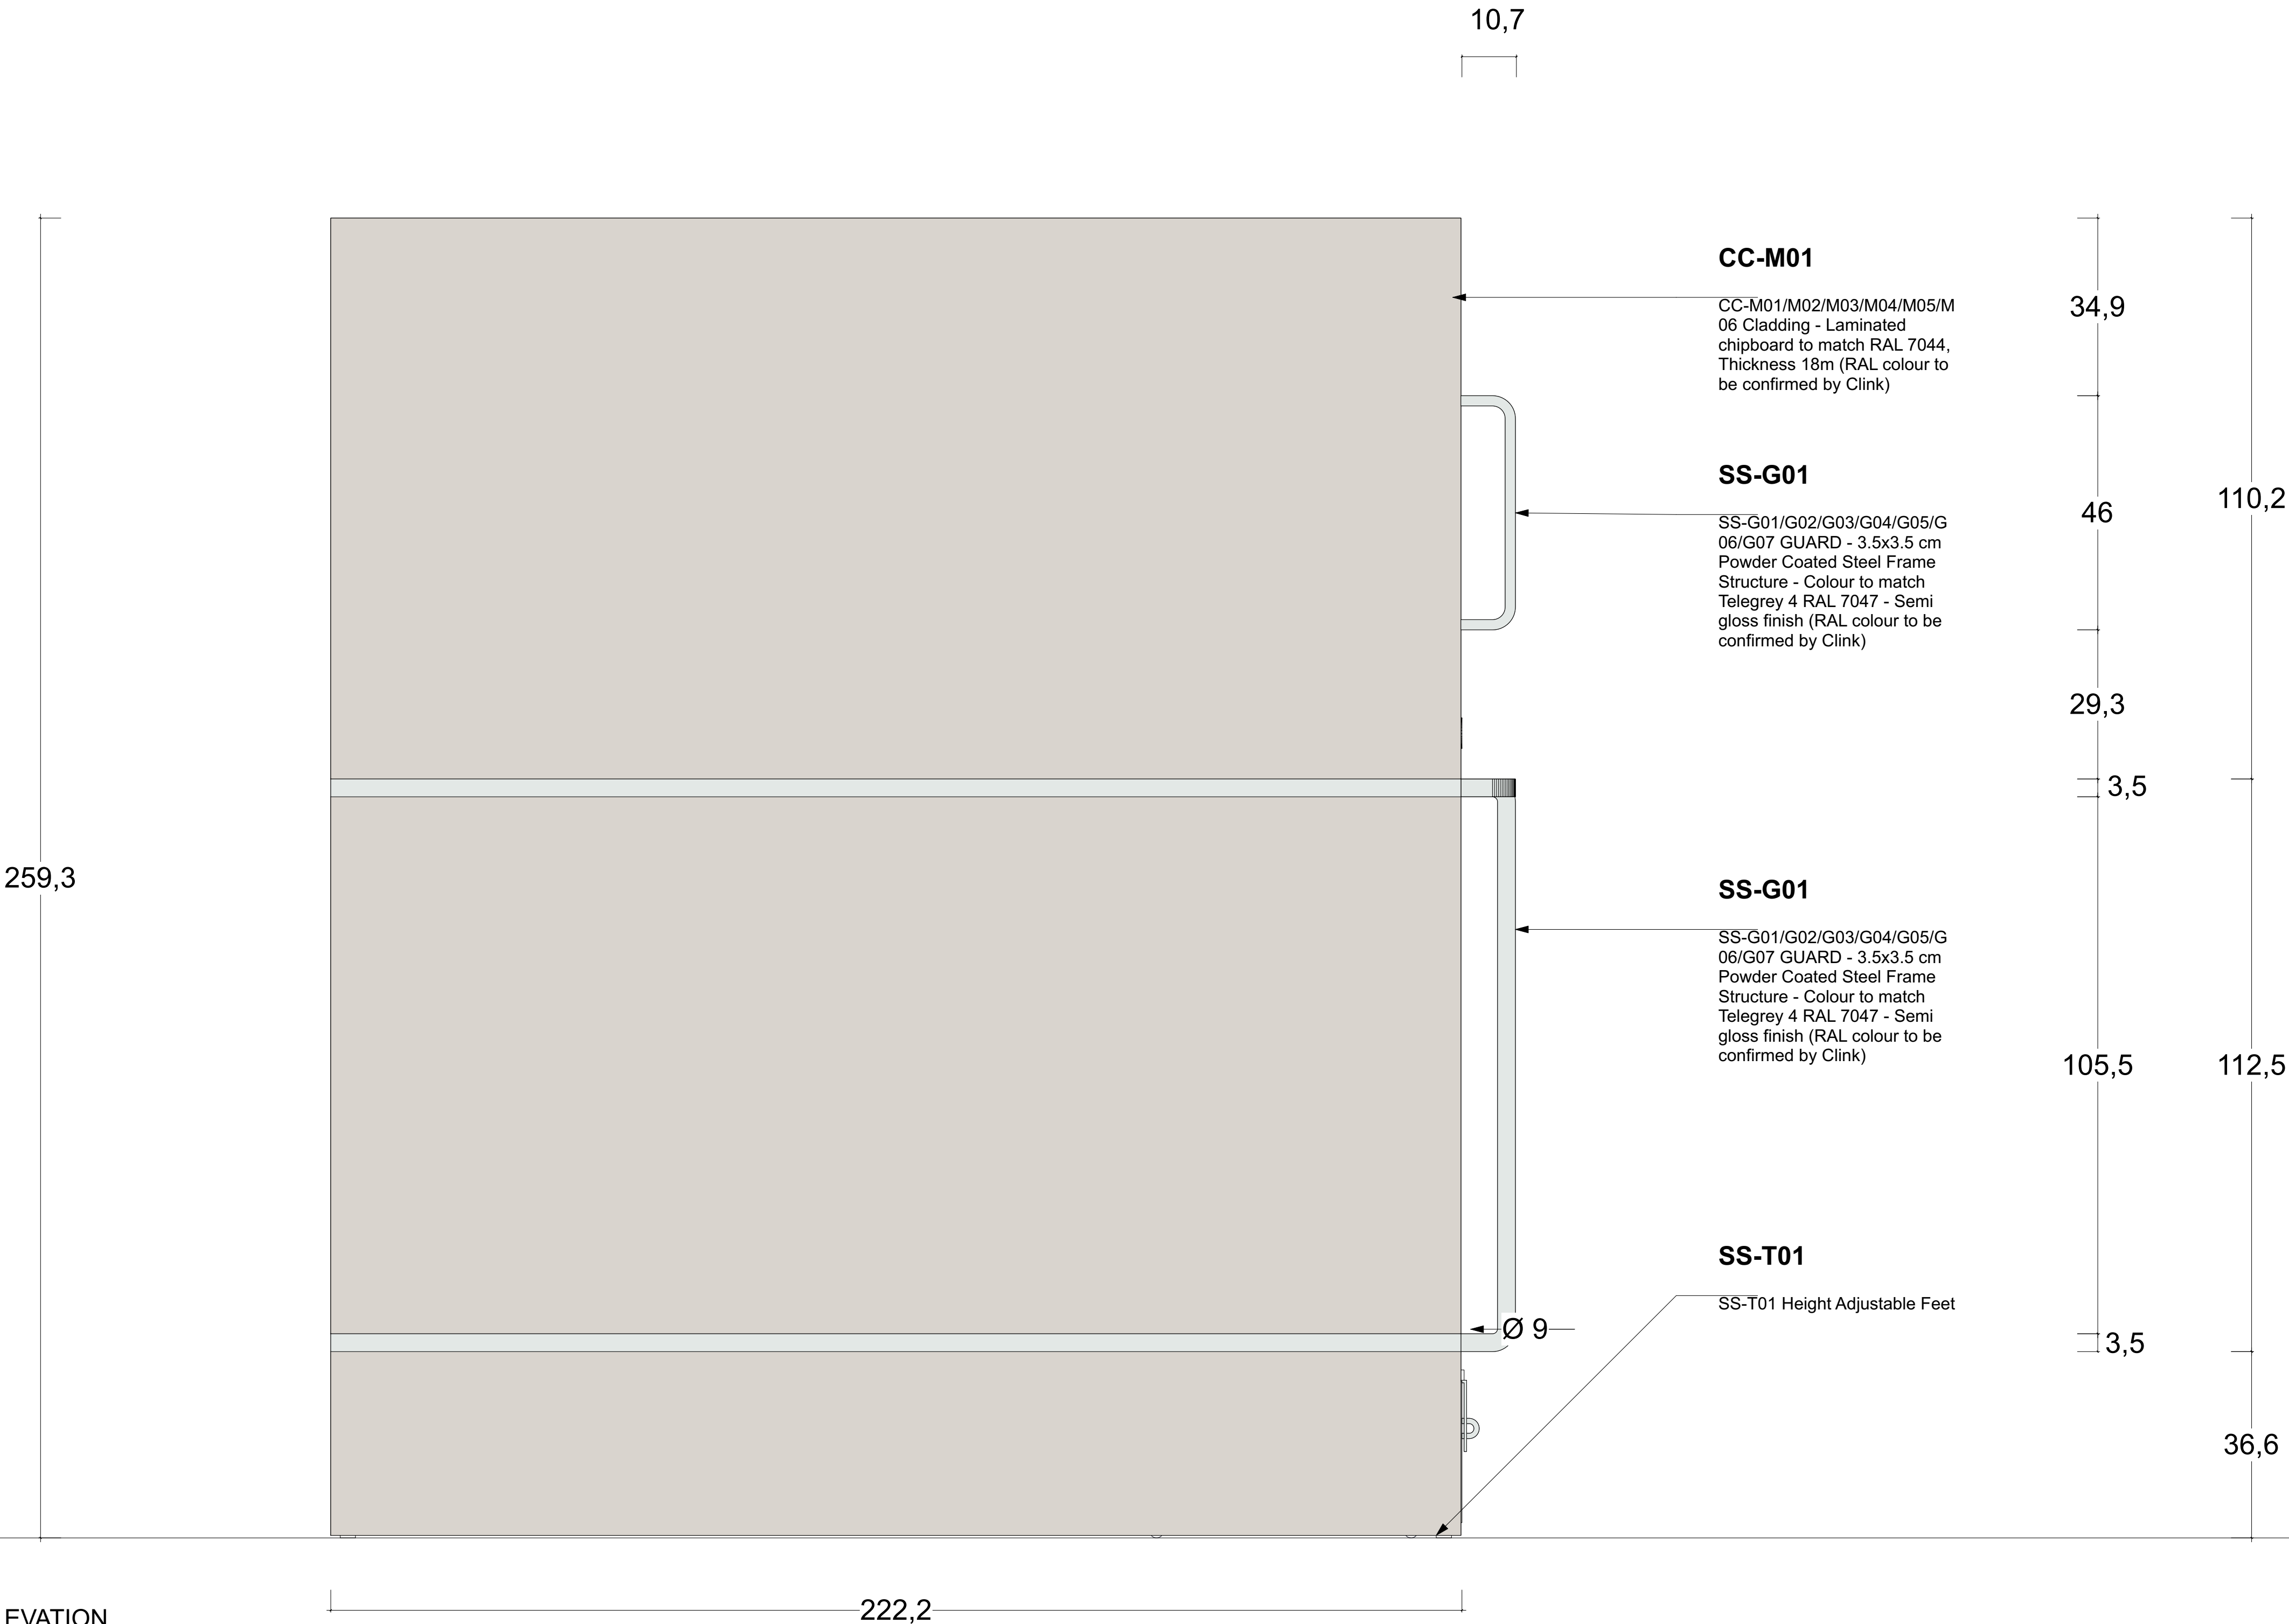

PODS - TYPE 2-P - SECTION 1

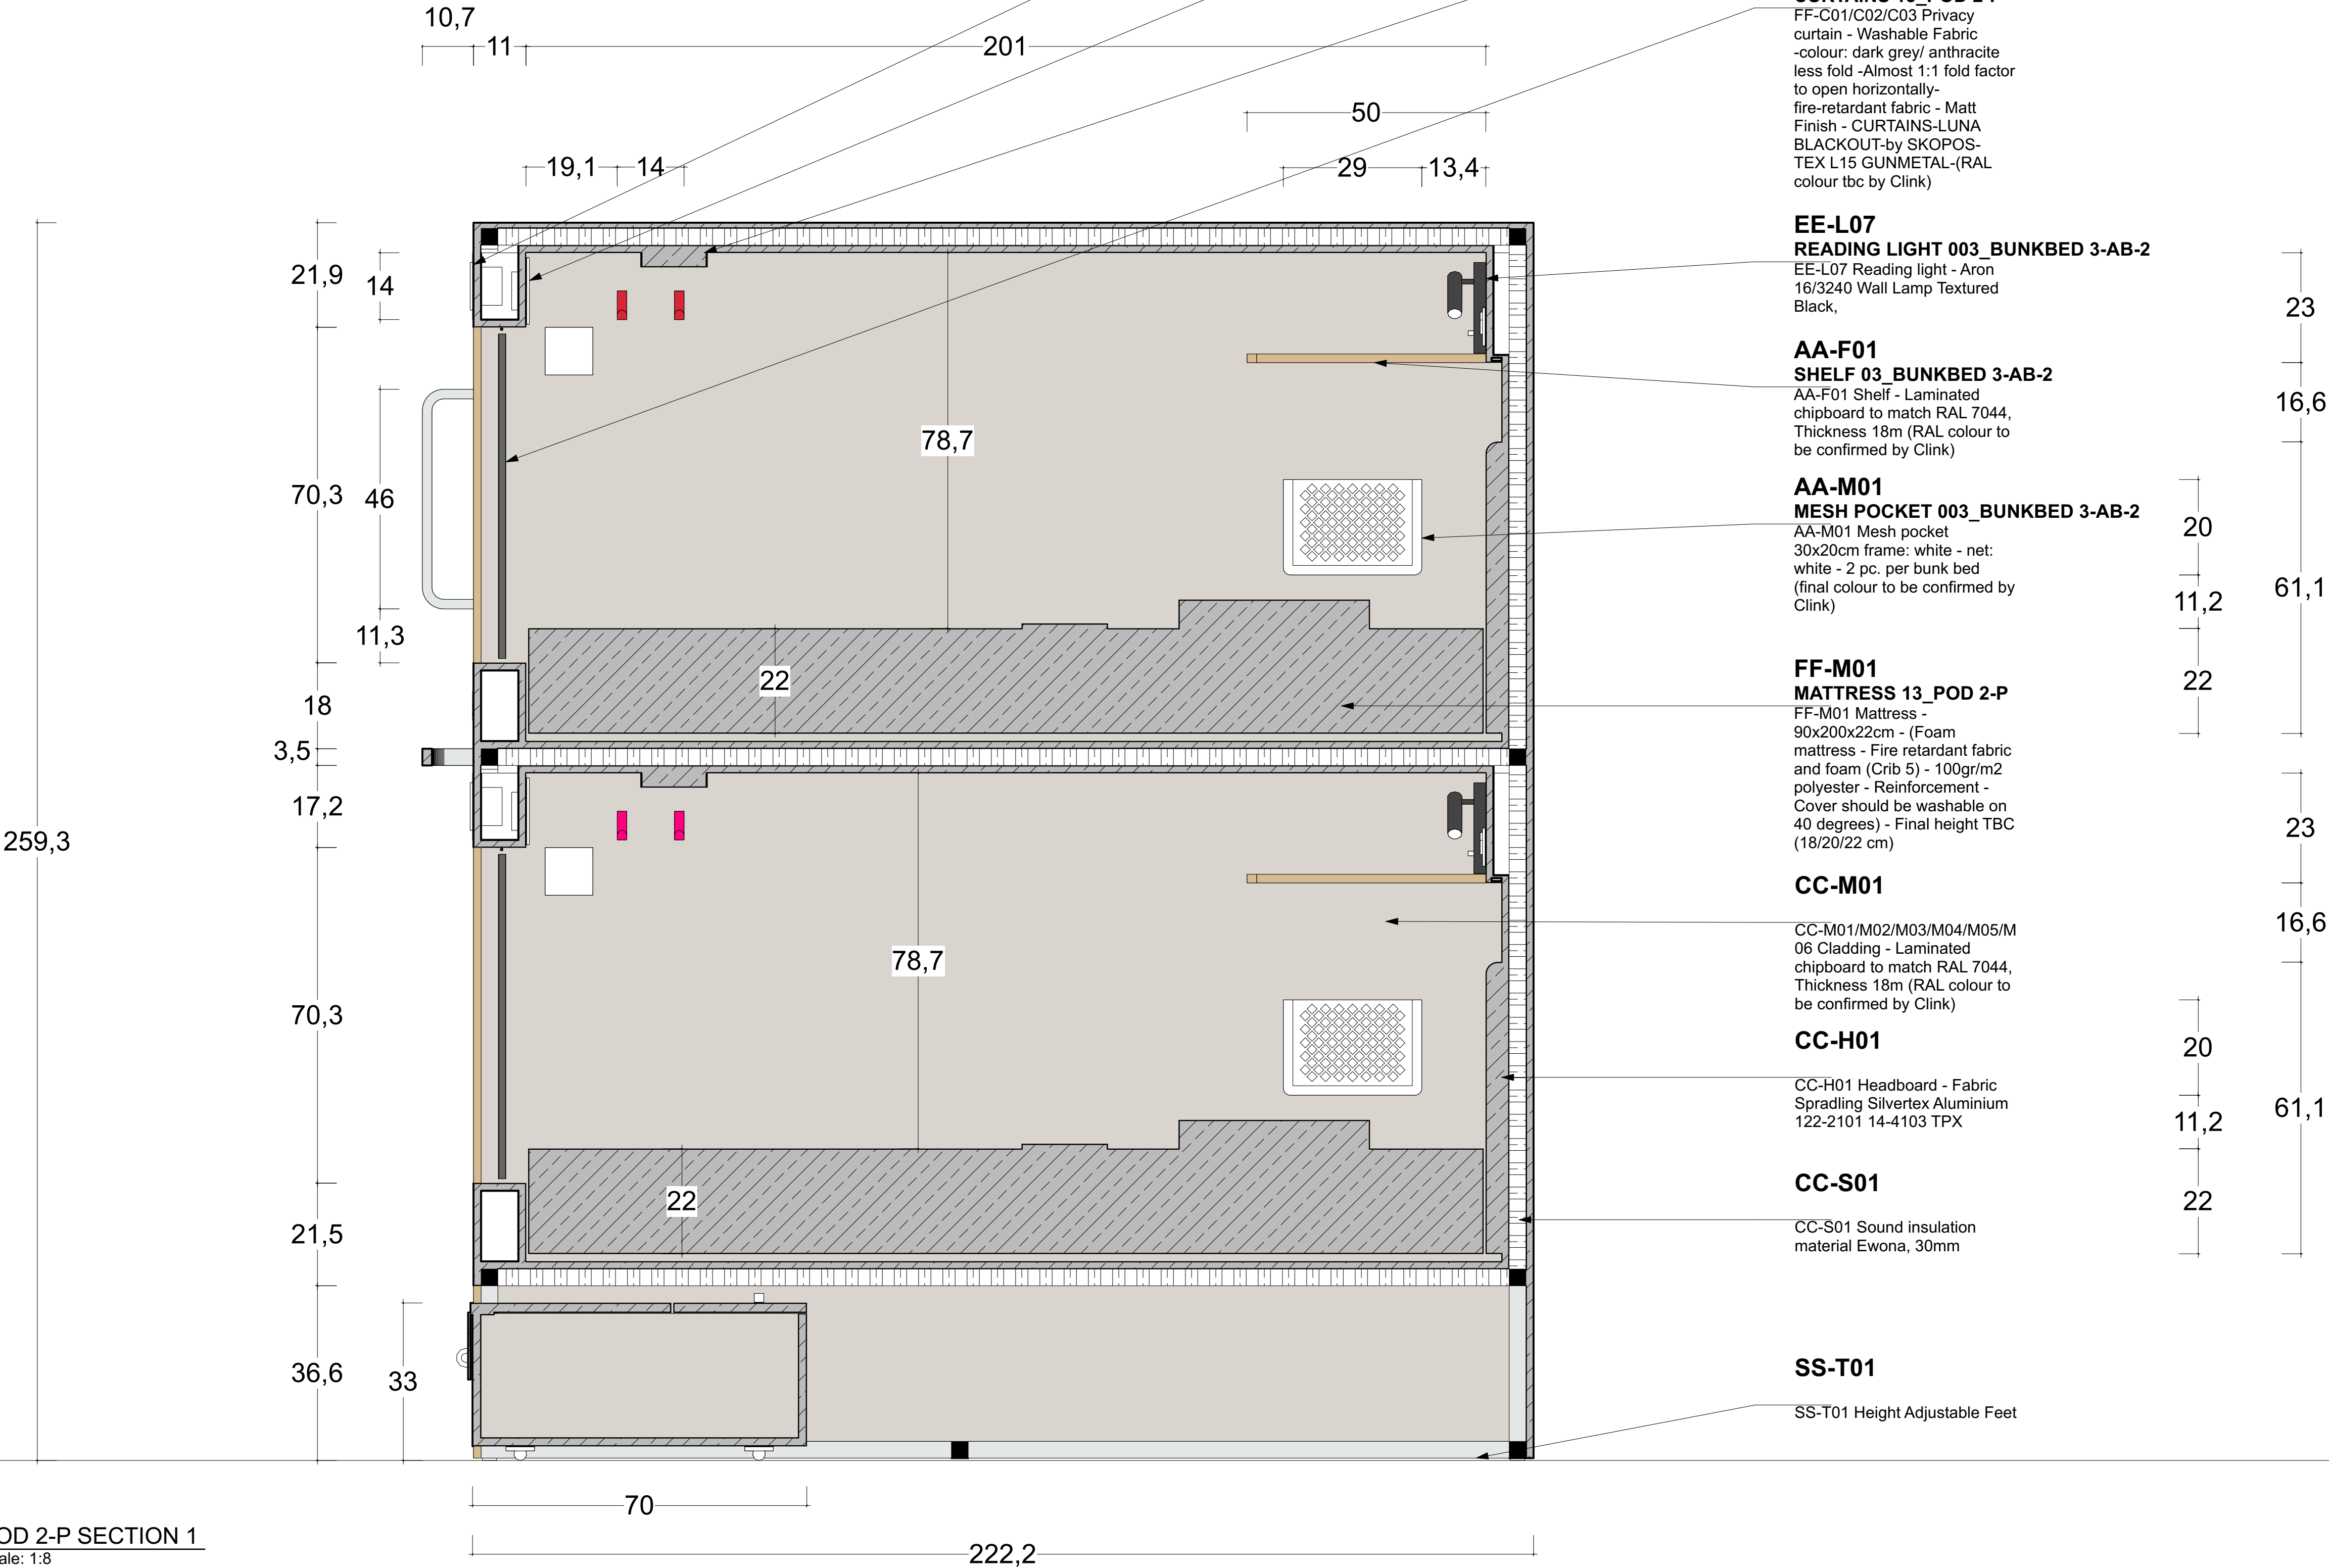

KEY

Index

A) 04.05.2026 Plan Set UP

All measurements have to be verified according to existing conditions by the contractor! Discrepancies must be reported immediately to the responsible project manager. The contractor has to produce fully dimensioned shop drawings prior to the start of the contract and they have to be approved by the client/ investor / interior designer

Project

CLINK 78 - BEDS

Logo



Project Address

CLINK 78
78 King's Cross Rd
London WC1X 9QG
United Kingdom

Client's Address

CLINK 78
78 King's Cross Rd
London WC1X 9QG
United Kingdom

Sheet Number 2-P-506

Total Sheets 82

Sheet Title
POD 2-P SECTION 1

Level

File Name

260425_CLINK 78_BEDs AA DRAFT 03.vwx

Date	Sheet Size	Scale	Signed
28.04.26	A1	1:8	AA

Stefanie Jaensch INTERIOR DESIGNS

Global Headquarter | Stefanie Jaensch c/o WeWork
Taubusanlage 8 | 60329 Frankfurt a.M.

E-Mail info@stefaniejaensch.de | DE +49 (0) 174 6756098

www.stefaniejaensch.de



Legal address | Stefanie Jaensch | Offenbacher Landstraße 434 | 60599 Frankfurt a.M.

© 2023 All Rights Reserved | Stefanie Jaensch

S1

POD 2-P SECTION 1
Scale: 1:8

PODS - TYPE 2-P - SECTION 2

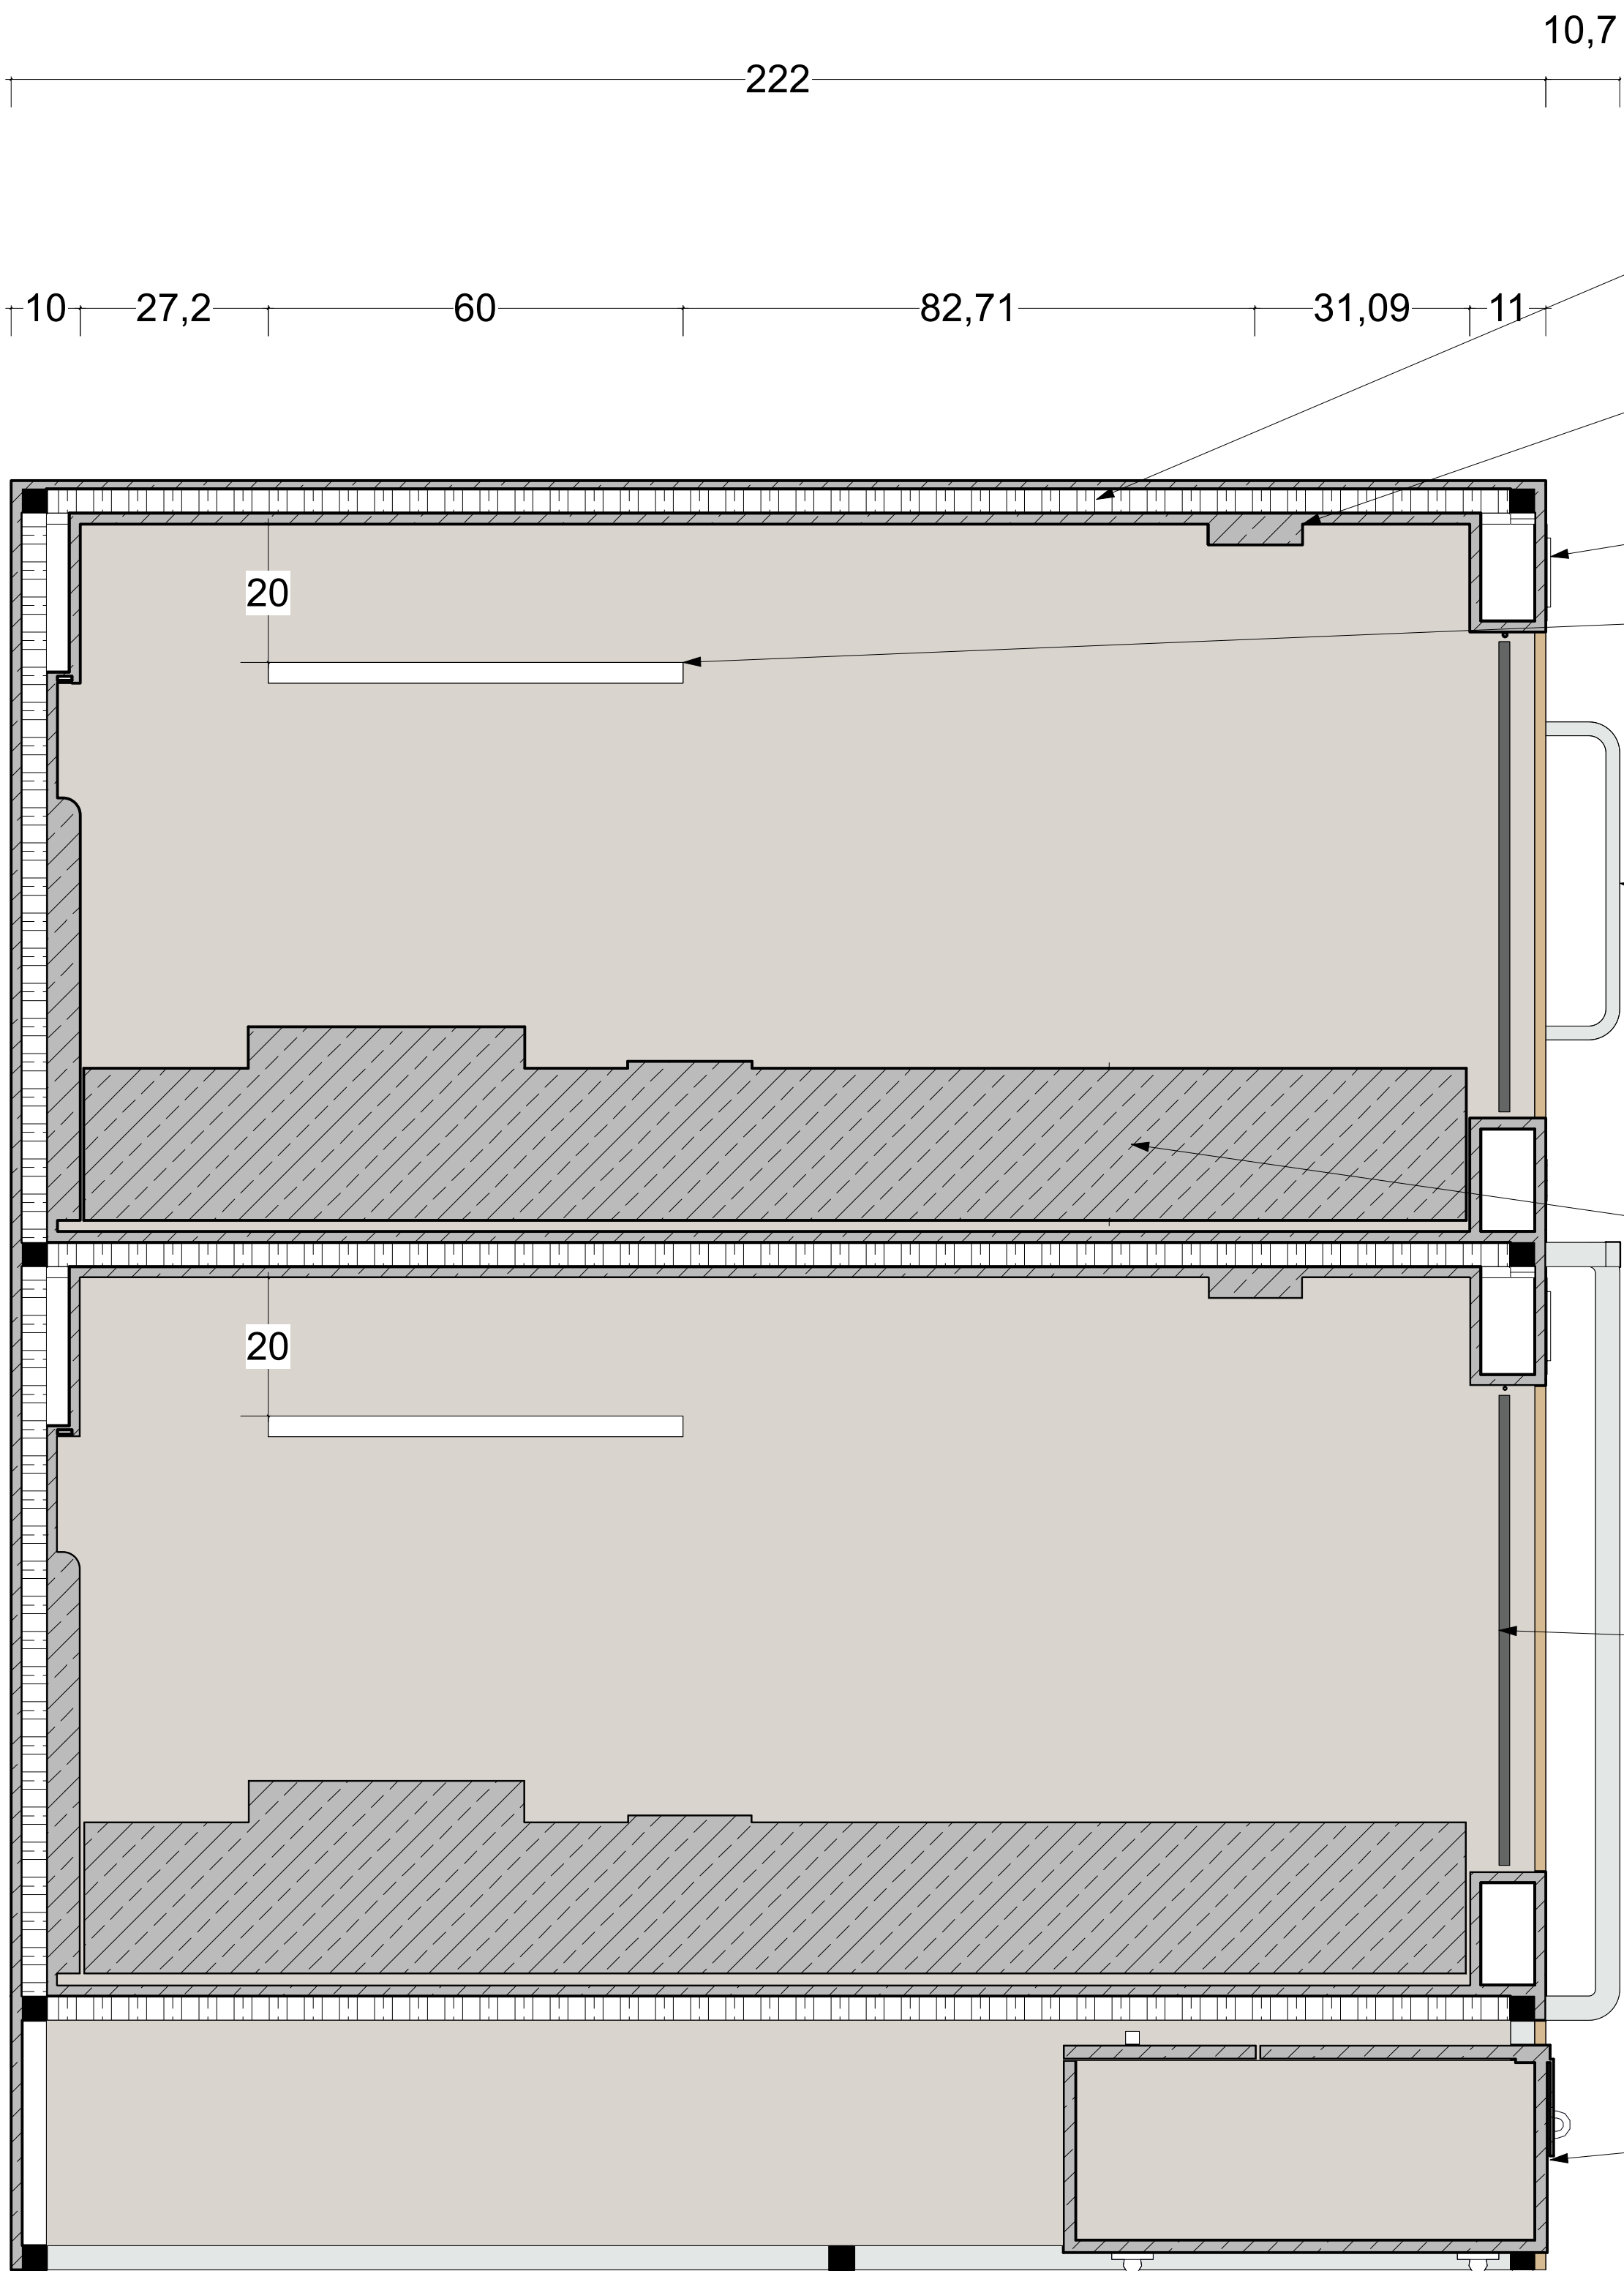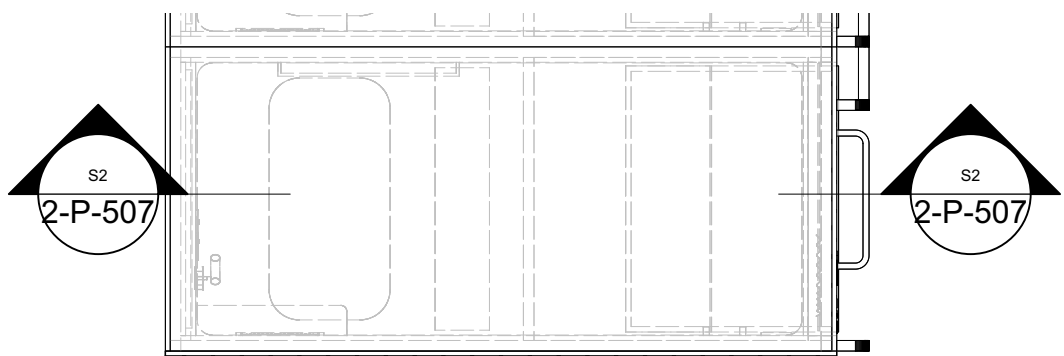

CC-S01

CC-S01 Sound insulation material Ewona, 30mm

EE-D01

EE-D01 Smoke detector optical

ME-V01

ME-V01 Ventilation system: Europlast NGA100

AA-R01

AA-R01 TOWEL RACK - stainless steel - powder coated - The same colour as the metal frame, polished edges for safety reasons, to fit into the metal frame size - according to the drawing (RAL colour to be confirmed by Clink)

SS-G01

SS-G01/G02/G03/G04/G05/G06/G07 GUARD - 3.5x3.5 cm Powder Coated Steel Frame Structure - Colour to match Telegrey 4 RAL 7047 - Semi gloss finish (RAL colour to be confirmed by Clink)

FF-M01


MATTRESS 13_POD 2-P FF-M01 Mattress - 90x200x22cm - (Foam mattress - Fire retardant fabric and foam (Crib 5) - 100gr/m2 polyester - Reinforcement - Cover should be washable on 40 degrees) - Final height TBC (18/20/22 cm)

FF-C02

FF-C01/C02/C03 Privacy curtain - Washable Fabric -colour: dark grey/ anthracite less fold -Almost 1:1 fold factor to open horizontally- fire-retardant fabric - Matt Finish - CURTAINS-LUNA BLACKOUT-by SKOPOS-TEX L15 GUNMETAL-(RAL colour tbc by Clink)

CC-L01

CLADDING 001_LOCKER 3 AA-L01 LOCKER - Lock - Powder Coated Steel Colour to match Telegrey 4 RAL 7047 - Semi gloss finish (RAL colour to be confirmed by Clink)

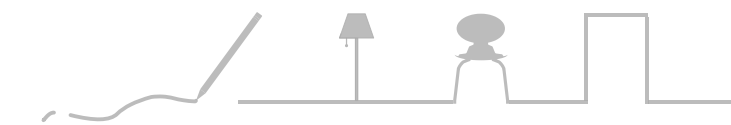

KEY

Index

A) 04.05.2026 Plan Set UP

All measurements have to be verified according to existing conditions by the contractor! Discrepancies must be reported immediately to the responsible project manager. The contractor has to produce fully dimensioned shop drawings prior to the start of the contract and they have to be approved by the client/ investor / interior designer

Project

CLINK 78 - BEDS

Logo



Project Address

CLINK 78
78 King's Cross Rd
London WC1X 9QG
United Kingdom

Client's Address

CLINK 78
78 King's Cross Rd
London WC1X 9QG
United Kingdom

Sheet Number 2-P-507		Total Sheets 82	
Sheet Title POD 2-P SECTION 2		Level	
File Name 260425_CLINK 78_BEDs AA DRAFT 03.vwx			
Date 28.04.26	Sheet Size A1	Scale 1:8	Signed AA

Stefanie Jaensch INTERIOR DESIGNS

Global Headquarter | Stefanie Jaensch c/o WeWork
Taubusanlage 8 | 60329 Frankfurt a.M.



E-Mail info@stefaniejaensch.de | DE +49 (0) 174 6756098

www.stefaniejaensch.de

Legal address | Stefanie Jaensch | Offenbacher Landstraße 434 | 60599 Frankfurt a.M.

© 2023 All Rights Reserved | Stefanie Jaensch

PODS - TYPE 2-P - SECTION 3

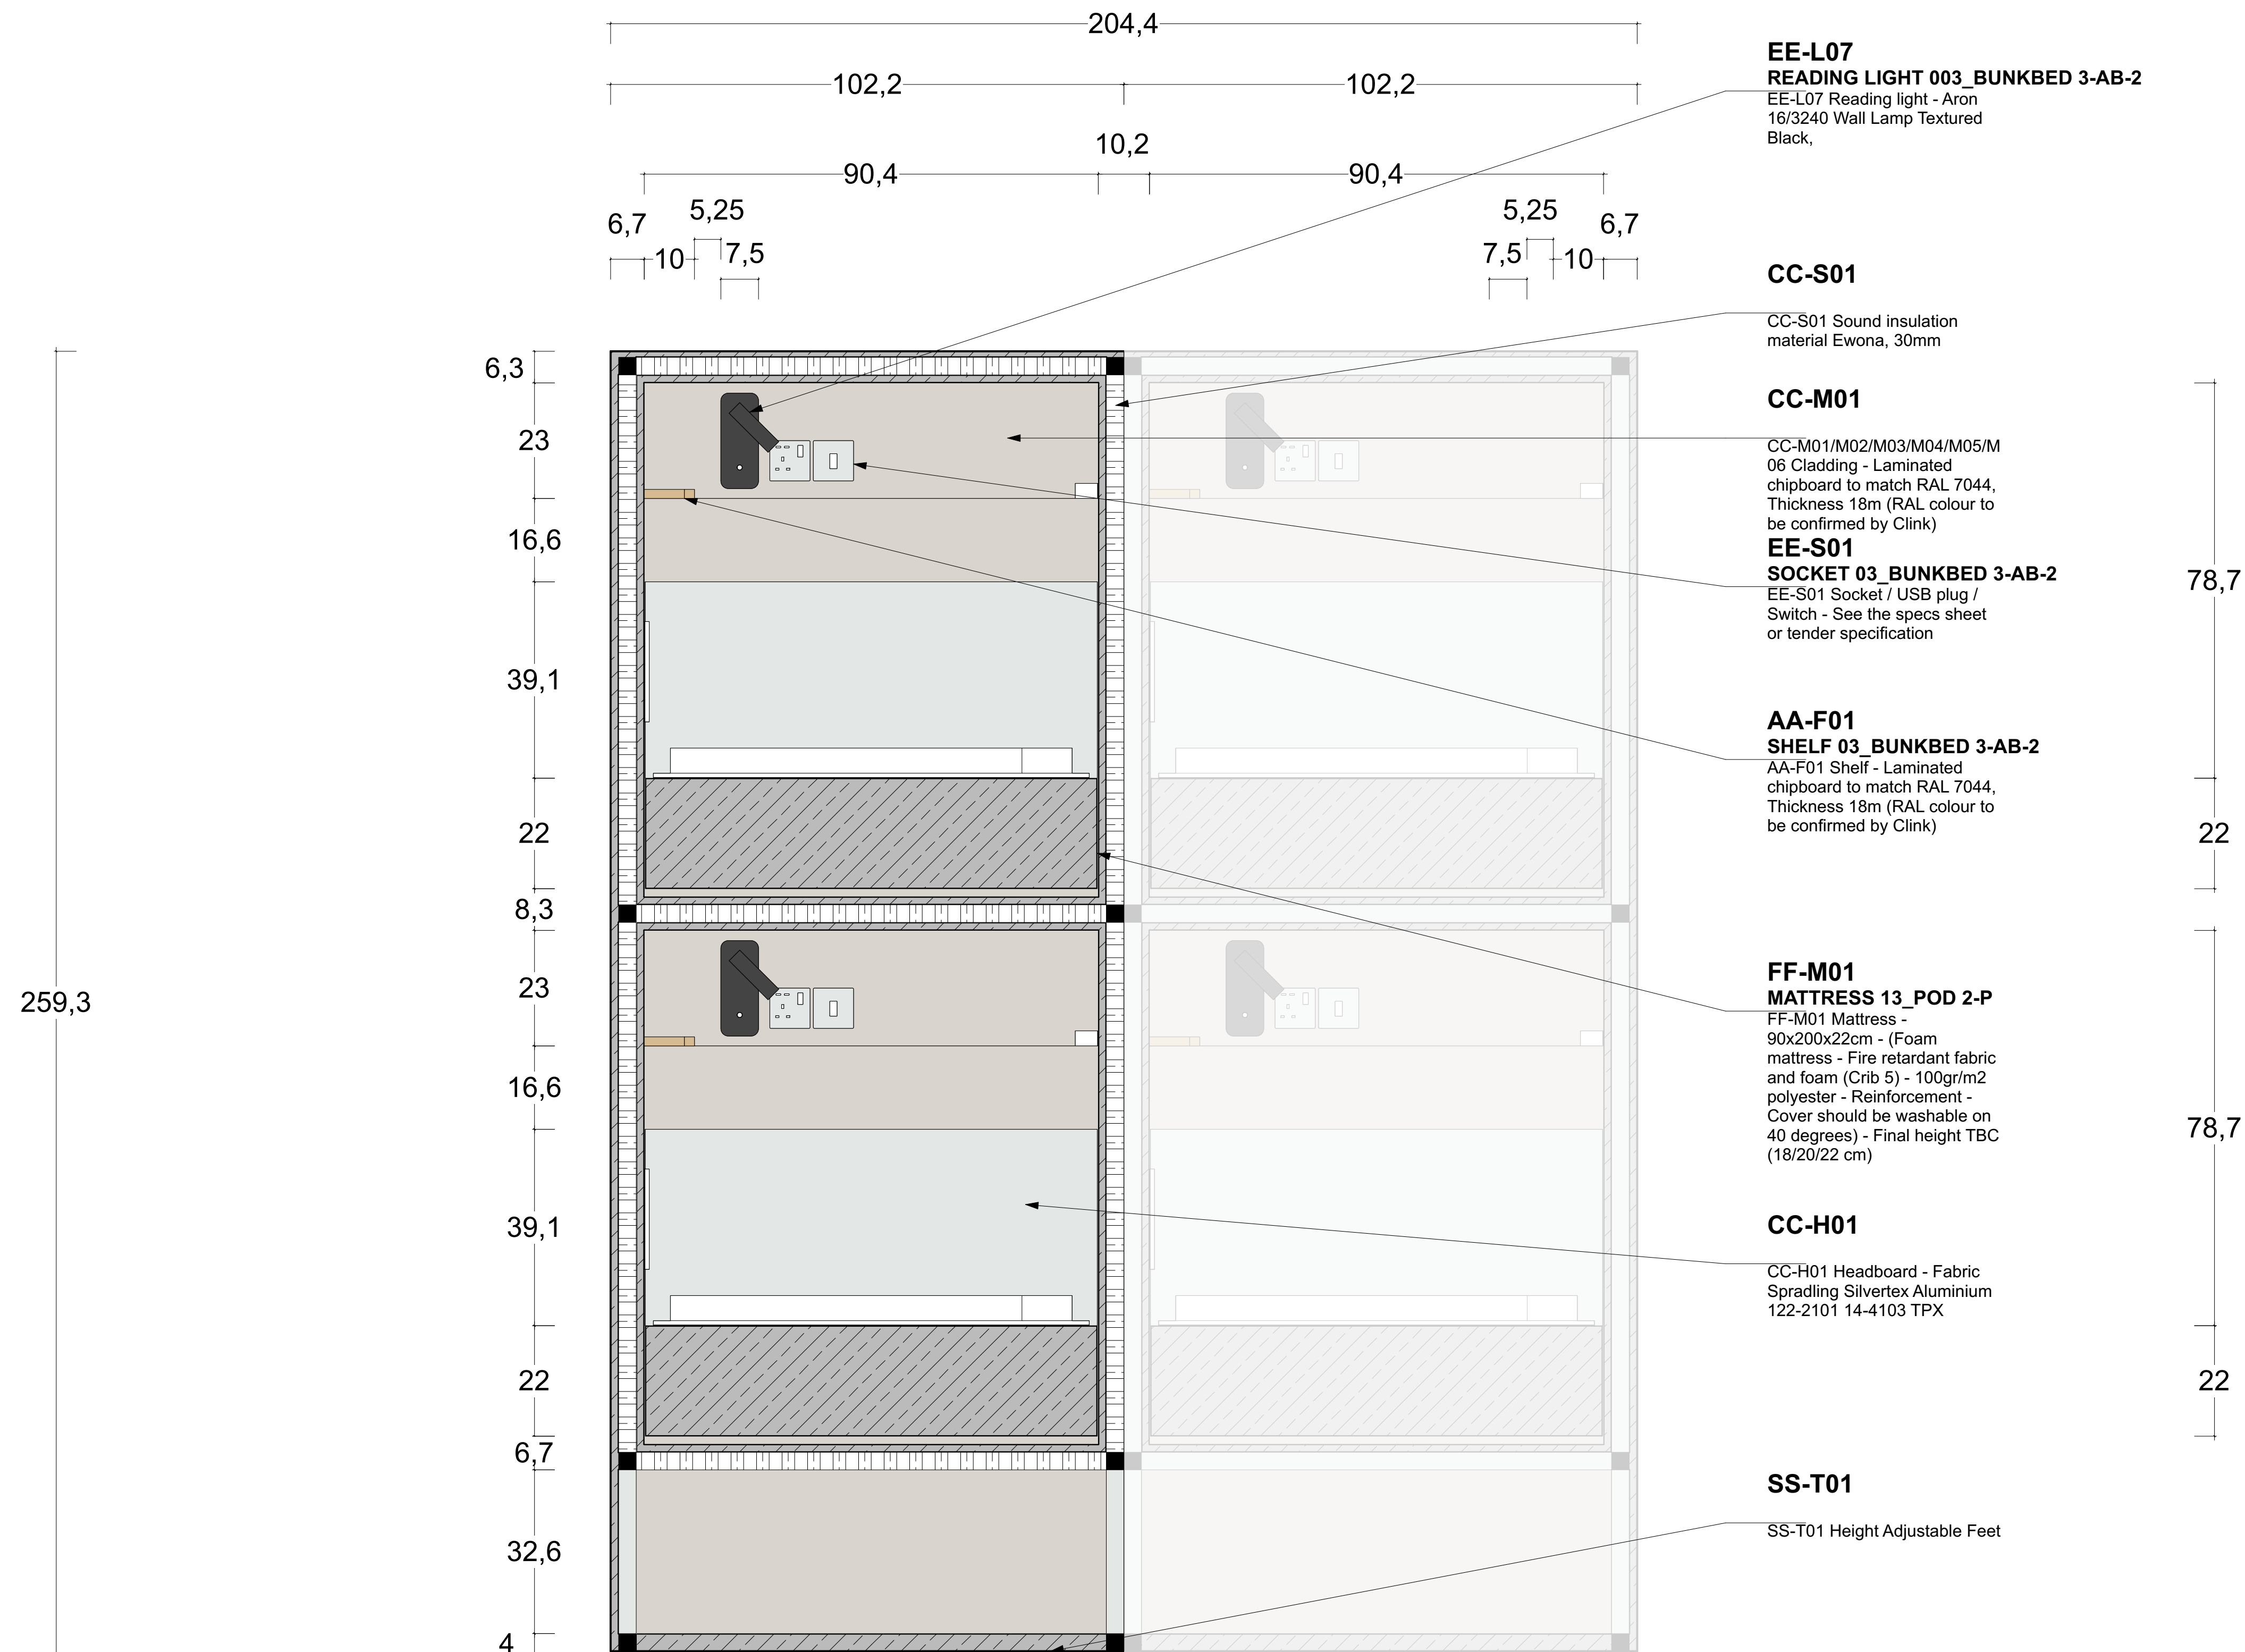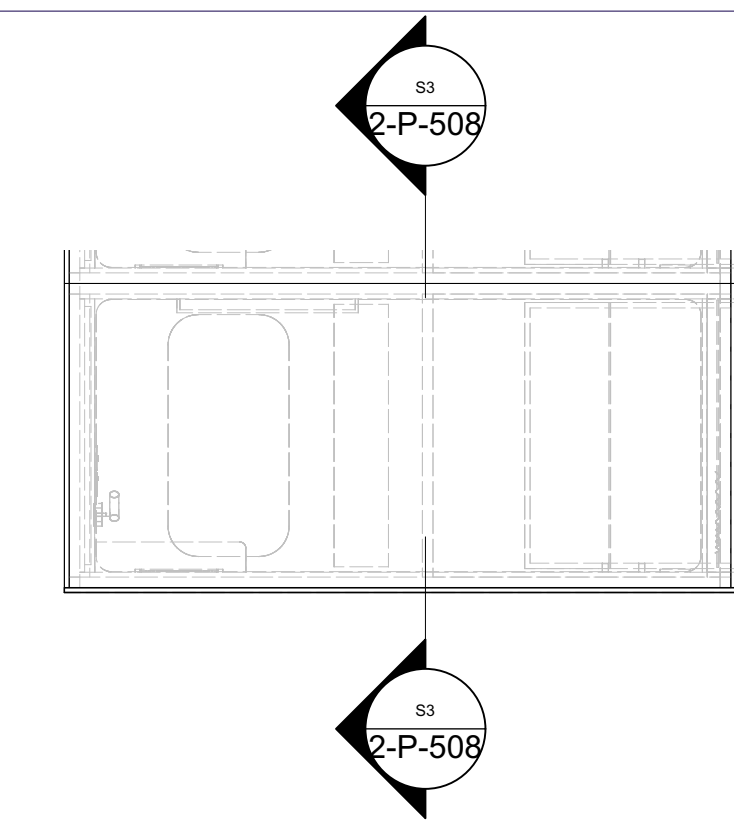

KEY

Index

A) 04.05.2026 Plan Set UP

All measurements have to be verified according to existing conditions by the contractor! Discrepancies must be reported immediately to the responsible project manager. The contractor has to produce fully dimensioned shop drawings prior to the start of the contract and they have to be approved by the client/ investor / interior designer

Project

CLINK 78 - BEDS

Logo



Project Address

CLINK 78
78 King's Cross Rd
London WC1X 9QG
United Kingdom

Client's Address

CLINK 78
78 King's Cross Rd
London WC1X 9QG
United Kingdom

Sheet Number 2-P-508

Total Sheets

2

Sheet Title
POD 2-P SECTION 3

vel

File Name

260425_CLINK 78_BEDs AA DRAFT 03.vwx

Date _____

8.04.26

Sheet Size	
------------	--

A1

cale

igned

Stefanie Jaensch INTERIOR DESIGNS

Global Headquarter | Stefanie Jaensch c/o WeWork

Headquart.: Stefanie Eichenhorn 8/8 Wehlener
Auenanlage 8 | 60329 Frankfurt a.M.




E-Mail info@stefaniejaensch.de | DE +49 (0) 174 6756098

www.stefaniejaensch.de

Legal address | Stefanie Jaensch | Offenbacher Landstraße 434 | 60599 Frankfurt a.M.

© 2023 All Rights Reserved | Stefanie Jaensch

PODS - TYPE 2-P - SECTION 4

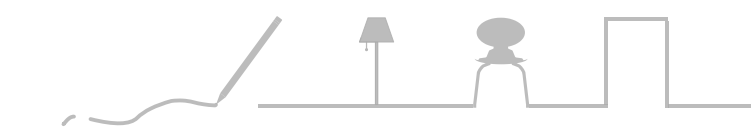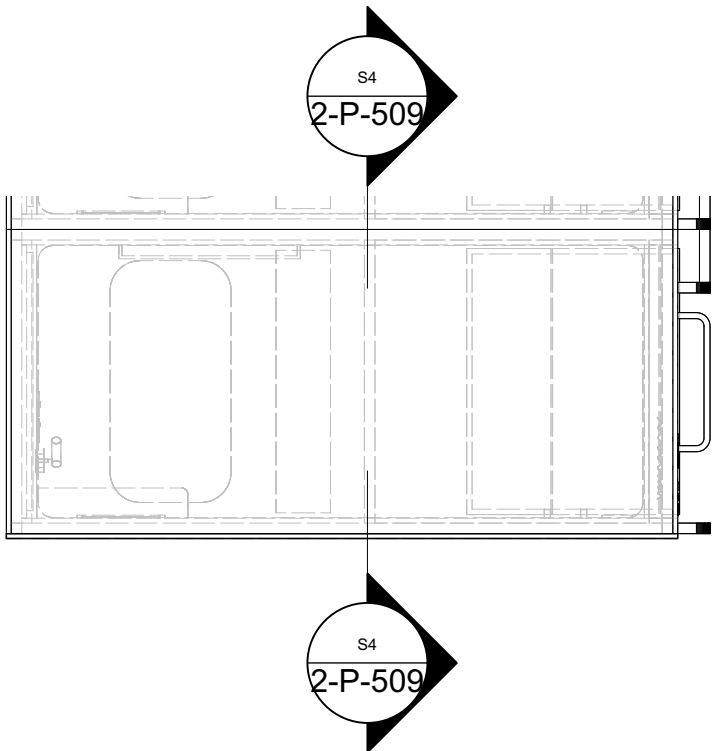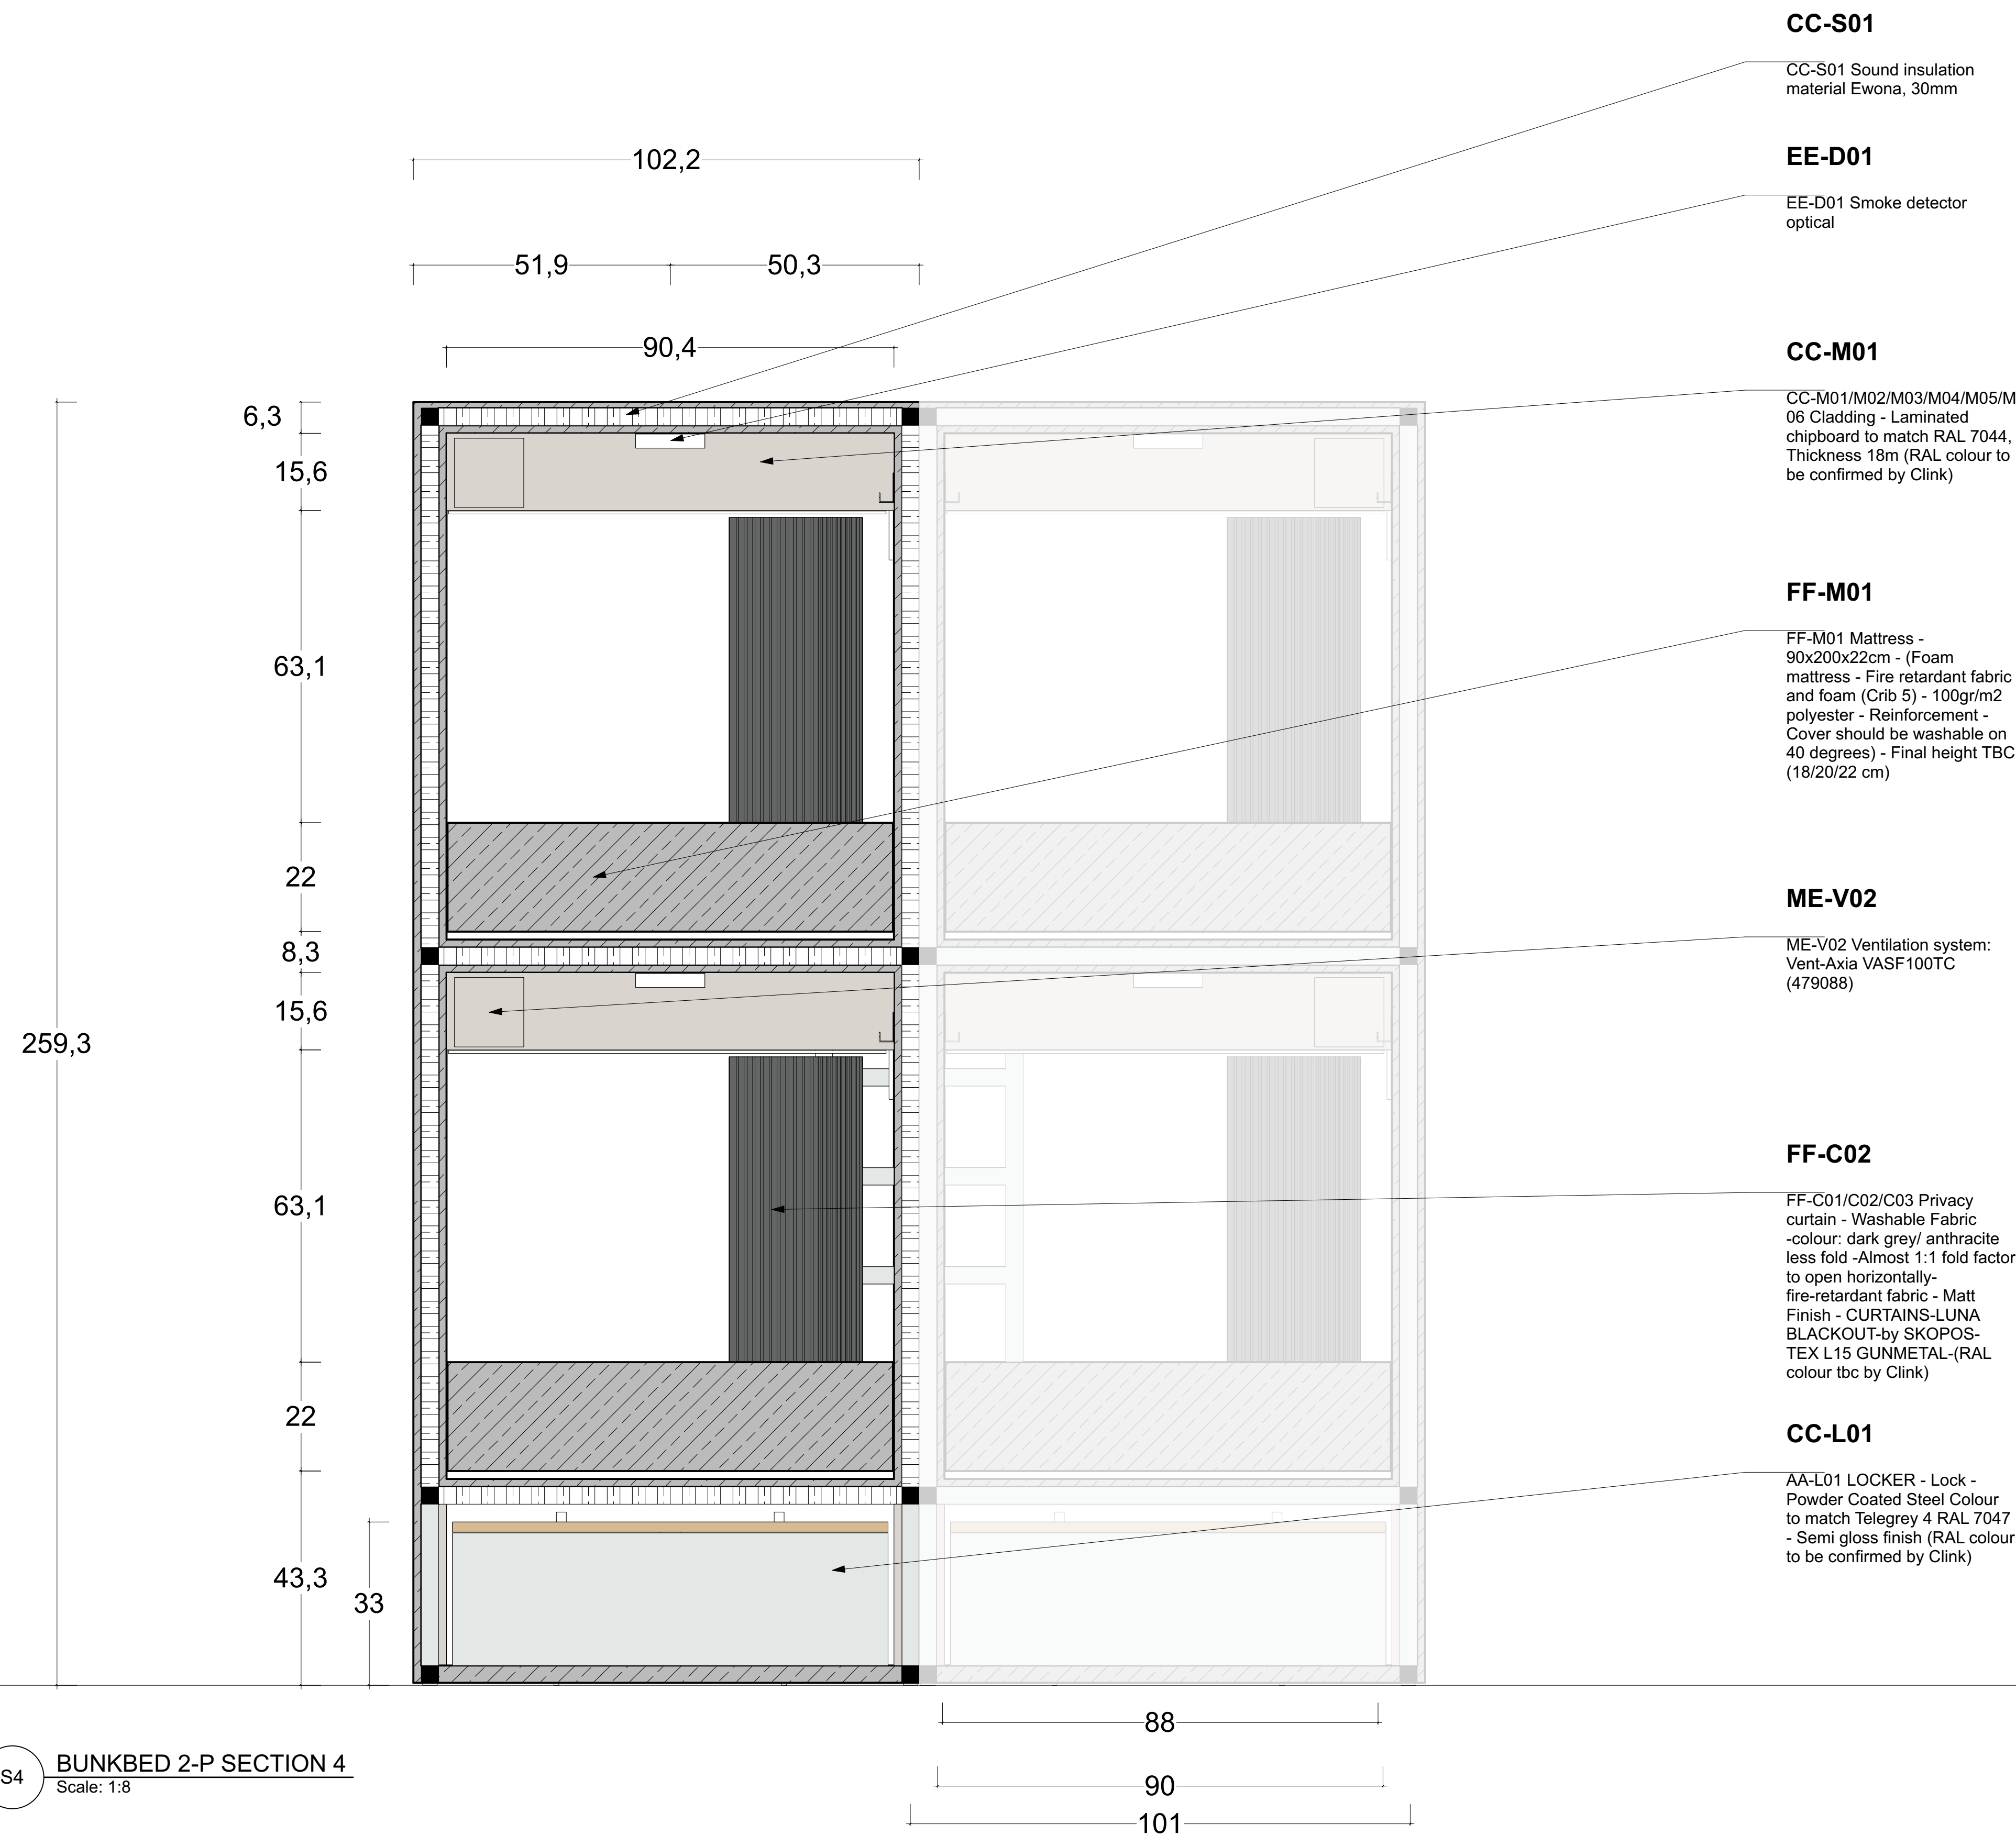

KEY

Index

A) 04.05.2026 Plan Set UP

All measurements have to be verified according to existing conditions by the contractor! Discrepancies must be reported immediately to the responsible project manager. The contractor has to produce fully dimensioned shop drawings prior to the start of the contract and they have to be approved by the client/ investor / interior designer

Project
CLINK 78 - BEDS




Project Address
CLINK 78
78 King's Cross Rd
London WC1X 9QG
United Kingdom

Client's Address
CLINK 78
78 King's Cross Rd
London WC1X 9QG
United Kingdom

Sheet Number 2-P-509		Total Sheets 82
Sheet Title POD 2-P SECTION 4		Level
File Name 260425_CLINK 78_BEDs AA DRAFT 03.vwx		

Date	Sheet Size	Scale	Signed
28.04.26	A1	1:8	AA

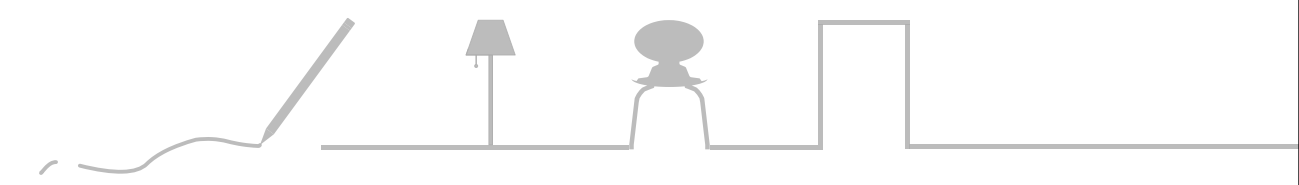

For




BUNKBEDS

TYPE 3

TEARAW



BUNKBEDS TYPE 3 (TRIPLE)

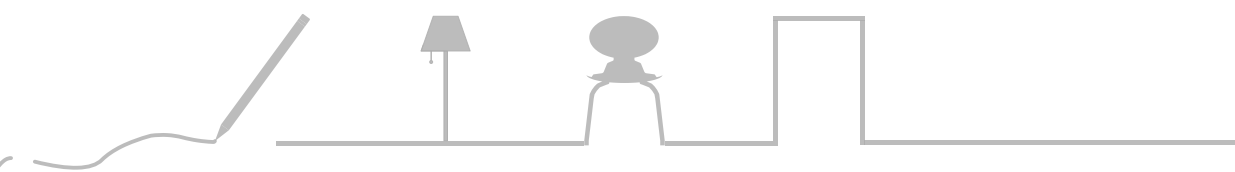


Stefanie Jaensch

INTERIOR DESIGNS

For

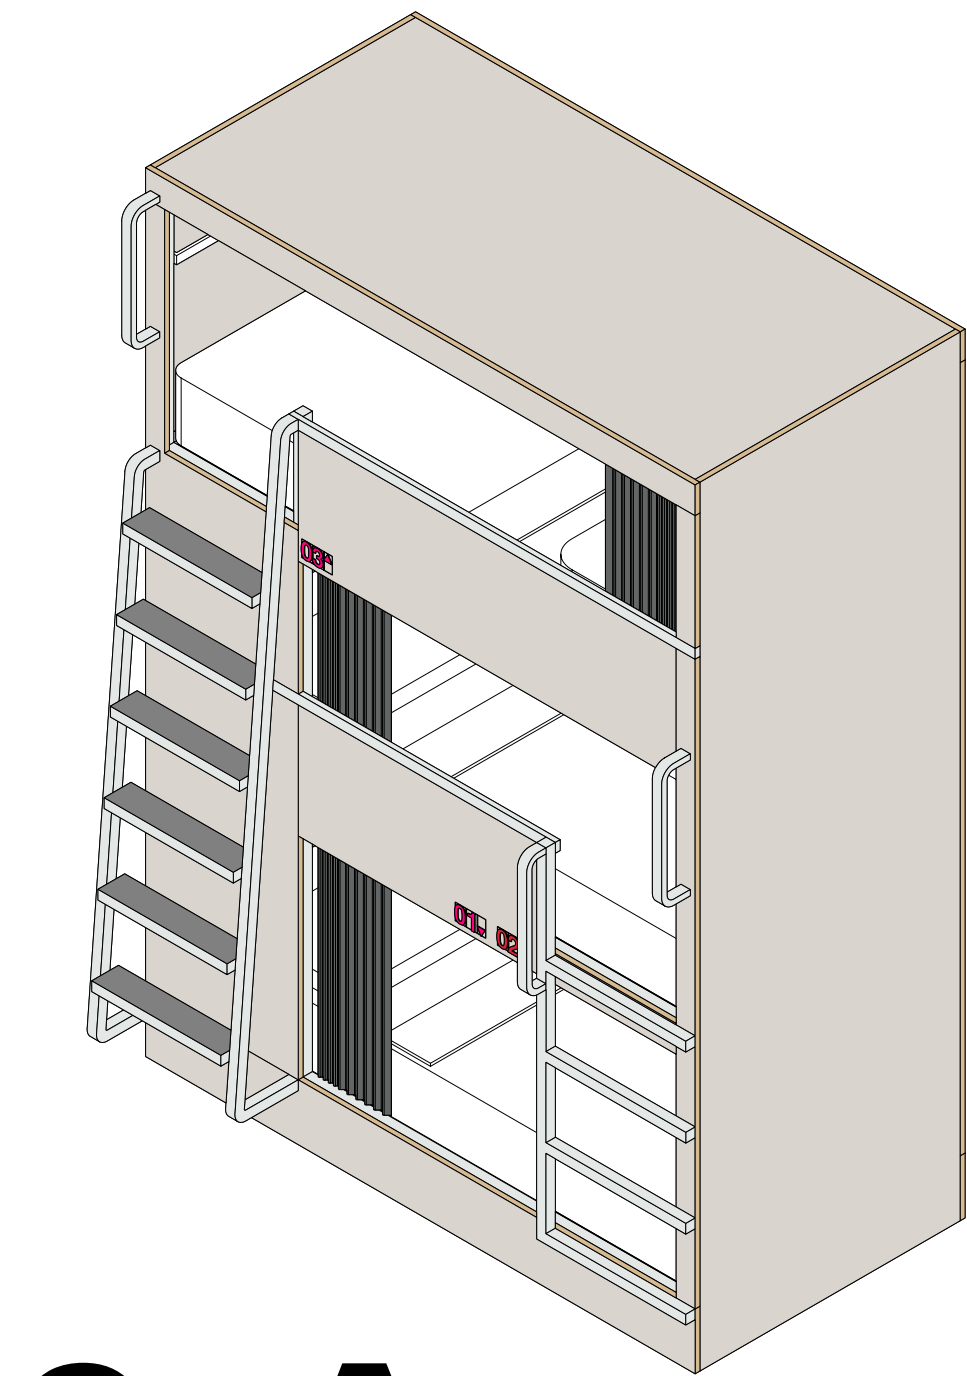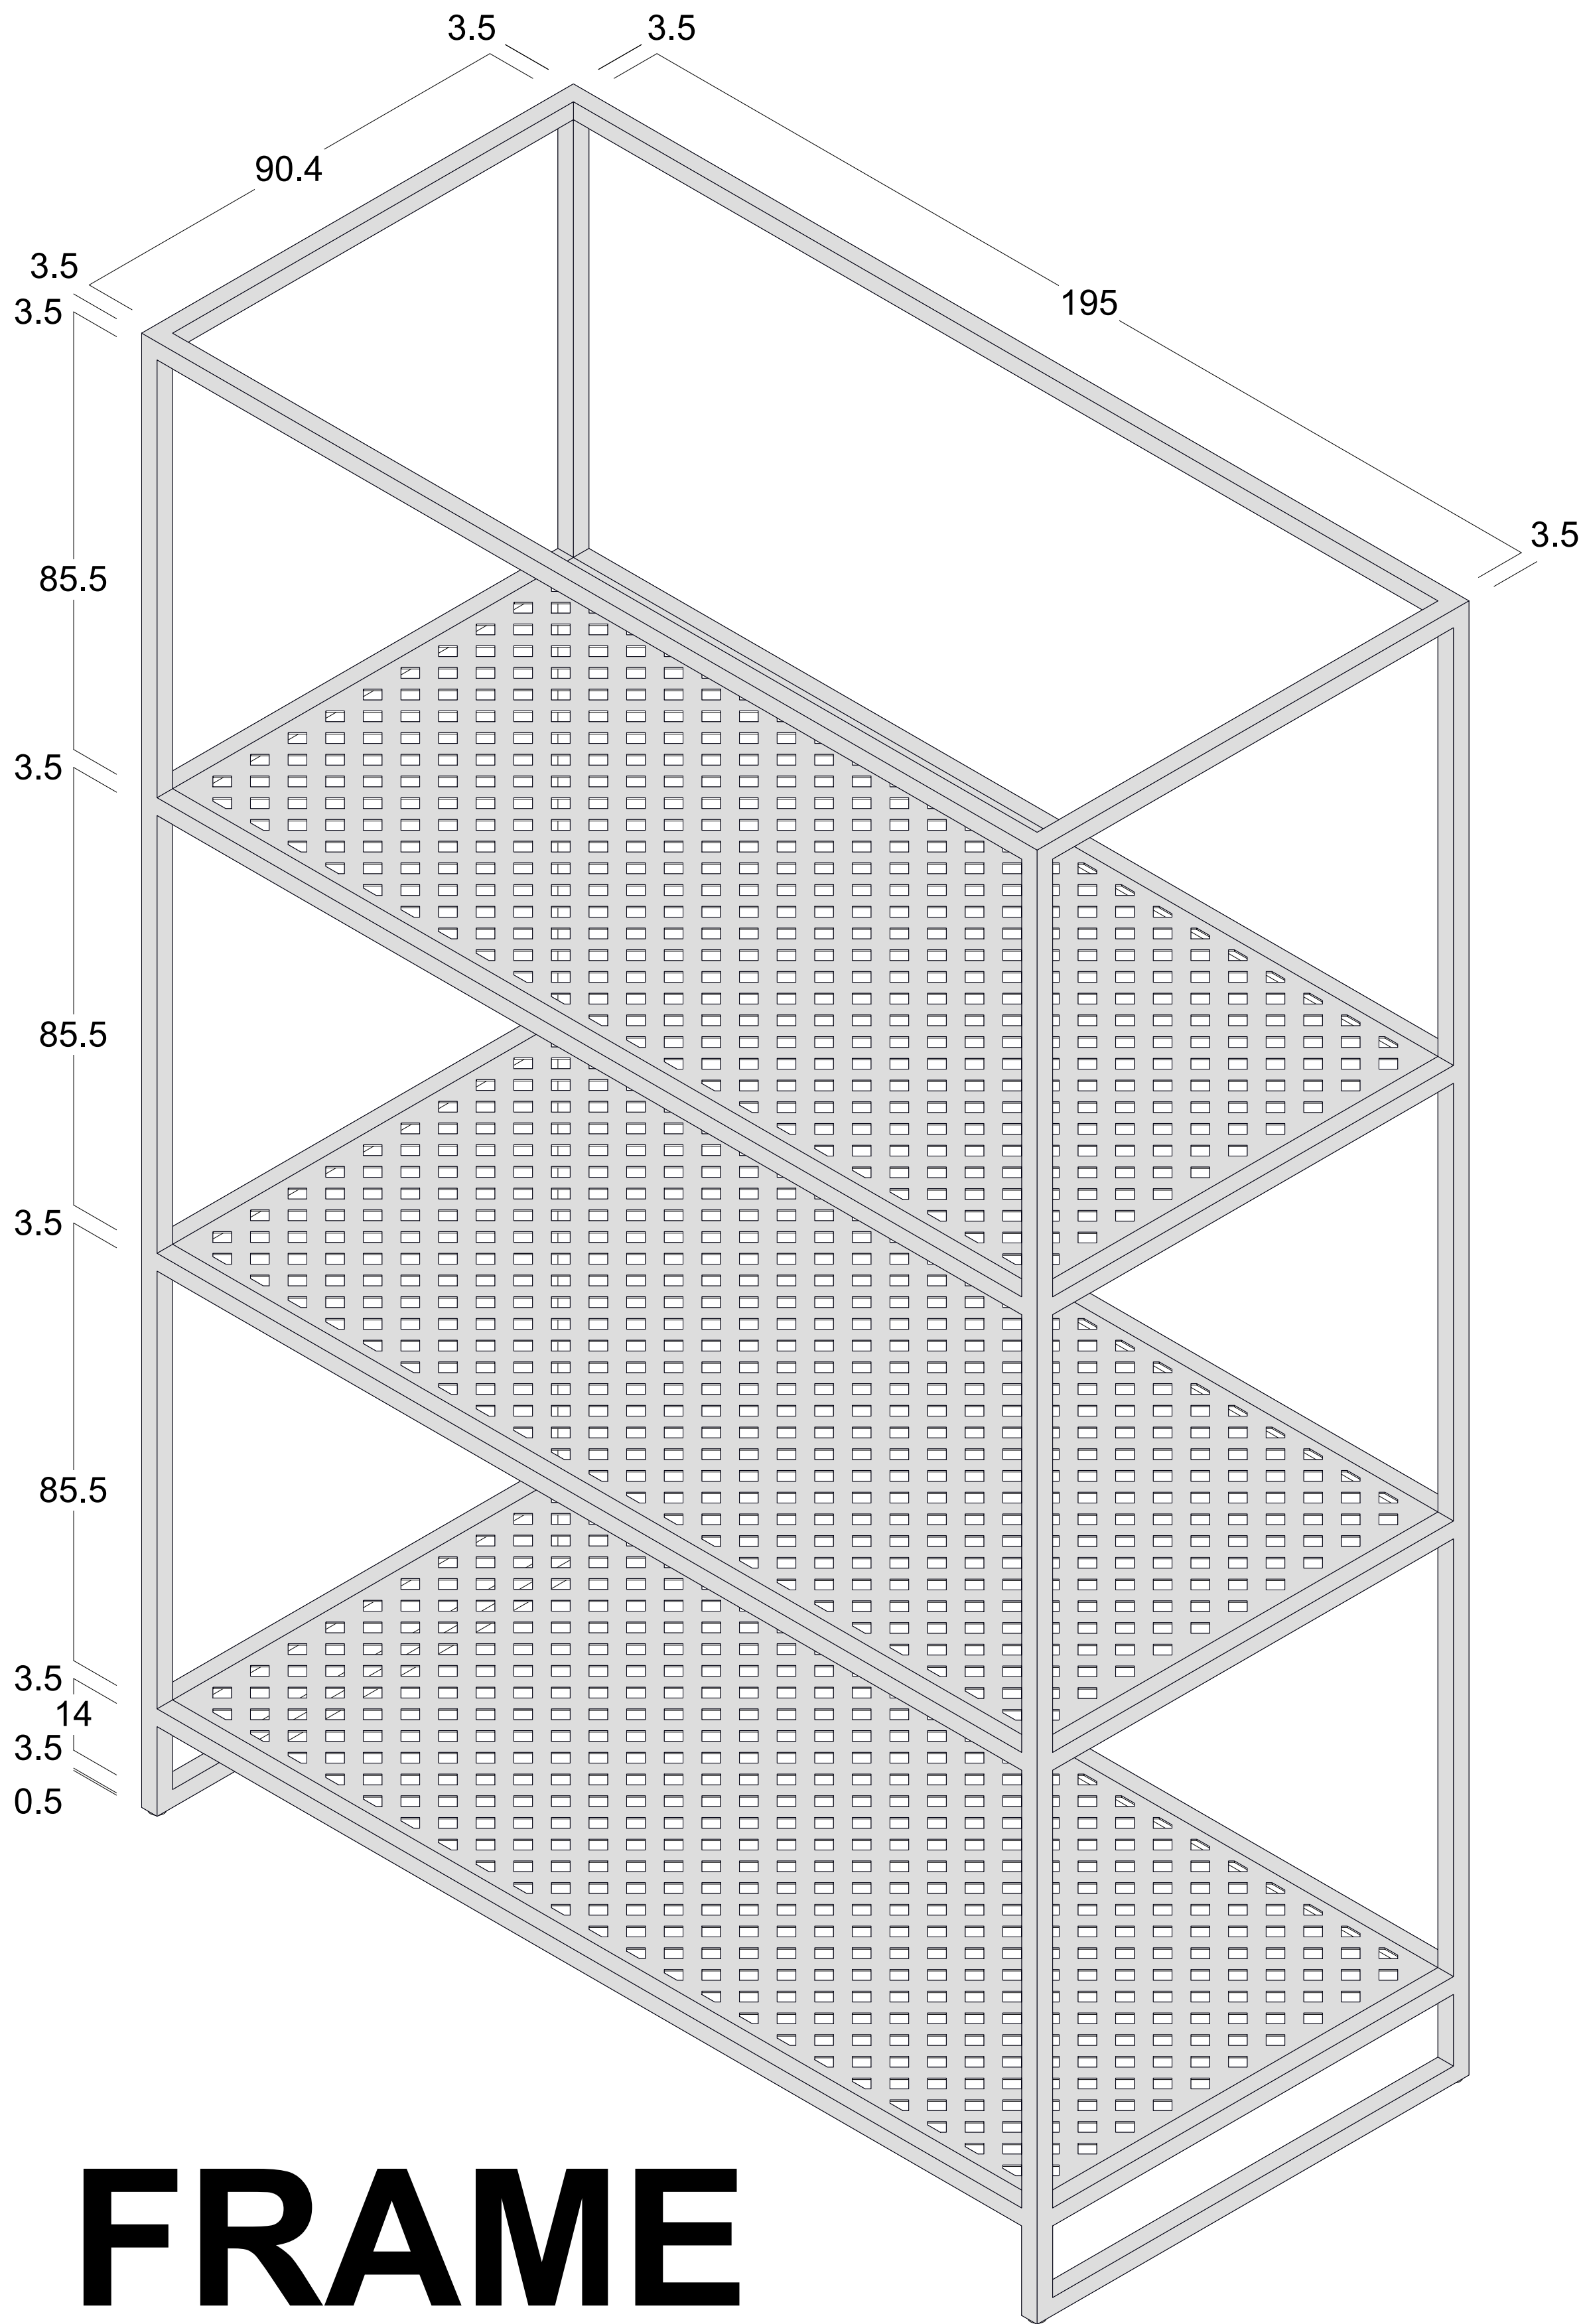

3-A

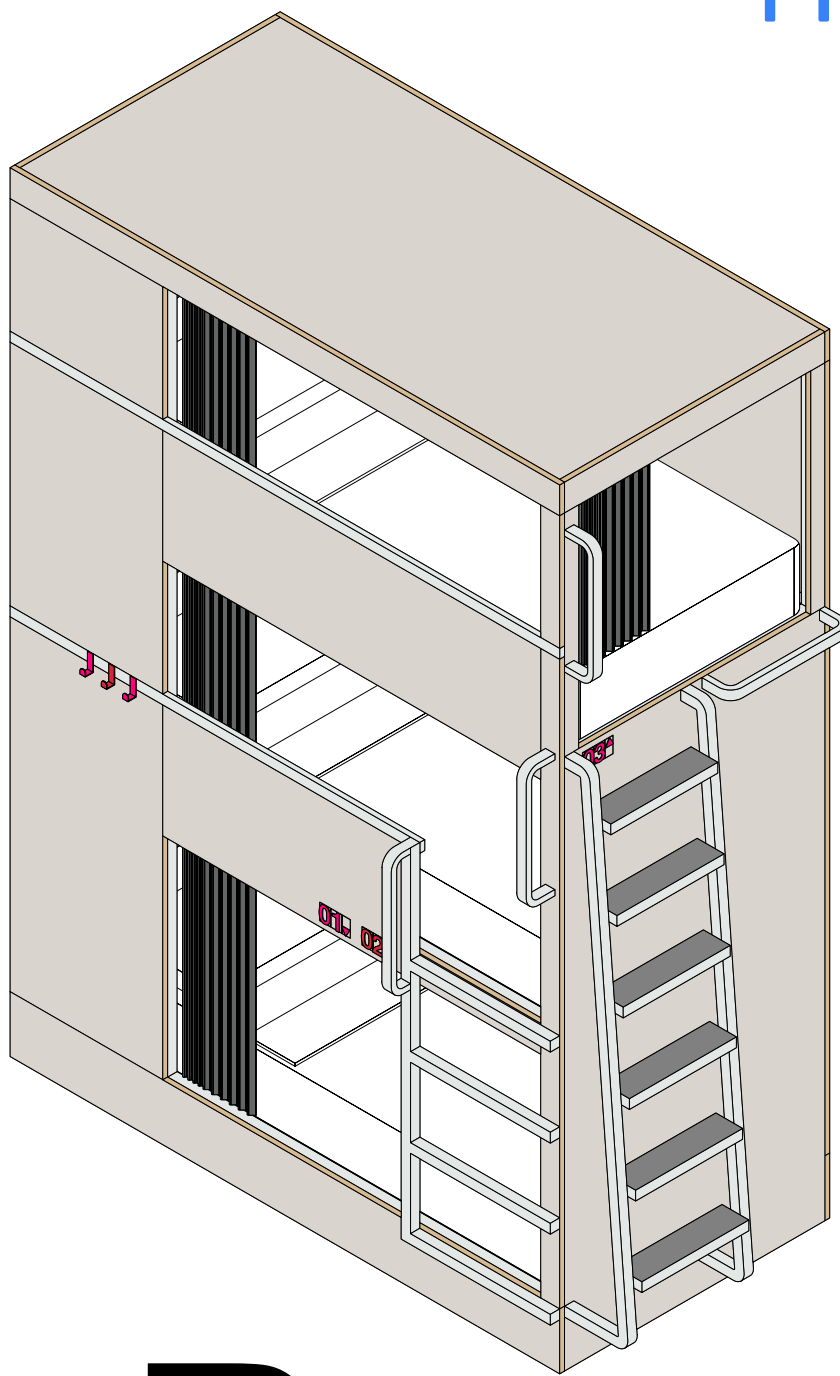



3-B

FRAME

202 x 97.4 x 288.5
(L x W x H) cm

STYLING
DRAWING

BUNKBEDS TYPE 3 (TRIPLE) - SIGNANGE








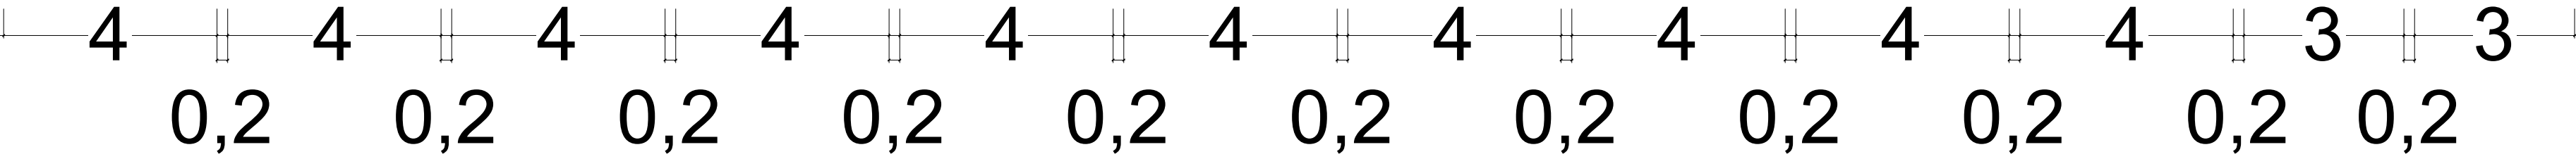
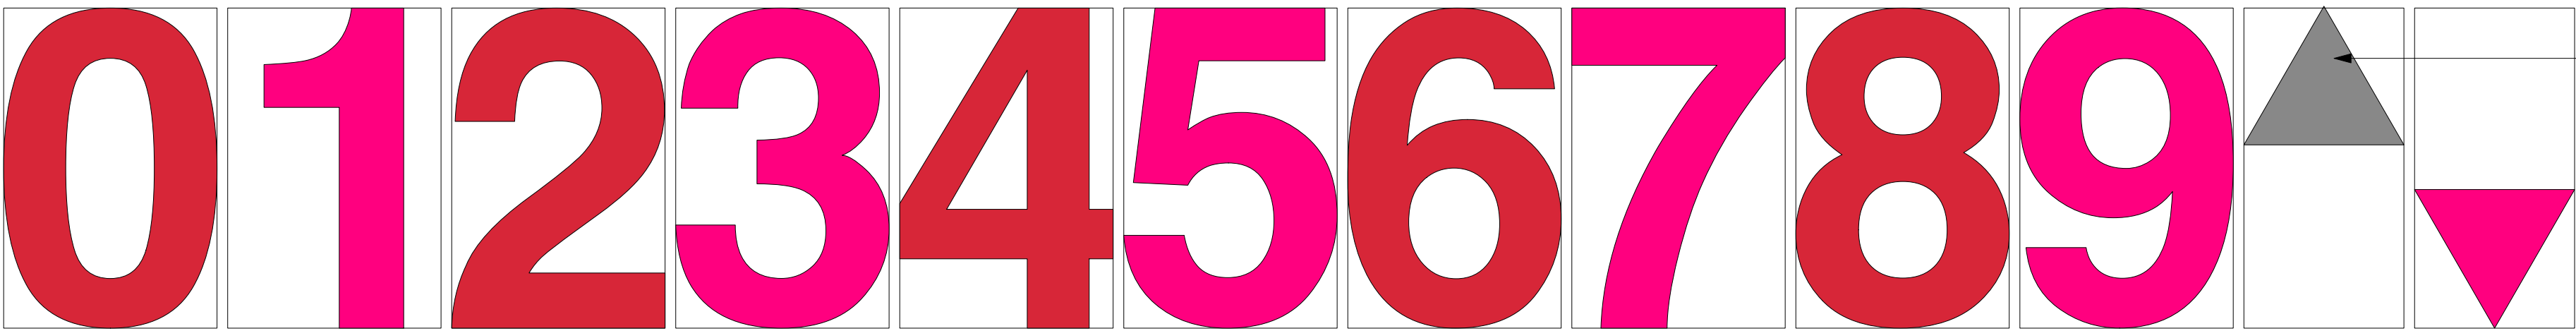


6


AA-S01
3-001 NUMBERS
AA-R01 TOWEL RACK -
stainless steel - powder coated
- The same colour as the
metal frame, polished edges
for safety reasons, to fit into
the metal frame size -
according to the drawing (RAL
colour to be confirmed by
Clink)

COLOUR EXAMPLE			
RAL 3020	TRIPLE BUNKBED 1	TRIPLE BUNKBED 2	
	03▲	06▲	
	02▲	05▲	
RAL 4010	01▼	04▼	


FINAL COLOURS TBC BY CLINK

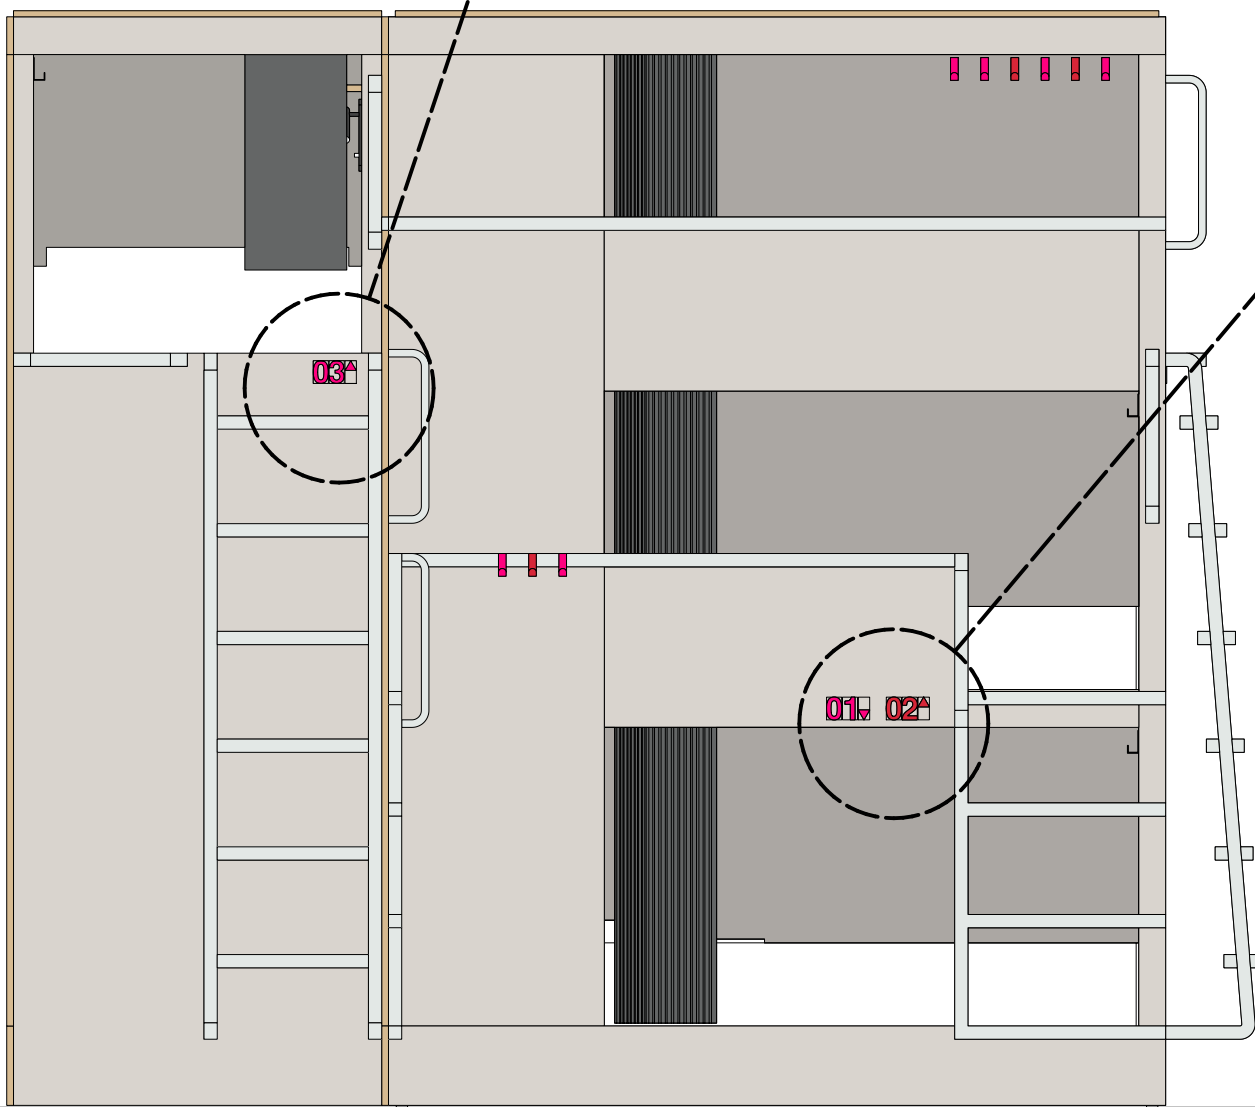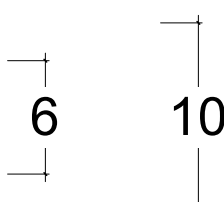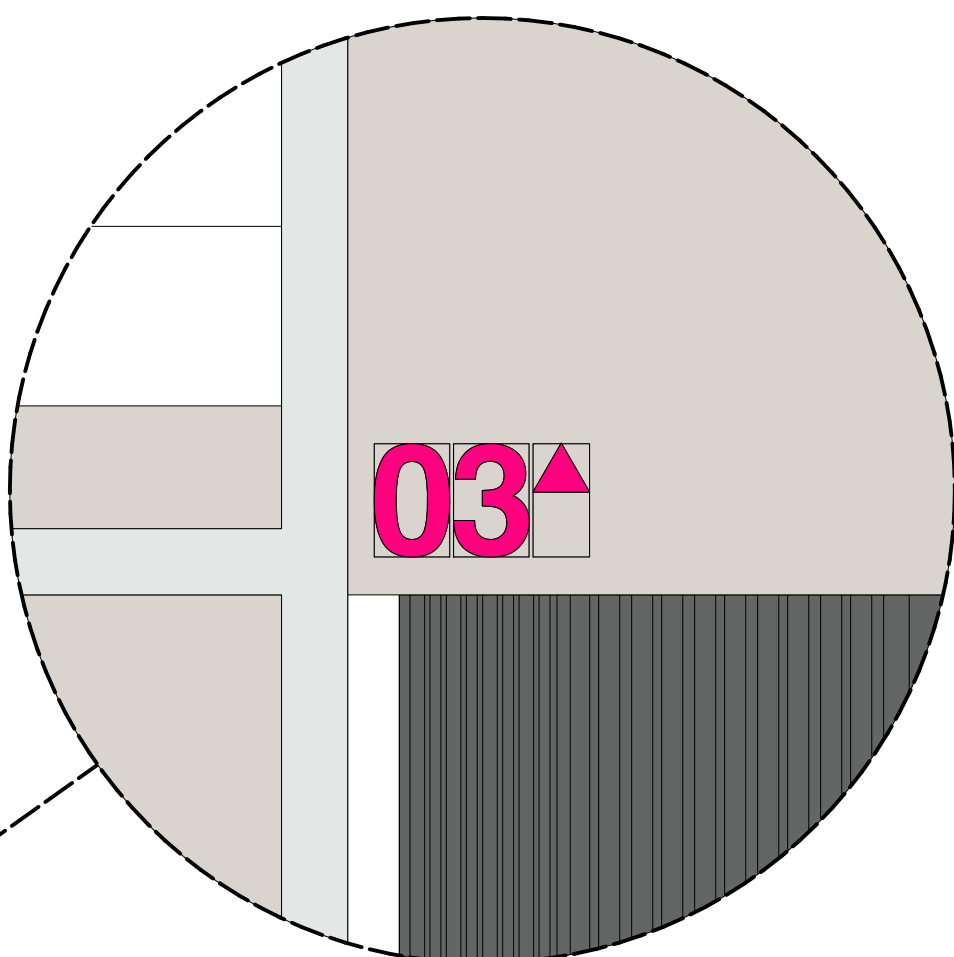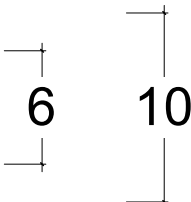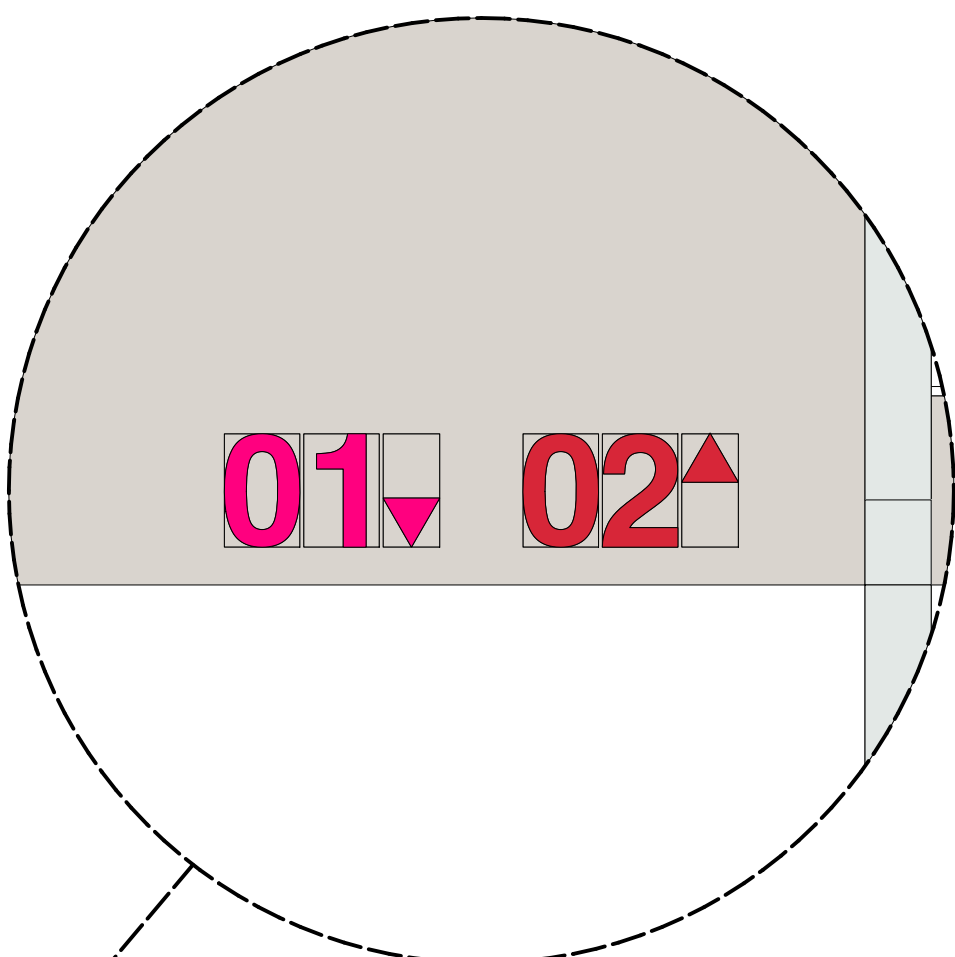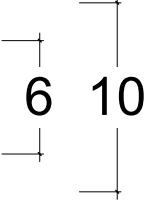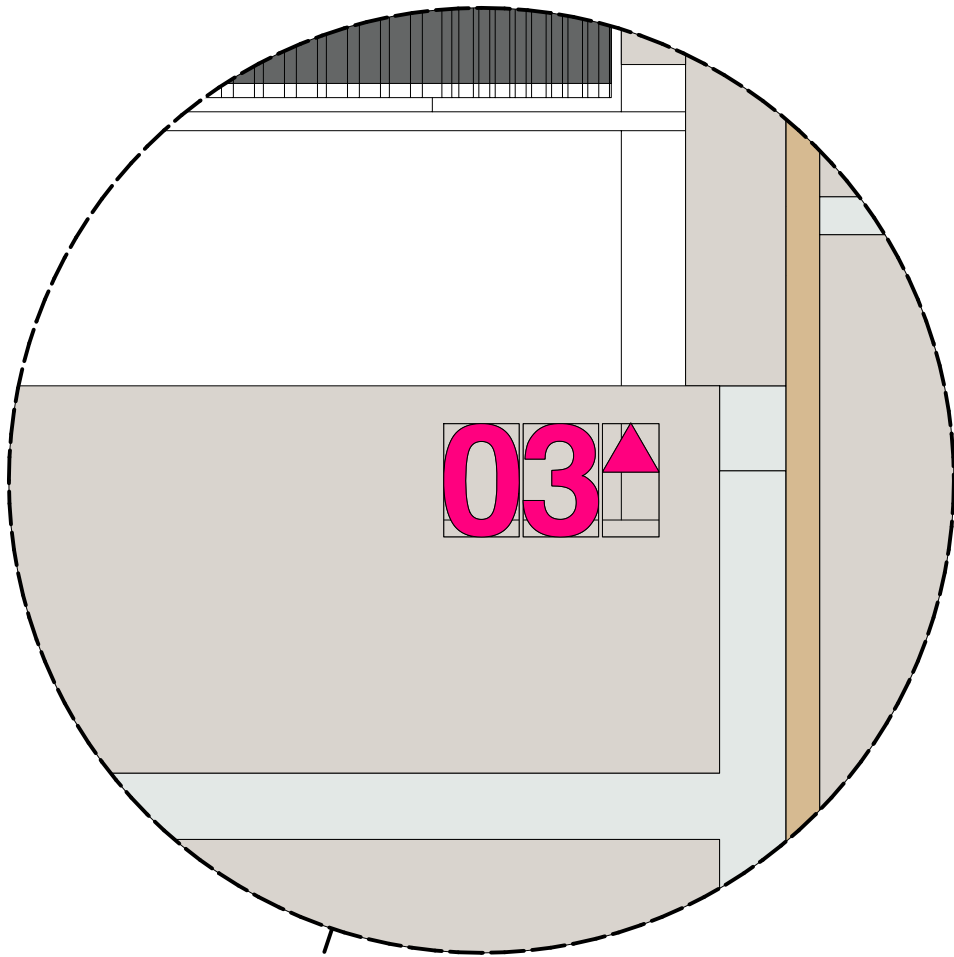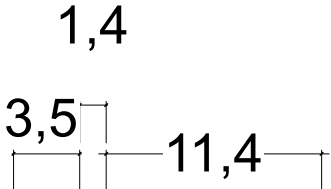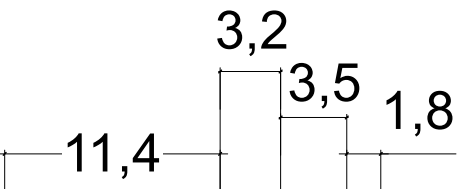


BUNKBED 3-B ELEVATIONS

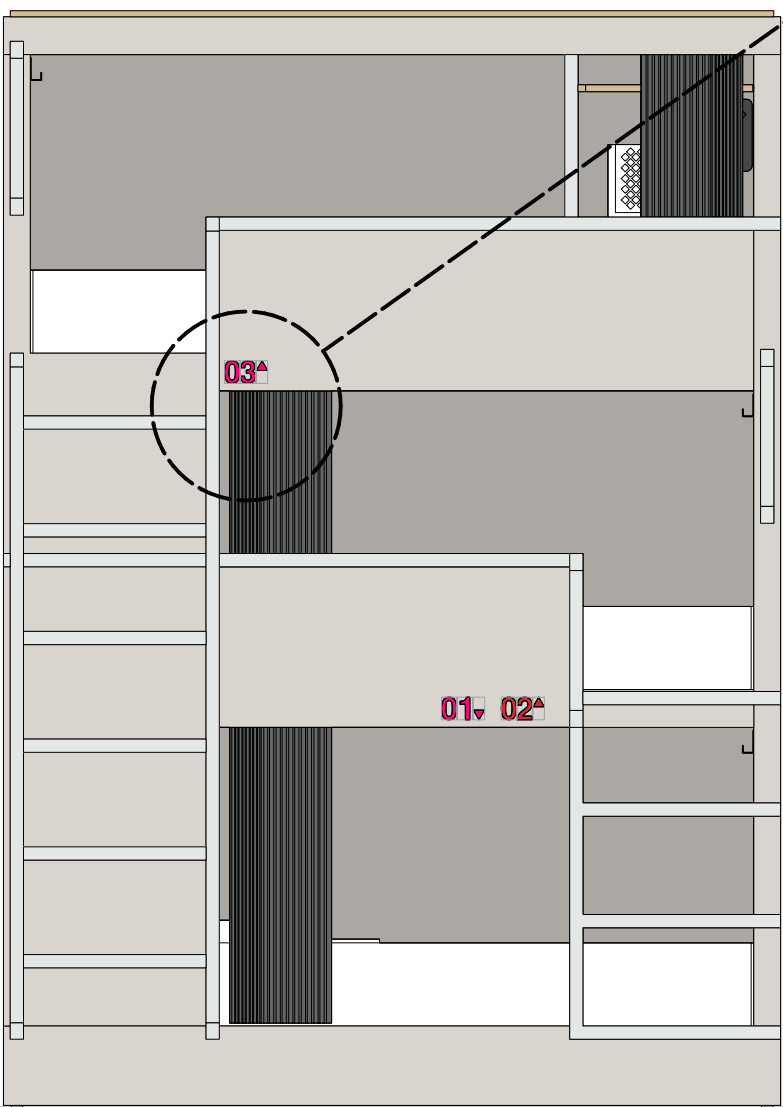

BUNKBED 3-A ELEVATIONS

 

SIGNAGE BAR
Signage numbers to be assigned after bunkbeds are installed.

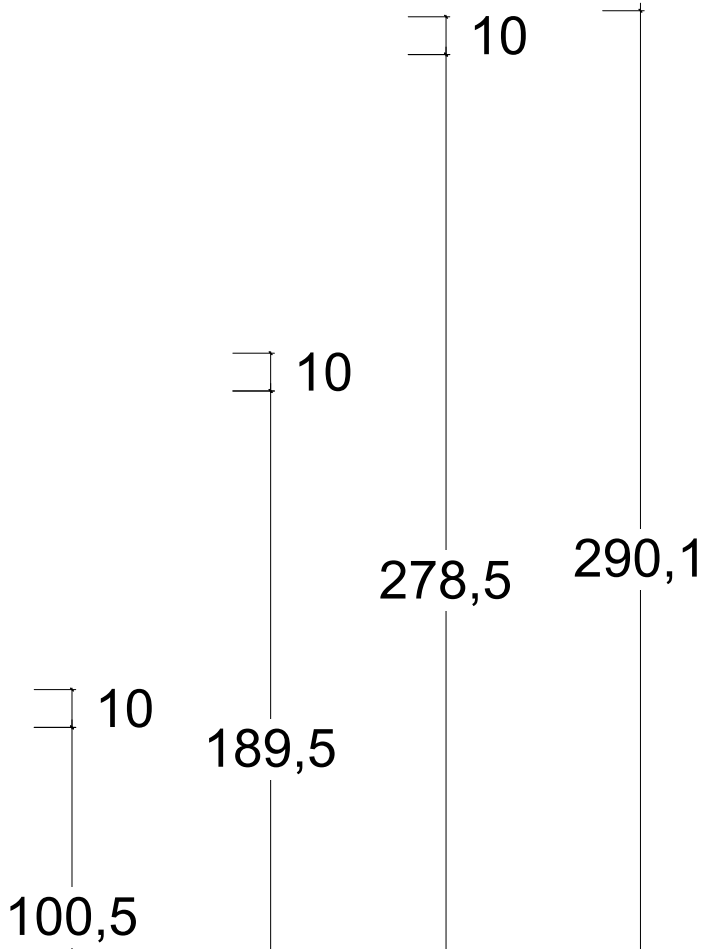

KEY

Index

A) 04.05.2026 Plan Set UP

All measurements have to be verified according to existing conditions by the contractor! Discrepancies must be reported immediately to the responsible project manager. The contractor has to produce fully dimensioned shop drawings prior to the start of the contract and they have to be approved by the client/ investor / interior designer

Project
CLINK 78 - BEDS



Project Address
CLINK 78
78 King's Cross Rd
London WC1X 9QG
United Kingdom

Client's Address
CLINK 78
78 King's Cross Rd
London WC1X 9QG
United Kingdom

Sheet Number 3-002 Total Sheets 82

Sheet Title TYPE 3 - SIGNAGE Level

File Name
260425_CLINK 78_BEDs AA DRAFT 03.vwx

Date	Sheet Size	Scale	Signed
28.04.26	A1		AA

Stefanie Jaensch INTERIOR DESIGNS

Global Headquarter | Stefanie Jaensch c/o WeWork
Taunusanlage 8 | 60329 Frankfurt a.M.


E-Mail info@stefaniejaensch.de | DE +49 (0) 174 6756098

www.stefaniejaensch.de

Legal address | Stefanie Jaensch | Offenbacher Landstraße 434 | 60599 Frankfurt a.M.



© 2023 All Rights Reserved | Stefanie Jaensch

BUNKBEDS TYPE 3 - LED LIGHTS PLAN


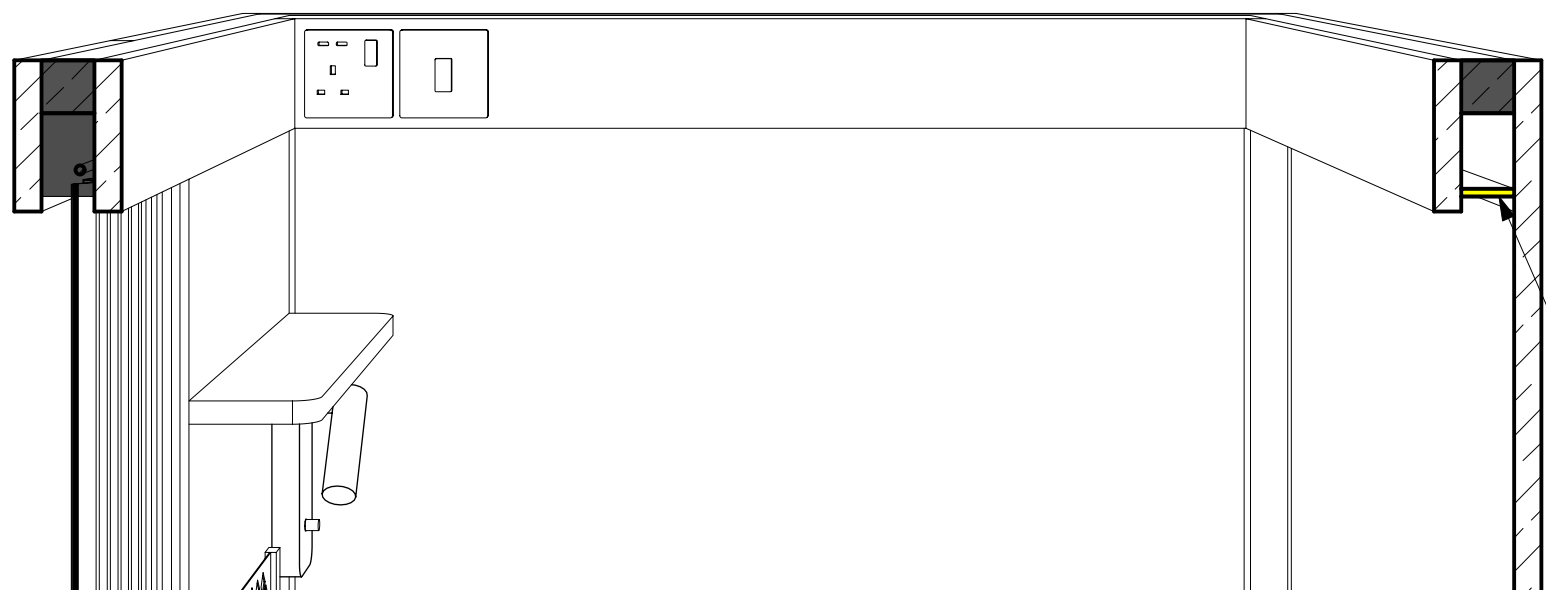


EE-L01
LED LIGHT 005_BUNKBED 2A
EE-L01/L02/L03/L04/L05/L06
LED light with light diffuser -
LED stripes - 2000 Calvin -
Warmwhite (in AI profile,
recessed)



LEVEL 3

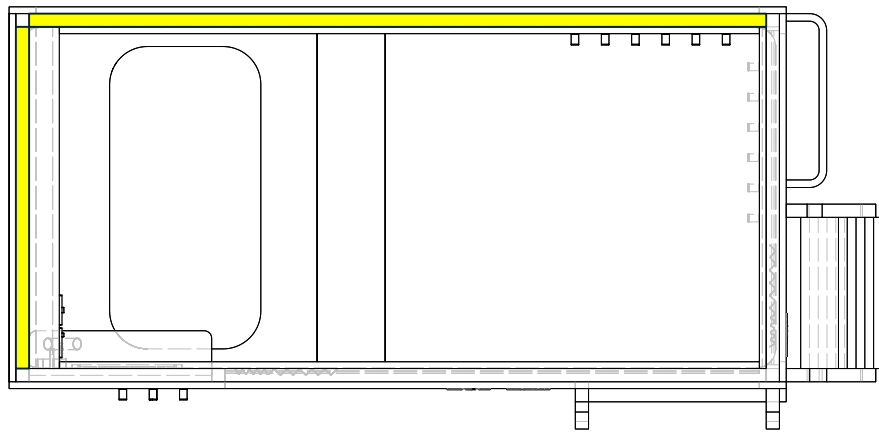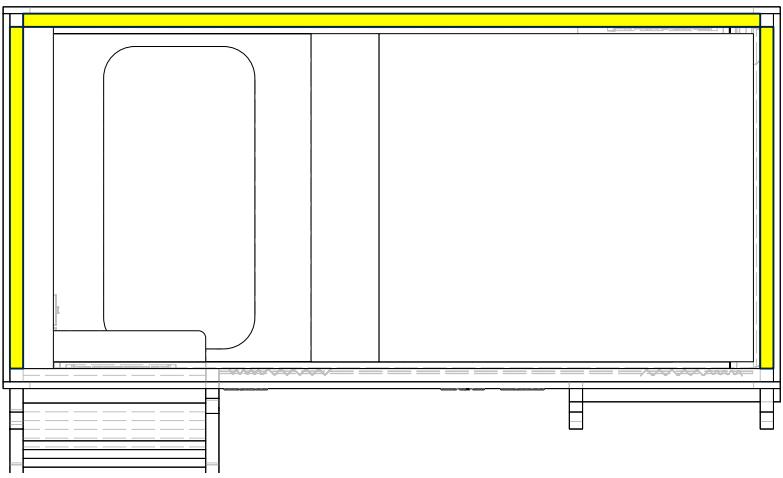

LEVEL 2

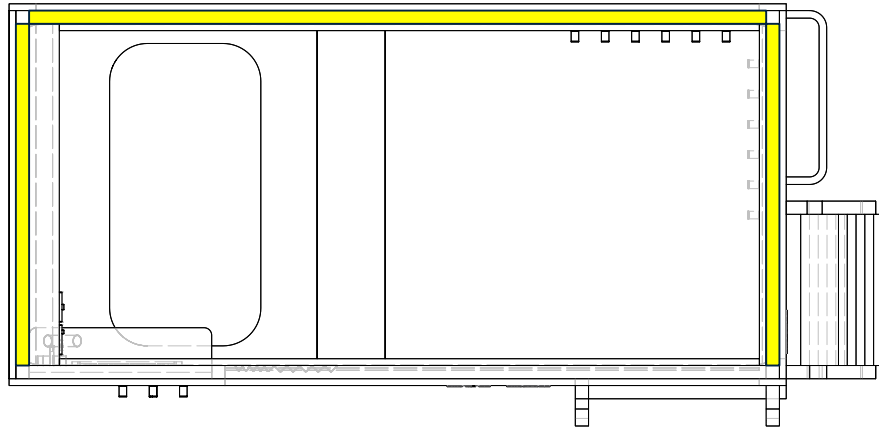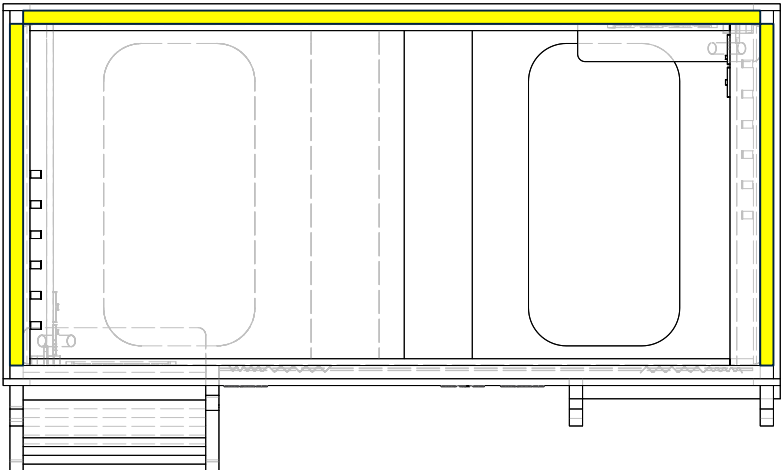


LEVEL 1

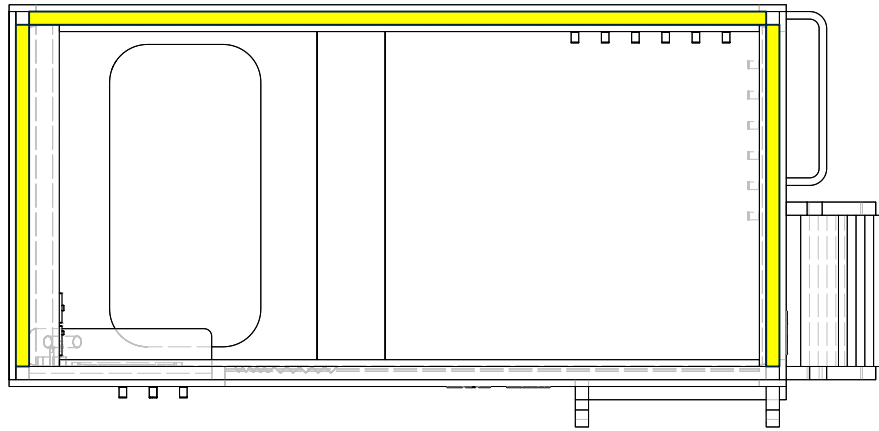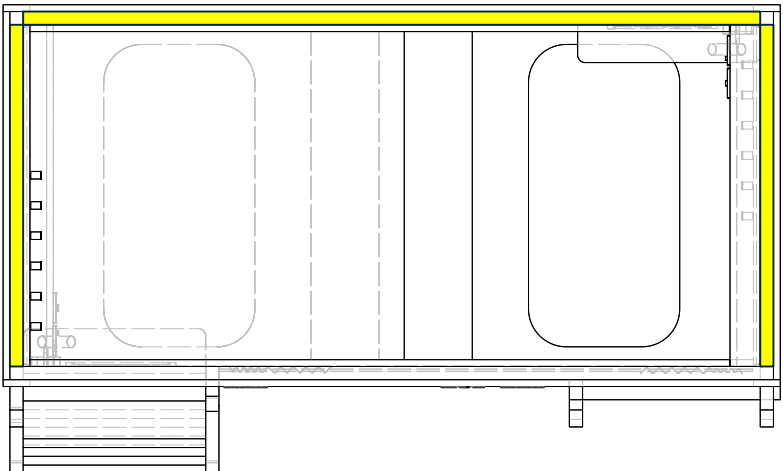

3-A

3-B

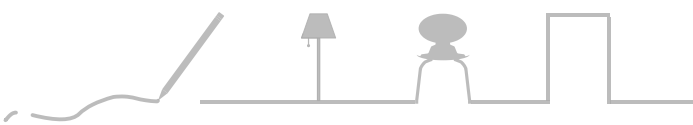

KEY

Index

A) 04.05.2026 Plan Set UP

All measurements have to be verified according to existing conditions by the contractor! Discrepancies must be reported immediately to the responsible project manager. The contractor has to produce fully dimensioned shop drawings prior to the start of the contract and they have to be approved by the client/ investor / interior designer

Project
CLINK 78 - BEDS



Project Address
CLINK 78
78 King's Cross Rd
London WC1X 9QG
United Kingdom


Client's Address
CLINK 78
78 King's Cross Rd
London WC1X 9QG
United Kingdom

Sheet Number	3-003	Total Sheets	82
Sheet Title	TYPE 3 - LED LIGHTS PLAN	Level	
File Name			
260425_CLINK 78_BEDs AA DRAFT 03.vwx			

Date	Sheet Size	Scale	Signed
28.04.26	A1		AA



Stefanie Jaensch INTERIOR DESIGNS
Global Headquarter | Stefanie Jaensch c/o WeWork
Taunusanlage 8 | 60329 Frankfurt a.M.
E-Mail info@stefaniejaensch.de | DE +49 (0) 174 6756098
www.stefaniejaensch.de
Legal address | Stefanie Jaensch | Offenbacher Landstraße 434 | 60599 Frankfurt a.M.
© 2023 All Rights Reserved | Stefanie Jaensch

BUNKBEDS TYPE 3 - CURTAINS PLAN


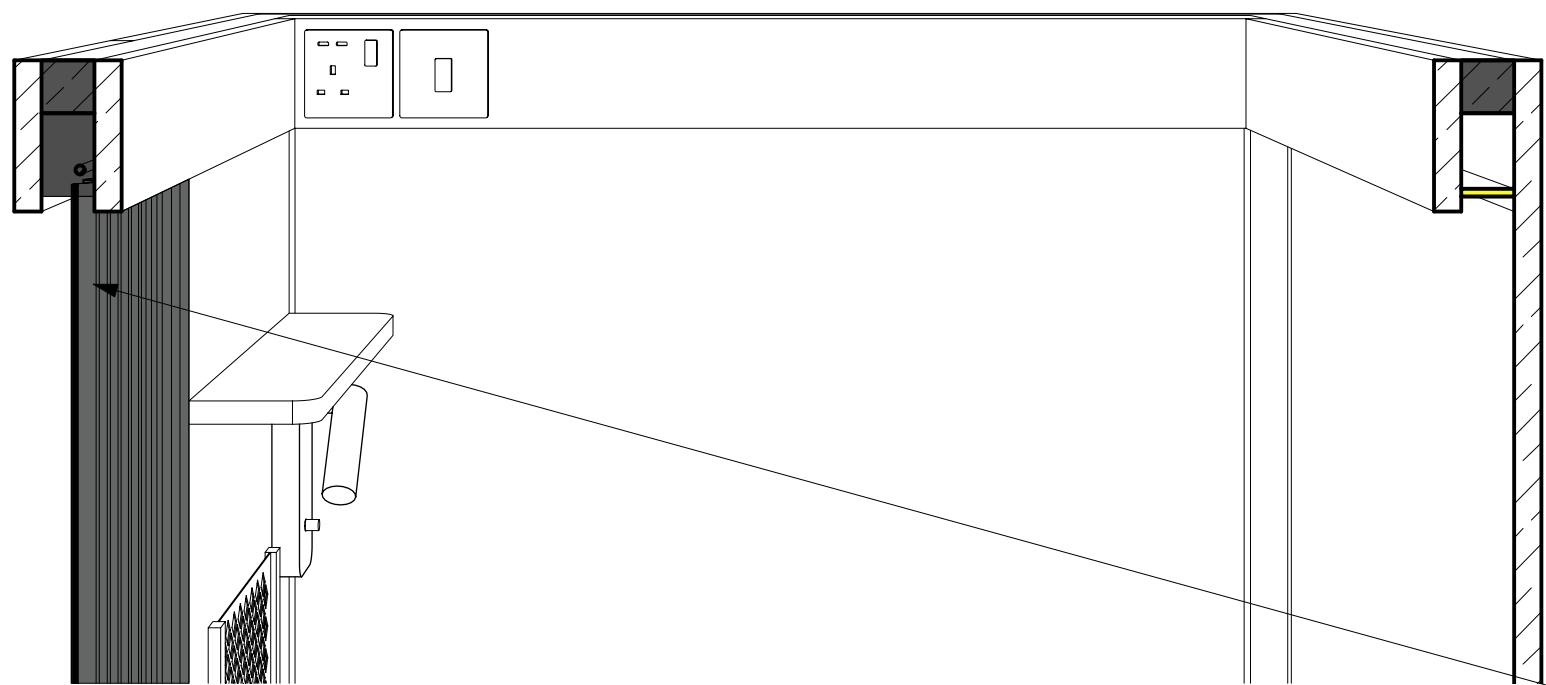


FF-C01
CURTAINS 02_BUNKBED 2-AB
FF-C01/C02/C03 Privacy
curtain - Washable Fabric
-colour: dark grey/ anthracite
less fold -Almost 1:1 fold factor
to open horizontally-
fire-retardant fabric - Matt
Finish - CURTAINS-LUNA
BLACKOUT-by SKOPOS-
TEX L15 GUNMETAL-(RAL
colour tbc by Clink)



LEVEL 3

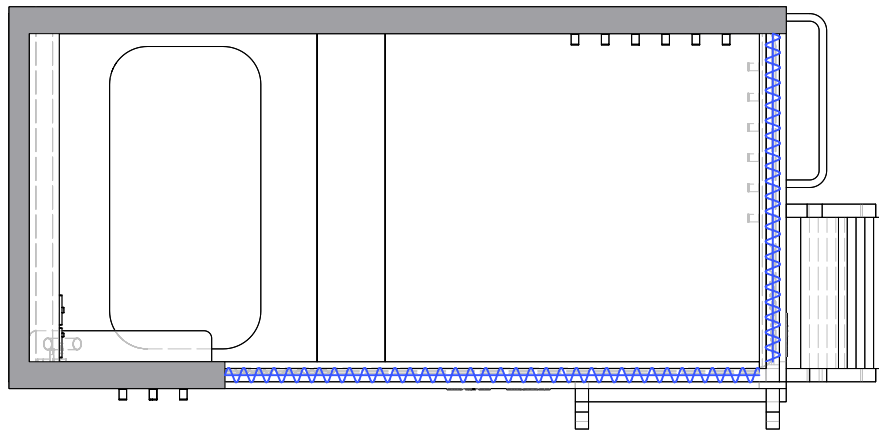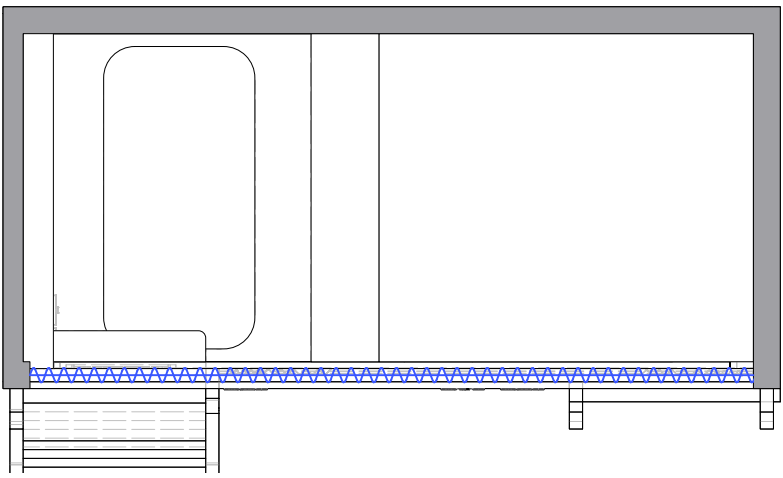

LEVEL 2

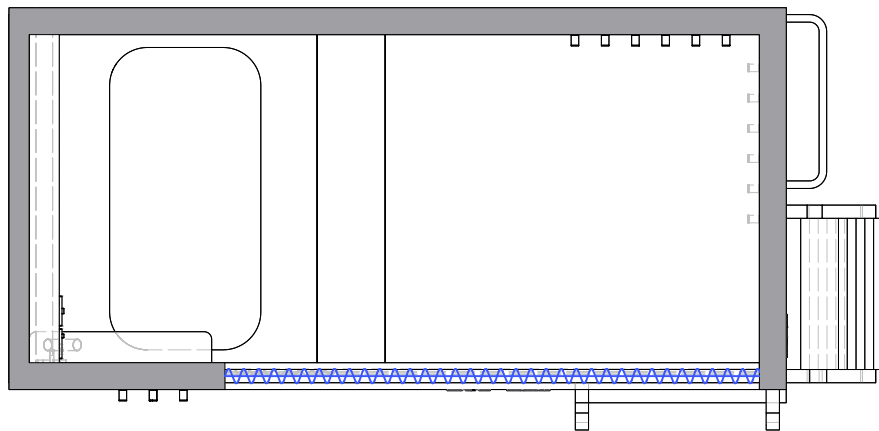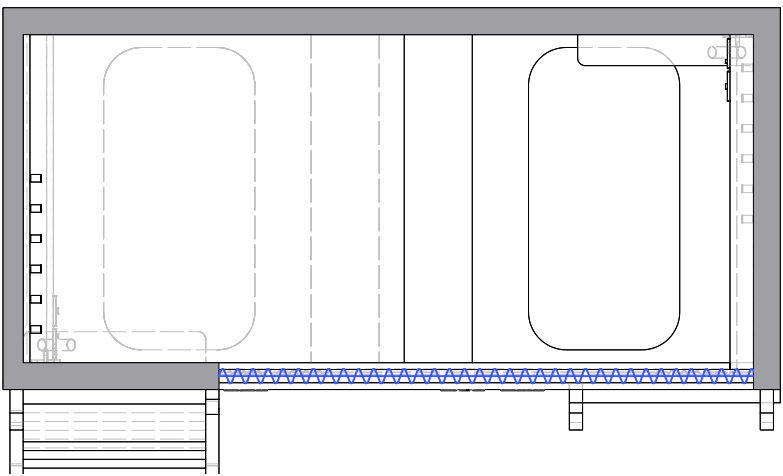


LEVEL 1

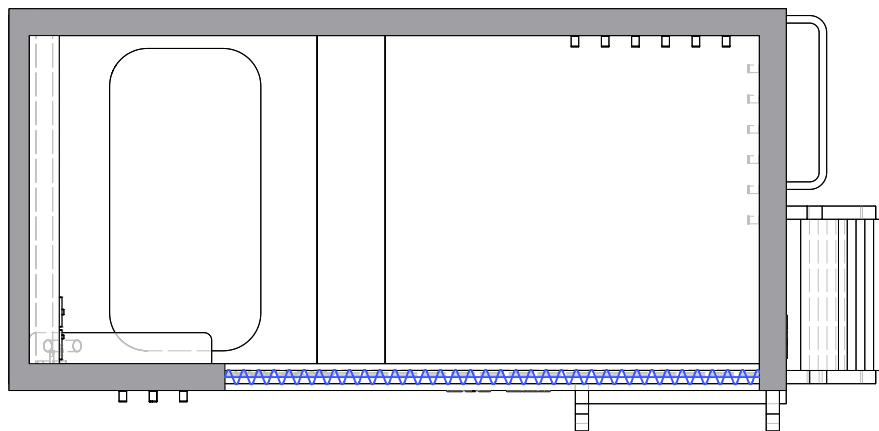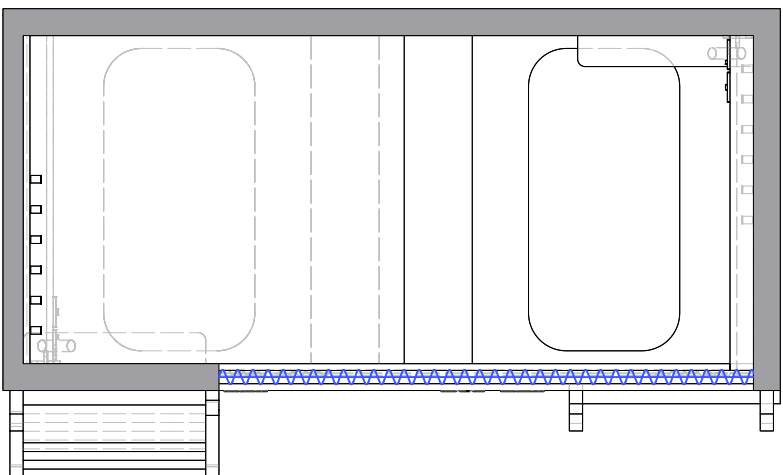

3-A

3-B

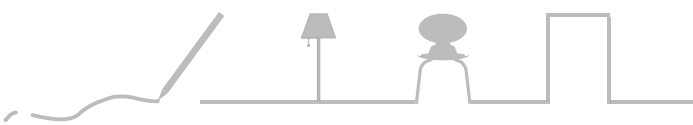

KEY

Index

A) 04.05.2026 Plan Set UP

All measurements have to be verified according to existing conditions by the contractor! Discrepancies must be reported immediately to the responsible project manager. The contractor has to produce fully dimensioned shop drawings prior to the start of the contract and they have to be approved by the client/ investor / interior designer

Project
CLINK 78 - BEDS



Project Address
CLINK 78
78 King's Cross Rd
London WC1X 9QG
United Kingdom

Client's Address
CLINK 78
78 King's Cross Rd
London WC1X 9QG
United Kingdom

Sheet Number	3-004	Total Sheets	82
--------------	-------	--------------	----


Sheet Title	TYPE 3 - CURTAINS PLAN	Level	
-------------	------------------------	-------	--

File Name
260425_CLINK 78_BEDs AA DRAFT 03.vwx

Date	Sheet Size	Scale	Signed
28.04.26	A1		AA

Stefanie Jaensch INTERIOR DESIGNS
Global Headquarter | Stefanie Jaensch c/o WeWork
Taunusanlage 8 | 60329 Frankfurt a.M.
E-Mail info@stefaniejaensch.de | DE +49 (0) 174 6756098
www.stefaniejaensch.de
Legal address | Stefanie Jaensch | Offenbacher Landstraße 434 | 60599 Frankfurt a.M.
© 2023 All Rights Reserved | Stefanie Jaensch

BUNKBEDS - TYPE 3-A (TRIPLE)

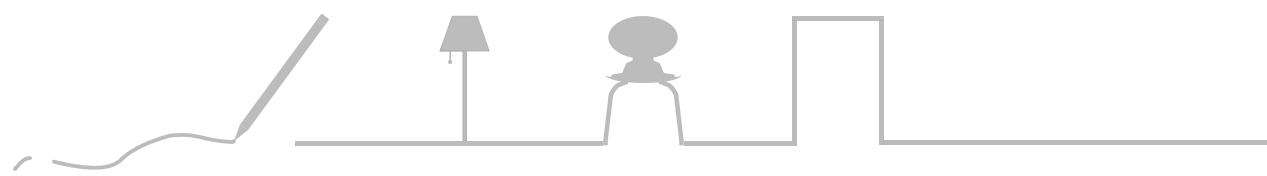


Stefanie Jaensch

INTERIOR DESIGNS

For



3-A

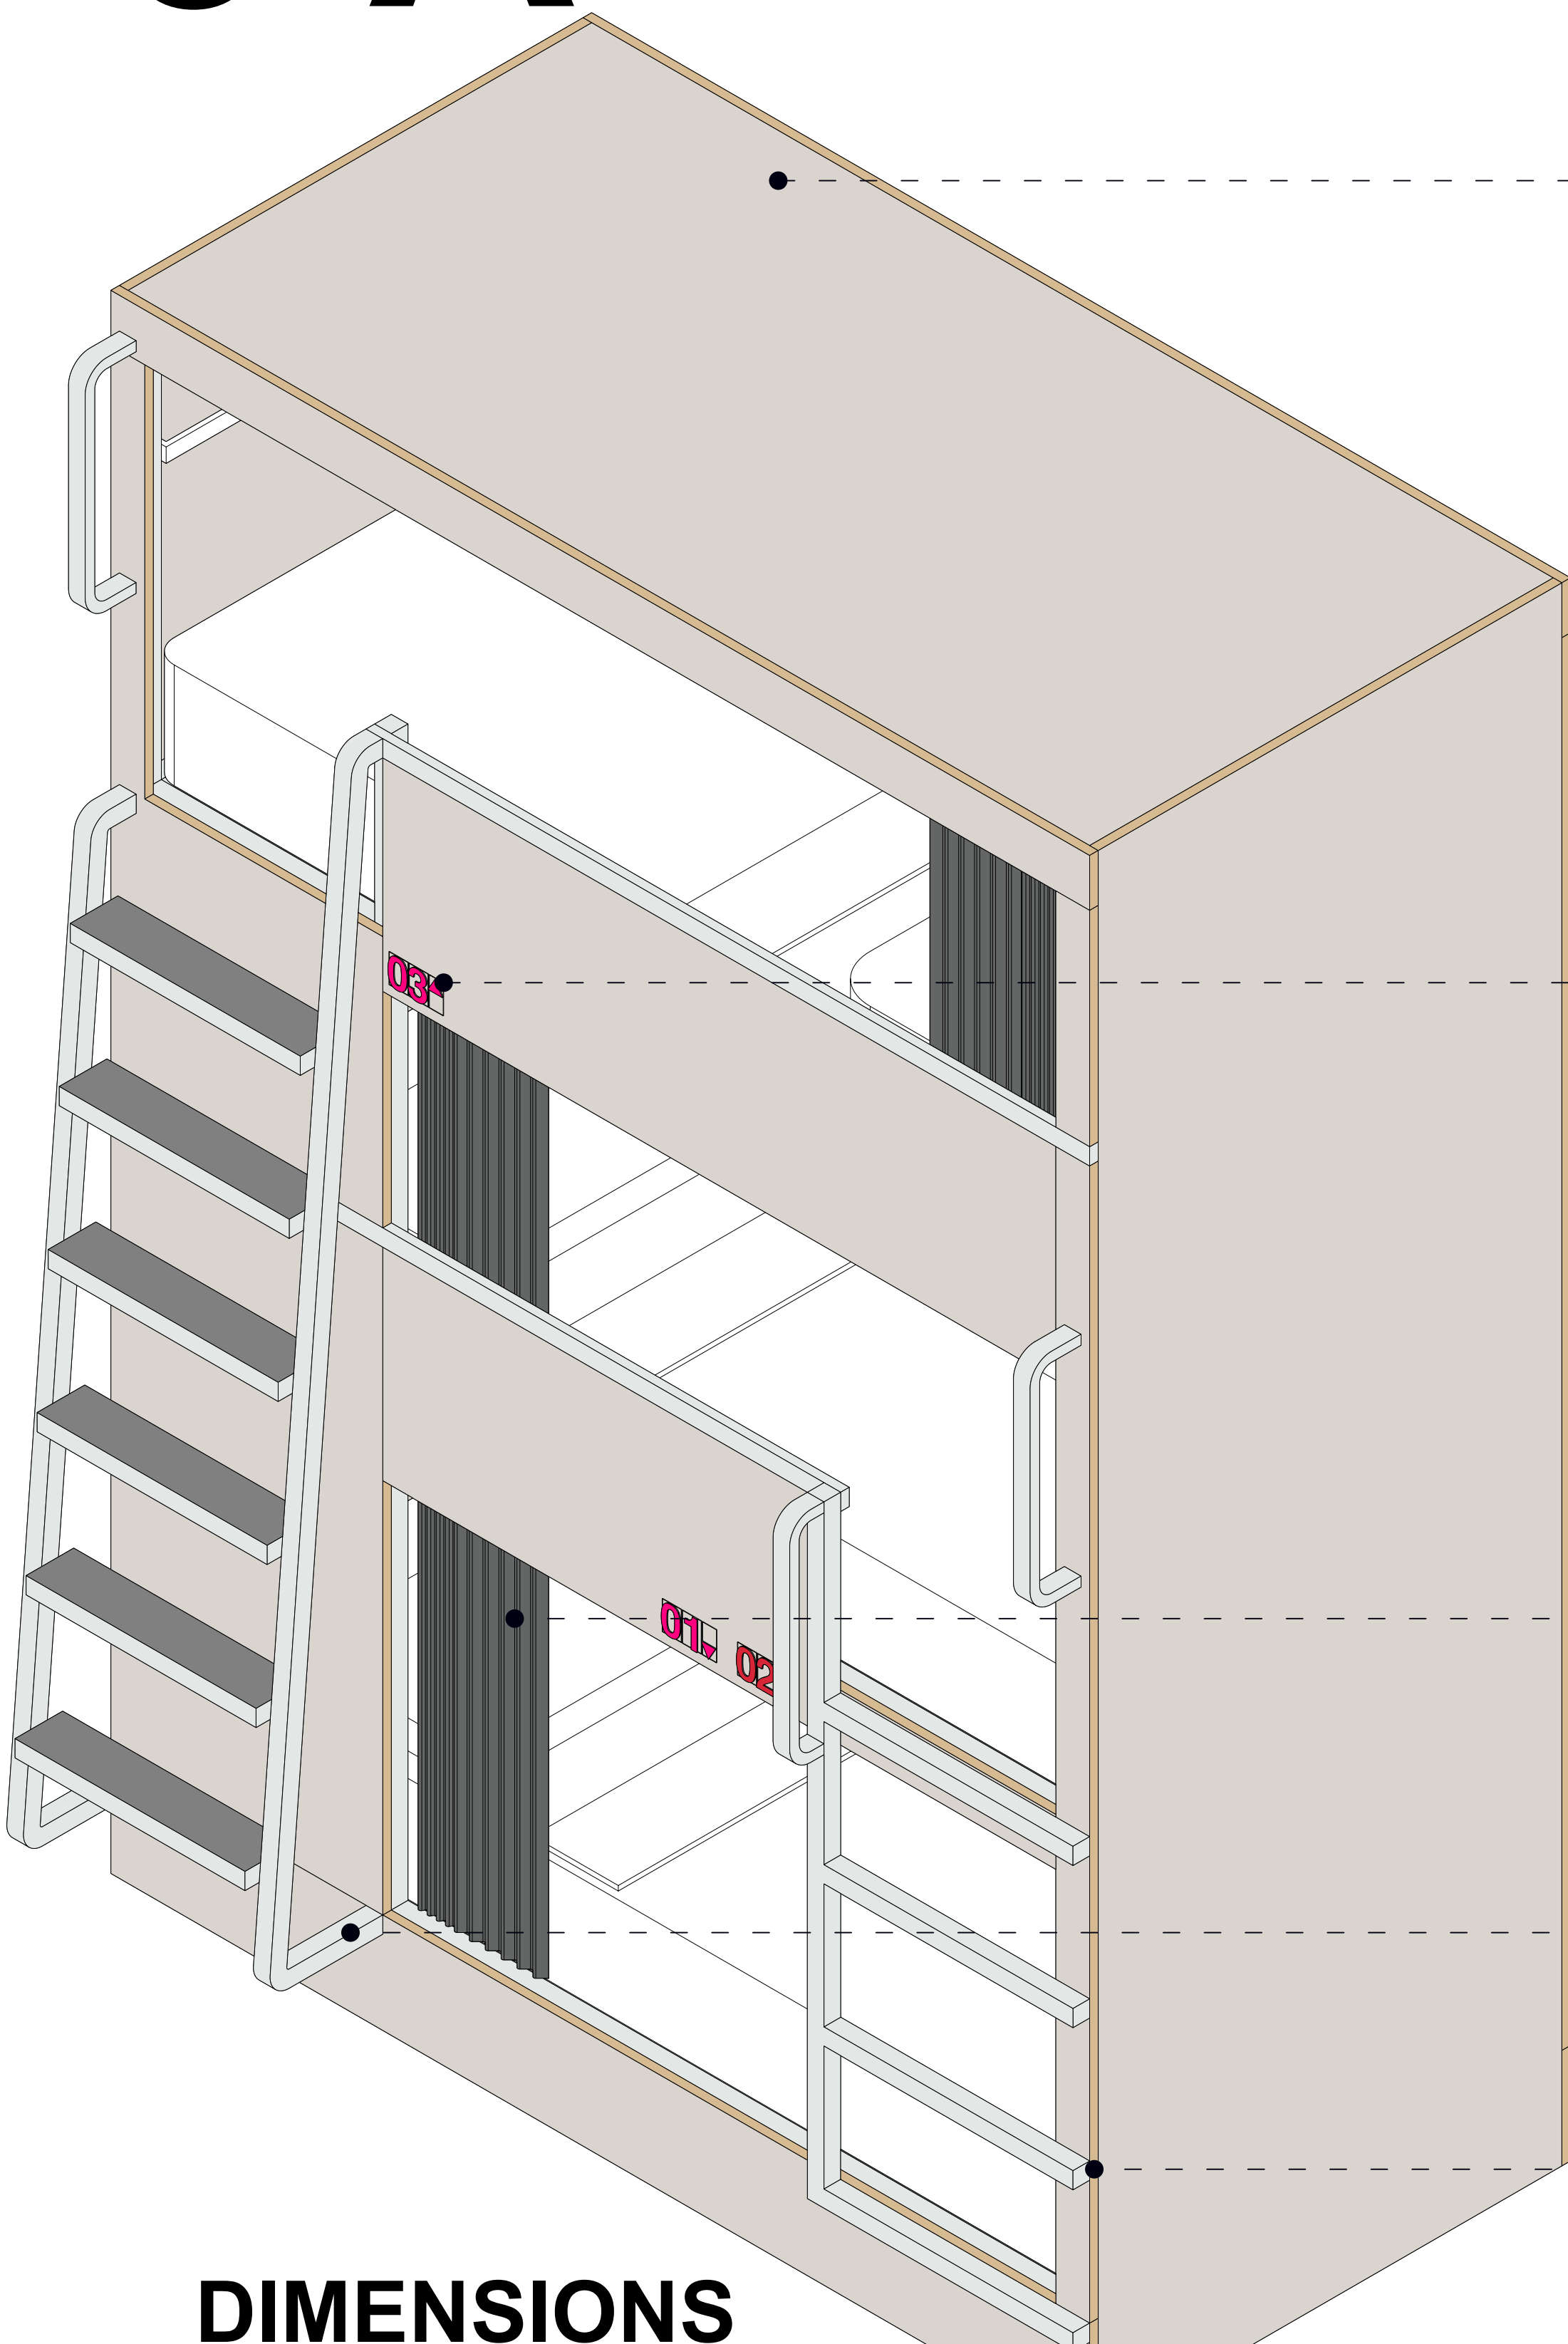


CC-M01
Cladding - Laminated
chipboard - Colour
RAL 7044 (Final RAL
Colour TBC by Clink),
Thickness 18m

AA-S01
SIGNAGE - Numbers -
laser-cut acrylic or MDF -
thickness 5mm - spray
painted - RAL 3020 Red &
RAL 4010 Rose - font
according to wayfinding
signage design
(RAL Colour TBC by Clink)

FF-C01 Metal ring curtains with
a sturdy/durable pole
Privacy curtain - washable
textile - colour: dark grey/
anthracite less fold - Almost 1:1
fold factor to open horizontally -
fire-retardant fabric
LUNA BLACKOUT by SKOPOS
TEXTURED L15 GUNMETAL
(Colour TBC by Clink)

SS-F/L/G Ladder/Guard - 3.5x3.5
cm Powder Coated Steel
Structure - Colour to match
Telegrey RAL 7047 - Semi gloss
finish (RAL Colour TBC by Clink)

CC-M07 Visible Edges
Plywood edges

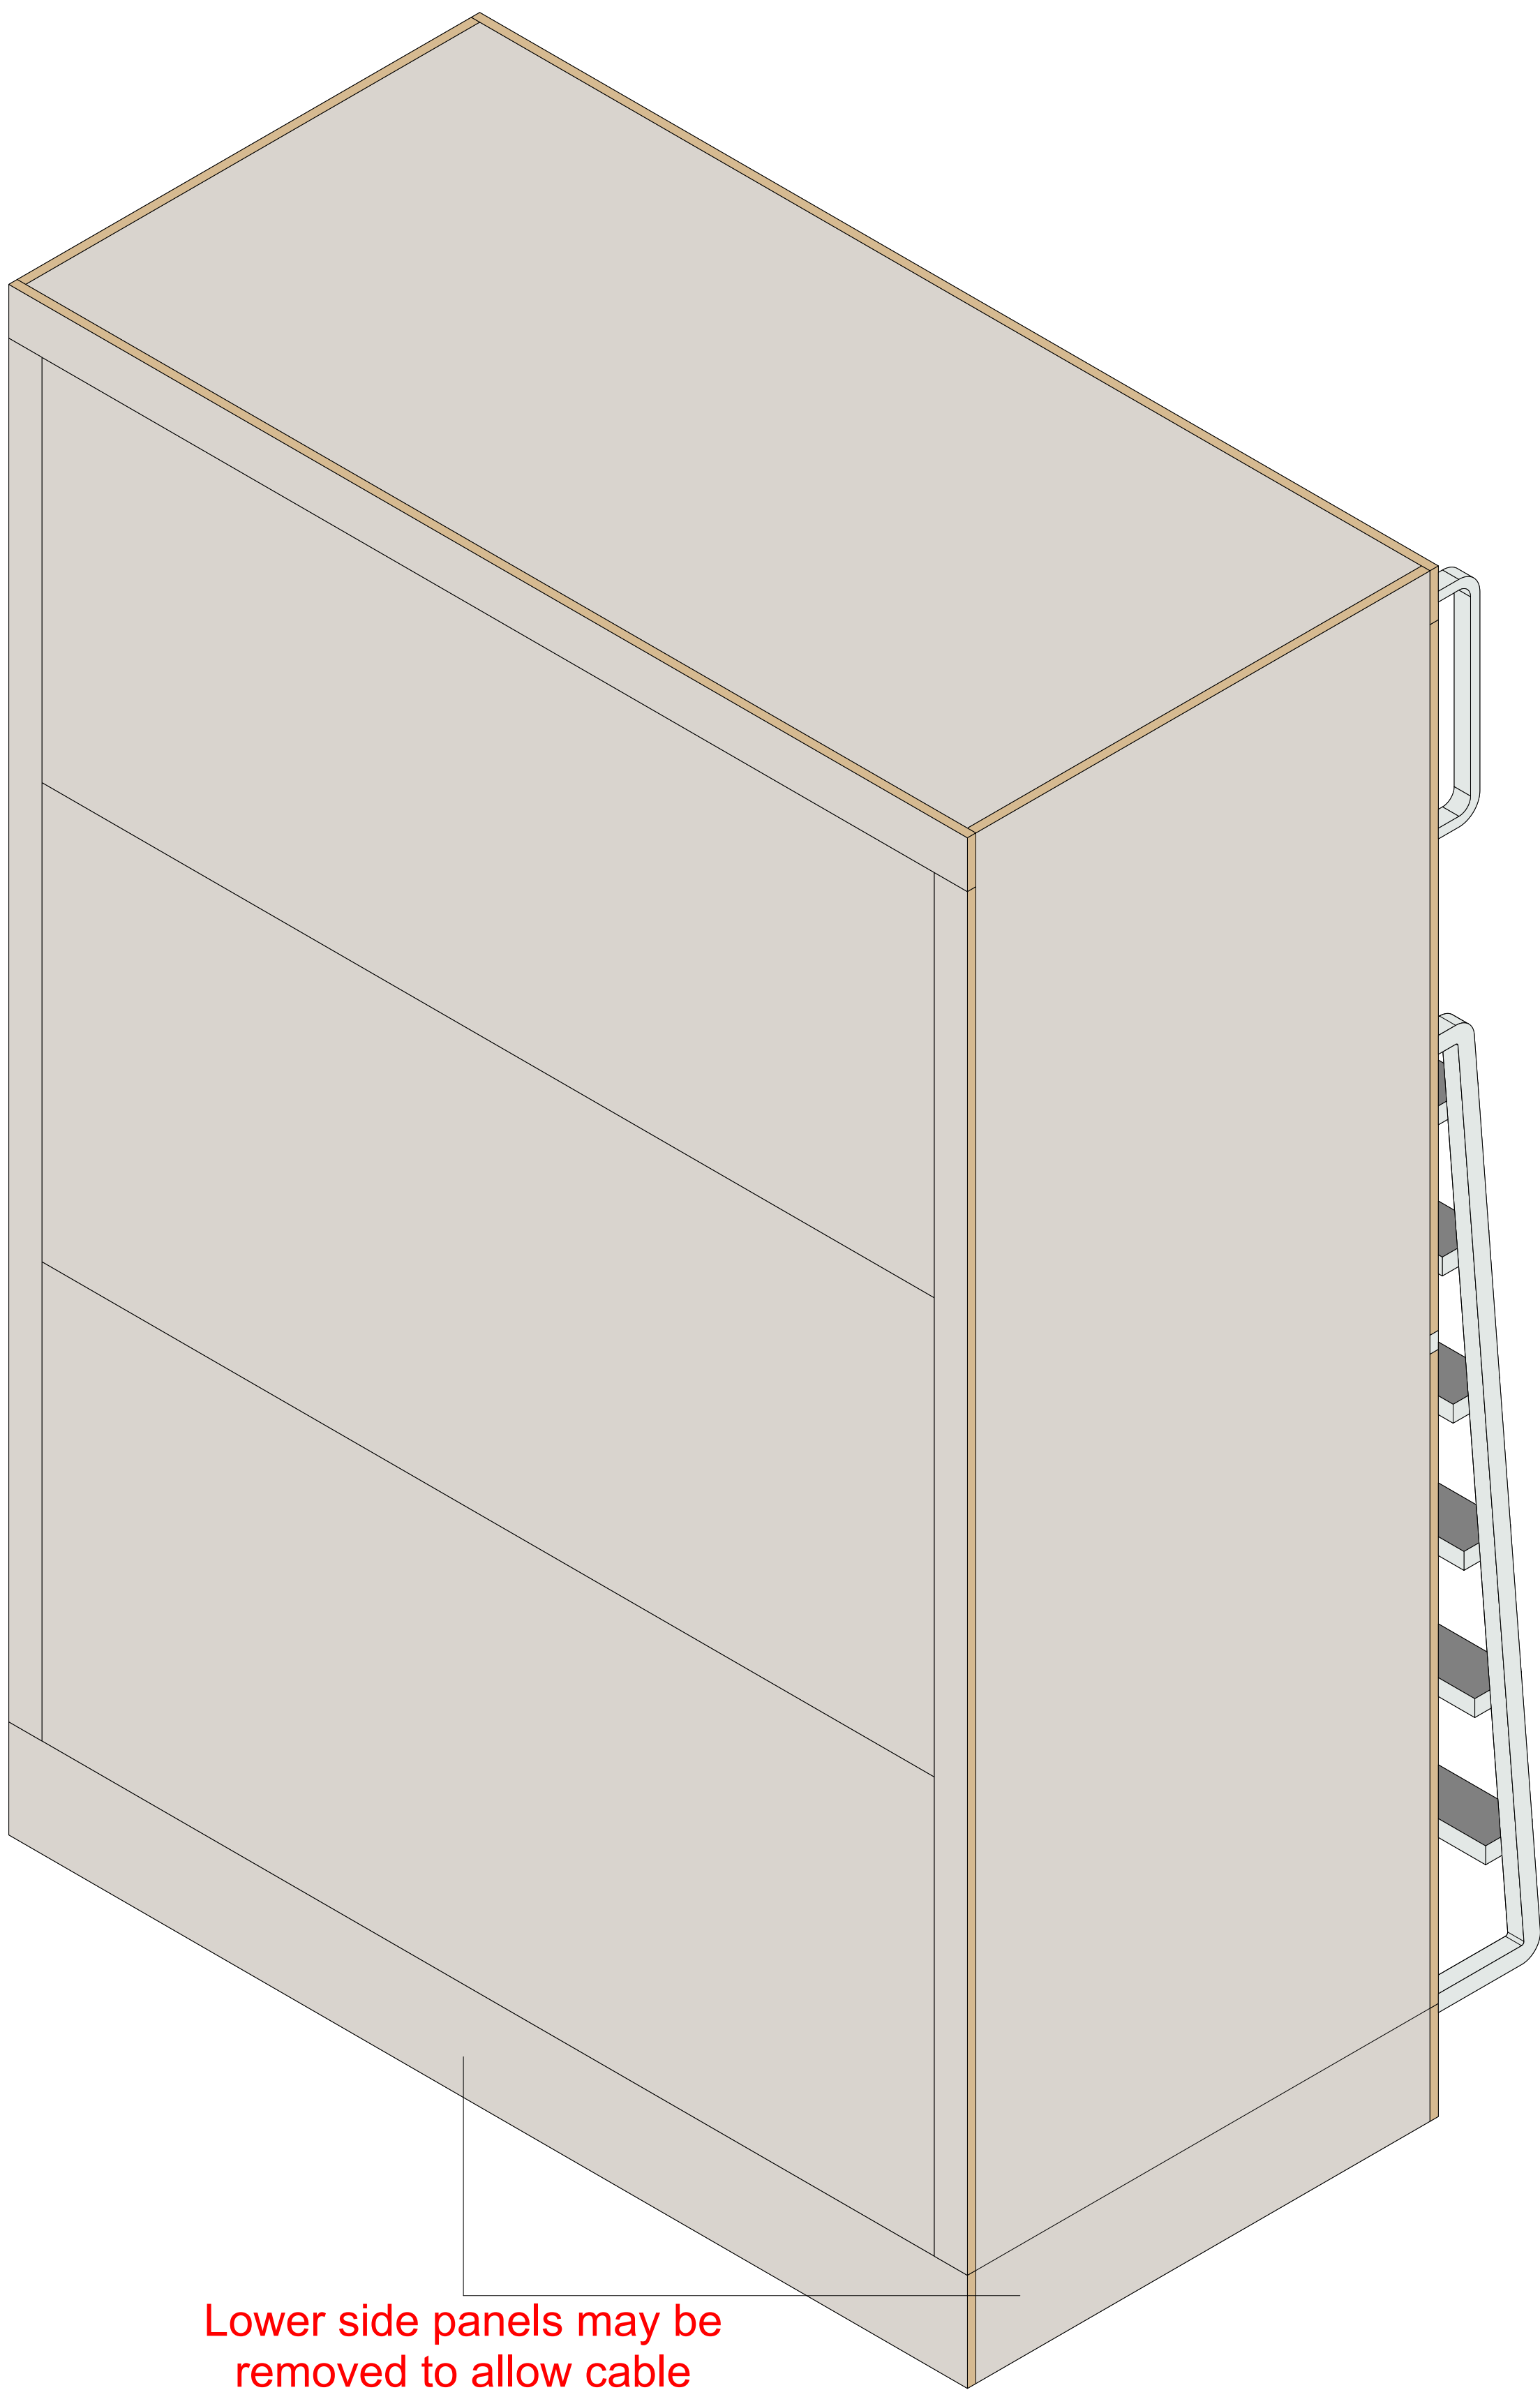



Lower side panels may be
removed to allow cable
connections.

DIMENSIONS

101 x 205.6 x 290.1 (WxLxH)cm

DRAFT

BUNKBEDS - TYPE 3-A (TRIPLE) - GA PLAN

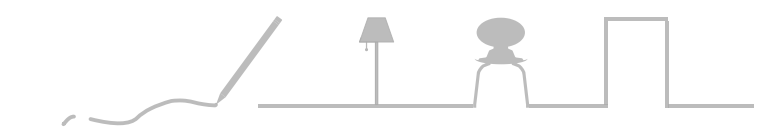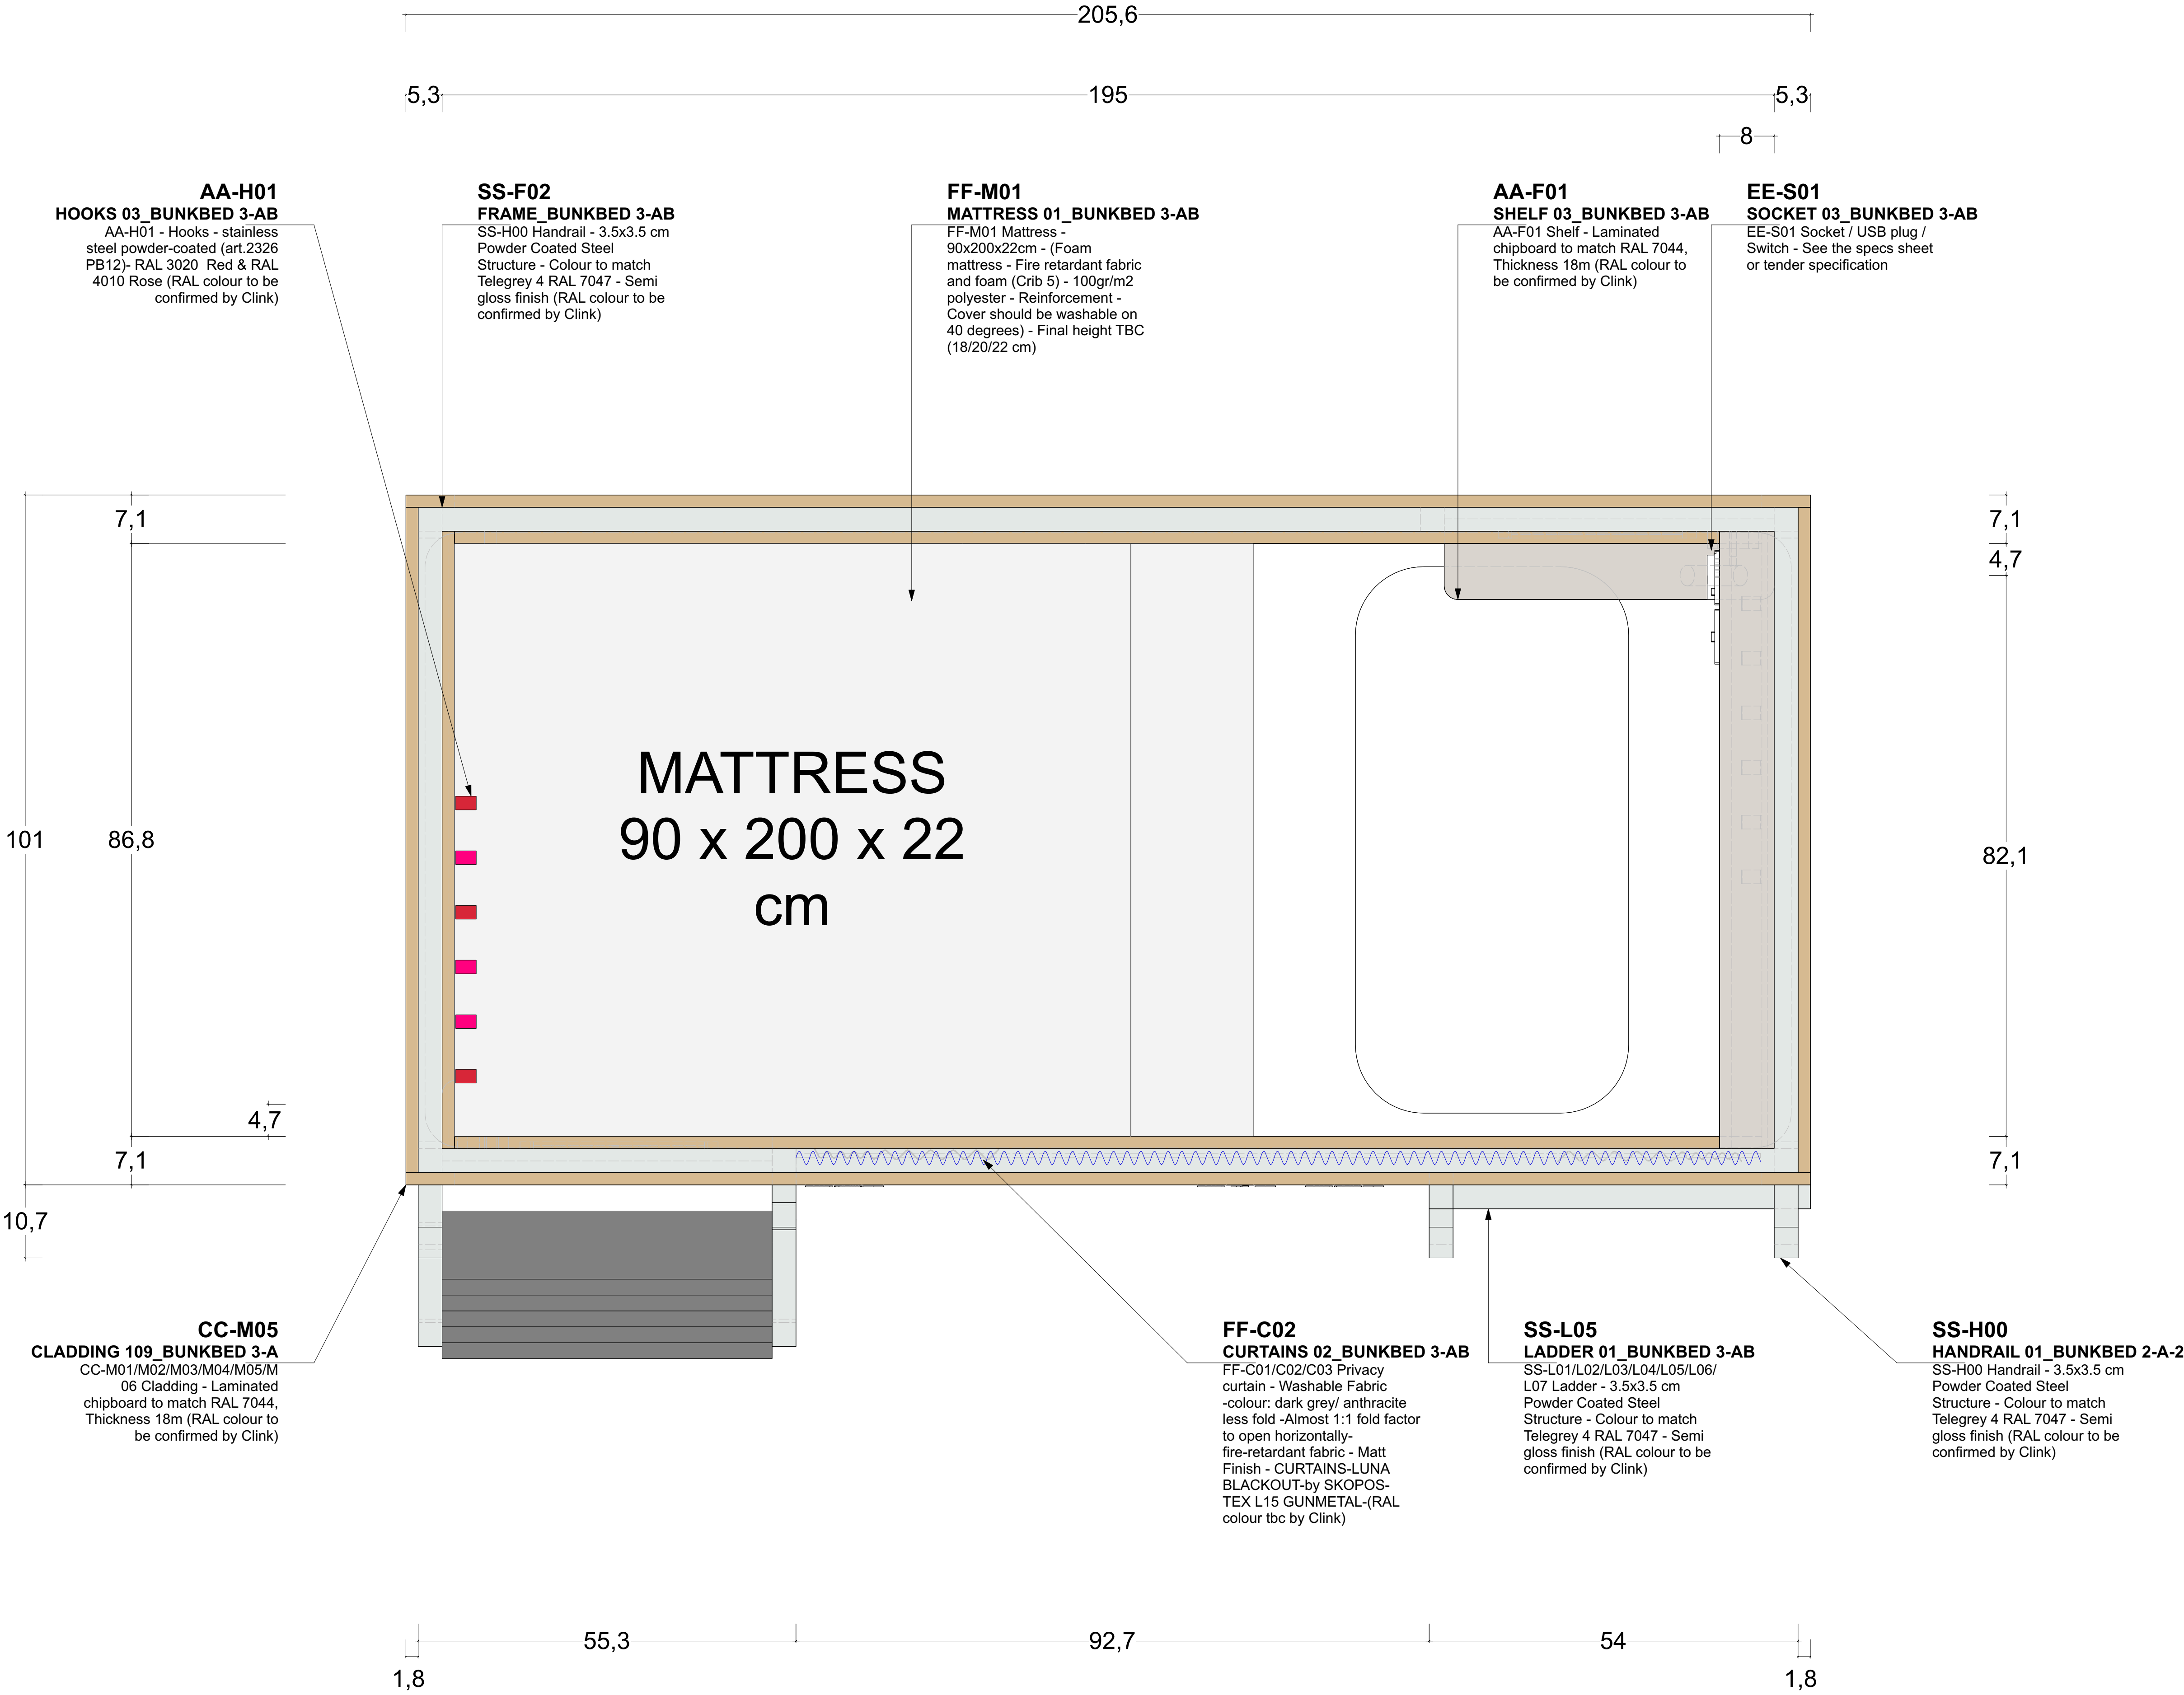

KEY

Index

A) 04.05.2026 Plan Set UP

All measurements have to be verified according to existing conditions by the contractor! Discrepancies must be reported immediately to the responsible project manager. The contractor has to produce fully dimensioned shop drawings prior to the start of the contract and they have to be approved by the client/ investor / interior designer

Project

CLINK 78 - BEDS

Logo



Project Address

CLINK 78
78 King's Cross Rd
London WC1X 9QG
United Kingdom

Client's Address

CLINK 78
78 King's Cross Rd
London WC1X 9QG
United Kingdom

Sheet Number	3-A-601	Total Sheets	82
--------------	---------	--------------	----

Sheet Title	BUNKBED 3-A GA	Level	
-------------	----------------	-------	--

File Name	260425_CLINK 78_BEDs AA DRAFT 03.vwx
-----------	--------------------------------------

Date	28.04.26	Sheet Size	A1	Scale	1:5	Signed	AA
------	----------	------------	----	-------	-----	--------	----

Stefanie Jaensch INTERIOR DESIGNS

Global Headquarter | Stefanie Jaensch c/o WeWork

Taunusanlage 8 | 60329 Frankfurt a.M.







E-Mail info@stefaniejaensch.de | DE +49 (0) 174 6756098

www.stefaniejaensch.de

Legal address | Stefanie Jaensch | Offenbacher Landstraße 434 | 60599 Frankfurt a.M.

© 2023 All Rights Reserved | Stefanie Jaensch

BUNKBEDS - TYPE 3-A (TRIPLE) - FRONT ELEVATION

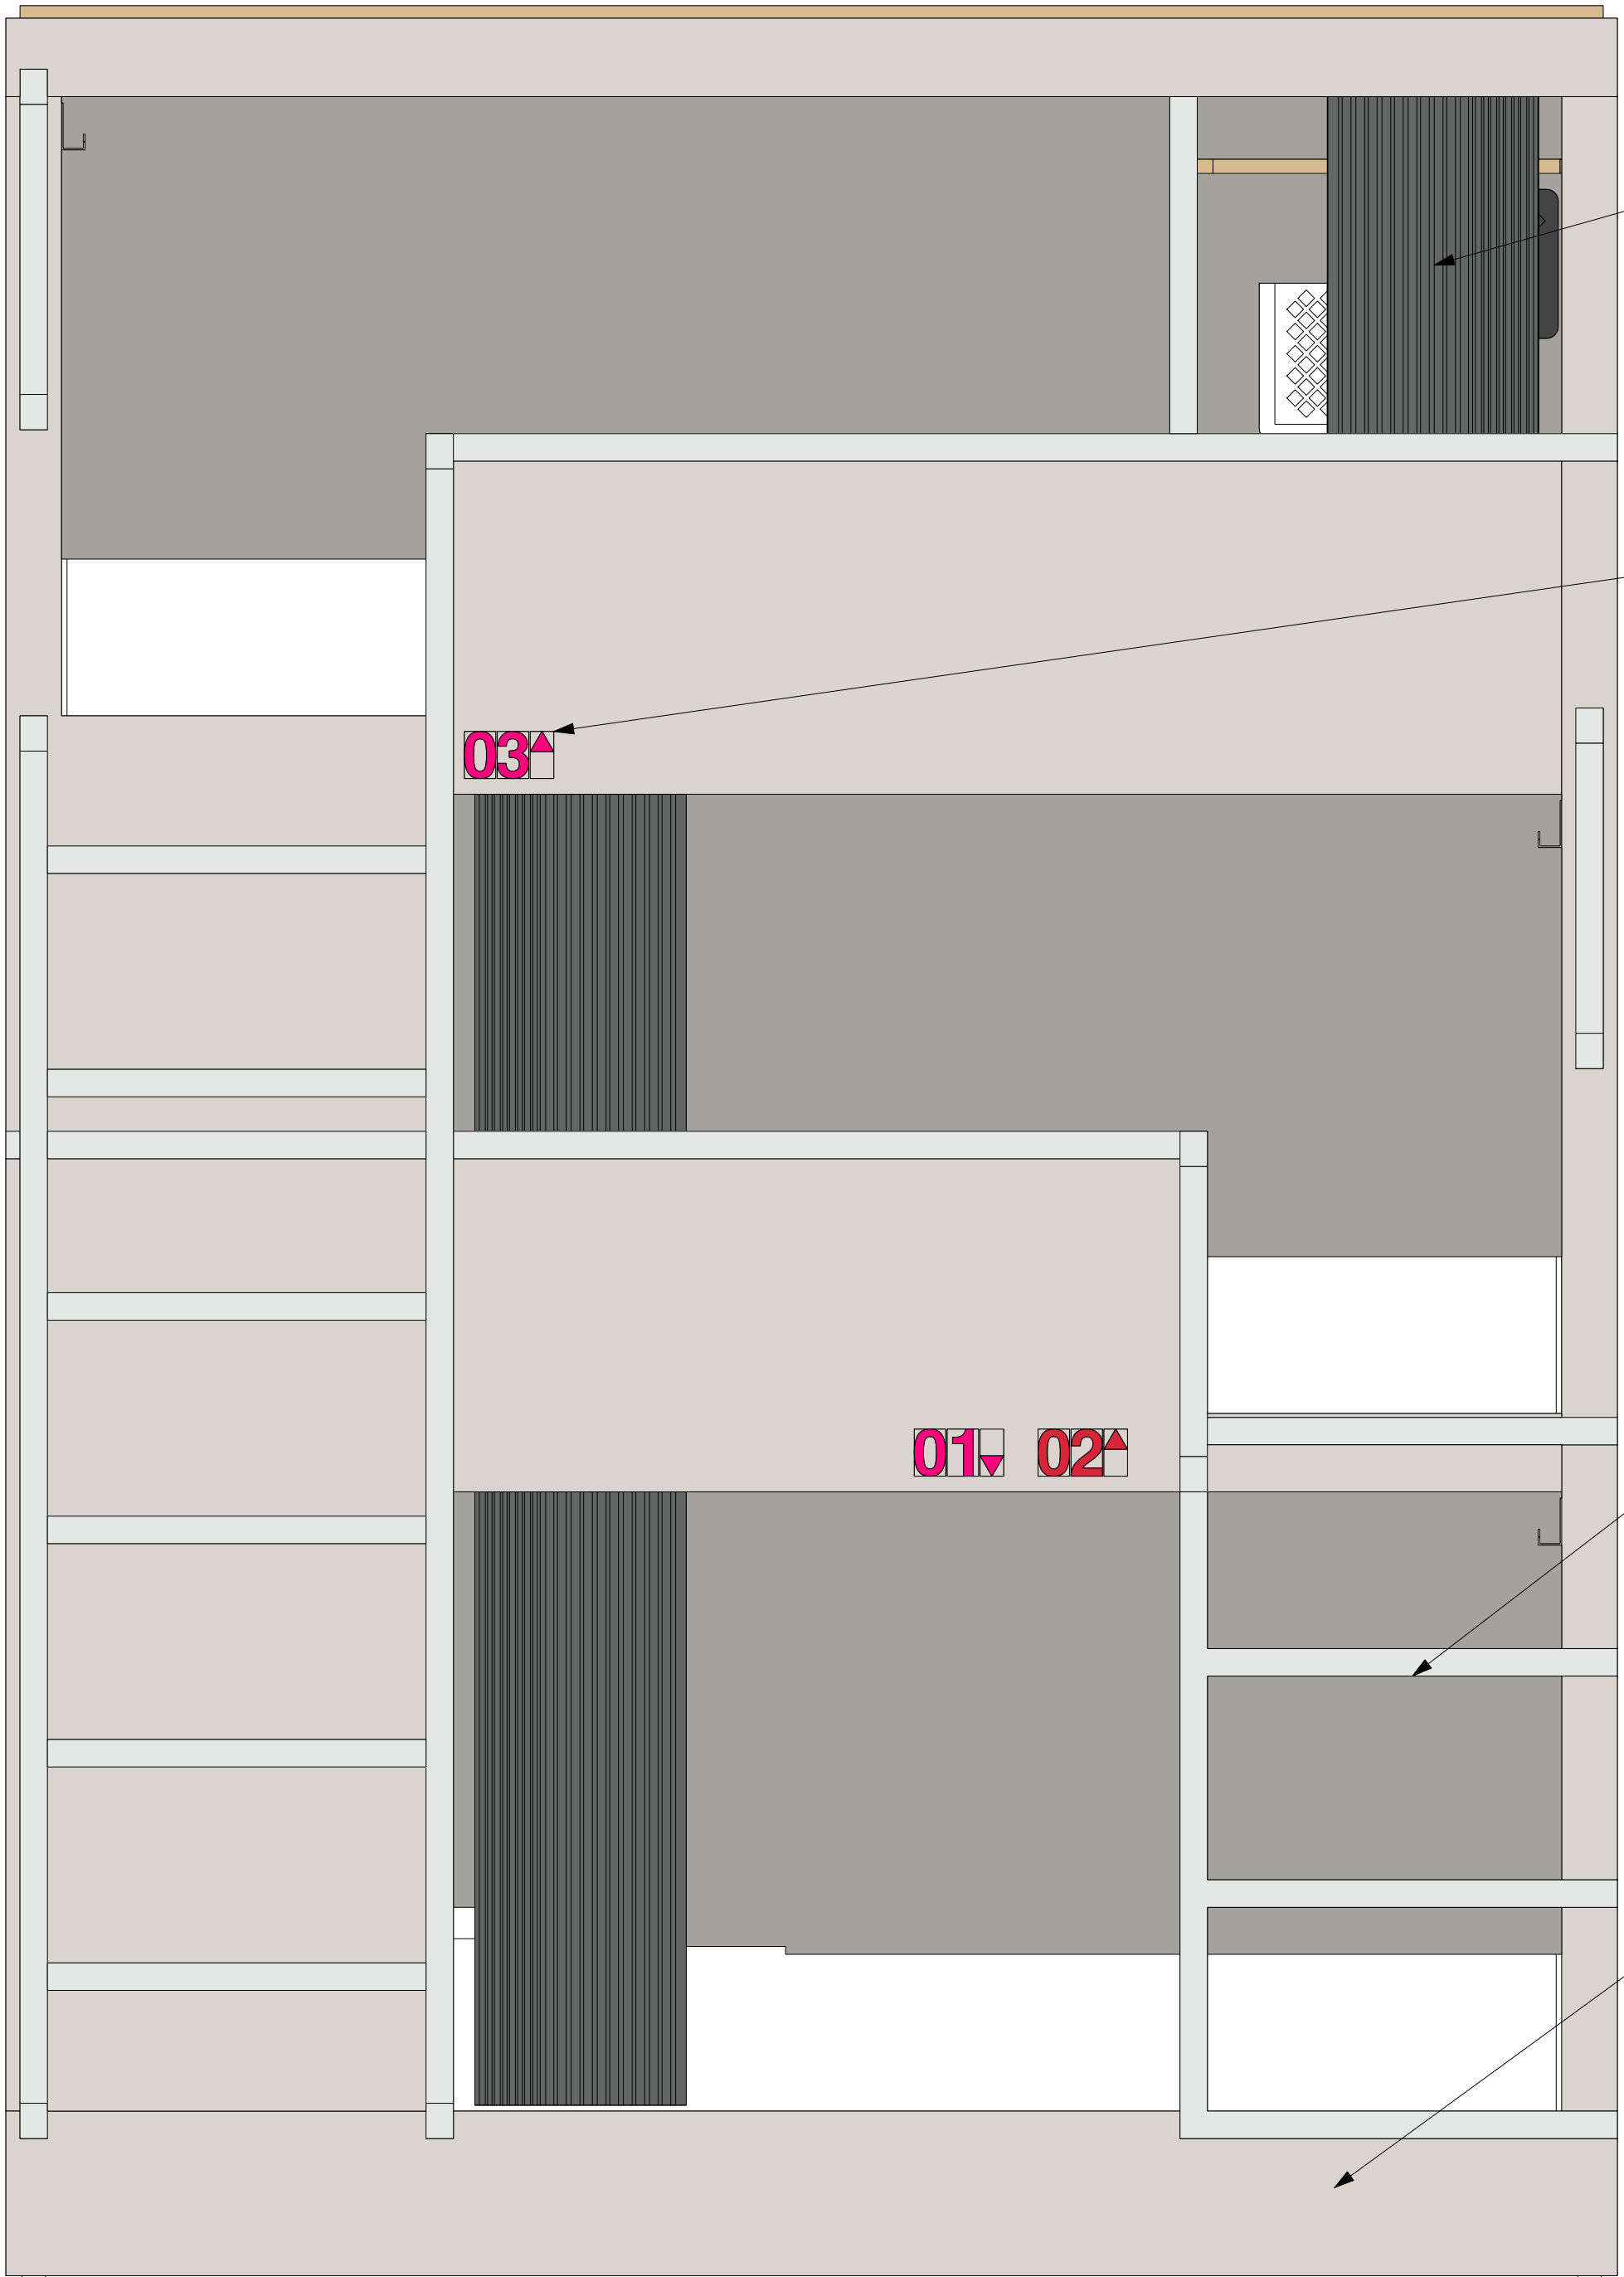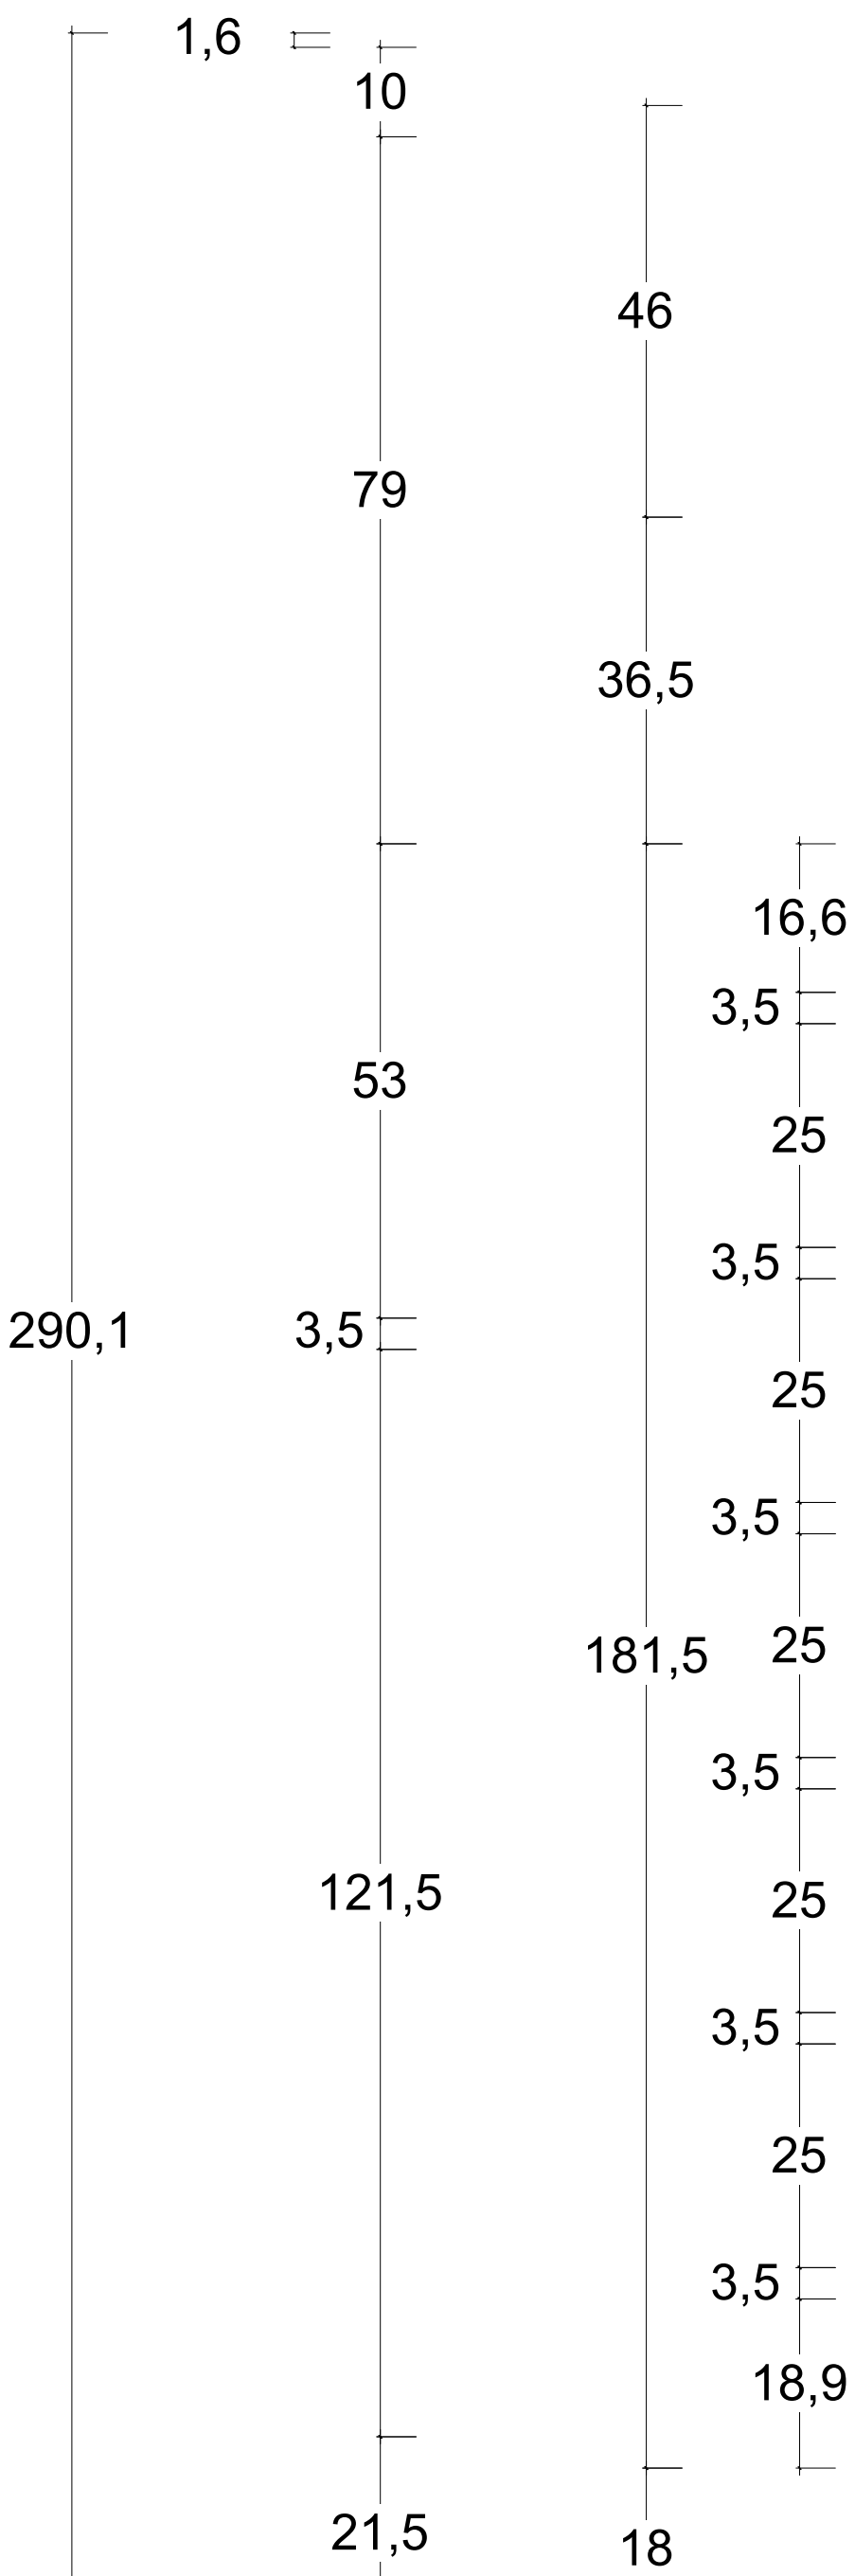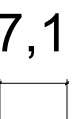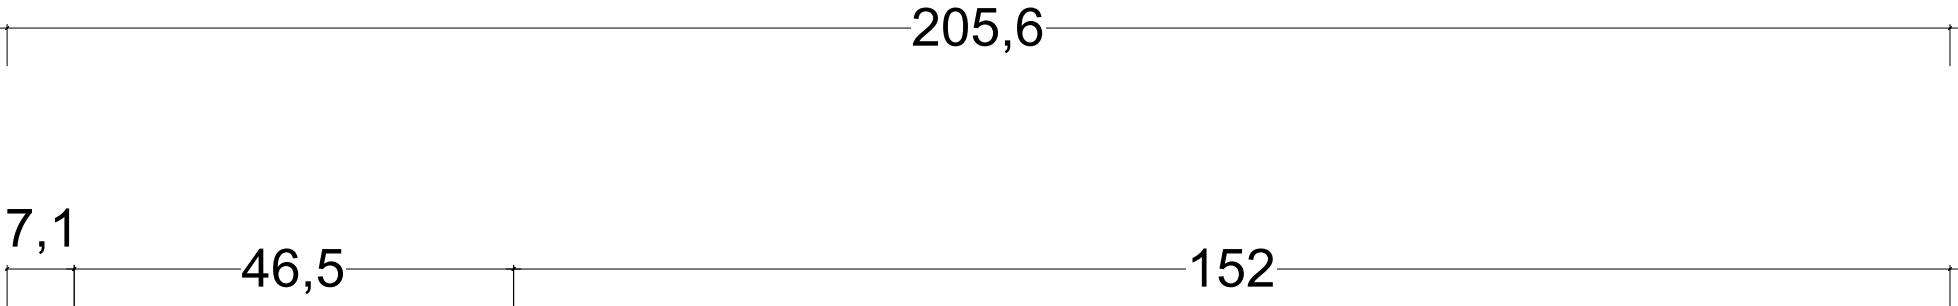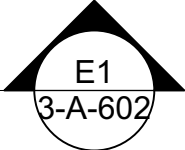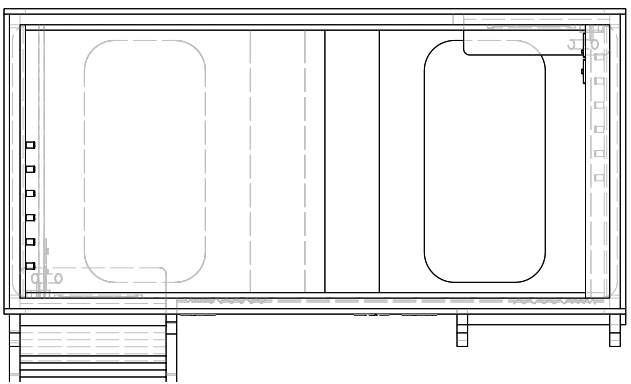


CC-M05
CLADDING 152_BUNKBED 3-A
CC-M01/M02/M03/M04/M05/M
06 Cladding - Laminated
chipboard to match RAL 7044,
Thickness 18m (RAL colour to
be confirmed by Clink)

AA-S01
SIGNAGE 03_BUNKBED 3-AB
AA-S01 SIGNAGE - Numbers
- laser-cut acrylic or MDF -
thickness 5mm - spray painted
- RAL 3020 Red & RAL 4010
Rose - font according to
wayfinding signage design
(RAL colour to be confirmed
by Clink)

SS-L05
LADDER 01_BUNKBED 3-AB
SS-L01/L02/L03/L04/L05/L06/
L07 Ladder - 3.5x3.5 cm
Powder Coated Steel
Structure - Colour to match
Telegrey 4 RAL 7047 - Semi
gloss finish (RAL colour to be
confirmed by Clink)

CC-M05
CLADDING 101_BUNKBED 3-A
CC-M01/M02/M03/M04/M05/M
06 Cladding - Laminated
chipboard to match RAL 7044,
Thickness 18m (RAL colour to
be confirmed by Clink)

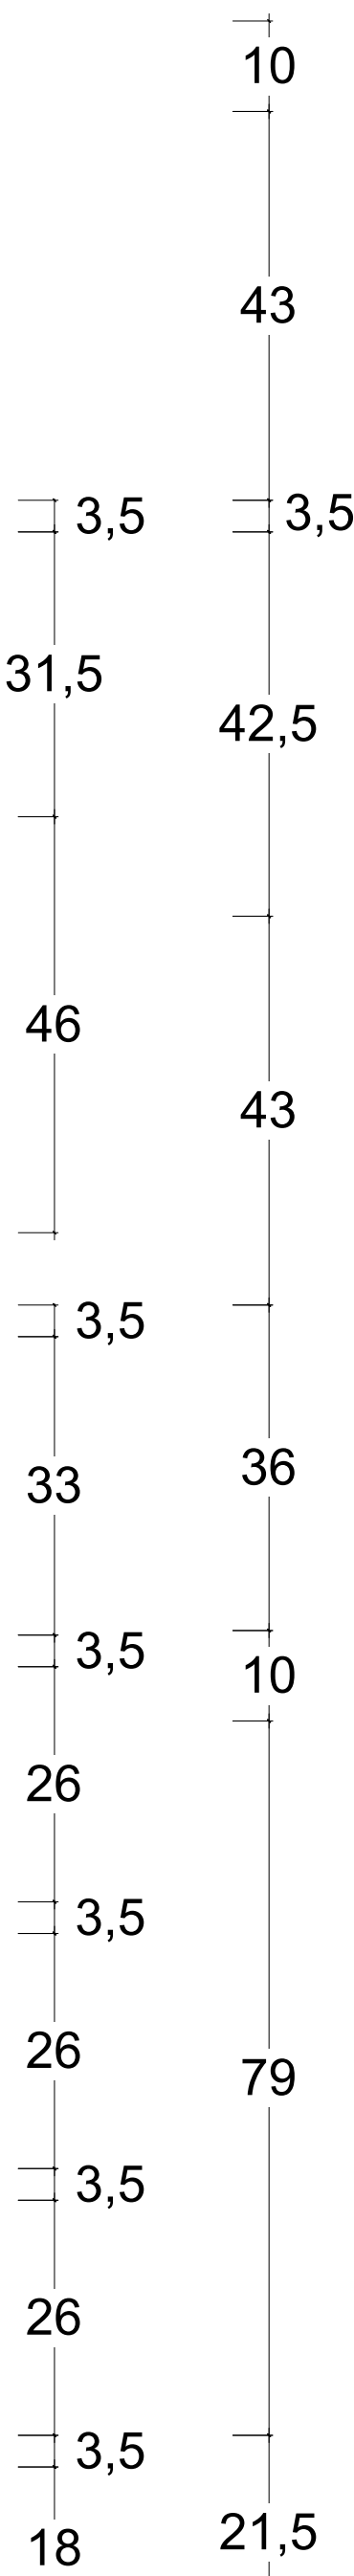

KEY

Index

A) 04.05.2026 Plan Set UP

All measurements have to be verified according to existing conditions by the contractor! Discrepancies must be reported immediately to the responsible project manager. The contractor has to produce fully dimensioned shop drawings prior to the start of the contract and they have to be approved by the client/ investor / interior designer

Project

CLINK 78 - BEDS

Logo



Project Address

CLINK 78
78 King's Cross Rd
London WC1X 9QG
United Kingdom

Client's Address

CLINK 78
78 King's Cross Rd
London WC1X 9QG
United Kingdom



Sheet Number 3-A-602		Total Sheets 82	
Sheet Title BUNKBED 3-A FRONT ELEVATION		Level	
File Name 260425_CLINK 78_BEDs AA DRAFT 03.vwx			
Date 28.04.26	Sheet Size A1	Scale 1:8	Signed AA

Stefanie Jaensch INTERIOR DESIGNS

Global Headquarter | Stefanie Jaensch c/o WeWork
Taunusanlage 8 | 60329 Frankfurt a.M.
E-Mail info@stefaniejaensch.de | DE +49 (0) 174 6756098
www.stefaniejaensch.de

Legal address | Stefanie Jaensch | Offenbacher Landstraße 434 | 60599 Frankfurt a.M.
© 2023 All Rights Reserved | Stefanie Jaensch

BUNKBEDS - TYPE 3-A (TRIPLE) - BACK ELEVATION

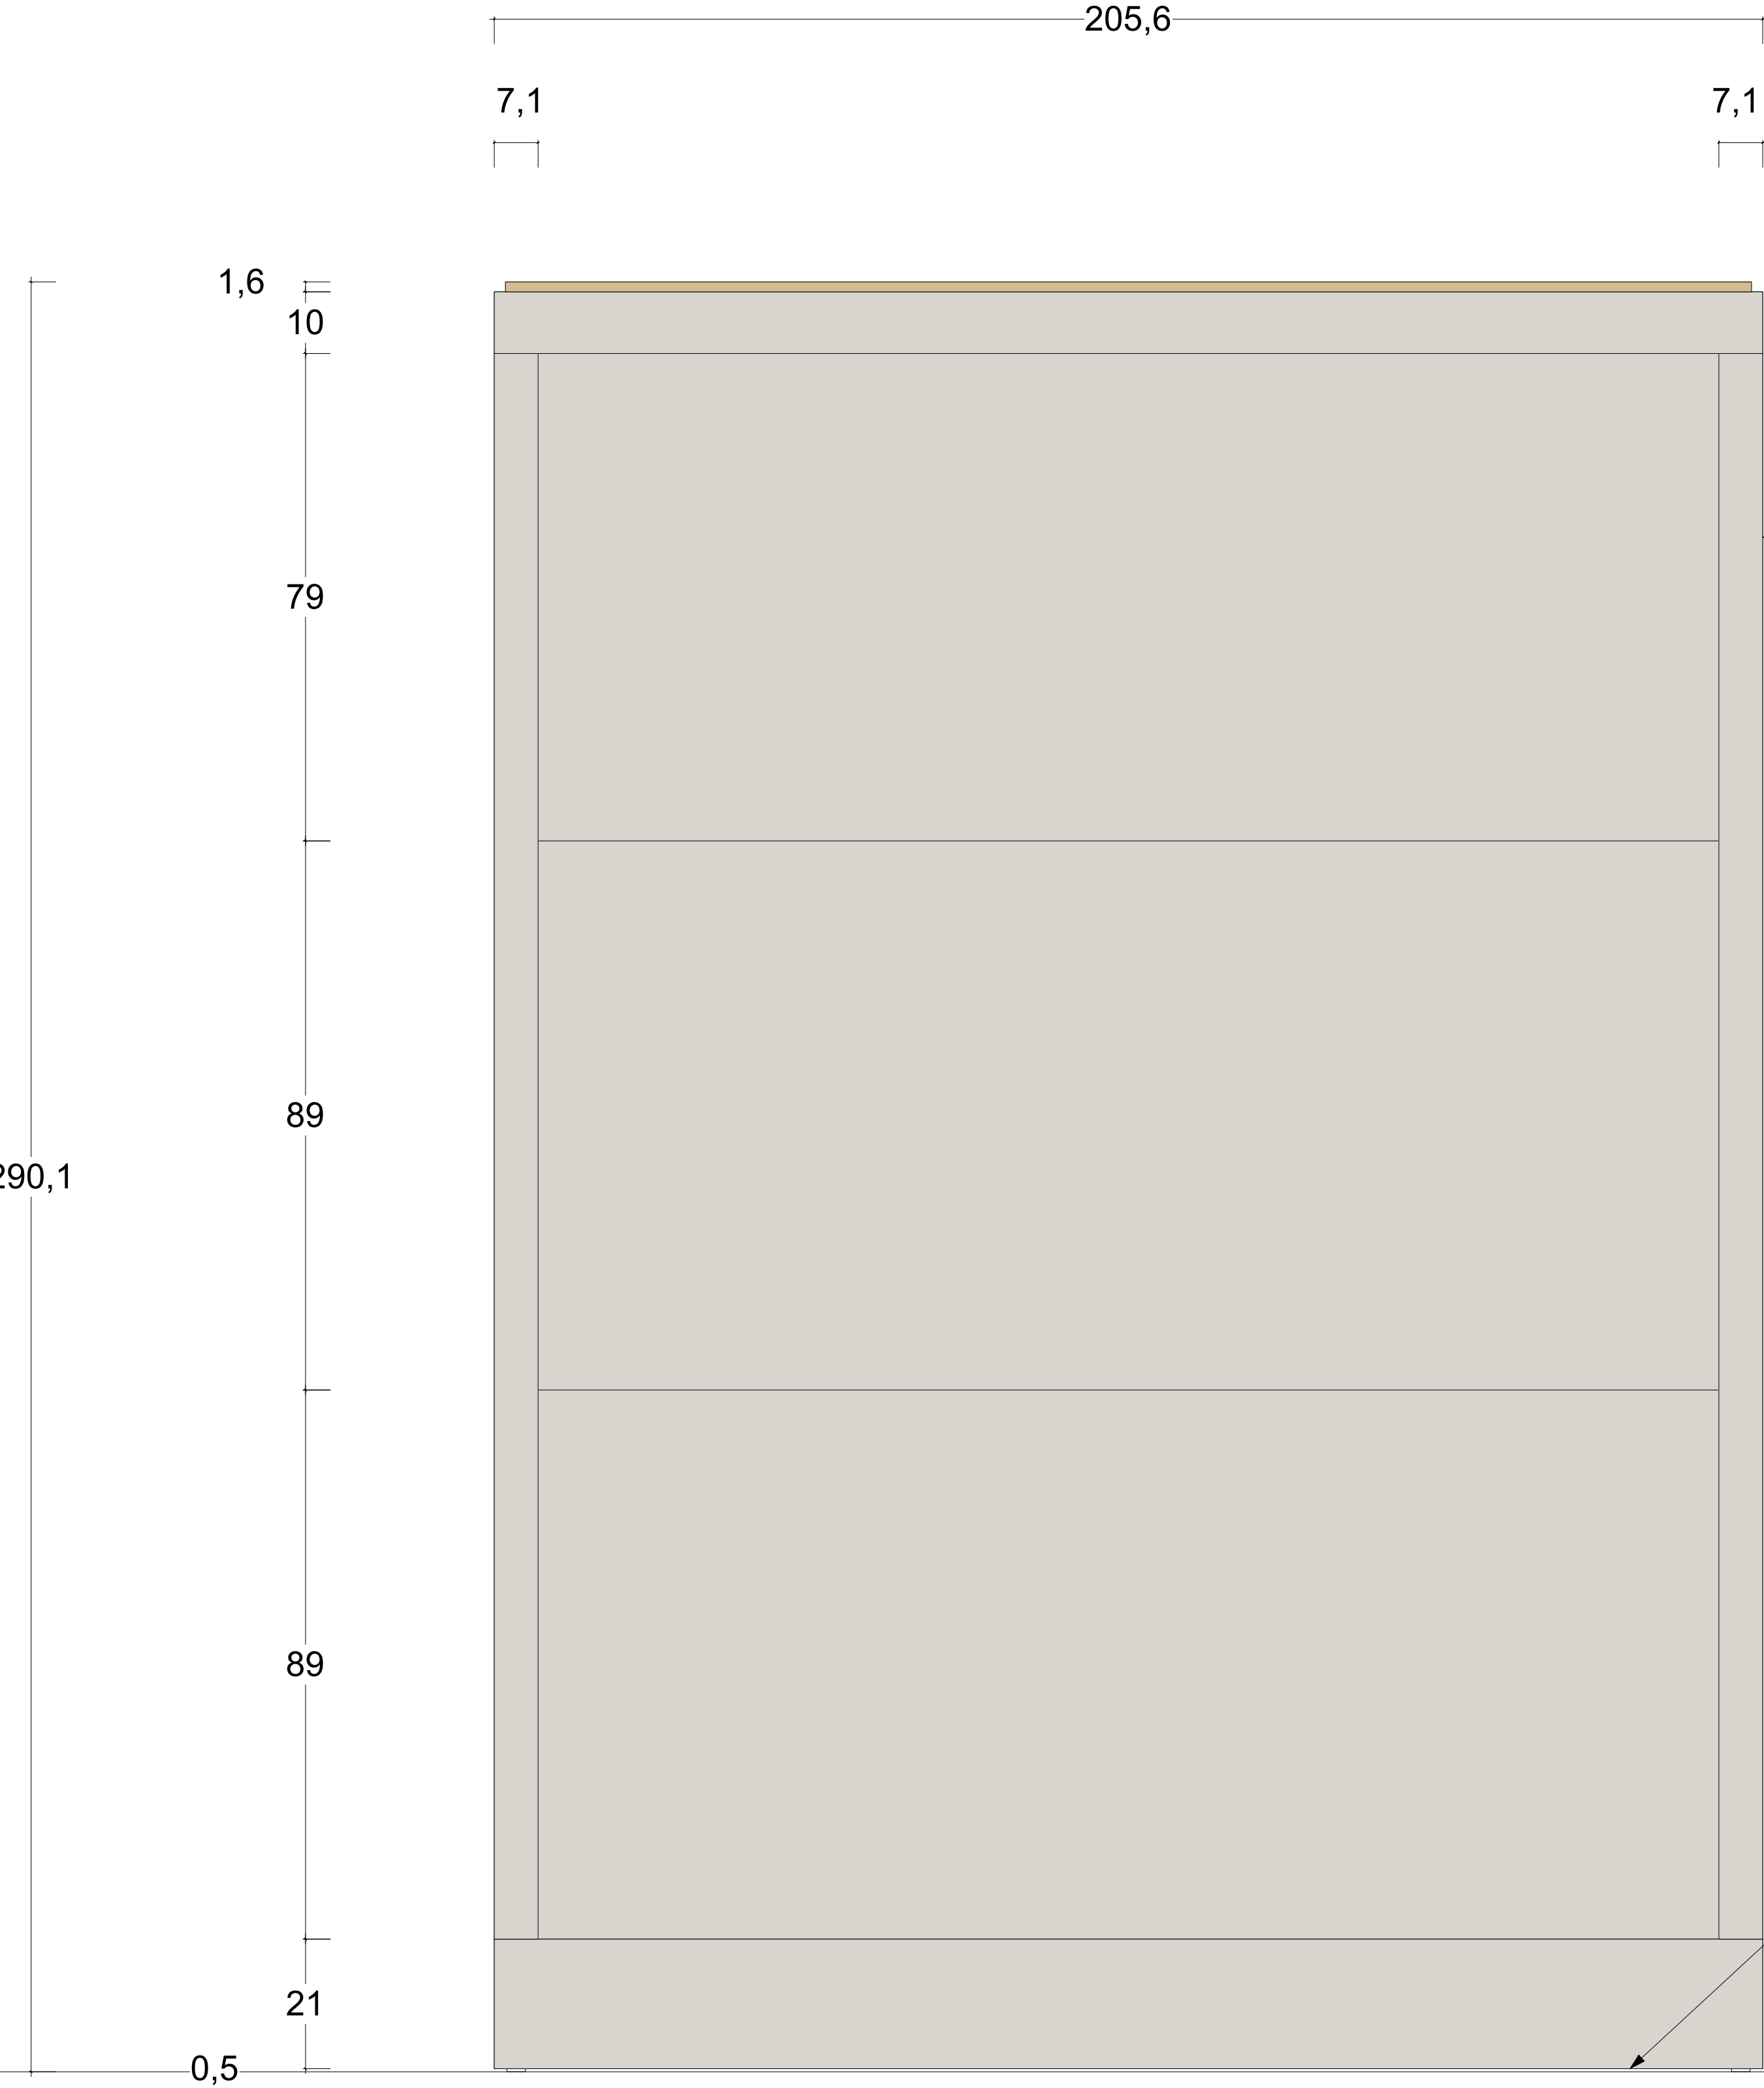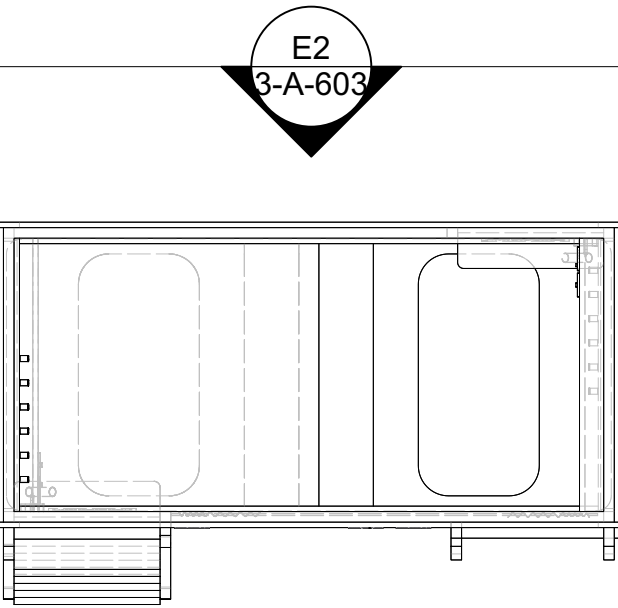

CC-M05
CLADDING 119_BUNKBED 3-A
CC-M01/M02/M03/M04/M05/M
06 Cladding - Laminated
chipboard to match RAL 7044,
Thickness 18m (RAL colour to
be confirmed by Clink)

SS-T01
FOOT_BUNKBED 3-AB
SS-T01 Height Adjustable Feet



KEY

Index

A) 04.05.2026 Plan Set UP

All measurements have to be verified according to existing conditions by the contractor! Discrepancies must be reported immediately to the responsible project manager. The contractor has to produce fully dimensioned shop drawings prior to the start of the contract and they have to be approved by the client/ investor / interior designer

Project

CLINK 78 - BEDS

Logo



Project Address

CLINK 78
78 King's Cross Rd
London WC1X 9QG
United Kingdom

Client's Address

CLINK 78
78 King's Cross Rd
London WC1X 9QG
United Kingdom

Sheet Number 3-A-603		Total Sheets 82
Sheet Title BUNKBED 3-A BACK ELEVATION		Level
File Name 260425_CLINK 78_BEDs AA DRAFT 03.vwx		

Date	Sheet Size	Scale	Signed
28.04.26	A1	1:8	AA

Stefanie Jaensch INTERIOR DESIGNS

Global Headquarter | Stefanie Jaensch c/o WeWork

Taunusanlage 8 | 60329 Frankfurt a.M.

E-Mail info@stefaniejaensch.de | DE +49 (0) 174 6756098

www.stefaniejaensch.de



Legal address | Stefanie Jaensch | Offenbacher Landstraße 434 | 60599 Frankfurt a.M.

© 2023 All Rights Reserved | Stefanie Jaensch

E2

BUNKBED 2-A BACK ELEVATION
Scale: 1:8

BUNKBEDS - TYPE 3-A (TRIPLE) - RIGHT ELEVATION

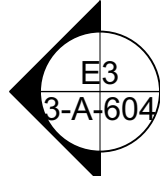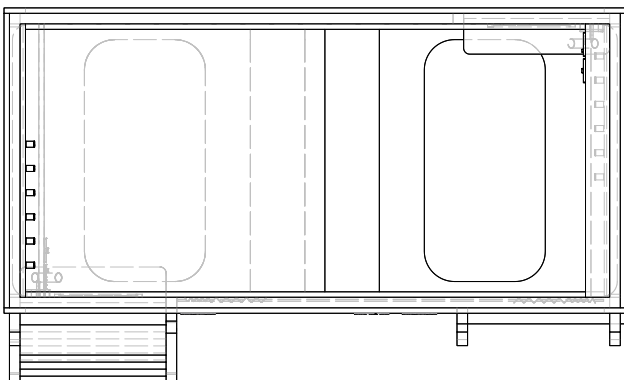

KEY

Index

A) 04.05.2026 Plan Set UP

All measurements have to be verified according to existing conditions by the contractor! Discrepancies must be reported immediately to the responsible project manager. The contractor has to produce fully dimensioned shop drawings prior to the start of the contract and they have to be approved by the client/ investor / interior designer

Project

CLINK 78 - BEDS

Logo

CLINK
HOSTELS

Project Address

CLINK 78
78 King's Cross Rd
London WC1X 9QG
United Kingdom

Client's Address

CLINK 78
78 King's Cross Rd
London WC1X 9QG
United Kingdom

Sheet Number 3-A-604		Total Sheets 82
Sheet Title BUNKBED 3-A RIGHT ELEVATION		Level
File Name 260425_CLINK 78_BEDs AA DRAFT 03.vwx		

Date	Sheet Size	Scale	Signed
28.04.26	A1	1:8	AA

Stefanie Jaensch INTERIOR DESIGNS

Global Headquarter | Stefanie Jaensch c/o WeWork
Taunusanlage 8 | 60329 Frankfurt a.M.
E-Mail info@stefaniejaensch.de | DE +49 (0) 174 6756098
www.stefaniejaensch.de

Legal address | Stefanie Jaensch | Offenbacher Landstraße 434 | 60599 Frankfurt a.M.
© 2023 All Rights Reserved | Stefanie Jaensch

10,7 101 1,8 97,4 1,8

1,6 53 6,5 46 290,1 217,5 18

CC-M05
CLADDING 124_BUNKBED 3-A
CC-M01/M02/M03/M04/M05/M
06 Cladding - Laminated
chipboard to match RAL 7044,
Thickness 18m (RAL colour to
be confirmed by Clink)

CC-M07
CC-M07 Visible Edge Band -
Plywood edges

AA-P01
LADDER 06_BUNKBED 3-A
AA-P01 Rubber Pad to be
placed on steps and the top of
the lockers



85°

23,64

E3

BUNKBED 3-A RIGHT ELEVATION
Scale: 1:8

BUNKBEDS - TYPE 3-A (TRIPLE) - LEFT ELEVATION

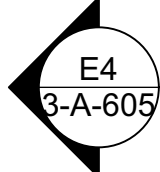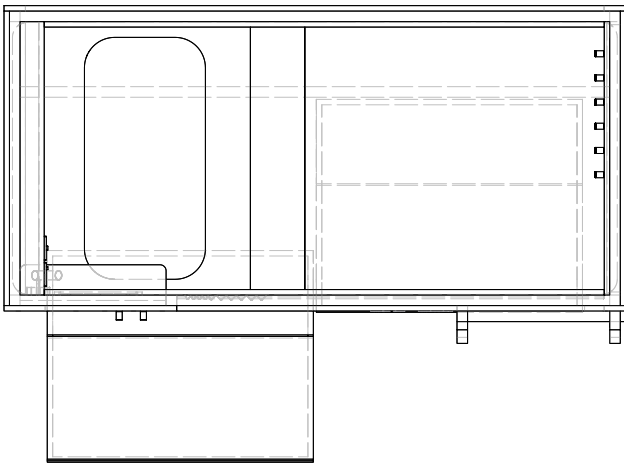

KEY

Index

A) 04.05.2026 Plan Set UP

All measurements have to be verified according to existing conditions by the contractor! Discrepancies must be reported immediately to the responsible project manager. The contractor has to produce fully dimensioned shop drawings prior to the start of the contract and they have to be approved by the client/ investor / interior designer

Project

CLINK 78 - BEDS

Logo



Project Address

CLINK 78
78 King's Cross Rd
London WC1X 9QG
United Kingdom

Client's Address

CLINK 78
78 King's Cross Rd
London WC1X 9QG
United Kingdom

Sheet Number	3-A-605	Total Sheets	82
Sheet Title	BUNKBED 3-A LEFT ELEVATION	Level	
File Name			
260425_CLINK 78_BEDs AA DRAFT 03.vwx			

Date	Sheet Size	Scale	Signed
28.04.26	A1	1:8	AA

Stefanie Jaensch INTERIOR DESIGNS

Global Headquarter | Stefanie Jaensch c/o WeWork
Taunusanlage 8 | 60329 Frankfurt a.M.
E-Mail info@stefaniejaensch.de | DE +49 (0) 174 6756098
www.stefaniejaensch.de

Legal address | Stefanie Jaensch | Offenbacher Landstraße 434 | 60599 Frankfurt a.M.
© 2023 All Rights Reserved | Stefanie Jaensch

101 10,7

290,1




181,5

18

E4

BUNKBED 3-A LEFT ELEVATION
Scale: 1:8

BUNKBEDS - TYPE 3-A (TRIPLE) - SECTION 1

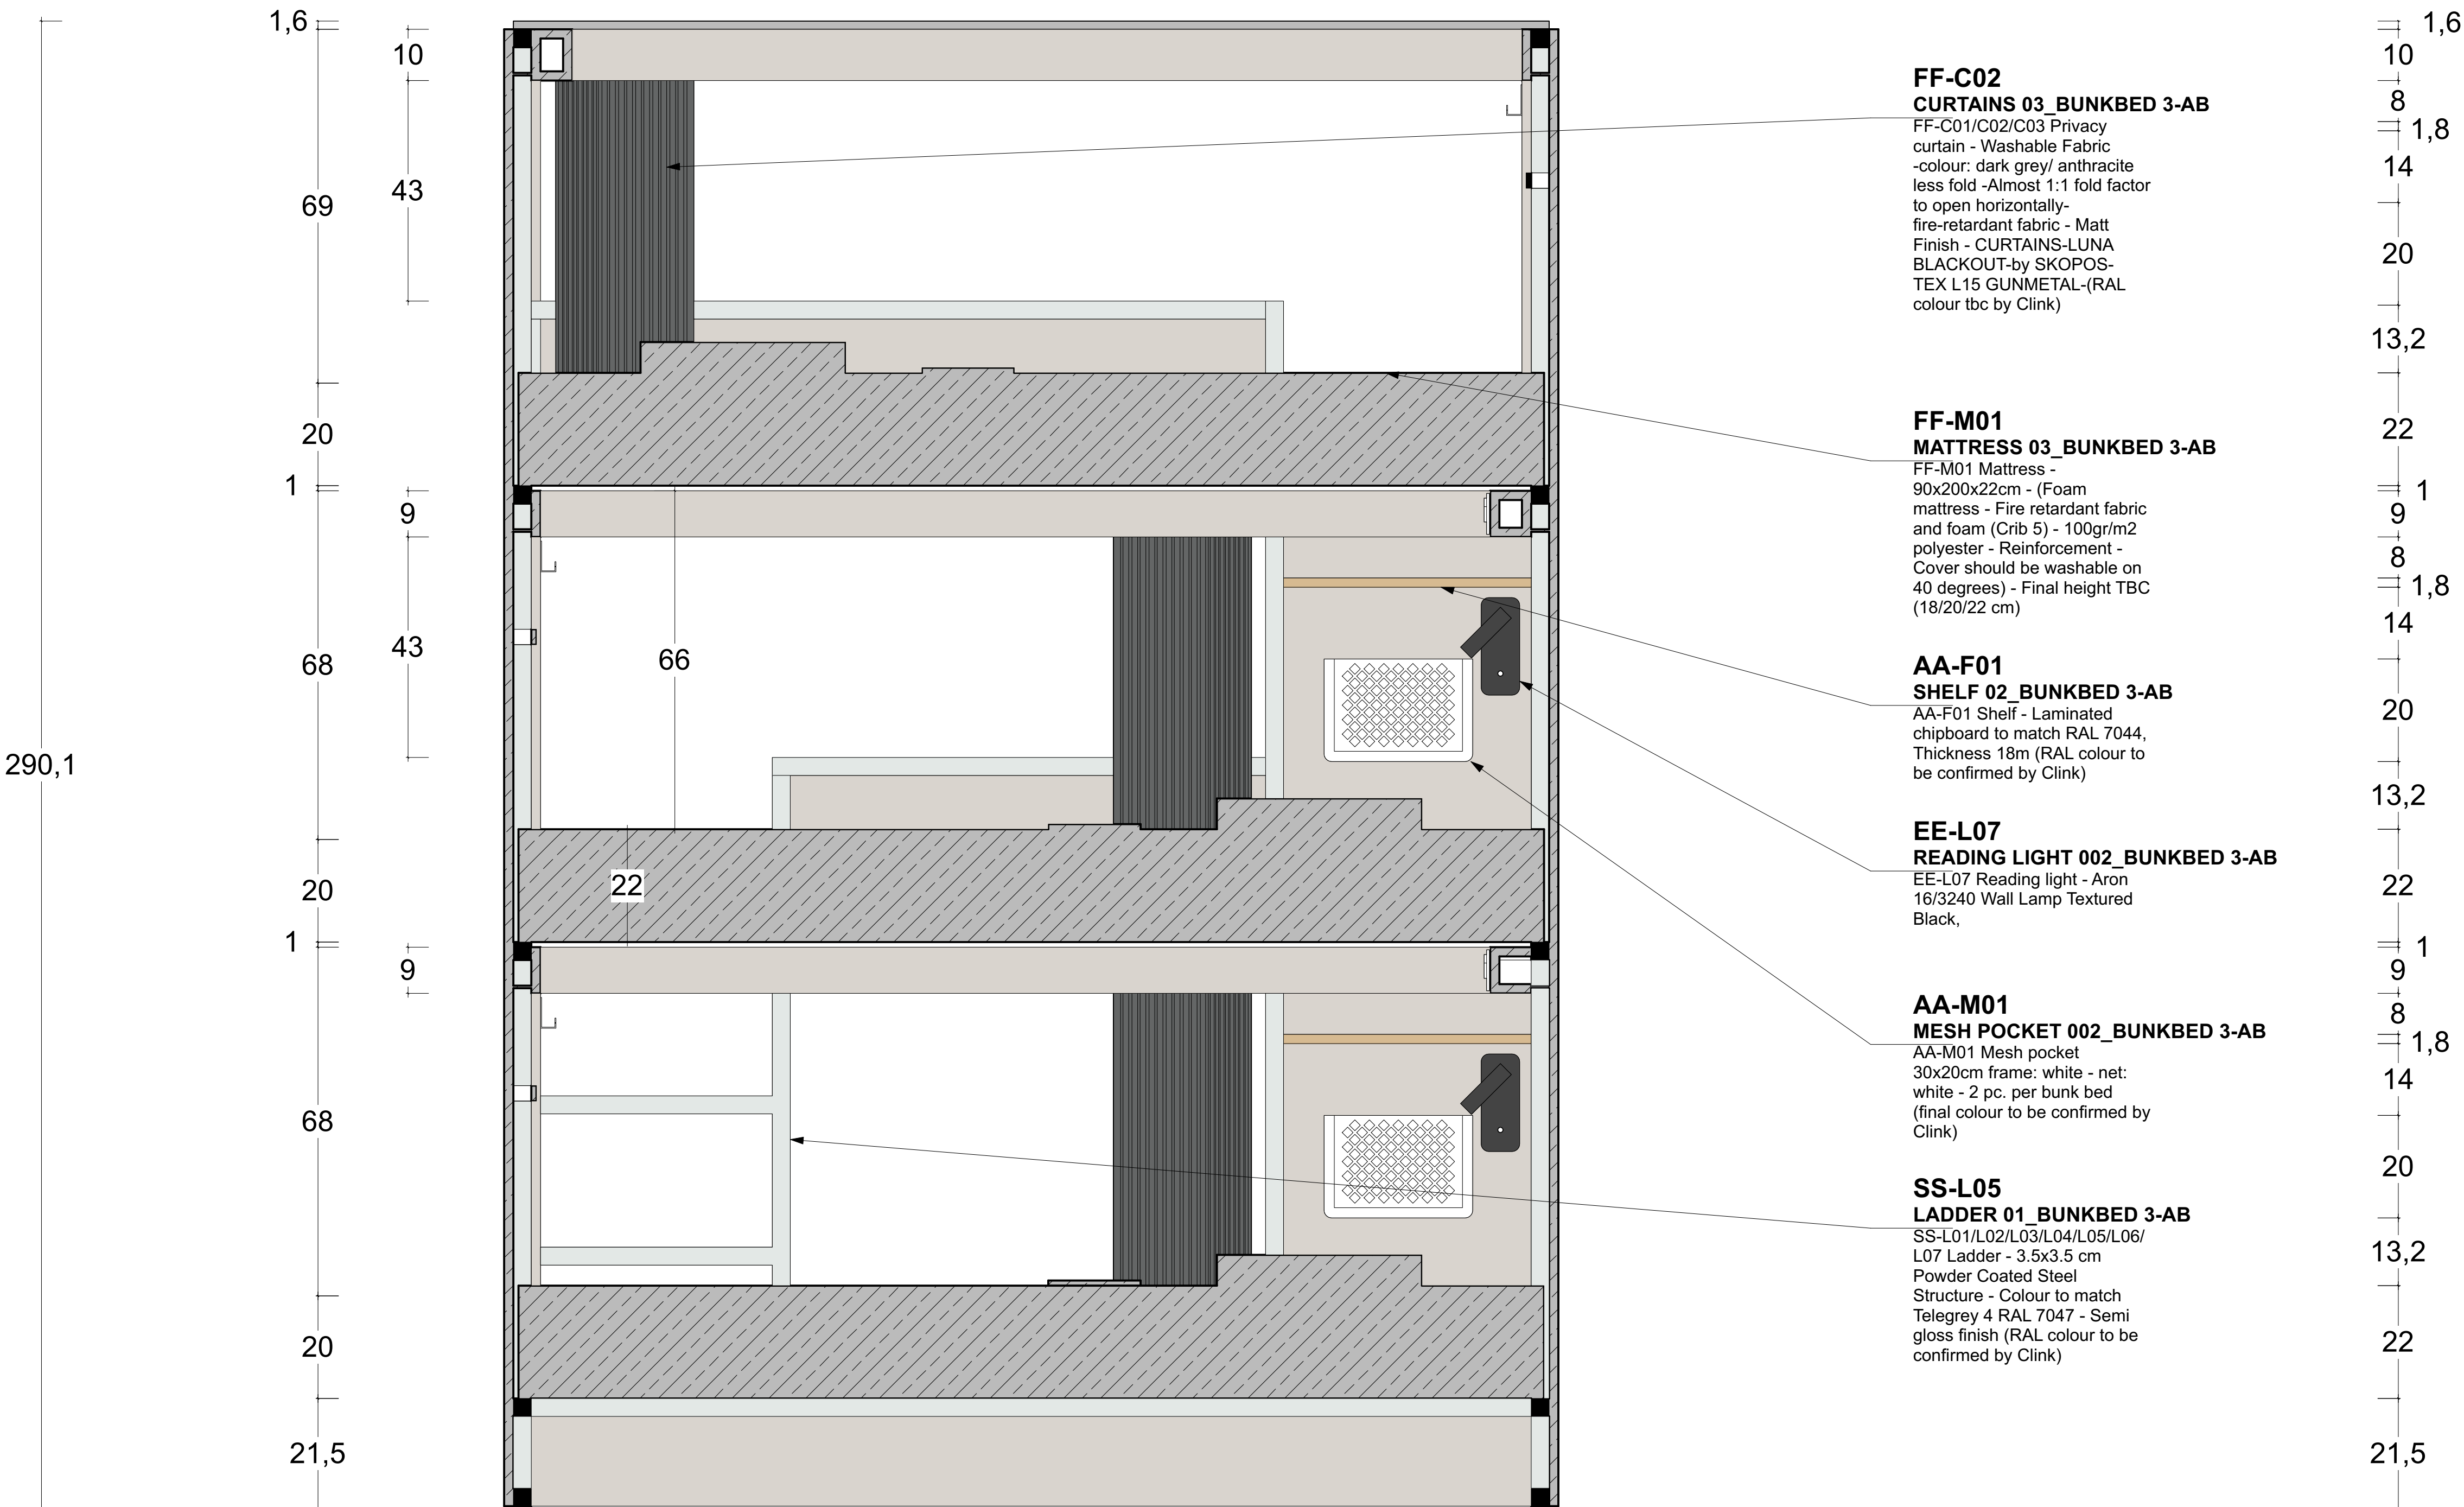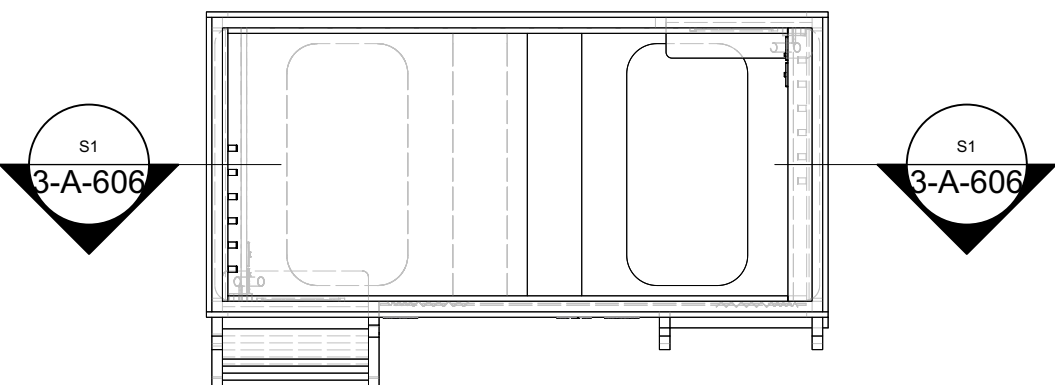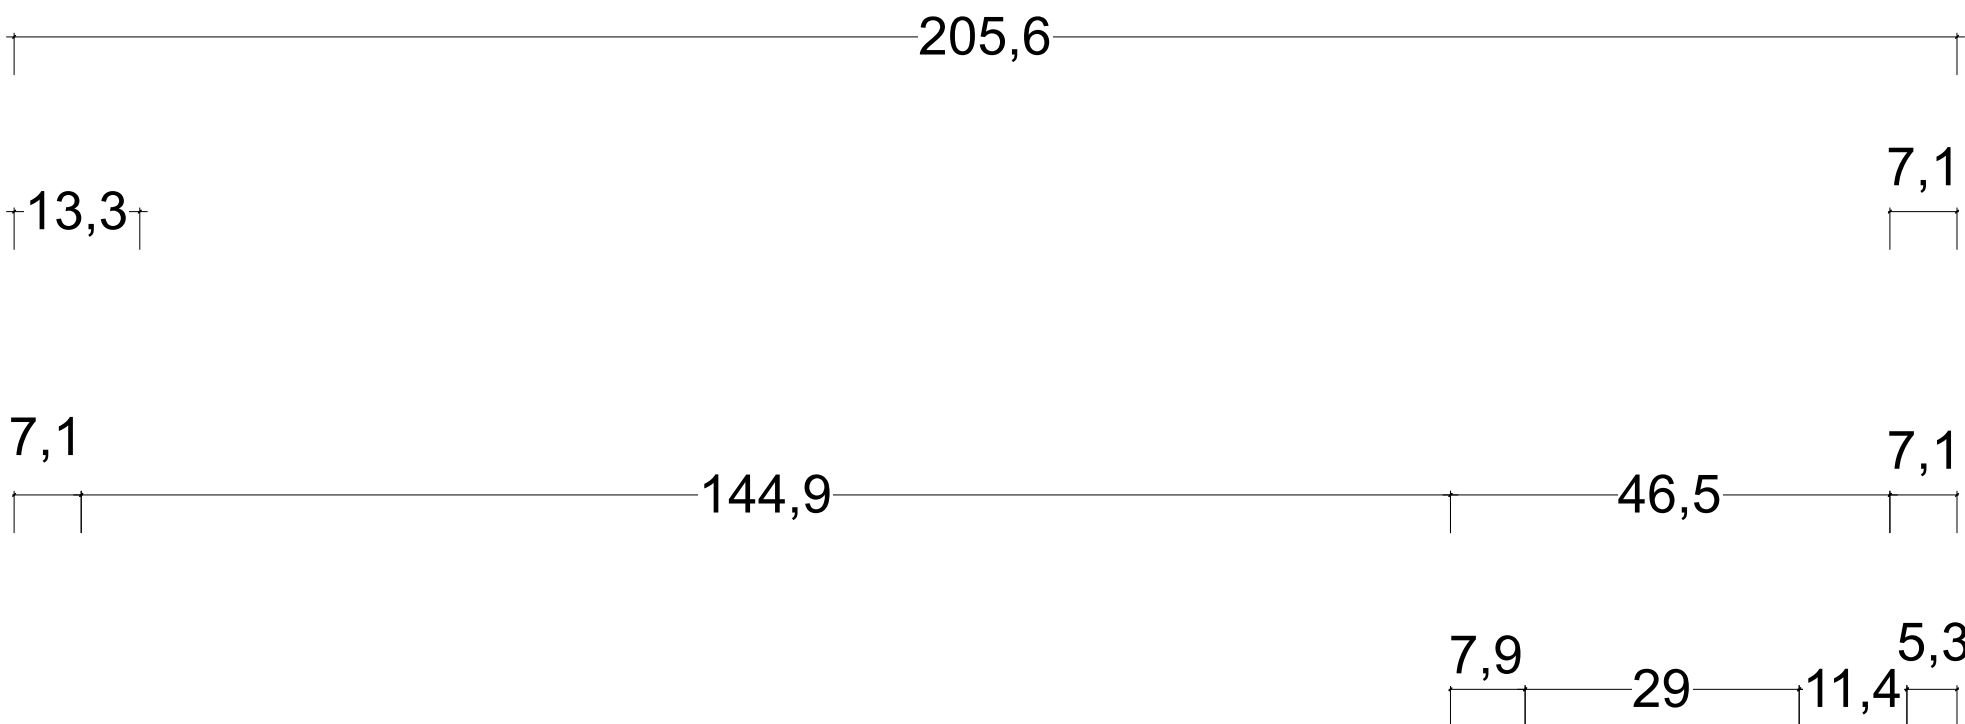

KEY

Index

A) 04.05.2026 Plan Set UP

All measurements have to be verified according to existing conditions by the contractor! Discrepancies must be reported immediately to the responsible project manager. The contractor has to produce fully dimensioned shop drawings prior to the start of the contract and they have to be approved by the client/ investor / interior designer

Project
CLINK 78 - BEDS




Project Address
CLINK 78
78 King's Cross Rd
London WC1X 9QG
United Kingdom



Client's Address
CLINK 78
78 King's Cross Rd
London WC1X 9QG
United Kingdom

Sheet Number	3-A-606	Total Sheets	82
Sheet Title	BUNKBED 3-A SECTION 1	Level	
File Name			
260425_CLINK 78_BEDs AA DRAFT 03.vwx			
Date	Sheet Size	Scale	Signed
28.04.26	A1	1:8	AA

Stefanie Jaensch INTERIOR DESIGNS
Global Headquarter | Stefanie Jaensch c/o WeWork
Taubusanlage 8 | 60329 Frankfurt a.M.
E-Mail info@stefaniejaensch.de | DE +49 (0) 174 6756098
www.stefaniejaensch.de
Legal address | Stefanie Jaensch | Offenbacher Landstraße 434 | 60599 Frankfurt a.M.
© 2023 All Rights Reserved | Stefanie Jaensch

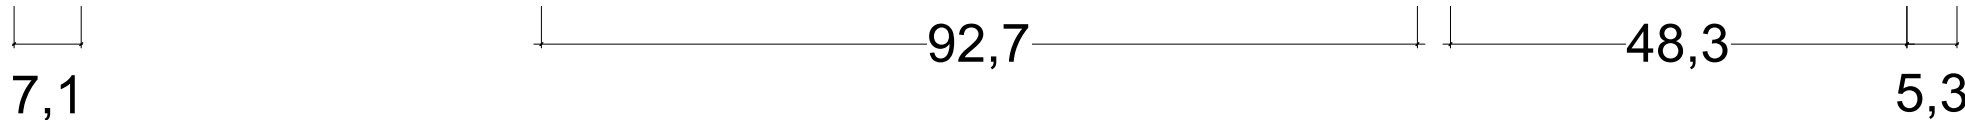

BUNKBEDS - TYPE 3-A (TRIPLE) - SECTION 2

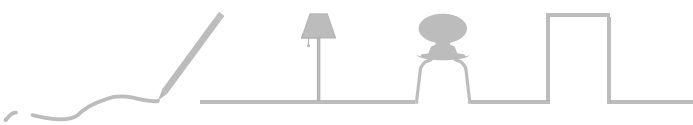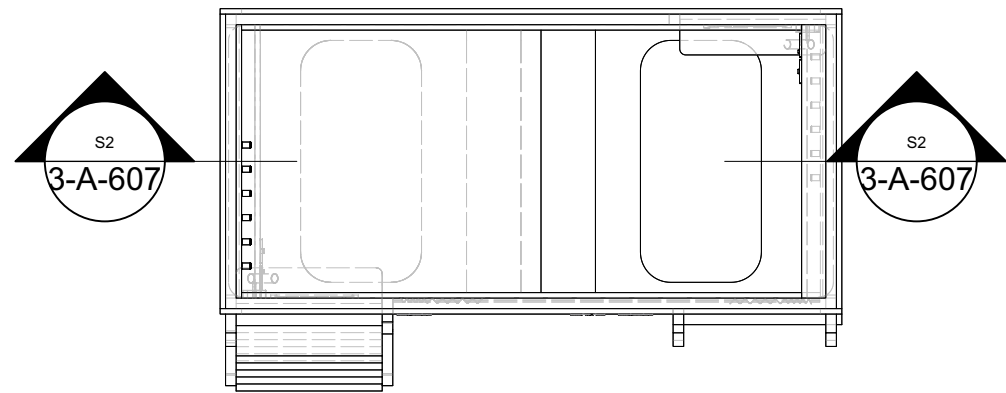

KEY

Index

A) 04.05.2026 Plan Set UP

All measurements have to be verified according to existing conditions by the contractor! Discrepancies must be reported immediately to the responsible project manager. The contractor has to produce fully dimensioned shop drawings prior to the start of the contract and they have to be approved by the client/ investor / interior designer

Project

CLINK 78 - BEDS

Logo

CLINK
HOSTELS

Project Address

CLINK 78
78 King's Cross Rd
London WC1X 9QG
United Kingdom

Client's Address

CLINK 78
78 King's Cross Rd
London WC1X 9QG
United Kingdom

Sheet Number 3-A-607

Total Sheets 82

Sheet Title
BUNKBED 3-A SECTION 2

Level

File Name

260425_CLINK 78_BEDs AA DRAFT 03.vwx

Date

28.04.26

Sheet Size

A1

Scale

1:8

Signed

AA

Stefanie Jaensch INTERIOR DESIGNS

Global Headquarter | Stefanie Jaensch c/o WeWork
Taubusanlage 8 | 60329 Frankfurt a.M.

E-Mail info@stefaniejaensch.de | DE +49 (0) 174 6756098

www.stefaniejaensch.de



Legal address | Stefanie Jaensch | Offenbacher Landstraße 434 | 60599 Frankfurt a.M.

© 2023 All Rights Reserved | Stefanie Jaensch

S2

BUNKBED 3-A SECTION 2
Scale: 1:8

BUNKBEDS - TYPE 3-A (TRIPLE) - SECTION 3

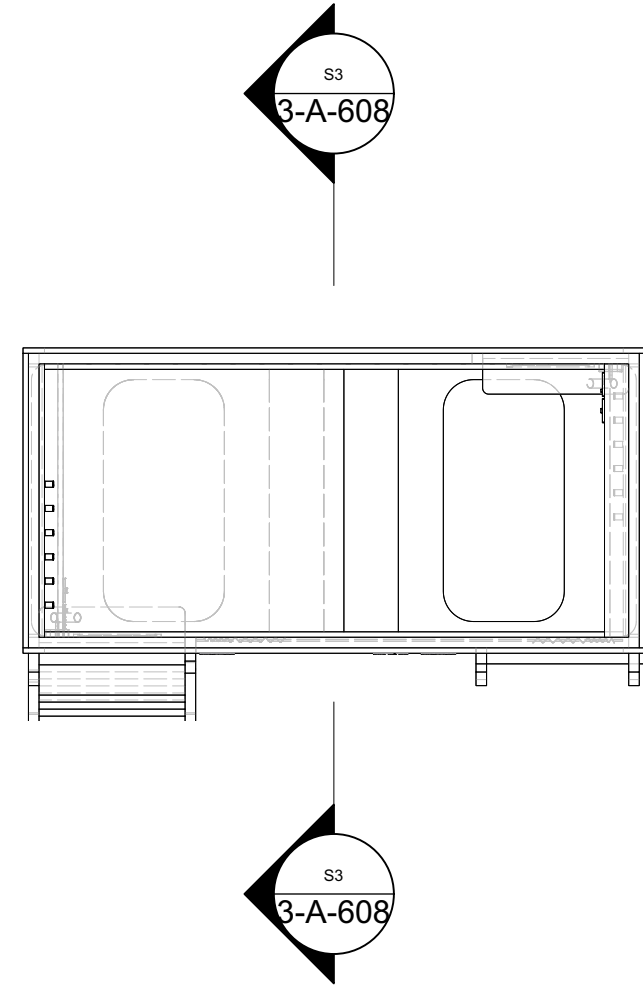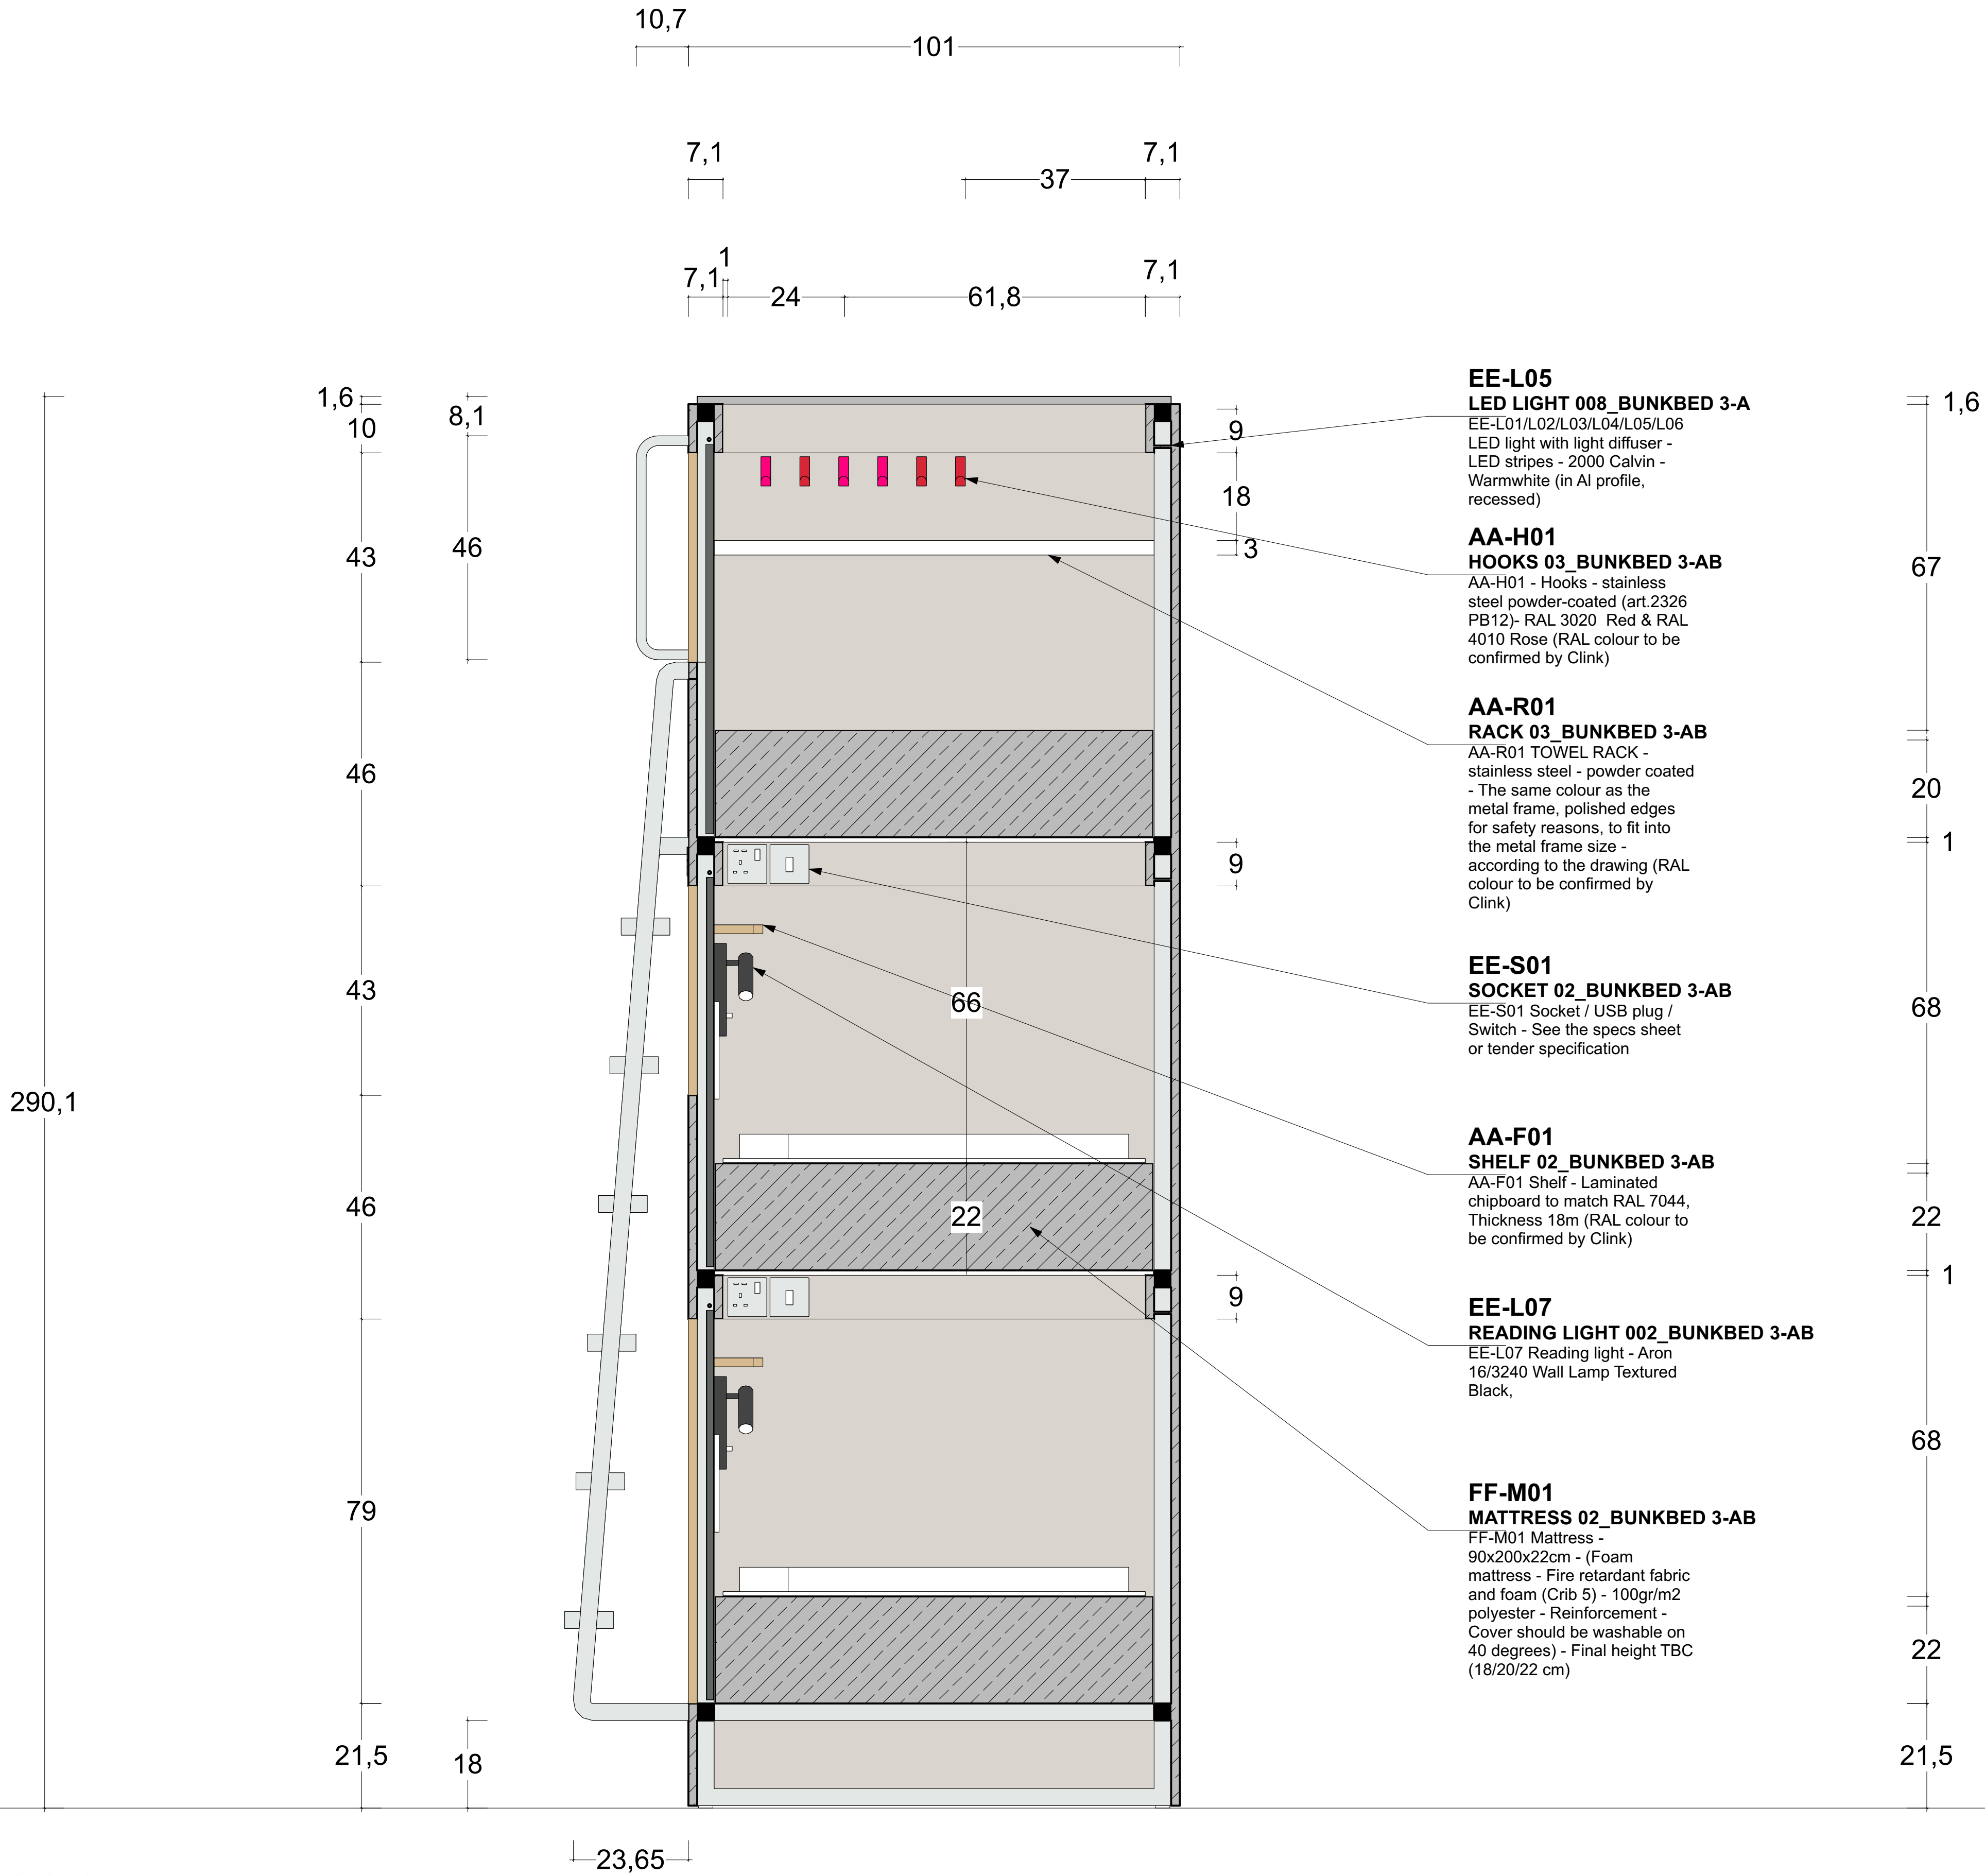

KEY

Index

A) 04.05.2026 Plan Set UP

All measurements have to be verified according to existing conditions by the contractor! Discrepancies must be reported immediately to the responsible project manager. The contractor has to produce fully dimensioned shop drawings prior to the start of the contract and they have to be approved by the client/ investor / interior designer

Project

CLINK 78 - BEDS

Logo



Project Address

CLINK 78
78 King's Cross Rd
London WC1X 9QG
United Kingdom

Client's Address

CLINK 78
78 King's Cross Rd
London WC1X 9QG
United Kingdom

Sheet Number 3-A-608

Total Sheets	82
--------------	----

Sheet Title
BUNKBED 3-A SECTION 3

Level

File Name

260425_CLINK 78_BEDs AA DRAFT 03.vwx

Date _____

28.04.20

Sheet Size	
------------	--

A1

Scale

1:8	AA
-----	----

Stefanie Jaensch INTERIOR DESIGNS

Global Headquarter | Stefanie Jaensch c/o WeWork


Taunusanlage 8 | 60329 Frankfurt a.M.

www.stefaniejaensch.de

Equal address | Stefanie Jaensch | Offenbacher Landstraße 434 | 60599 Frankfurt a.M.

© 2023 All Rights Reserved | Stefanie Jaensch

BUNKBEDS - TYPE 3-A (TRIPLE) - SECTION 4

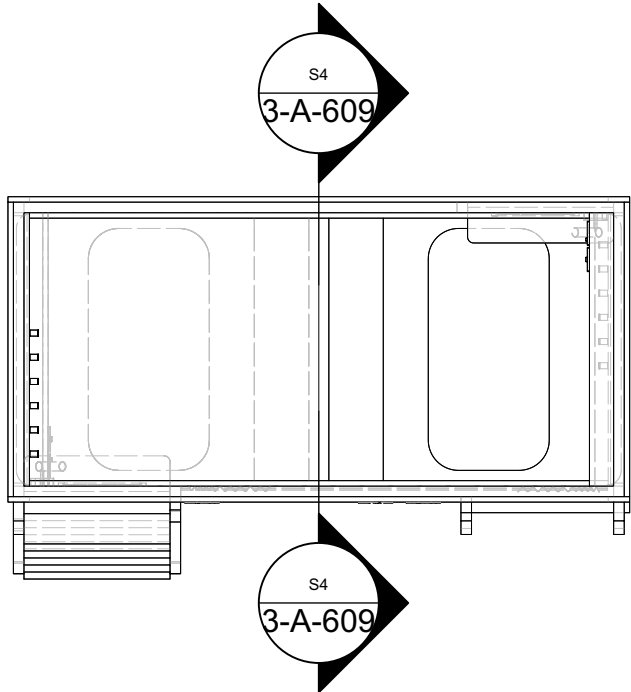

KEY

Index

A) 04.05.2026 Plan Set UP

All measurements have to be verified according to existing conditions by the contractor! Discrepancies must be reported immediately to the responsible project manager. The contractor has to produce fully dimensioned shop drawings prior to the start of the contract and they have to be approved by the client/ investor / interior designer

Project

CLINK 78 - BEDS

Logo



Project Address

CLINK 78
78 King's Cross Rd
London WC1X 9QG
United Kingdom

Client's Address

CLINK 78
78 King's Cross Rd
London WC1X 9QG
United Kingdom


Sheet Number	3-A-609	Total Sheets	82
Sheet Title	BUNKBED 3-A SECTION 4	Level	
File Name			
260425_CLINK 78_BEDs AA DRAFT 03.vwx			

Date	Sheet Size	Scale	Signed
28.04.26	A1	1:8	AA


Stefanie Jaensch INTERIOR DESIGNS

Global Headquarter | Stefanie Jaensch c/o WeWork
Taubusanlage 8 | 60329 Frankfurt a.M.
E-Mail info@stefaniejaensch.de | DE +49 (0) 174 6756098
www.stefaniejaensch.de

Legal address | Stefanie Jaensch | Offenbacher Landstraße 434 | 60599 Frankfurt a.M.
© 2023 All Rights Reserved | Stefanie Jaensch

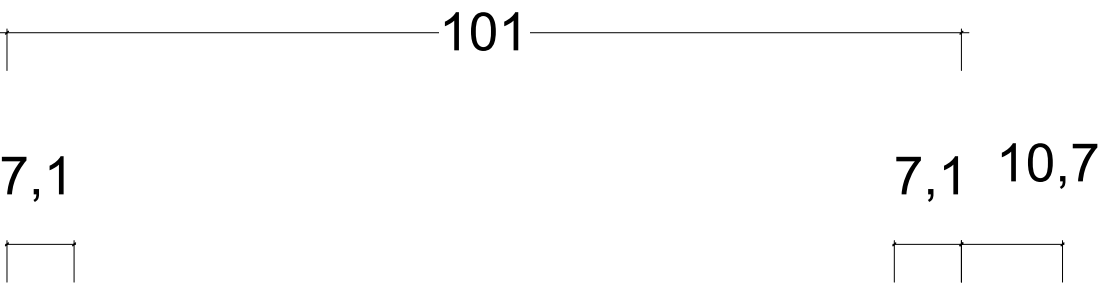

10

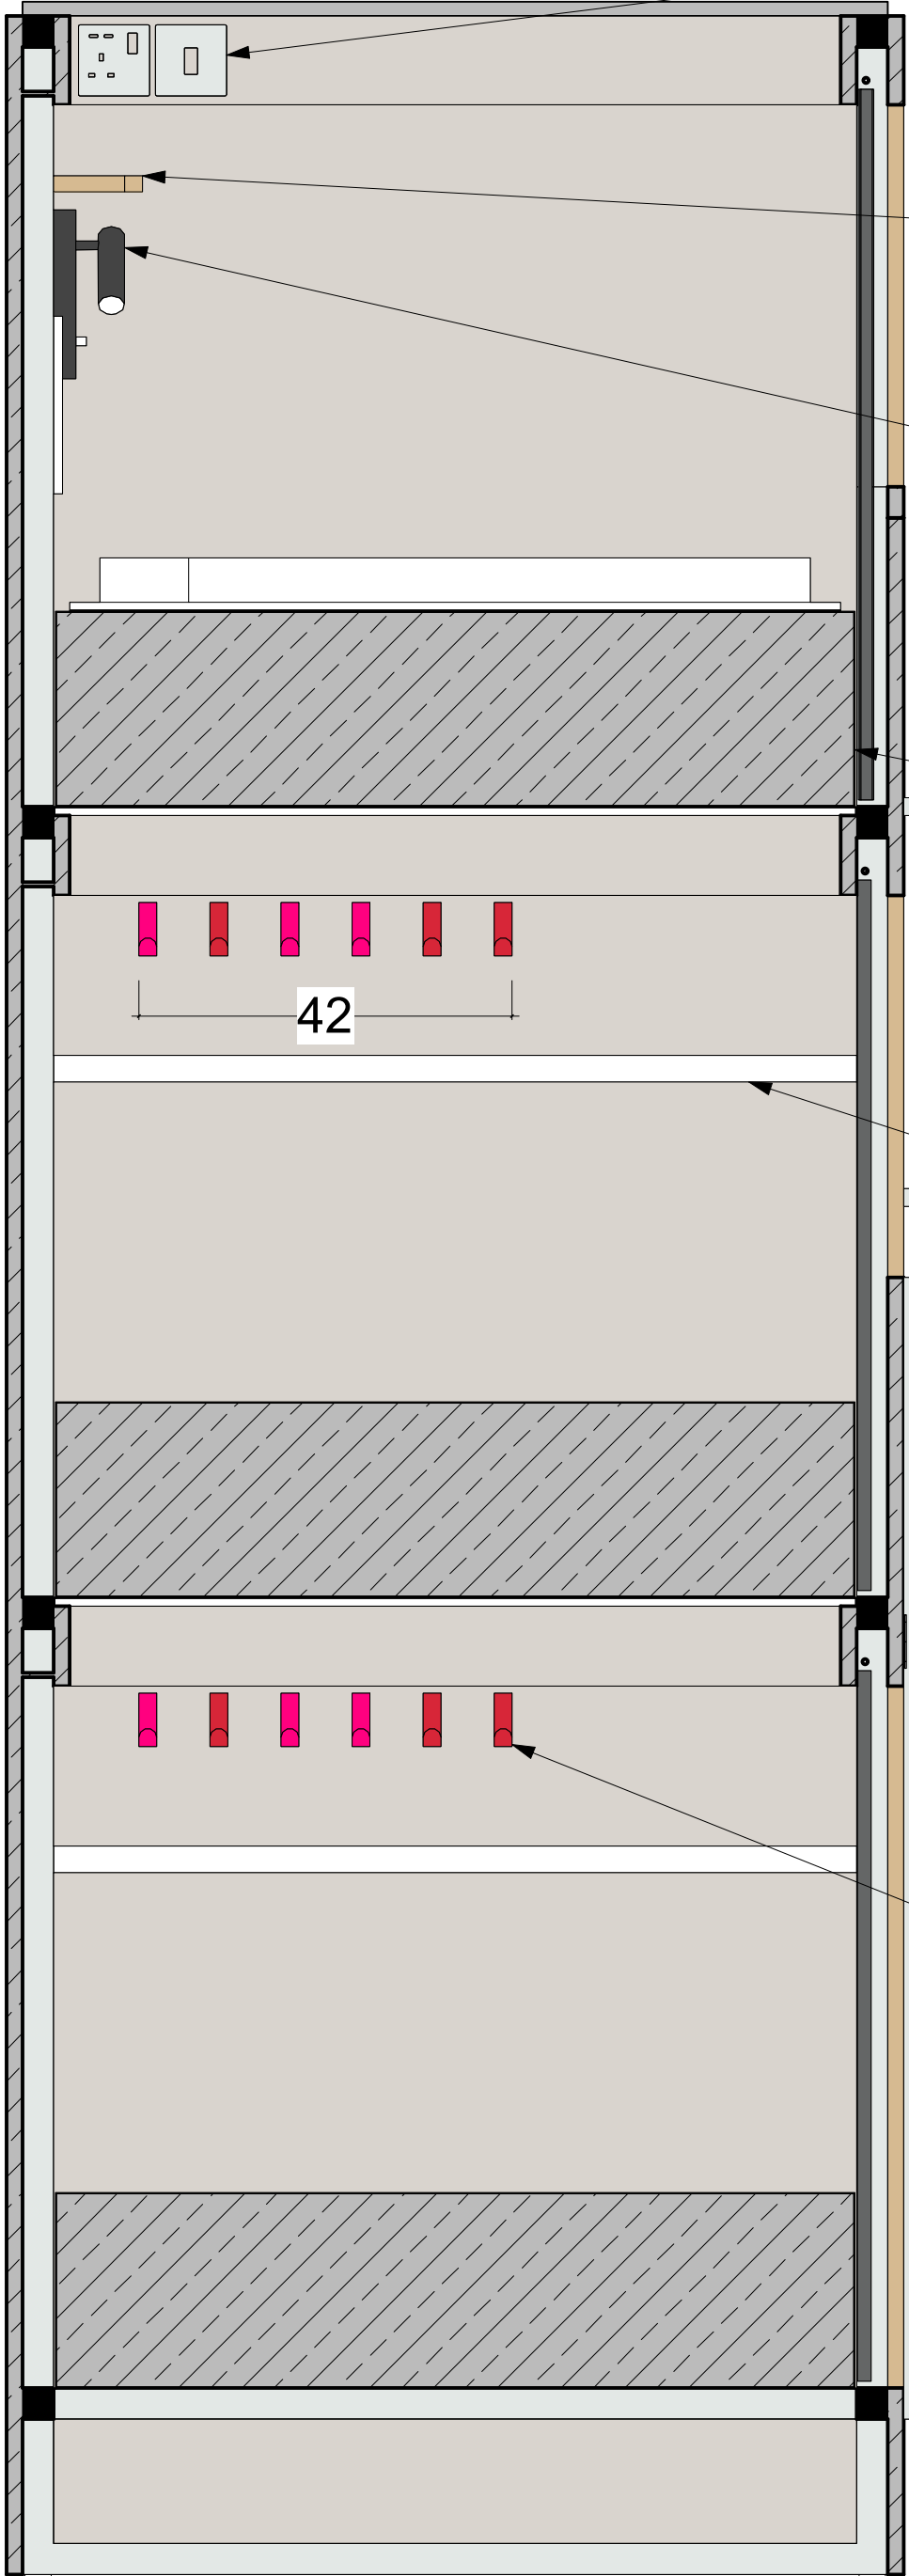

EE-S01
SOCKET 03_BUNKBED 3-AB
EE-S01 Socket / USB plug / Switch - See the specs sheet or tender specification

AA-F01
SHELF 03_BUNKBED 3-AB
AA-F01 Shelf - Laminated chipboard to match RAL 7044, Thickness 18m (RAL colour to be confirmed by Clink)

EE-L07
READING LIGHT 003_BUNKBED 3-AB
EE-L07 Reading light - Aron 16/3240 Wall Lamp Textured Black,


FF-M01
MATTRESS 03_BUNKBED 3-AB
FF-M01 Mattress - 90x200x22cm - (Foam mattress - Fire retardant fabric and foam (Crib 5) - 100gr/m2 polyester - Reinforcement - Cover should be washable on 40 degrees) - Final height TBC (18/20/22 cm)

AA-R01
RACK 02_BUNKBED 3-AB
AA-R01 TOWEL RACK - stainless steel - powder coated - The same colour as the metal frame, polished edges for safety reasons, to fit into the metal frame size - according to the drawing (RAL colour to be confirmed by Clink)

SS-H00
HANDRAIL 02_BUNKBED 2-A-3
SS-H00 Handrail - 3.5x3.5 cm Powder Coated Steel Structure - Colour to match Telegrey 4 RAL 7047 - Semi gloss finish (RAL colour to be confirmed by Clink)

AA-H01
HOOKS 01_BUNKBED 3-AB
AA-H01 - Hooks - stainless steel powder-coated (art.2326 PB12)- RAL 3020 Red & RAL 4010 Rose (RAL colour to be confirmed by Clink)

BUNKBEDS - TYPE 3-B (TRIPLE)

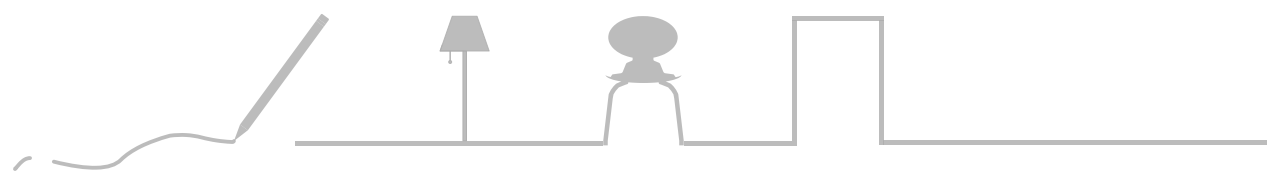


Stefanie Jaensch

INTERIOR DESIGNS


For

CLINK
HOSTELS

3-B

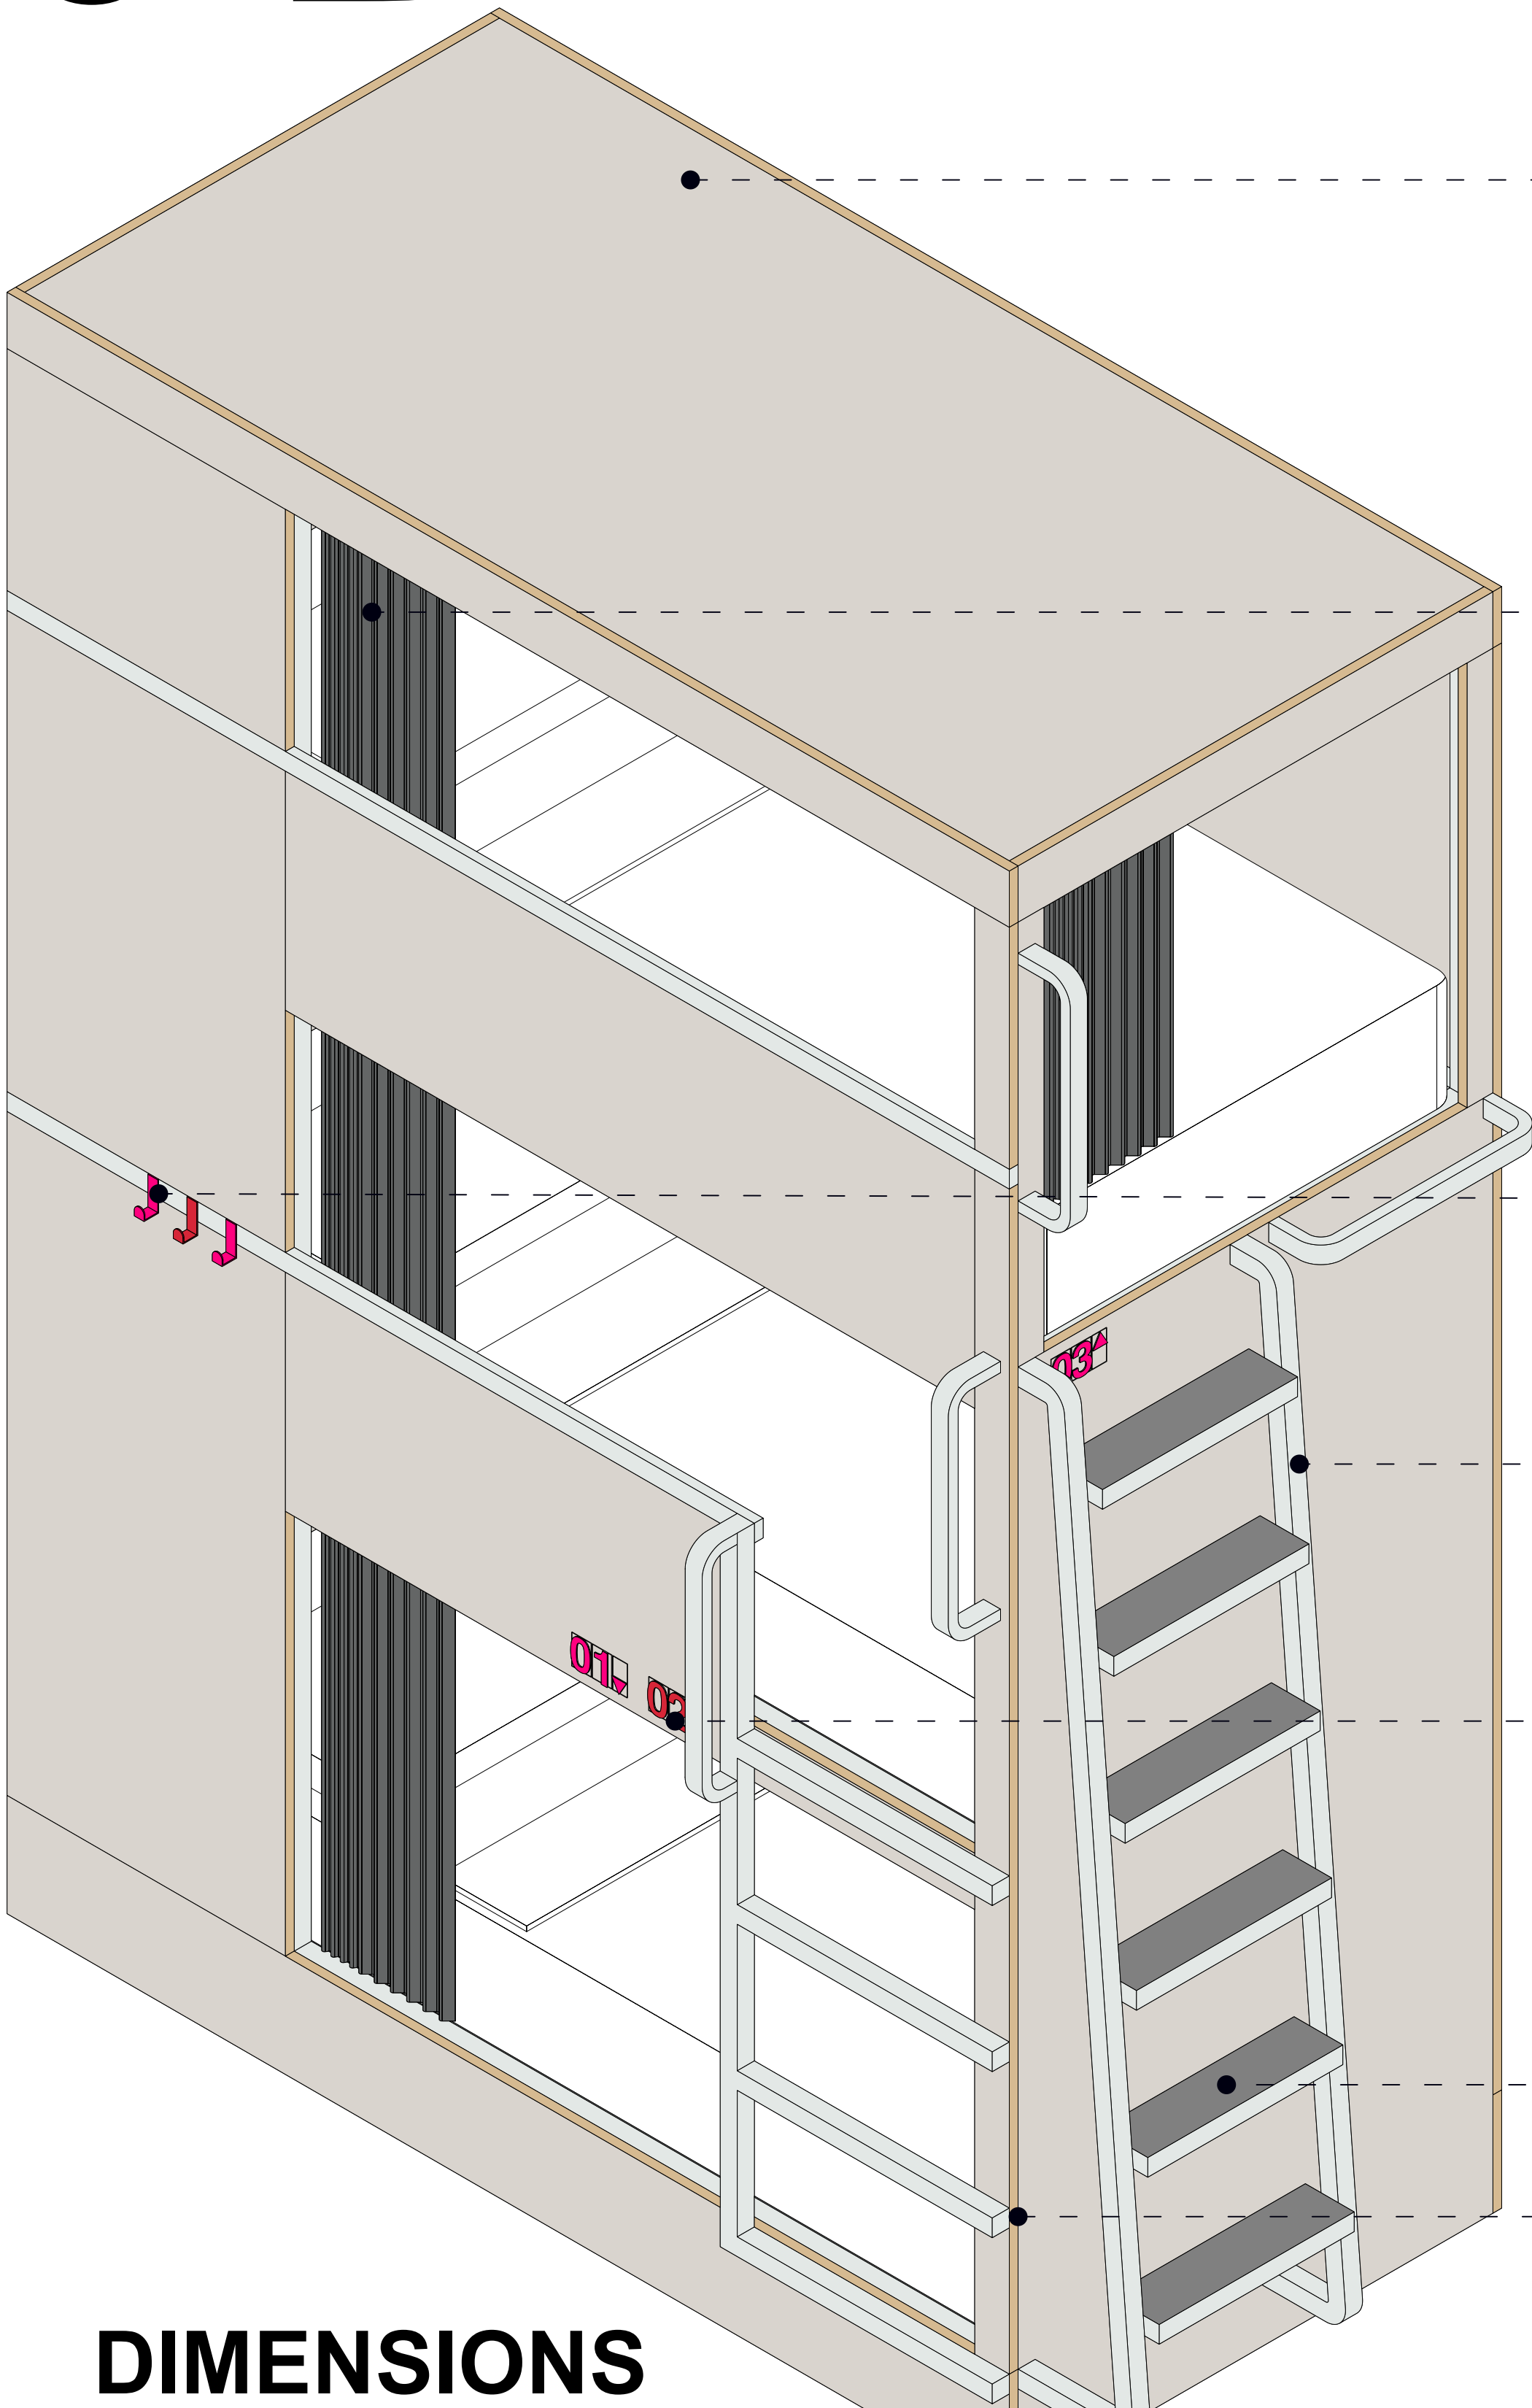

- CC-M01
Cladding - Laminated chipboard - Colour (TBC) RAL 7044, Thickness 18m (RAL Colour TBC by Clink)
- FF-C01 Metal ring curtains with a sturdy/durable pole
Privacy curtain - washable textile - colour: dark grey/anthracite less fold - Almost 1:1 fold factor to open horizontally - fire-retardant fabric
LUNA BLACKOUT by SKOPOS
TEXTURED L15 GUNMETAL (Colour TBC by Clink)
- AA-H01 Hooks - stainless steel powder-coated - RAL 3020 Red & RAL 4010 Rose
FINAL HOOKS QUANTITY & Colour TBC
- SS-F/L/G
Frame/Ladder/Guard - 3.5x3.5 cm Powder Coated Steel
Structure - Colour to match Telegrey RAL 7047 - Semi gloss finish (RAL Colour TBC by Clink)
- AA-S01
SIGNAGE - Numbers - laser-cut acrylic or MDF - thickness 5mm - spray painted - RAL 3020 Red & RAL 4010 Rose - font according to wayfinding signage design (RAL Colour TBC by Clink)
- Rubber Pad on top (Colour TBC)
- CC-M07 Visible Edges
Plywood edges


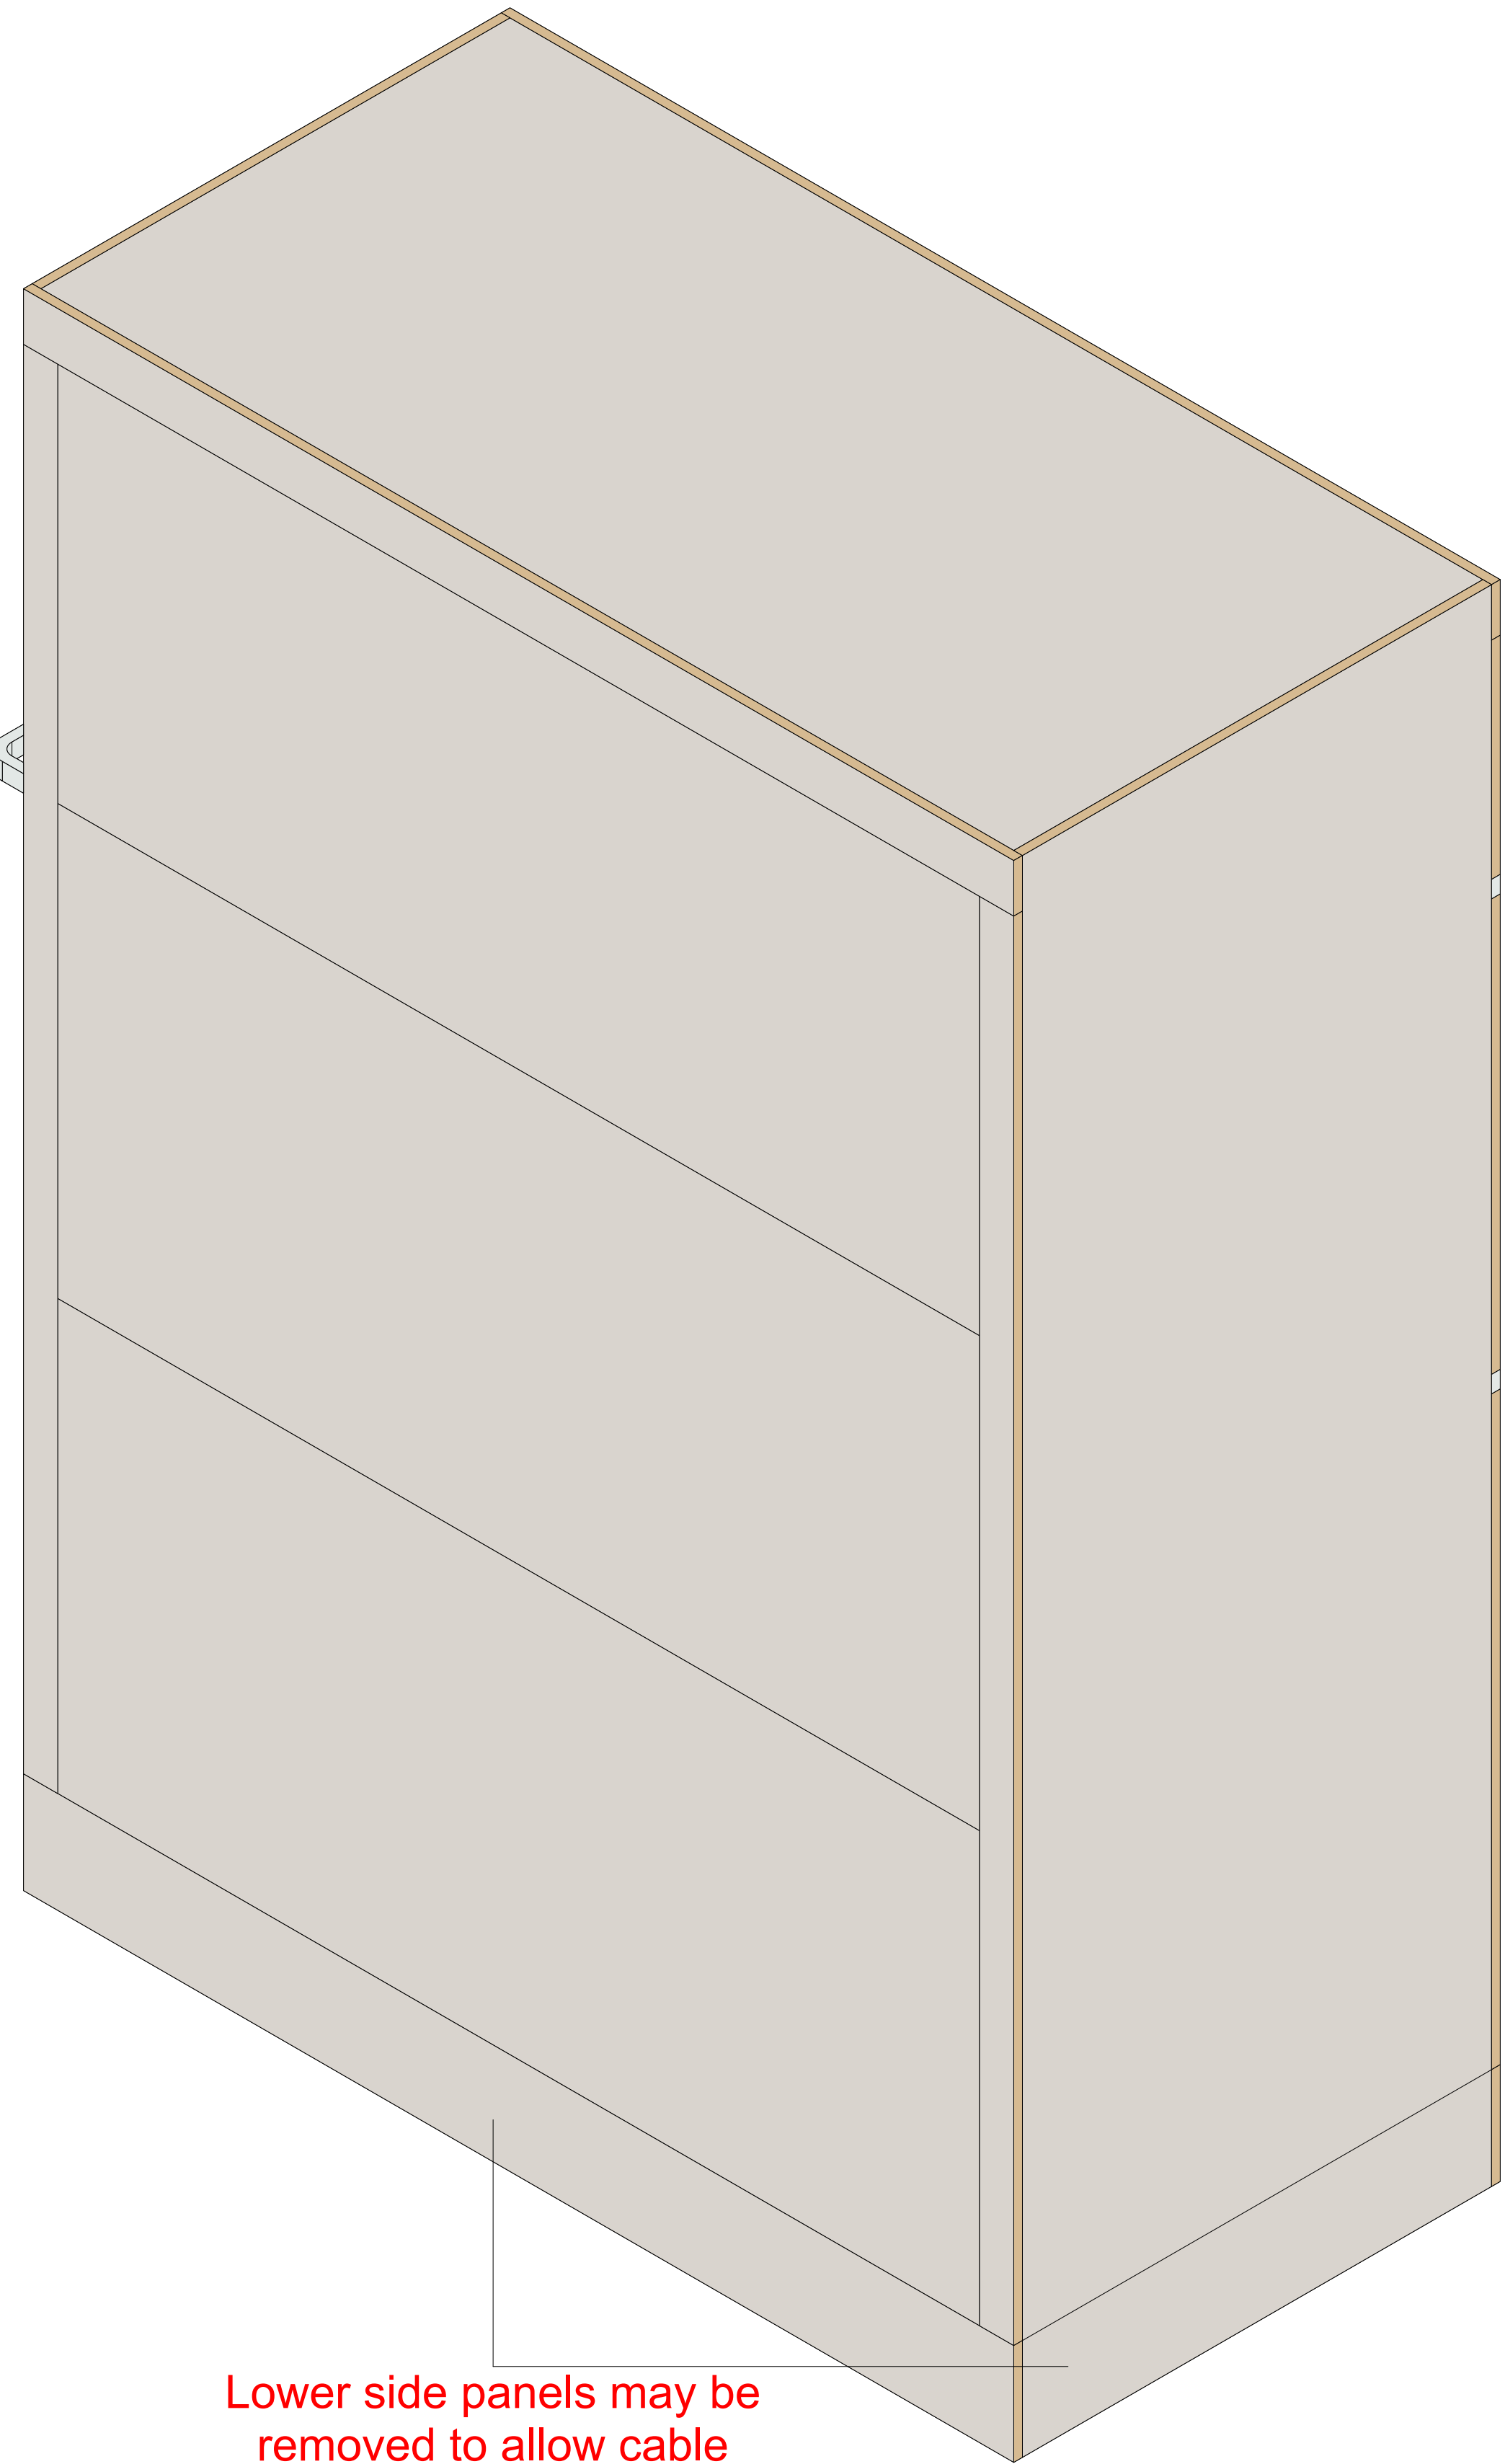


Lower side panels may be removed to allow cable connections.

DIMENSIONS
101 x 205.6 x 290.1 (WxLxH)cm

DRAFT

BUNKBEDS - TYPE 3-B (TRIPLE) - GA PLAN

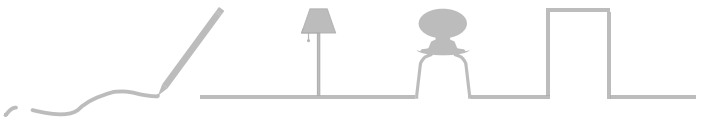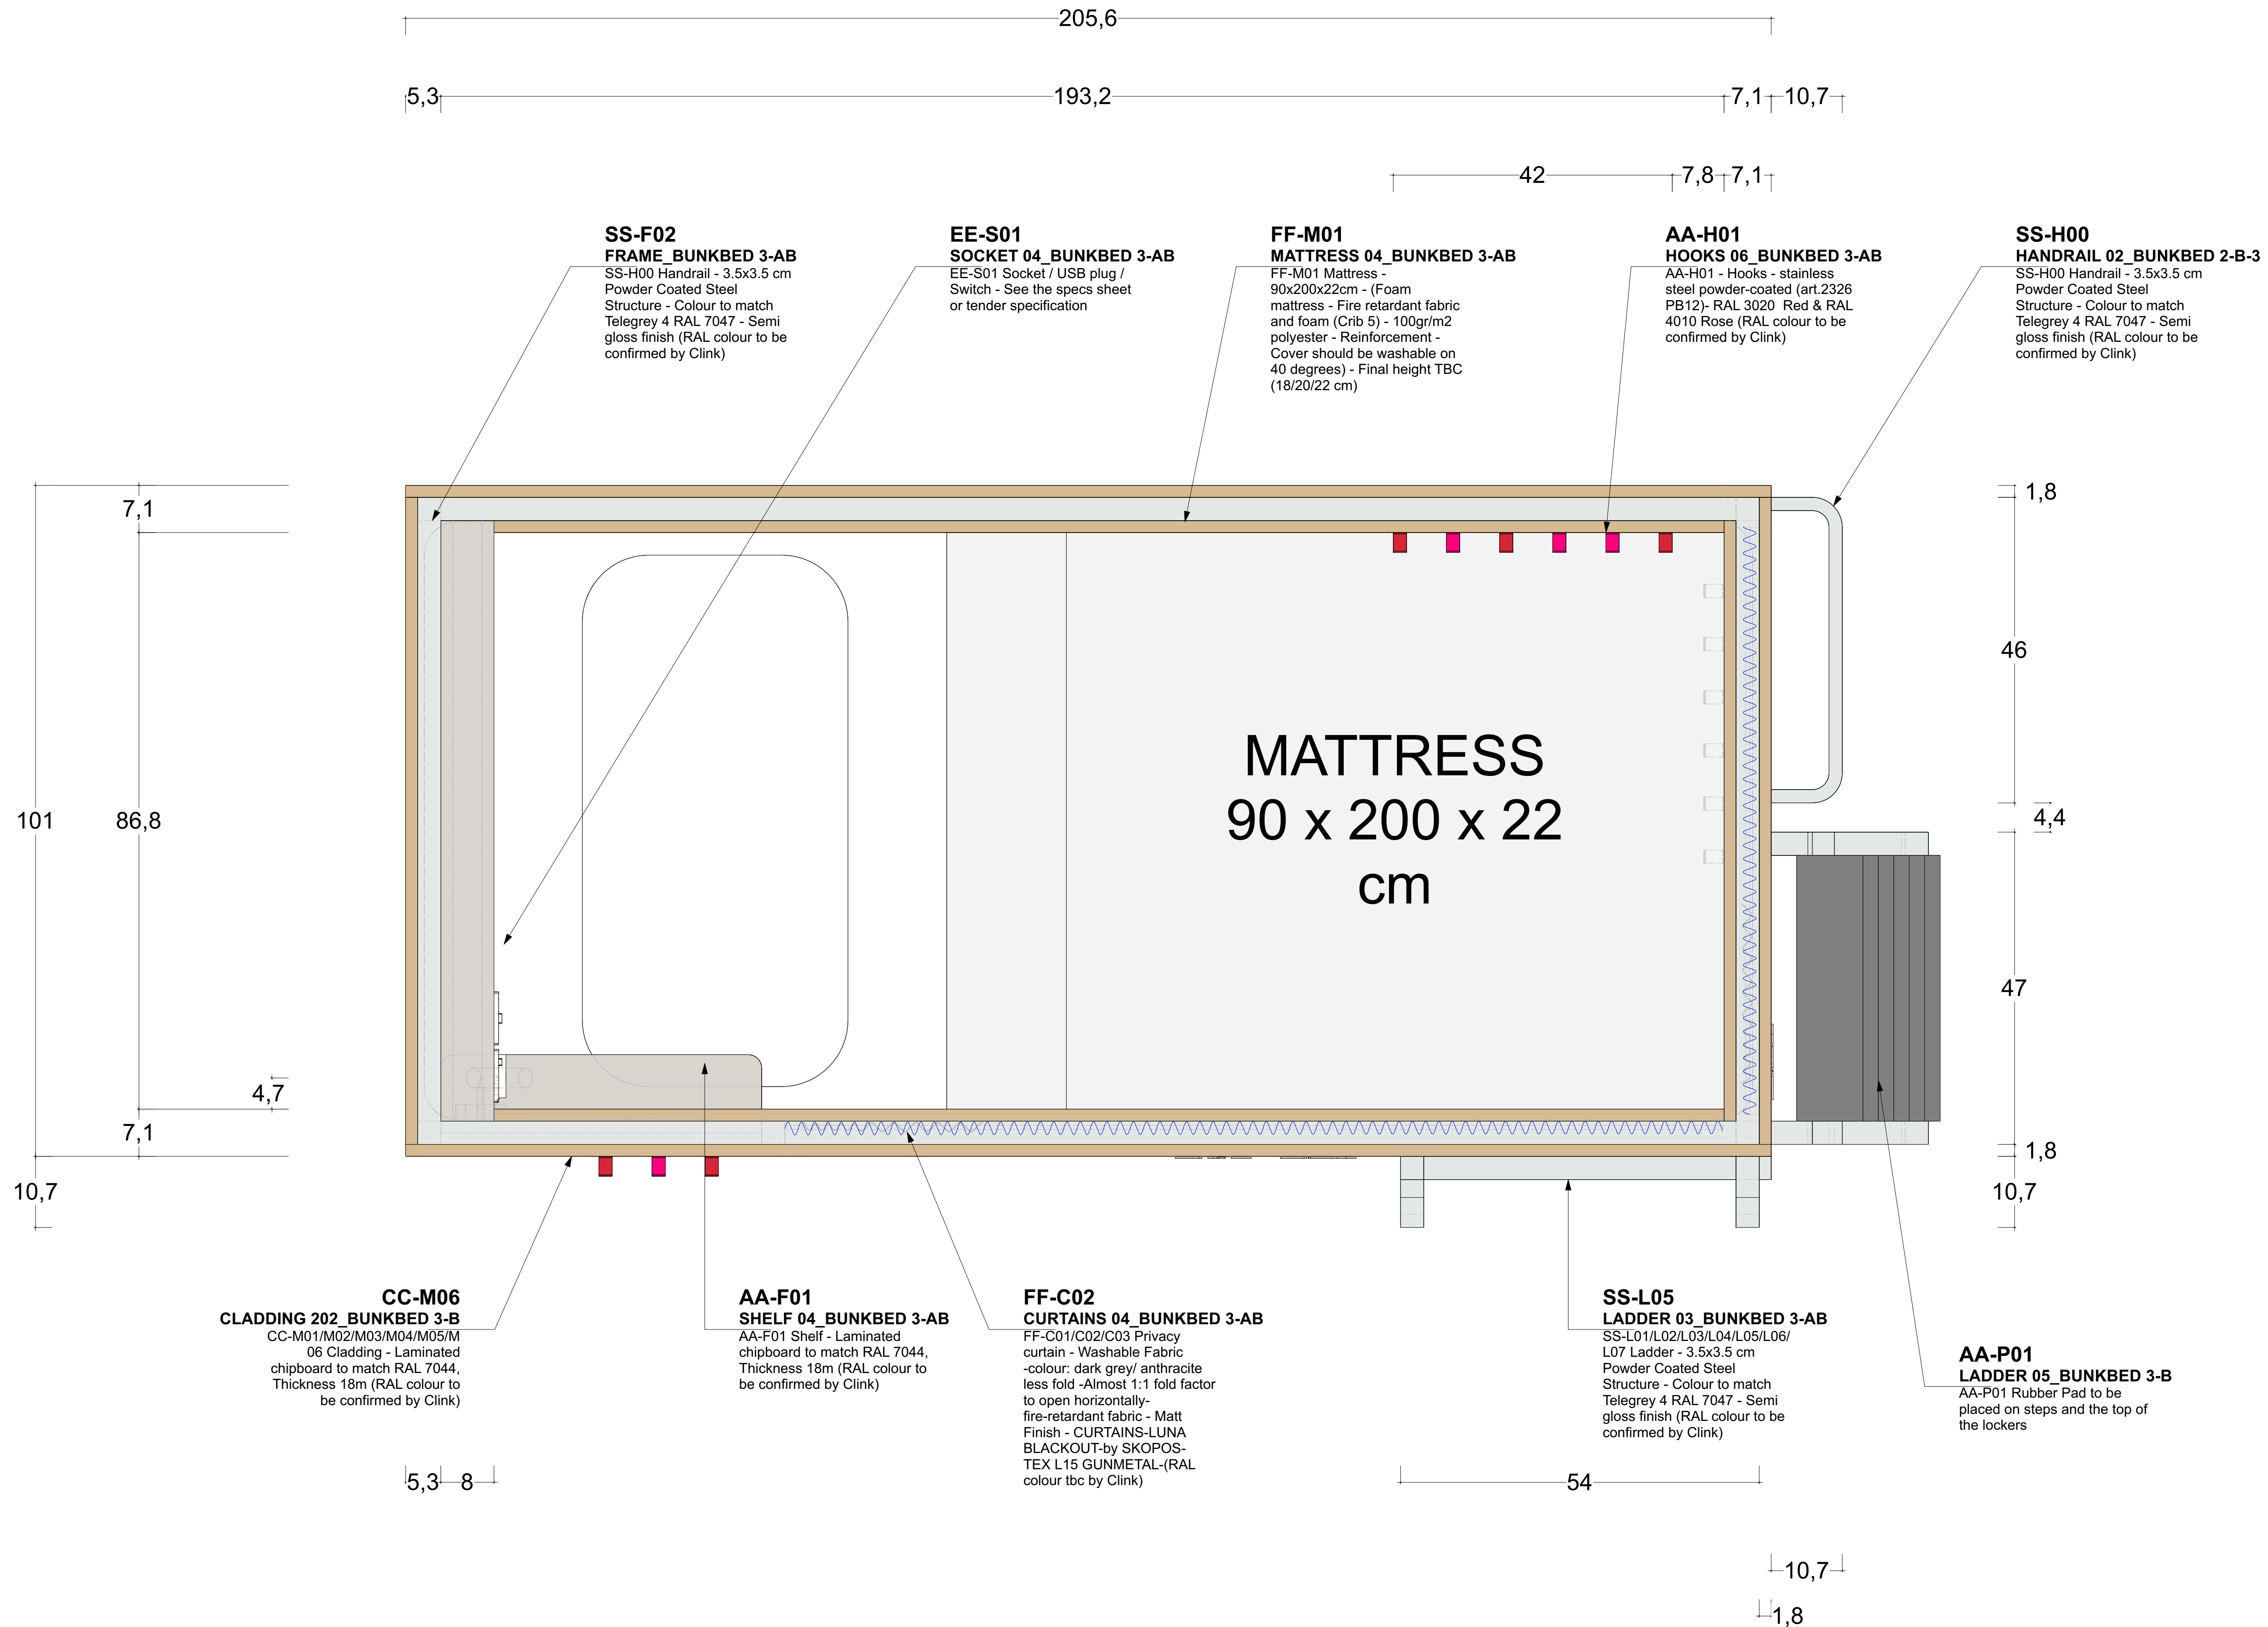

KEY

Index

A) 04.05.2026 Plan Set UP

All measurements have to be verified according to existing conditions by the contractor! Discrepancies must be reported immediately to the responsible project manager. The contractor has to produce fully dimensioned shop drawings prior to the start of the contract and they have to be approved by the client/ investor / interior designer

Project
CLINK 78 - BEDS

Logo

The logo for CLINK HOSTELS features the word "CLINK" in a large, bold, blue sans-serif font. Below it, the word "HOSTELS" is written in a smaller, blue sans-serif font. The letters are spaced out, and the overall design is clean and modern.

Project Address

CLINK 78
78 King's Cross Rd
London WC1X 9QG
United Kingdom

Client's Address

CLINK 78
78 King's Cross Rd
London WC1X 9QG
United Kingdom

Sheet Number 3-B-701

82

Sheet Title
BUNKBED 3-B GA

Level	
-------	--

File Name

260425_CLINK 78_BEDs AA DRAFT 03.vwx




Date	Sheet Size	Scale	Signed
28.04.26	A1	1:5	AA

Stefanie Jaensch INTERIOR DESIGNS

Global Headquarter I Stefanie Jaensch c/o WeWork
Tausunanlage 8 I 60329 Frankfurt a.M.
E-Mail info@stefaniejaensch.de I DE +49 (0) 174 6756098
www.stefaniejaensch.de

Legal address | Stefanie Jaensch | Offenbacher Landstraße 434 | 60599 Frankfurt a.M.
© 2023 All Rights Reserved | Stefanie Jaensch

BUNKBEDS - TYPE 3-B (TRIPLE) - FRONT ELEVATION

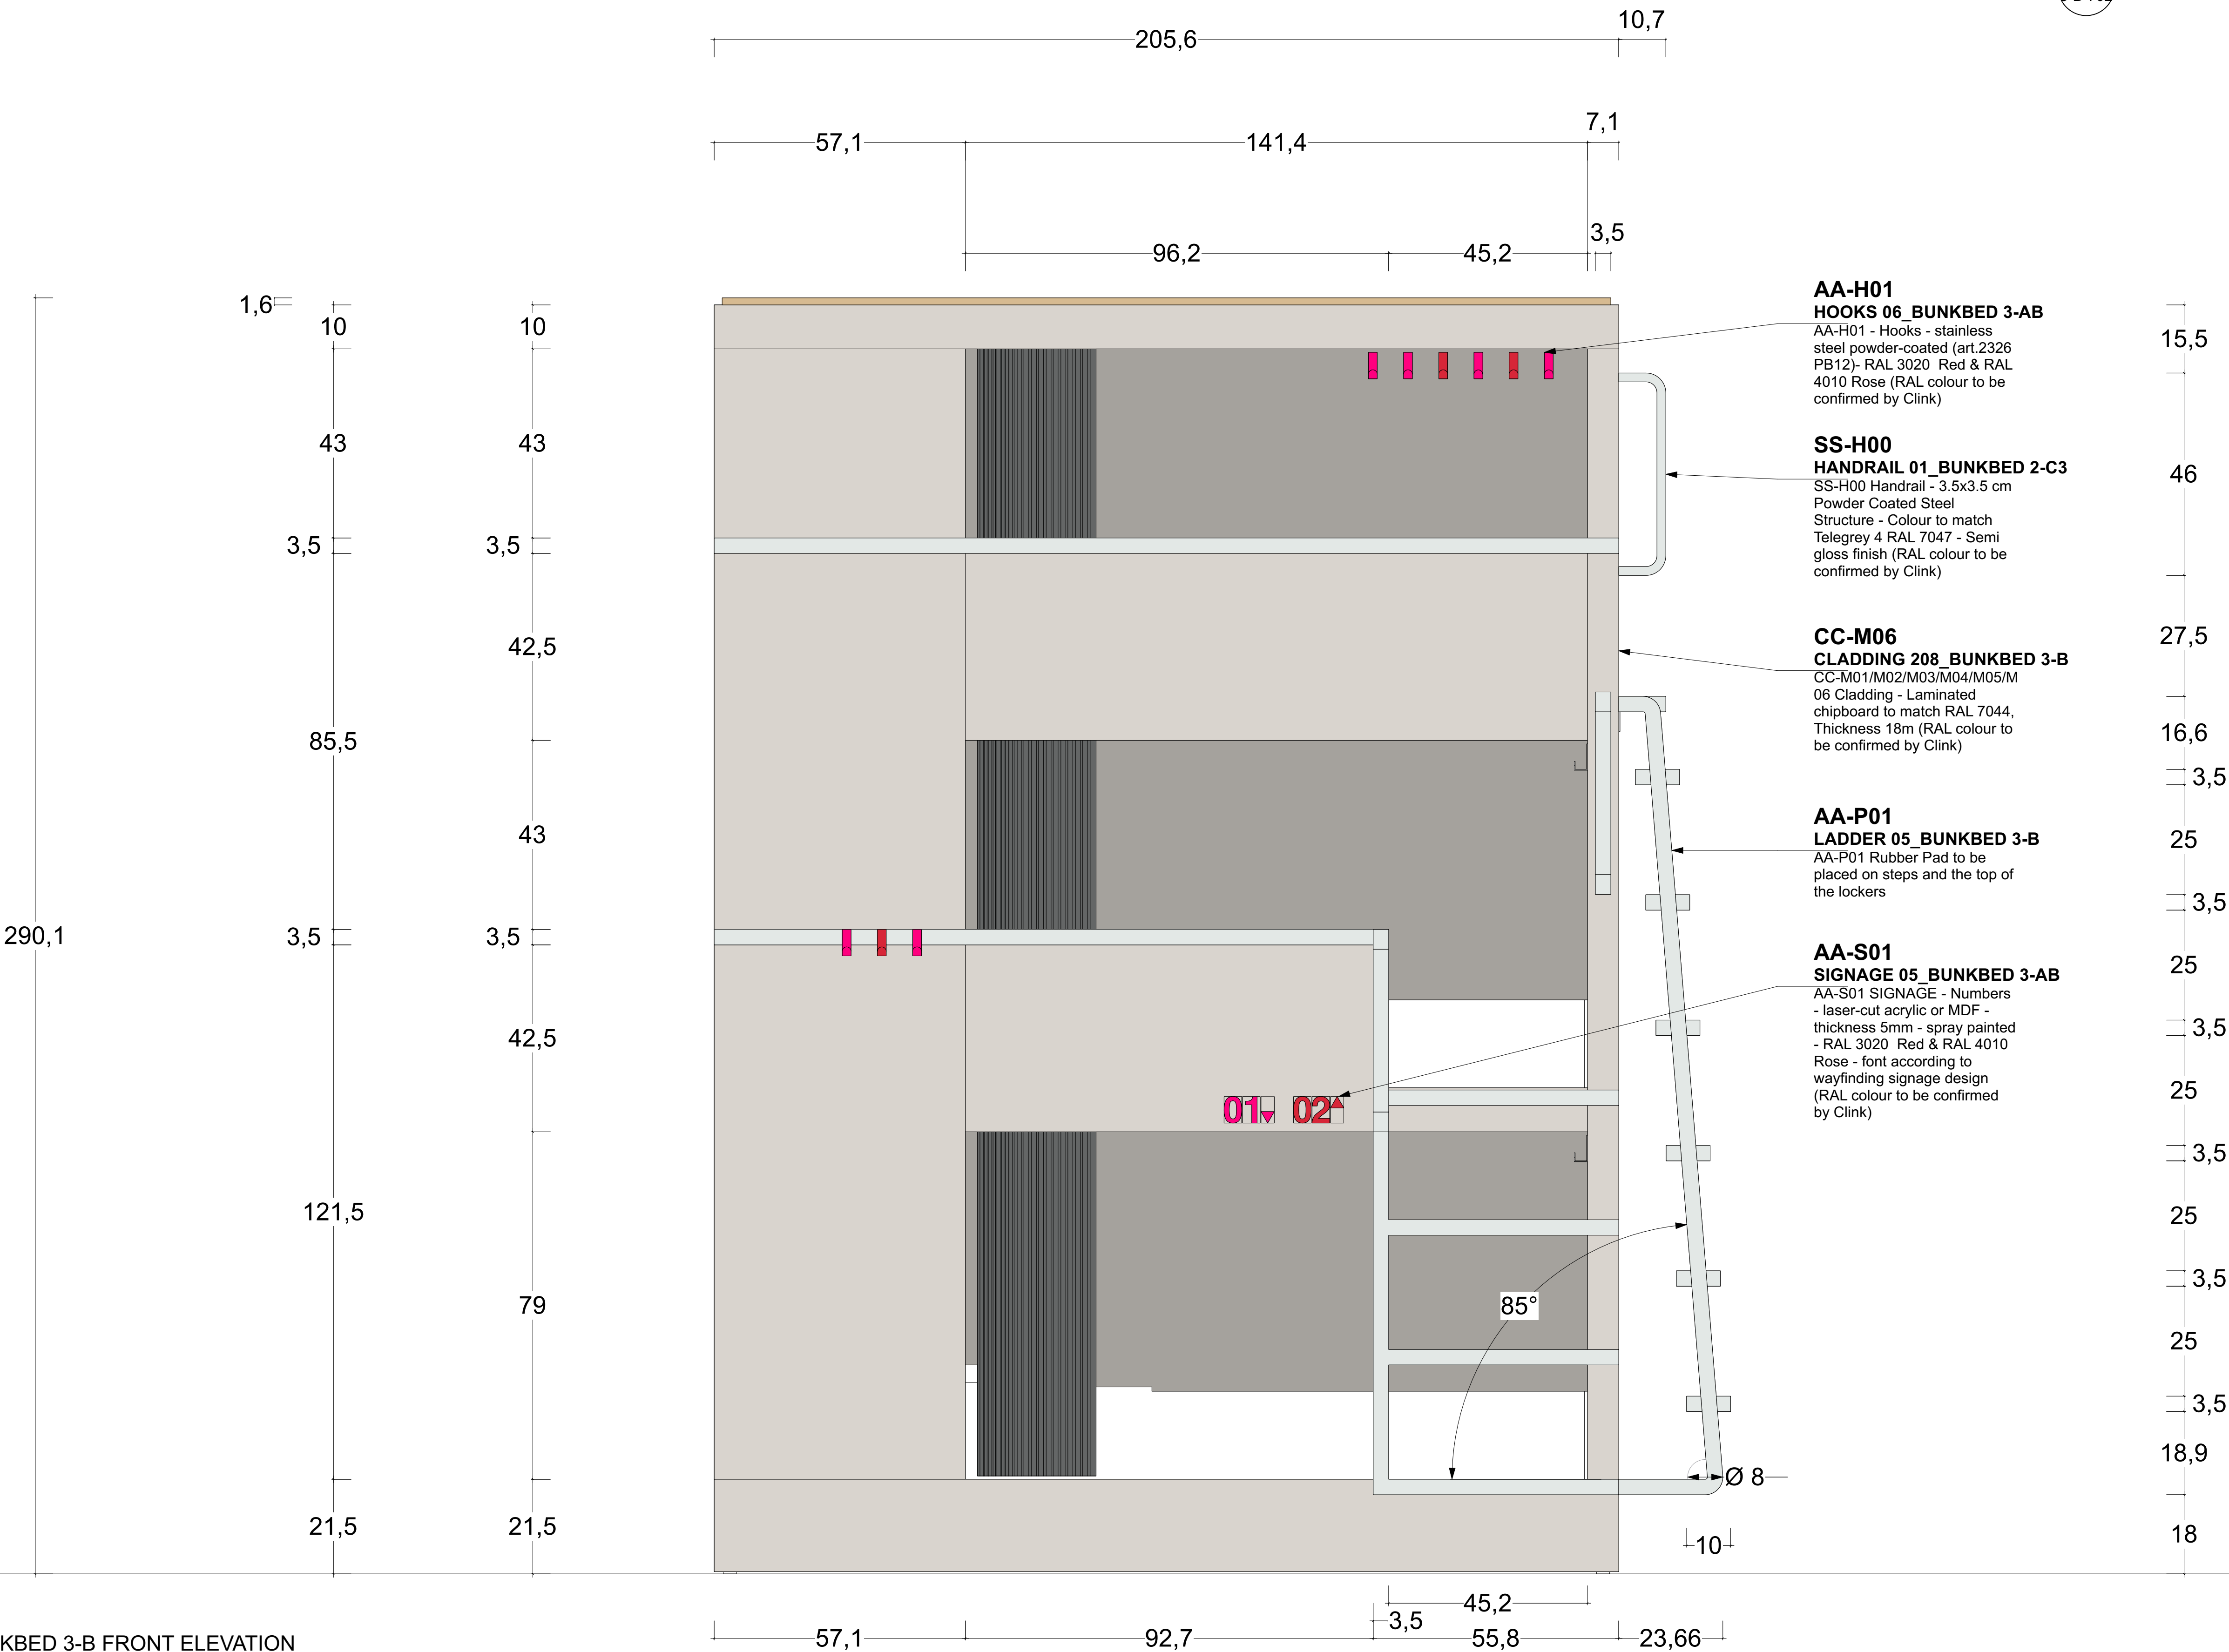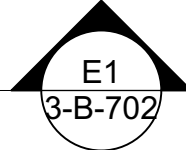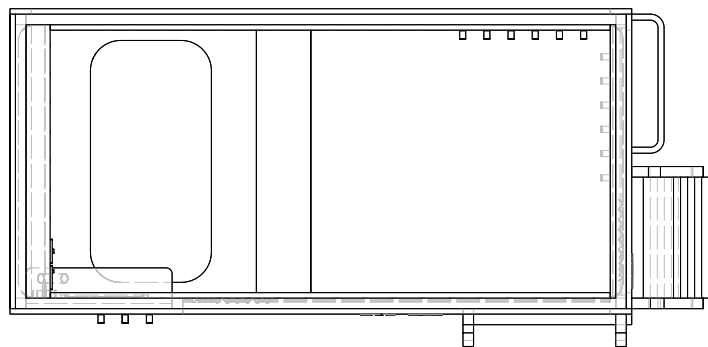

KEY

Index

A) 04.05.2026 Plan Set UP

All measurements have to be verified according to existing conditions by the contractor! Discrepancies must be reported immediately to the responsible project manager. The contractor has to produce fully dimensioned shop drawings prior to the start of the contract and they have to be approved by the client/ investor / interior designer

Project

CLINK 78 - BEDS

Logo



Project Address

CLINK 78
78 King's Cross Rd
London WC1X 9QG
United Kingdom

Client's Address

CLINK 78
78 King's Cross Rd
London WC1X 9QG
United Kingdom

Sheet Number 3-B-702		Total Sheets 82
Sheet Title BUNKBED 3-B FRONT ELEVATION		Level
File Name 260425_CLINK 78_BEDs AA DRAFT 03.vwx		
Date 28.04.26	Sheet Size A1	Scale 1:8
		Signed AA

Stefanie Jaensch INTERIOR DESIGNS

Global Headquarter | Stefanie Jaensch c/o WeWork
Taubusanlage 8 | 60329 Frankfurt a.M.

E-Mail info@stefaniejaensch.de | DE +49 (0) 174 6756098

www.stefaniejaensch.de



Legal address | Stefanie Jaensch | Offenbacher Landstraße 434 | 60599 Frankfurt a.M.

© 2023 All Rights Reserved | Stefanie Jaensch

E1

BUNKBED 3-B FRONT ELEVATION
Scale: 1:8

BUNKBEDS - TYPE 3-B (TRIPLE) - BACK ELEVATION

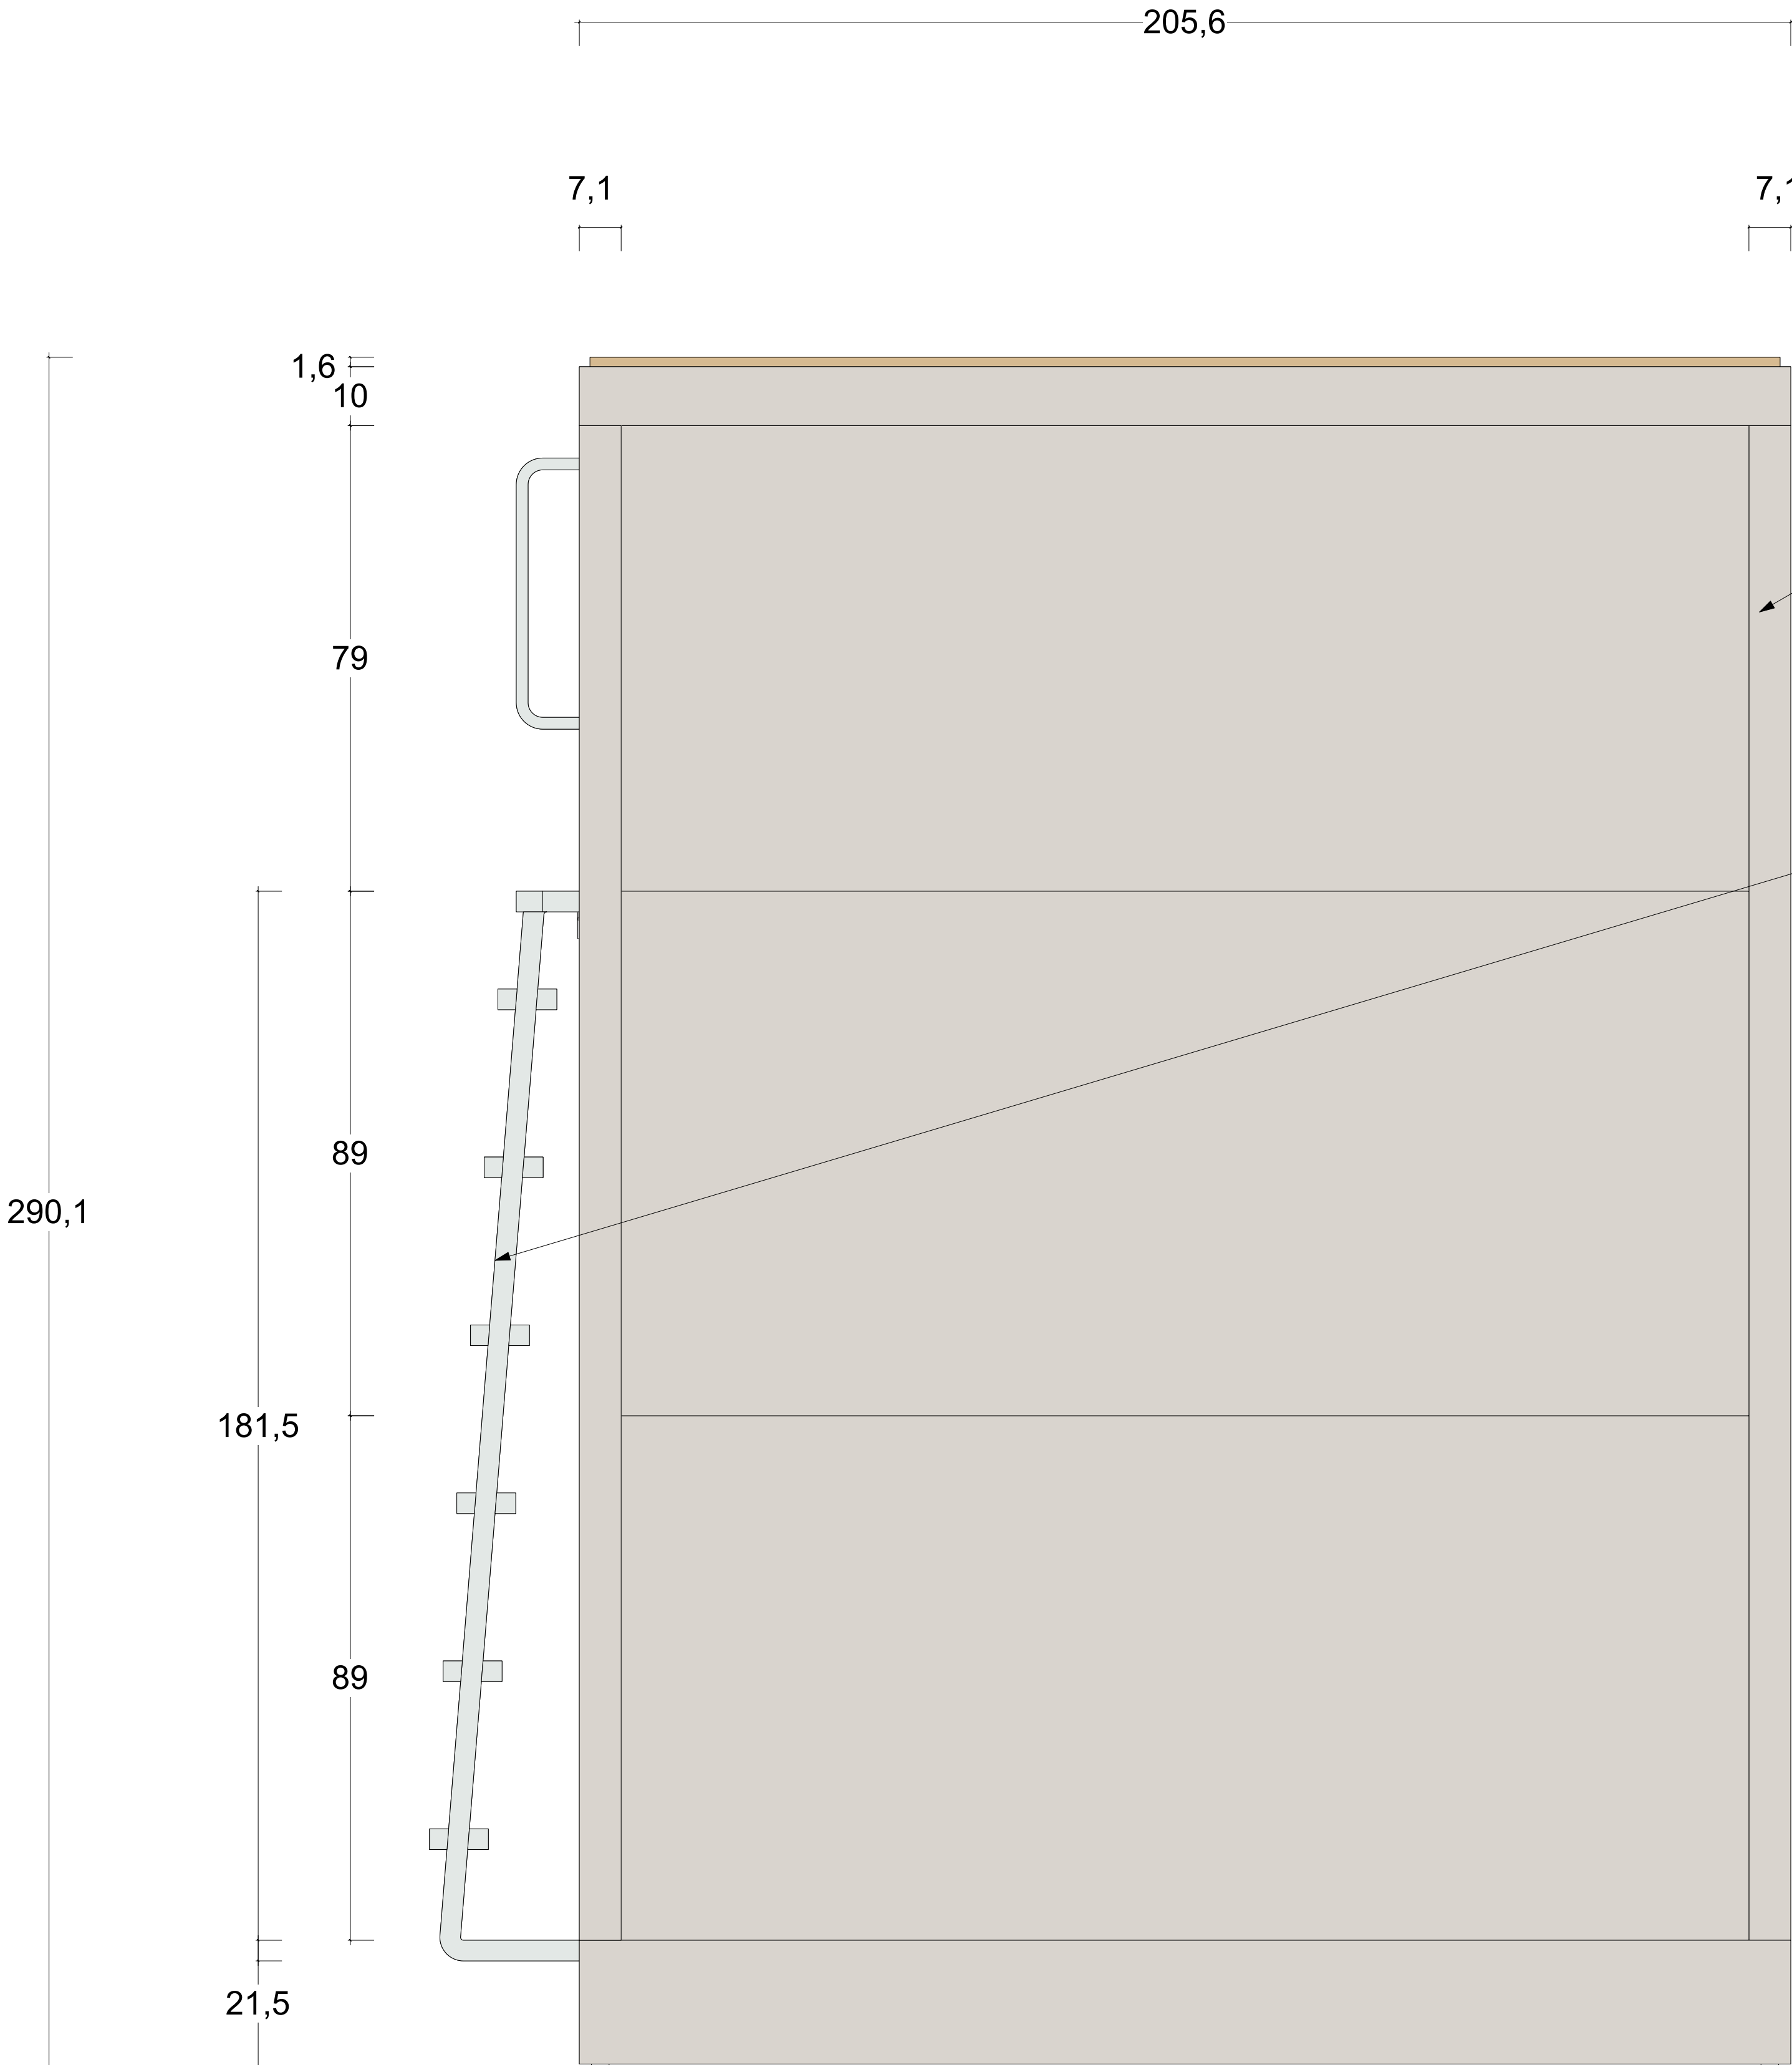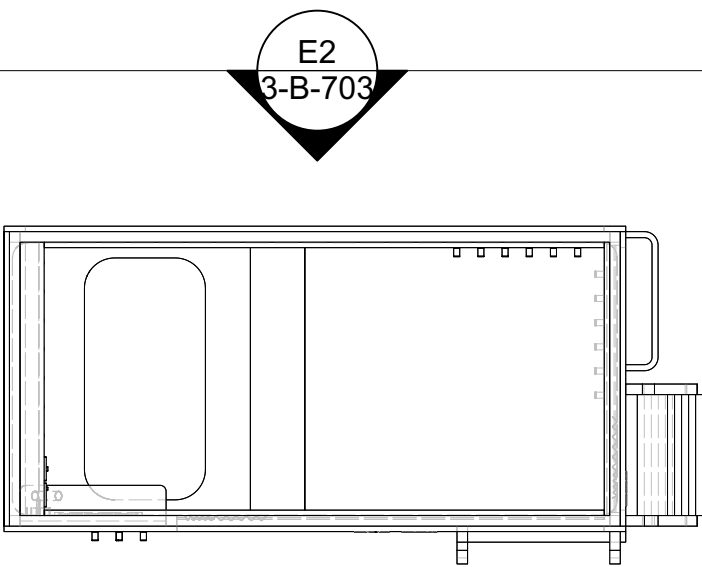

CC-M06
CLADDING 152_BUNKBED 3-B
CC-M01/M02/M03/M04/M05/M
06 Cladding - Laminated
chipboard to match RAL 7044,
Thickness 18m (RAL colour to
be confirmed by Clink)

AA-P01
LADDER 05_BUNKBED 3-B
AA-P01 Rubber Pad to be
placed on steps and the top of
the lockers



KEY

Index
A) 04.05.2026 Plan Set UP

All measurements have to be verified according to existing conditions by the contractor! Discrepancies must be reported immediately to the responsible project manager. The contractor has to produce fully dimensioned shop drawings prior to the start of the contract and they have to be approved by the client/ investor / interior designer

Project
CLINK 78 - BEDS



Project Address
CLINK 78
78 King's Cross Rd
London WC1X 9QG
United Kingdom




Client's Address
CLINK 78
78 King's Cross Rd
London WC1X 9QG
United Kingdom

Sheet Number 3-B-703		Total Sheets 82
Sheet Title BUNKBED 3-B BACK ELEVATION		Level
File Name 260425_CLINK 78_BEDs AA DRAFT 03.vwx		

Date	Sheet Size	Scale	Signed
28.04.26	A1	1:8	AA

Stefanie Jaensch **INTERIOR DESIGNS**
Global Headquarter | Stefanie Jaensch c/o WeWork
Taunusanlage 8 | 60329 Frankfurt a.M.
E-Mail info@stefaniejaensch.de | DE +49 (0) 174 6756098
www.stefaniejaensch.de
Legal address | Stefanie Jaensch | Offenbacher Landstraße 434 | 60599 Frankfurt a.M.
© 2023 All Rights Reserved | Stefanie Jaensch

BUNKBEDS - TYPE 3-B (TRIPLE) - RIGHT ELEVATION

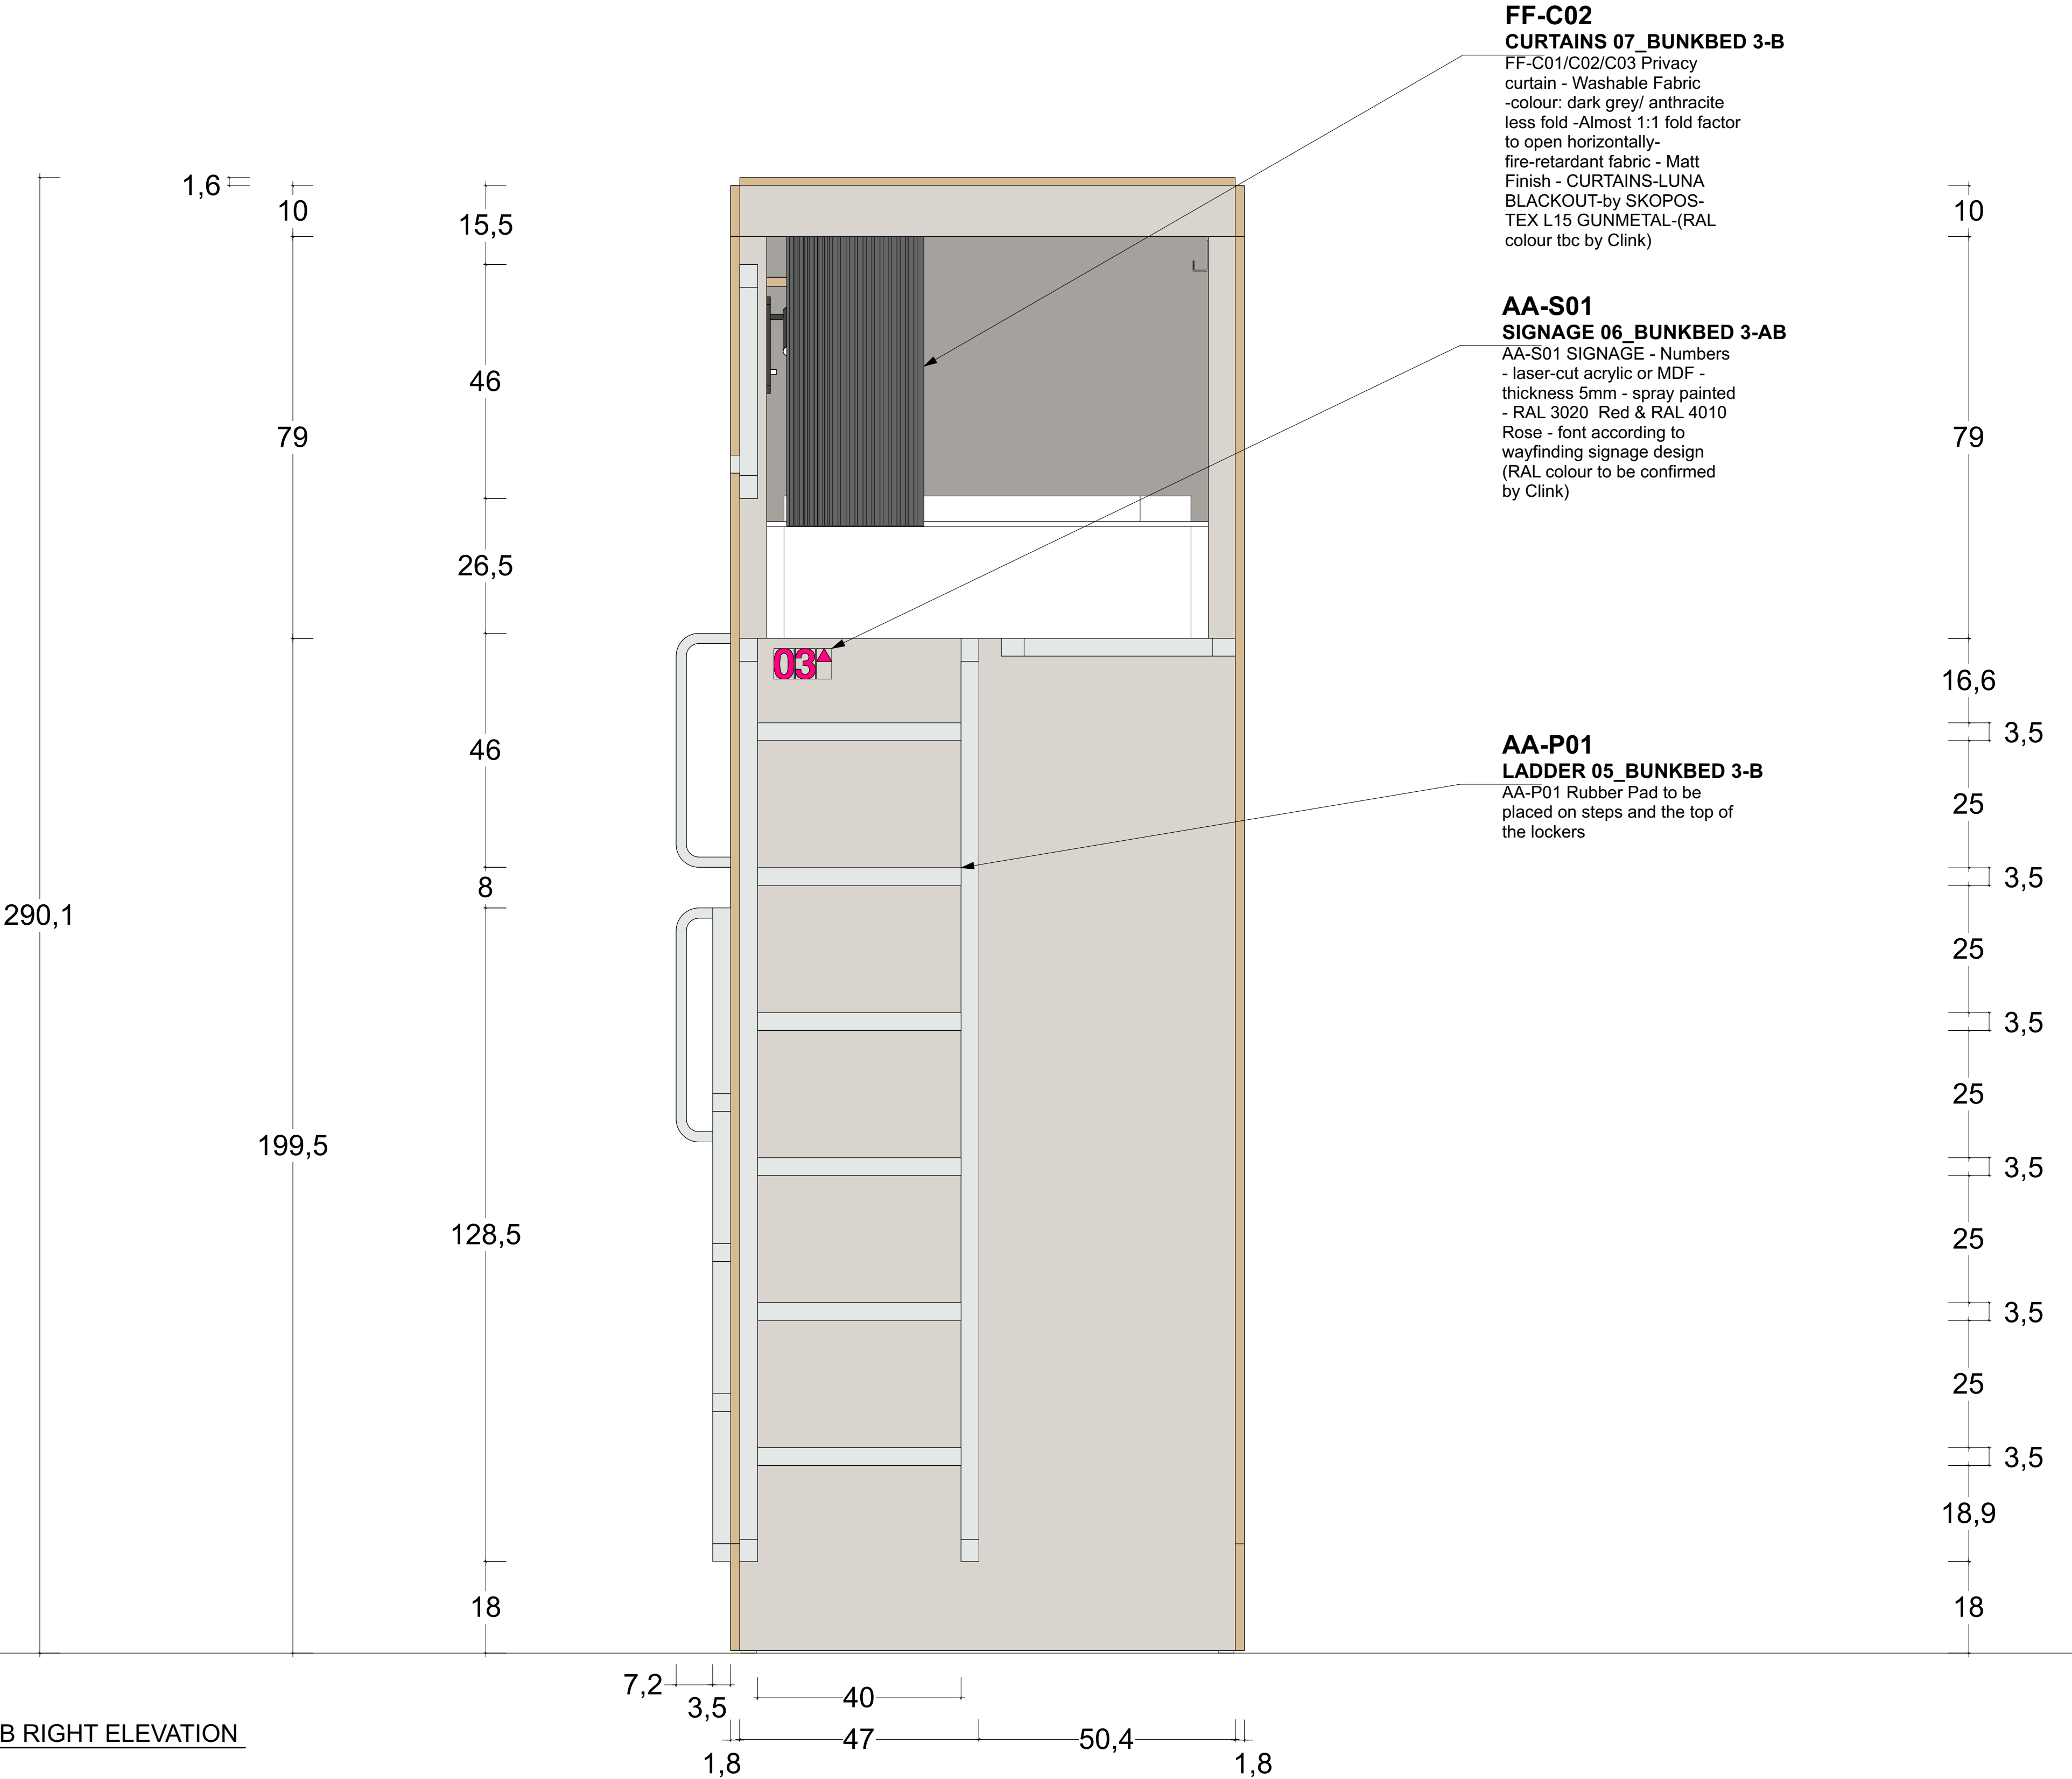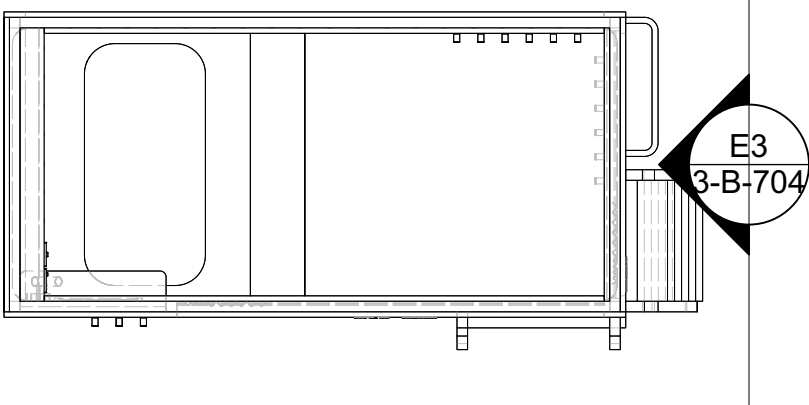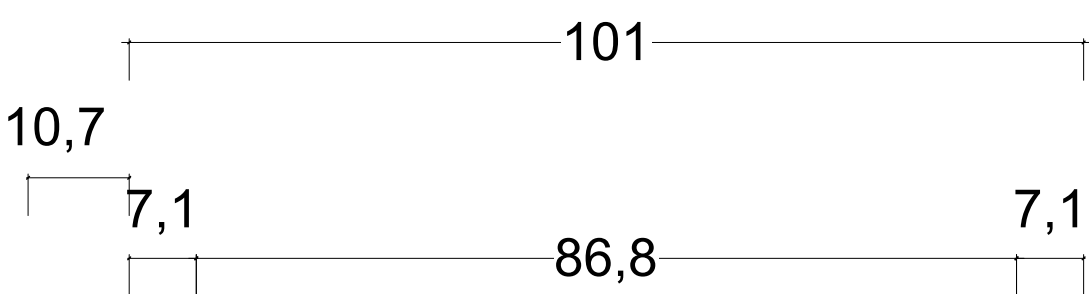

KEY

Index

A) 04.05.2026 Plan Set UP

All measurements have to be verified according to existing conditions by the contractor! Discrepancies must be reported immediately to the responsible project manager. The contractor has to produce fully dimensioned shop drawings prior to the start of the contract and they have to be approved by the client/ investor / interior designer

Project

CLINK 78 - BEDS

Logo



Project Address

CLINK 78
78 King's Cross Rd
London WC1X 9QG
United Kingdom

Client's Address

CLINK 78
78 King's Cross Rd
London WC1X 9QG
United Kingdom

Sheet Number 3-B-704		Total Sheets 82	
Sheet Title BUNKBED 3-B RIGHT ELEVATION		Level	
File Name 260425_CLINK 78_BEDs AA DRAFT 03.vwx			
Date 28.04.26	Sheet Size A1	Scale 1:8	Signed AA

Stefanie Jaensch INTERIOR DESIGNS



Global Headquarter | Stefanie Jaensch c/o WeWork
Taunusanlage 8 | 60329 Frankfurt a.M.
E-Mail info@stefaniejaensch.de | DE +49 (0) 174 6756098
www.stefaniejaensch.de

Legal address | Stefanie Jaensch | Offenbacher Landstraße 434 | 60599 Frankfurt a.M.
© 2023 All Rights Reserved | Stefanie Jaensch

E3

BUNKBED 3-B RIGHT ELEVATION
Scale: 1:8

BUNKBEDS - TYPE 3-B (TRIPLE) - LEFT ELEVATION

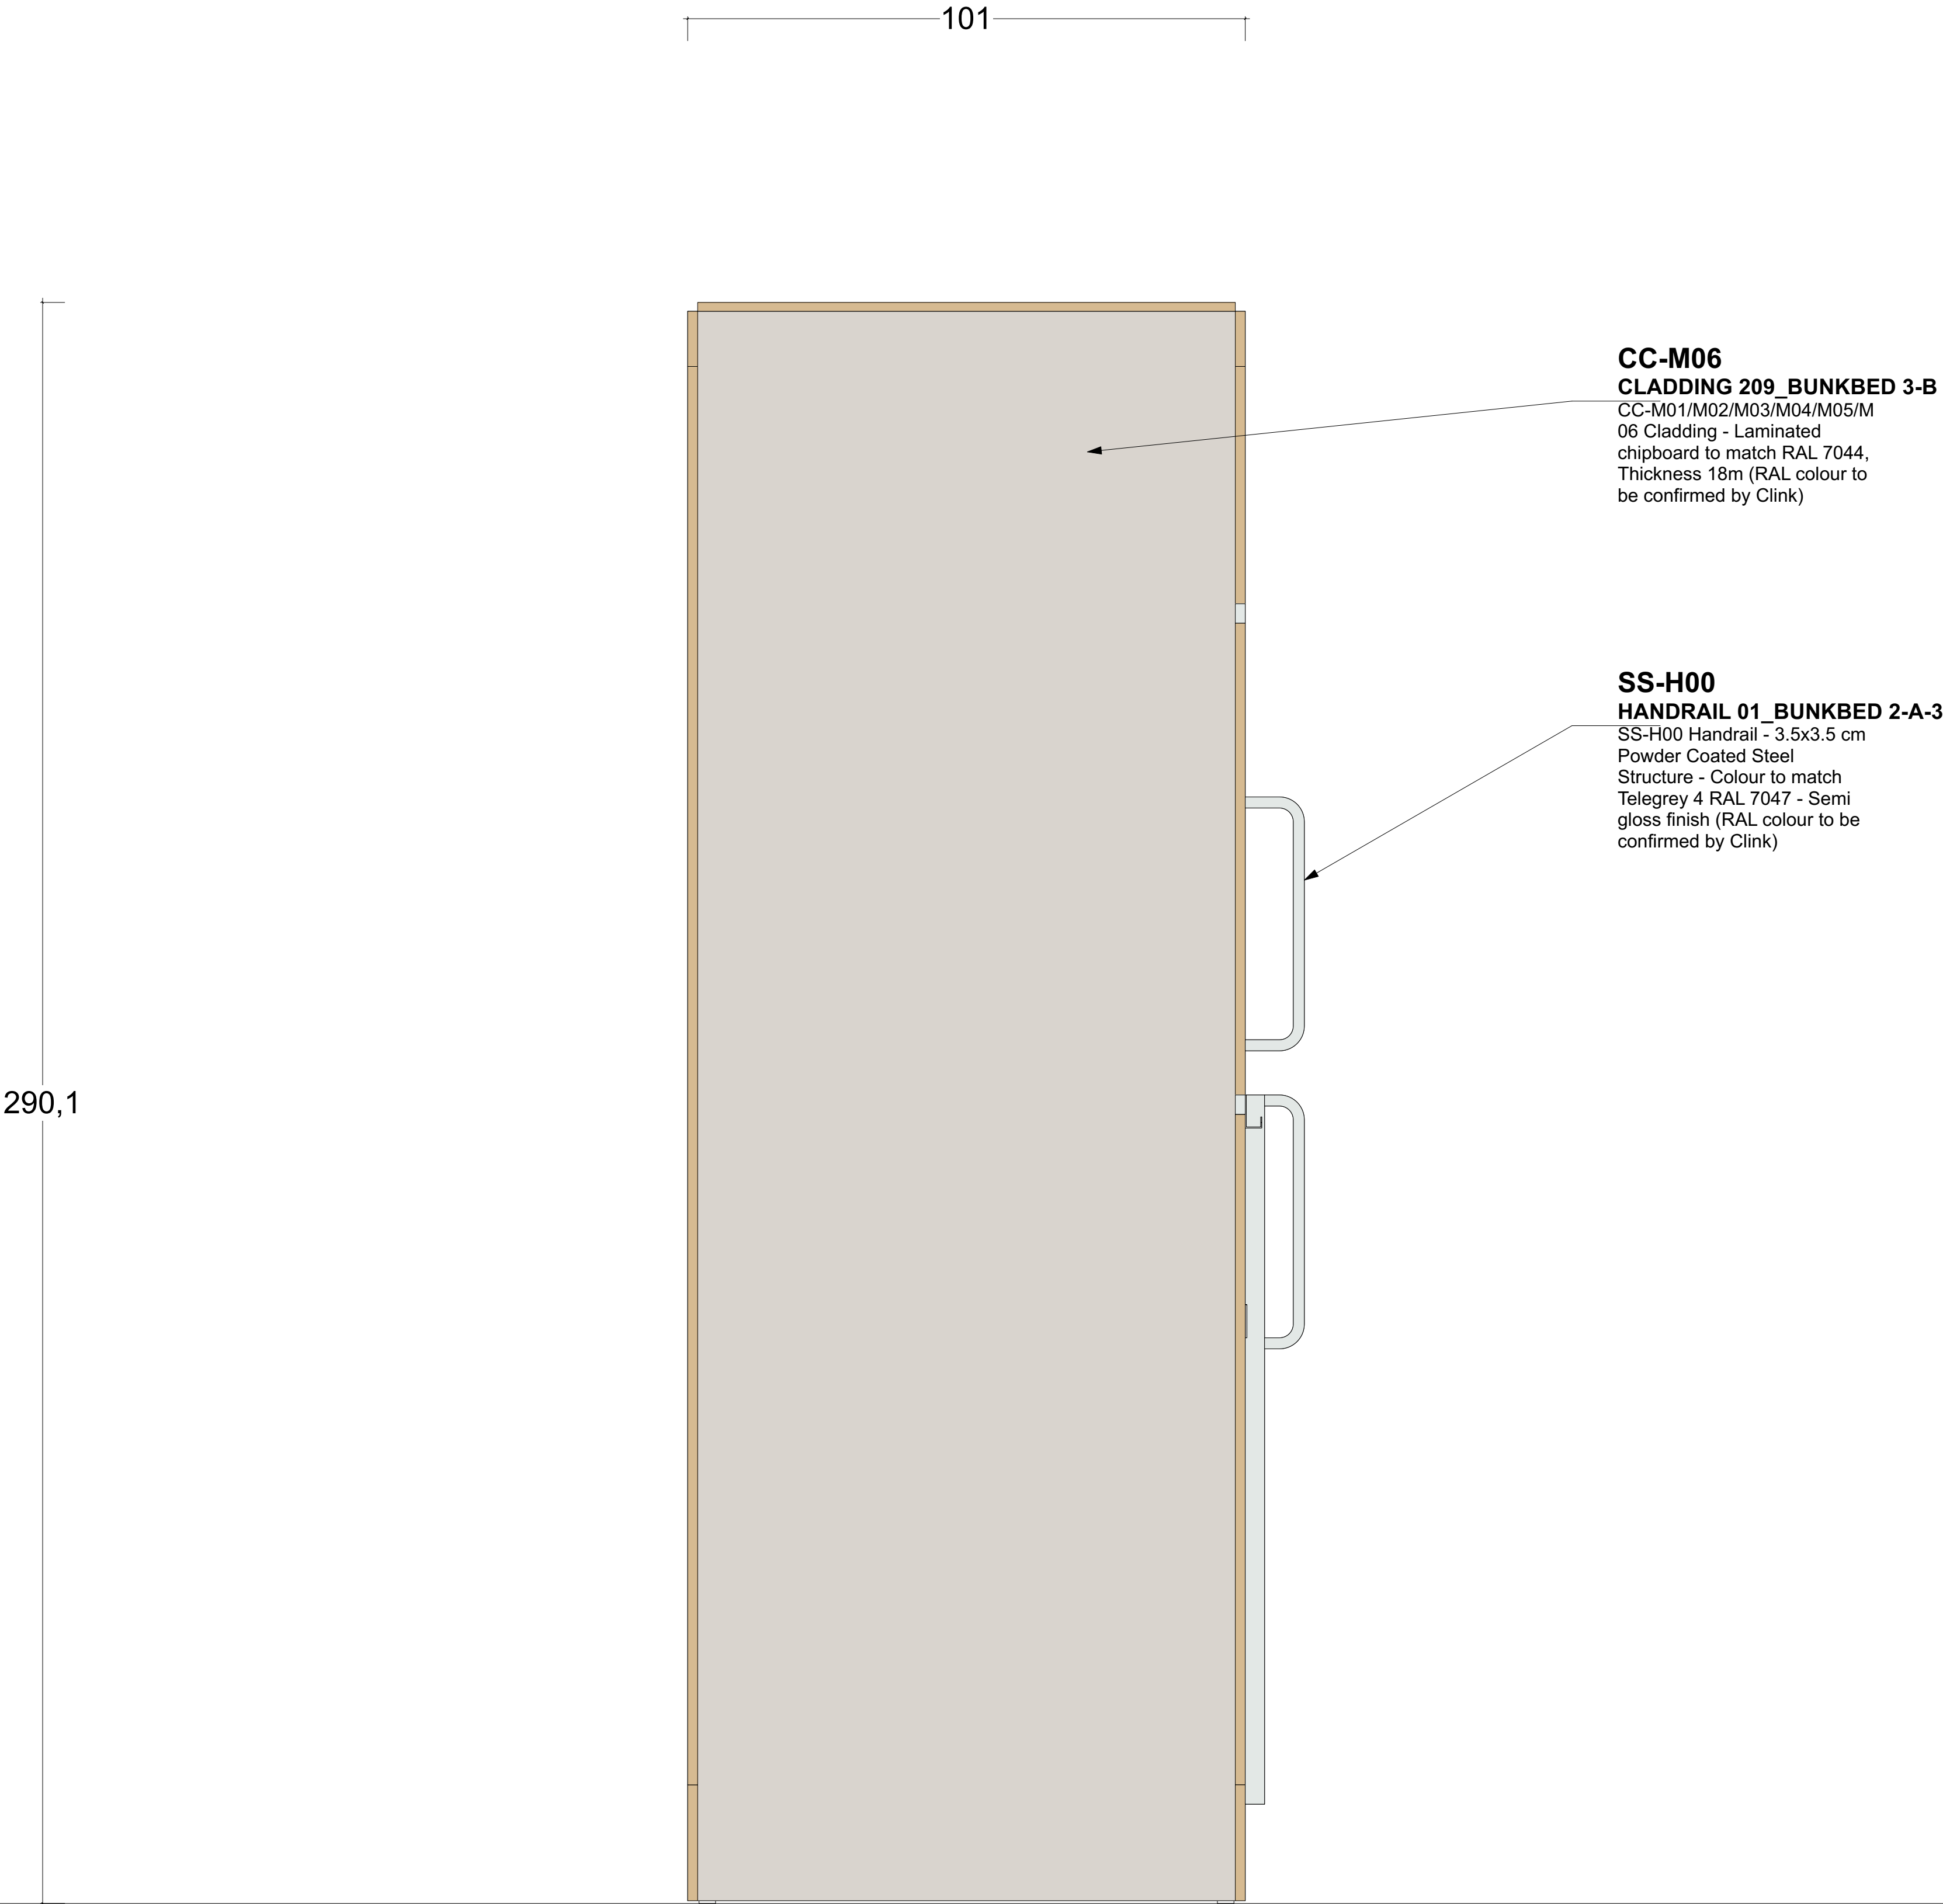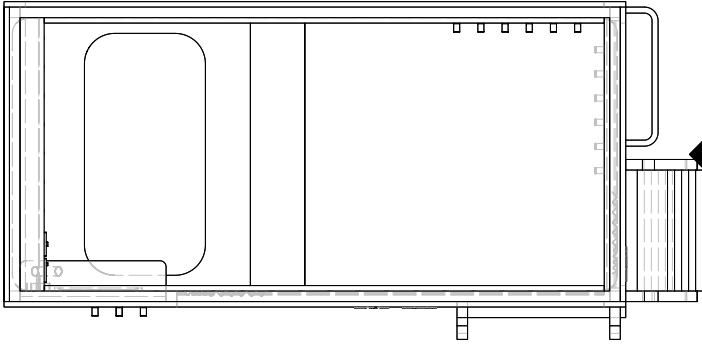

KEY

Index

A) 04.05.2026 Plan Set UP

All measurements have to be verified according to existing conditions by the contractor! Discrepancies must be reported immediately to the responsible project manager. The contractor has to produce fully dimensioned shop drawings prior to the start of the contract and they have to be approved by the client/ investor / interior designer

Project

CLINK 78 - BEDS

Logo



Project Address

CLINK 78
78 King's Cross Rd
London WC1X 9QG
United Kingdom

Client's Address

CLINK 78
78 King's Cross Rd
London WC1X 9QG
United Kingdom

Sheet Number 3-B-705		Total Sheets 82
Sheet Title BUNKBED 3-B LEFT ELEVATION		Level
File Name 260425_CLINK 78_BEDs AA DRAFT 03.vwx		

Date	Sheet Size	Scale	Signed
28.04.26	A1	1:8	AA

Stefanie Jaensch INTERIOR DESIGNS

Global Headquarter | Stefanie Jaensch c/o WeWork

Taunusanlage 8 | 60329 Frankfurt a.M.


E-Mail info@stefaniejaensch.de | DE +49 (0) 174 6756098

www.stefaniejaensch.de

Legal address | Stefanie Jaensch | Offenbacher Landstraße 434 | 60599 Frankfurt a.M.

© 2023 All Rights Reserved | Stefanie Jaensch

BUNKBEDS - TYPE 3-B (TRIPLE) - SECTION 1

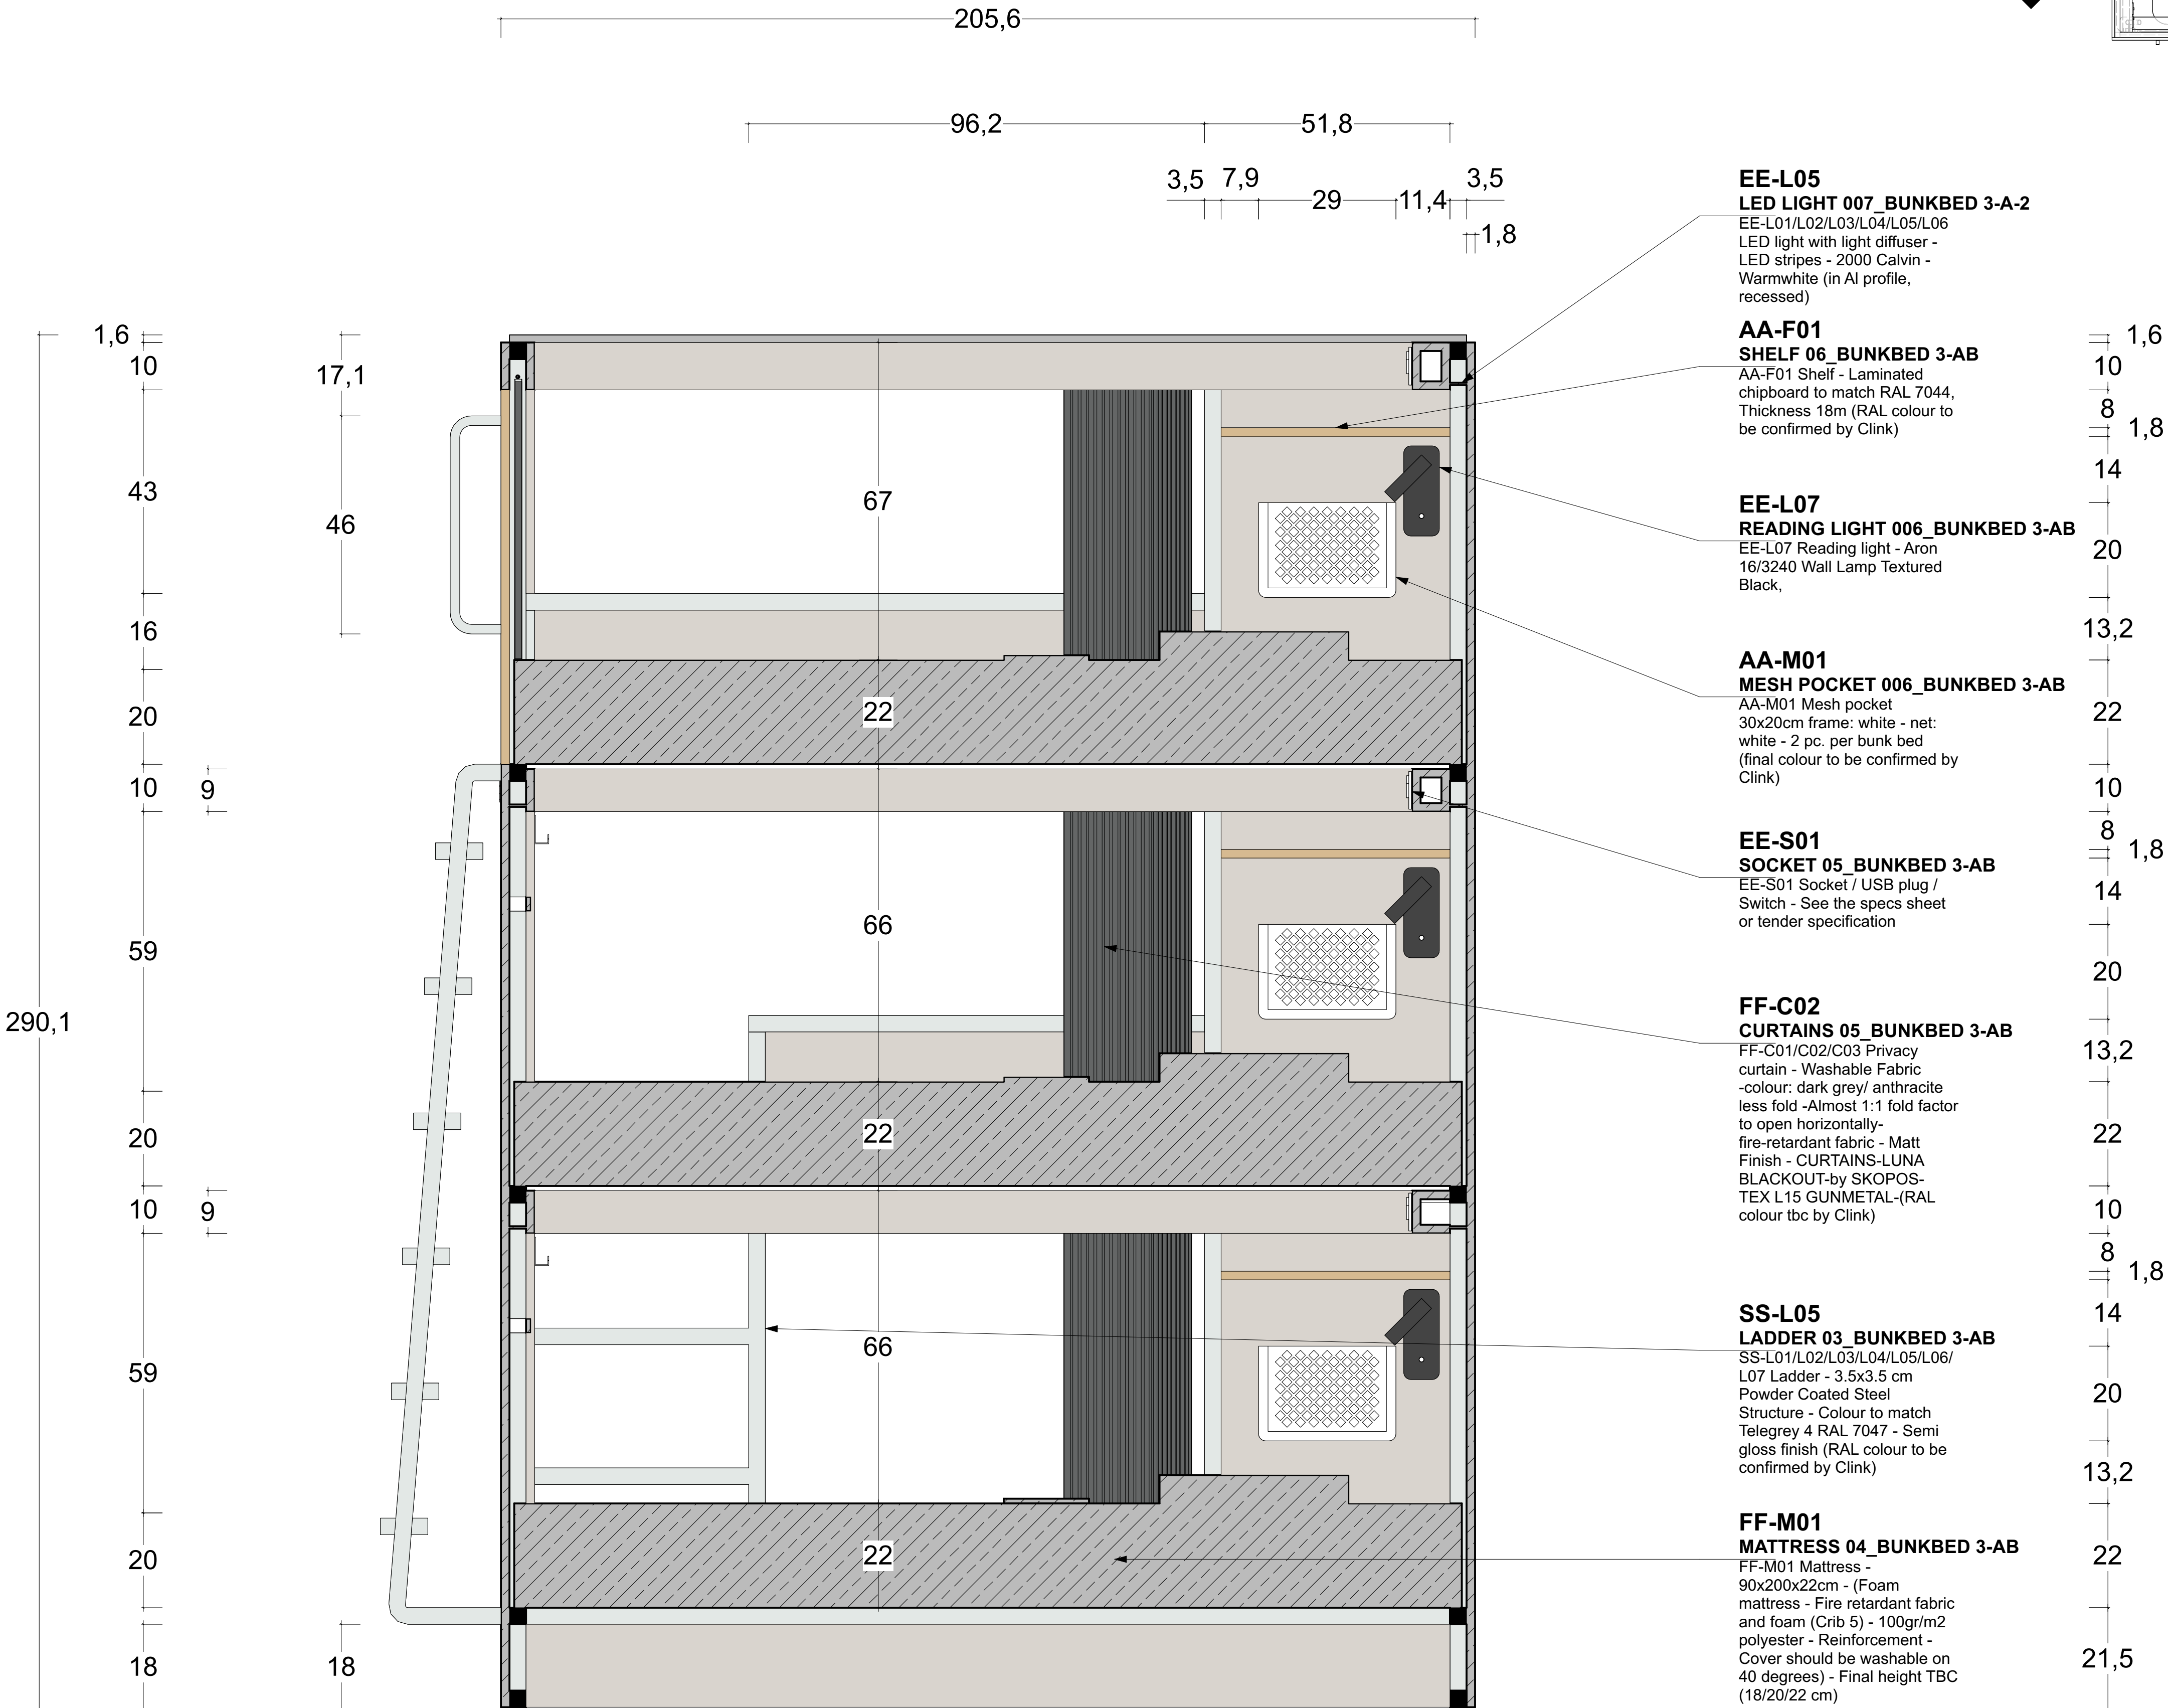

KEY

Index

A) 04.05.2026 Plan Set UP

All measurements have to be verified according to existing conditions by the contractor! Discrepancies must be reported immediately to the responsible project manager. The contractor has to produce fully dimensioned shop drawings prior to the start of the contract and they have to be approved by the client/ investor / interior designer

Project
CLINK 78 - BEDS





Project Address
CLINK 78
78 King's Cross Rd
London WC1X 9QG
United Kingdom

Client's Address
CLINK 78
78 King's Cross Rd
London WC1X 9QG
United Kingdom

Sheet Number 3-B-706		Total Sheets 82	
Sheet Title BUNKBED 3-B SECTION 1		Level	
File Name 260425_CLINK 78_BEDs AA DRAFT 03.vwx			
Date 28.04.26	Sheet Size A1	Scale 1:8	Signed AA

Stefanie Jaensch INTERIOR DESIGNS
Global Headquarter | Stefanie Jaensch c/o WeWork
Taubusanlage 8 | 60329 Frankfurt a.M.
E-Mail info@stefaniejaensch.de | DE +49 (0) 174 6756098
www.stefaniejaensch.de
Legal address | Stefanie Jaensch | Offenbacher Landstraße 434 | 60599 Frankfurt a.M.
© 2023 All Rights Reserved | Stefanie Jaensch

BUNKBEDS - TYPE 3-B (TRIPLE) - SECTION 2

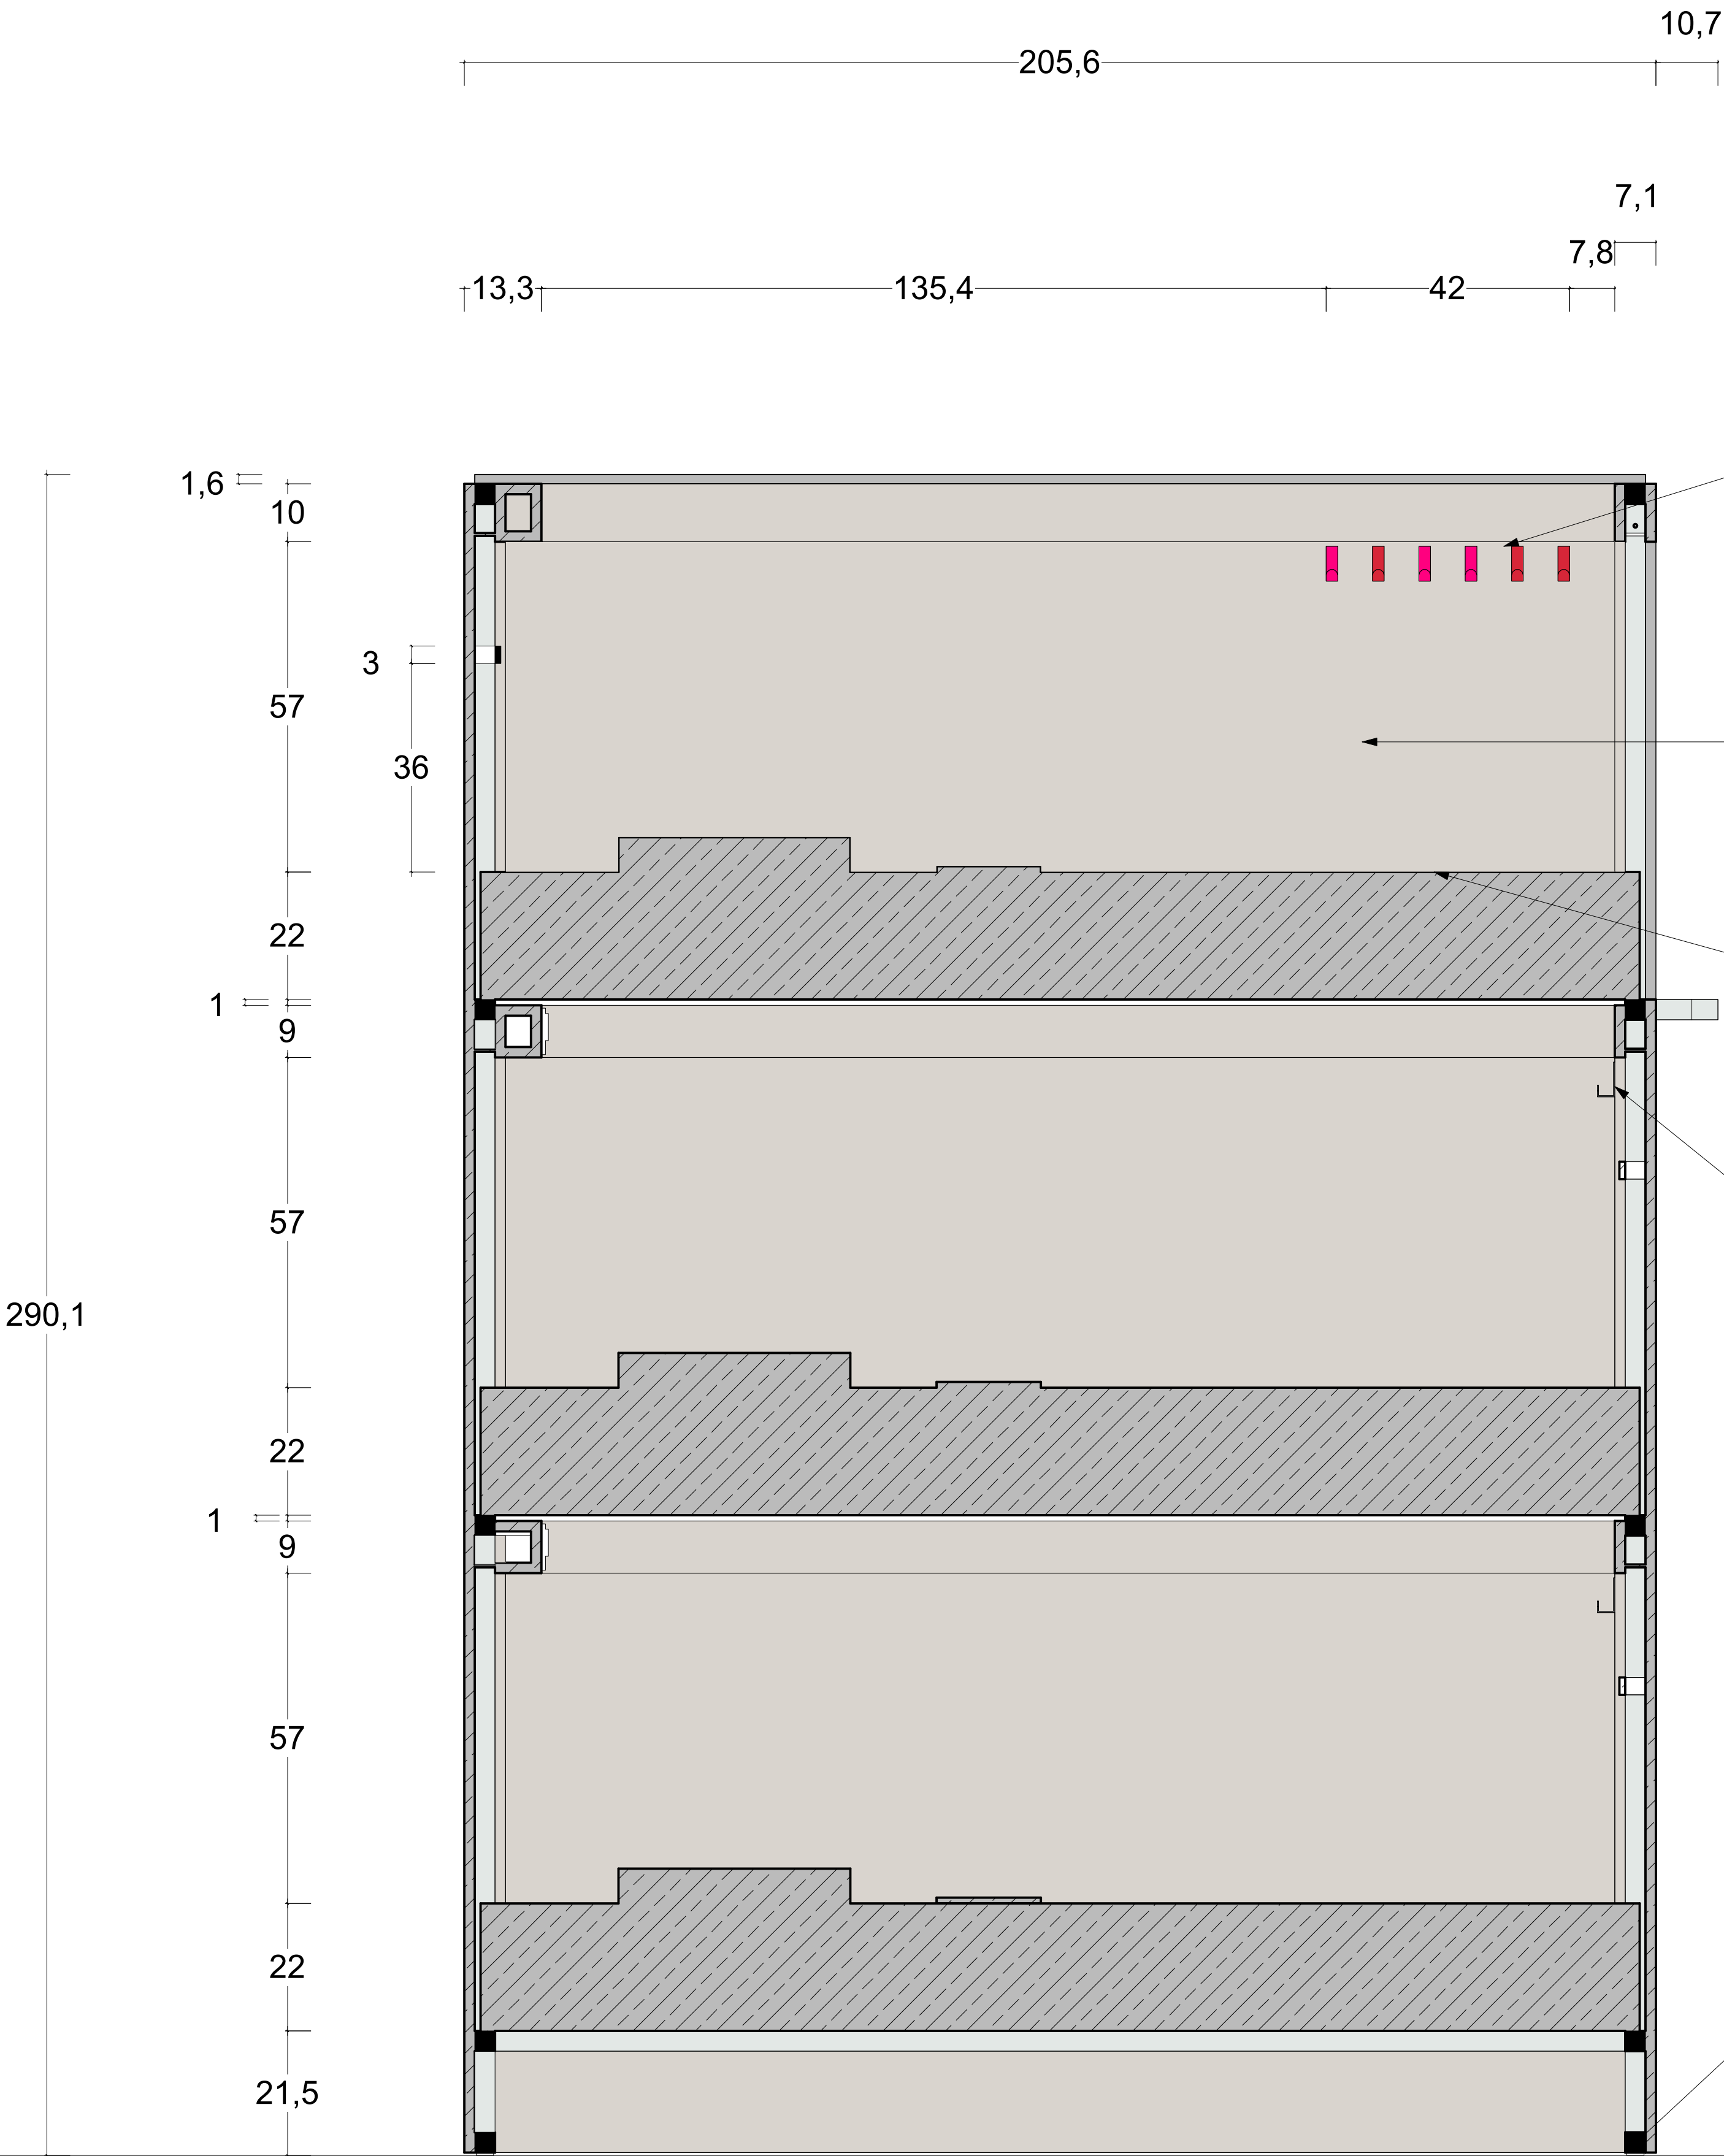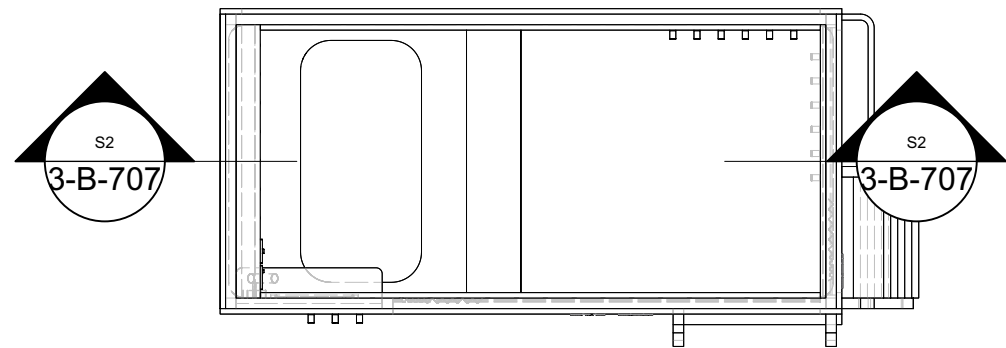

AA-H01
HOOKS 06_BUNKBED 3-AB
AA-H01 - Hooks - stainless steel powder-coated (art.2326 PB12)- RAL 3020 Red & RAL 4010 Rose (RAL colour to be confirmed by Clink)

CC-M06
mmm
CC-M01/M02/M03/M04/M05/M06 Cladding - Laminated chipboard to match RAL 7044, Thickness 18m (RAL colour to be confirmed by Clink)

FF-M01
MATTRESS 06_BUNKBED 3-AB
FF-M01 Mattress - 90x200x22cm - (Foam mattress - Fire retardant fabric and foam (Crib 5) - 100gr/m2 polyester - Reinforcement - Cover should be washable on 40 degrees) - Final height TBC (18/20/22 cm)

AA-H01
HOOKS 05_BUNKBED 3-AB
AA-H01 - Hooks - stainless steel powder-coated (art.2326 PB12)- RAL 3020 Red & RAL 4010 Rose (RAL colour to be confirmed by Clink)

SS-T01
FOOT_BUNKBED 3-AB
SS-T01 Height Adjustable Feet



KEY

Index

A) 04.05.2026 Plan Set UP

All measurements have to be verified according to existing conditions by the contractor! Discrepancies must be reported immediately to the responsible project manager. The contractor has to produce fully dimensioned shop drawings prior to the start of the contract and they have to be approved by the client/ investor / interior designer

Project
CLINK 78 - BEDS



Project Address
CLINK 78
78 King's Cross Rd
London WC1X 9QG
United Kingdom



Client's Address
CLINK 78
78 King's Cross Rd
London WC1X 9QG
United Kingdom

Sheet Number	3-B-707	Total Sheets	82
Sheet Title	BUNKBED 3-B SECTION 2	Level	
File Name	260425_CLINK 78_BEDs AA DRAFT 03.vwx		

Date	Sheet Size	Scale	Signed
28.04.26	A1	1:8	AA

Stefanie Jaensch INTERIOR DESIGNS
Global Headquarter | Stefanie Jaensch c/o WeWork
Taubusanlage 8 | 60329 Frankfurt a.M.
E-Mail info@stefaniejaensch.de | DE +49 (0) 174 6756098
www.stefaniejaensch.de
Legal address | Stefanie Jaensch | Offenbacher Landstraße 434 | 60599 Frankfurt a.M.
© 2023 All Rights Reserved | Stefanie Jaensch

BUNKBEDS - TYPE 3-B (TRIPLE) - SECTION 3

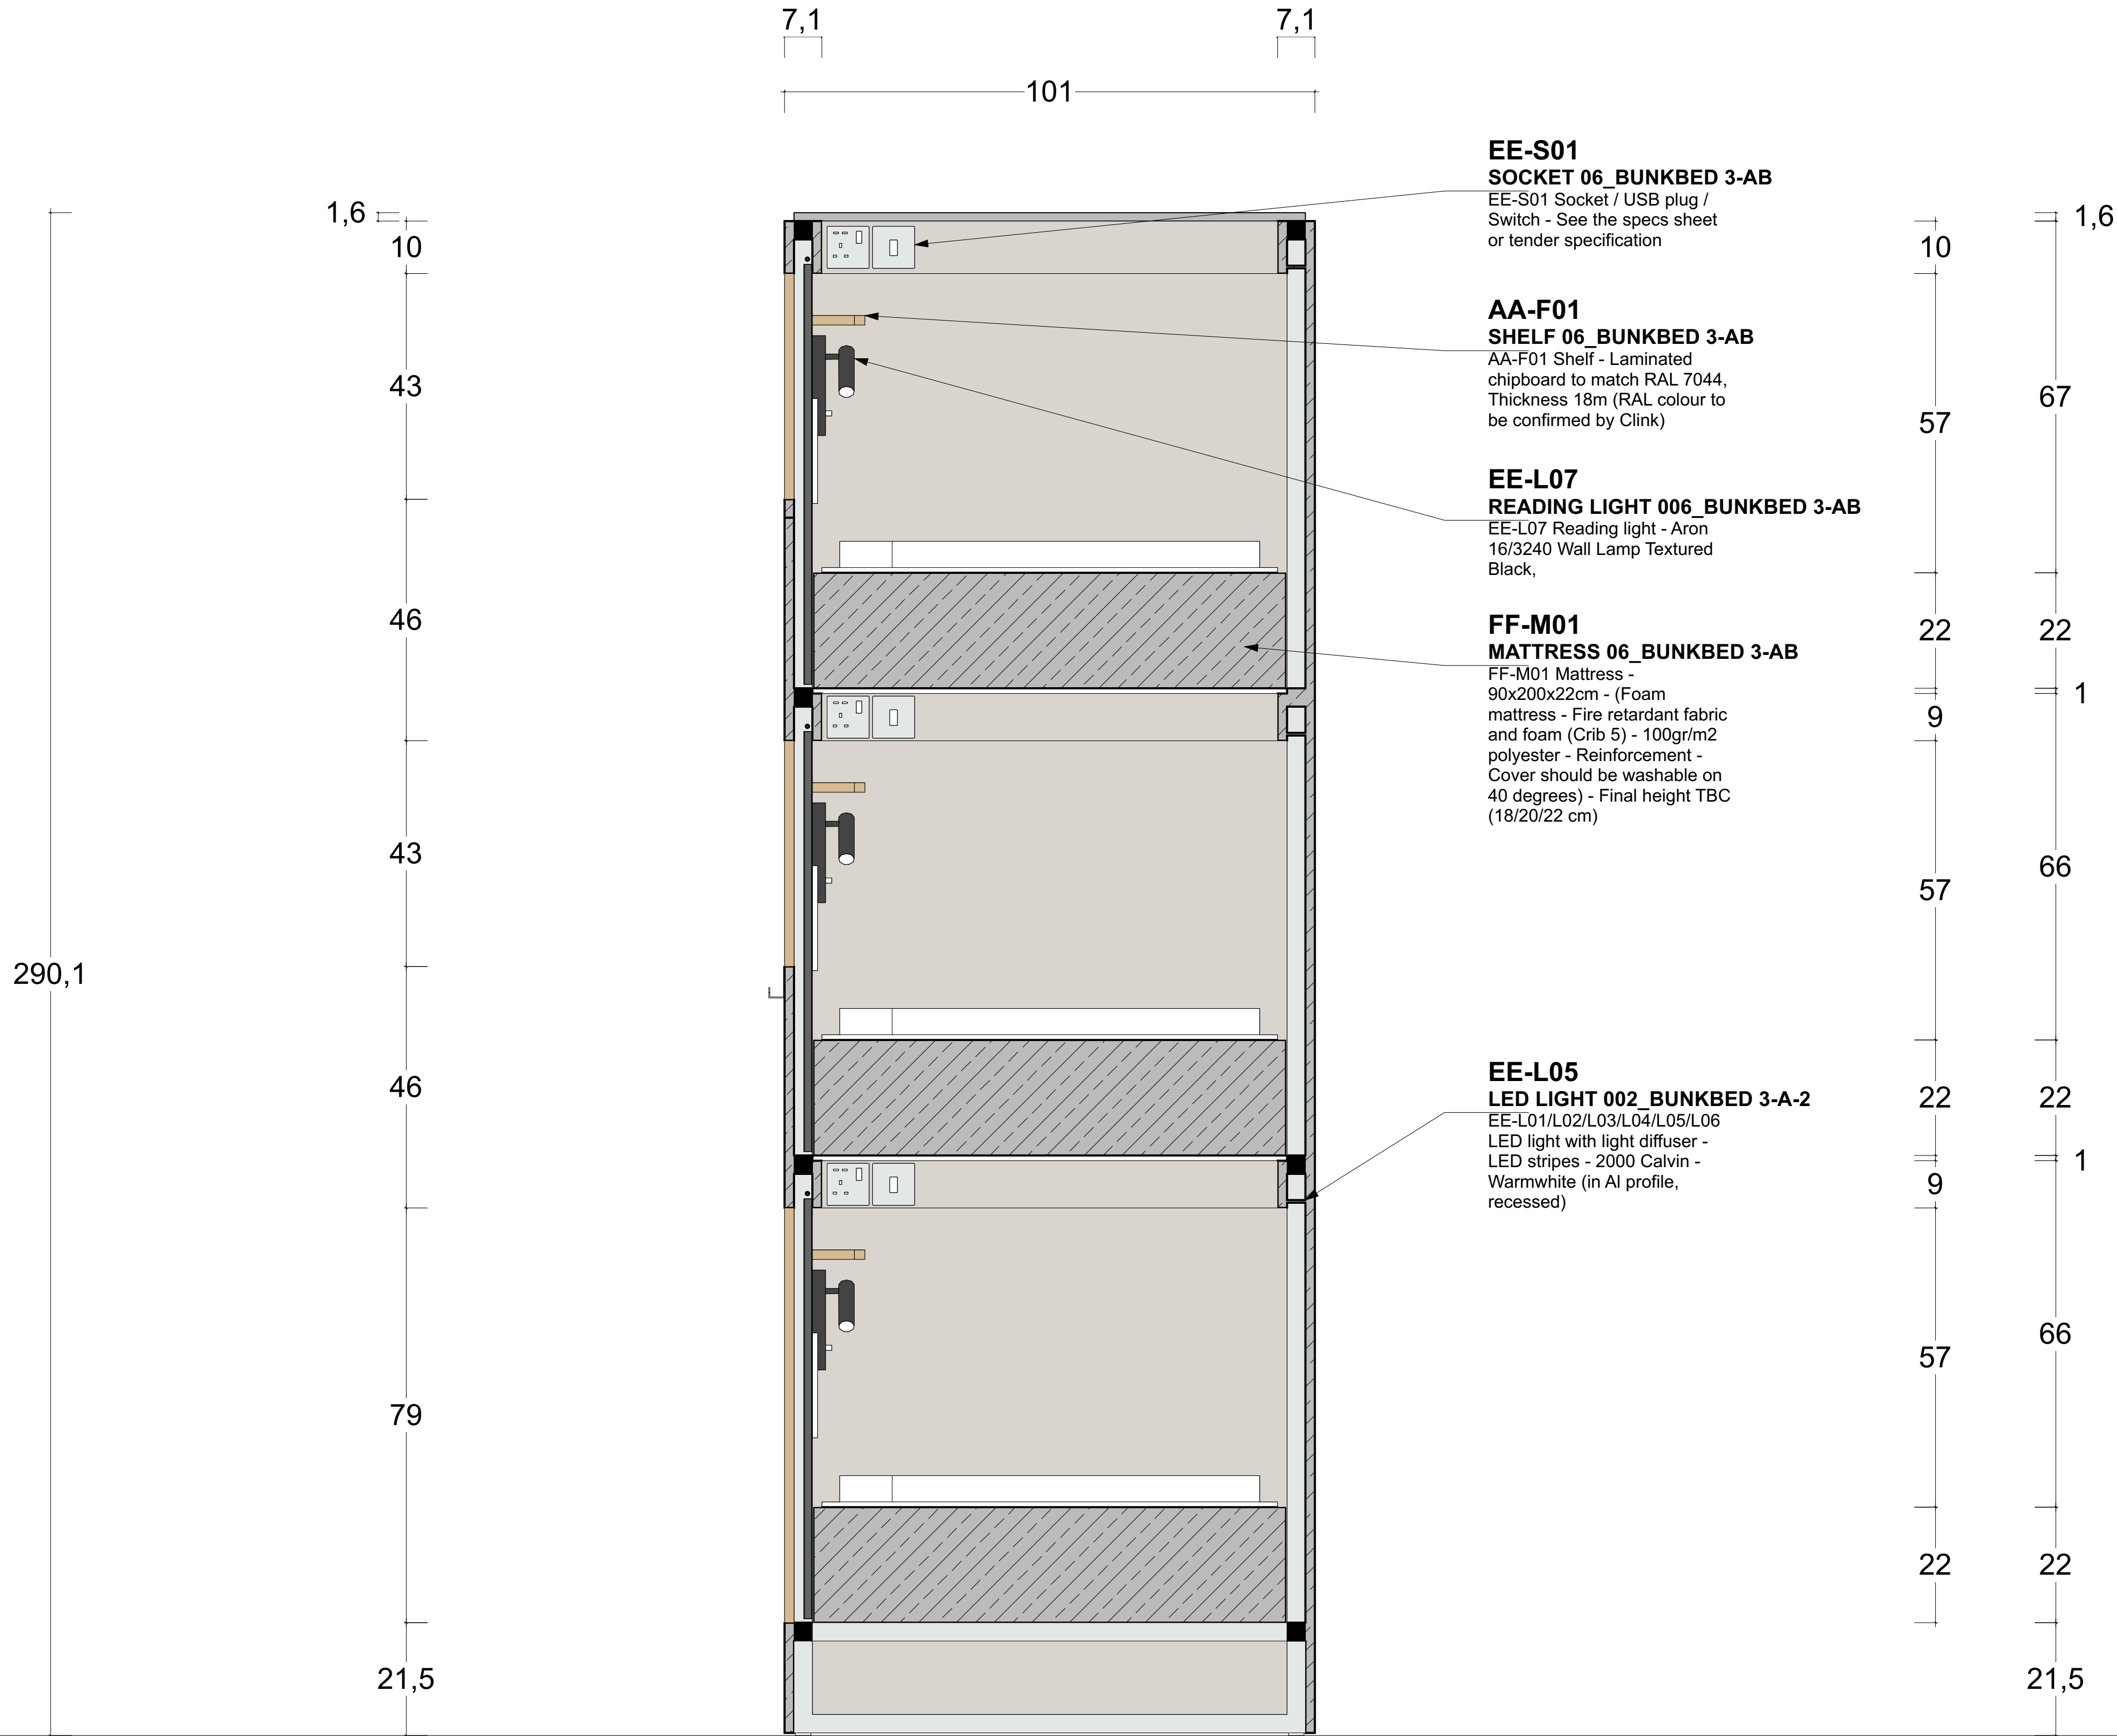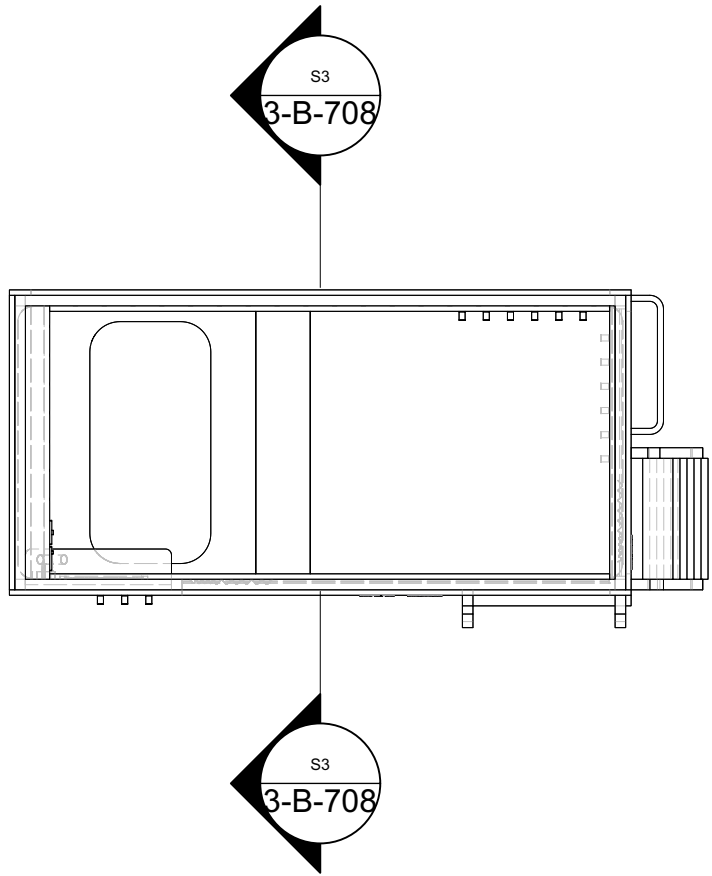

KEY

Index

A) 04.05.2026 Plan Set UP

All measurements have to be verified according to existing conditions by the contractor! Discrepancies must be reported immediately to the responsible project manager. The contractor has to produce fully dimensioned shop drawings prior to the start of the contract and they have to be approved by the client/ investor / interior designer

Project
CLINK 78 - BEDS



Project Address
CLINK 78
78 King's Cross Rd
London WC1X 9QG
United Kingdom





Client's Address
CLINK 78
78 King's Cross Rd
London WC1X 9QG
United Kingdom

Sheet Number 3-B-708		Total Sheets 82
Sheet Title BUNKBED 3-B SECTION 3		Level
File Name 260425_CLINK 78_BEDs AA DRAFT 03.vwx		

Date	Sheet Size	Scale	Signed
28.04.26	A1	1:8	AA

Stefanie Jaensch INTERIOR DESIGNS
Global Headquarter | Stefanie Jaensch c/o WeWork
Taubusanlage 8 | 60329 Frankfurt a.M.
E-Mail info@stefaniejaensch.de | DE +49 (0) 174 6756098
www.stefaniejaensch.de
Legal address | Stefanie Jaensch | Offenbacher Landstraße 434 | 60599 Frankfurt a.M.
© 2023 All Rights Reserved | Stefanie Jaensch

BUNKBEDS - TYPE 3-B (TRIPLE) - SECTION 4

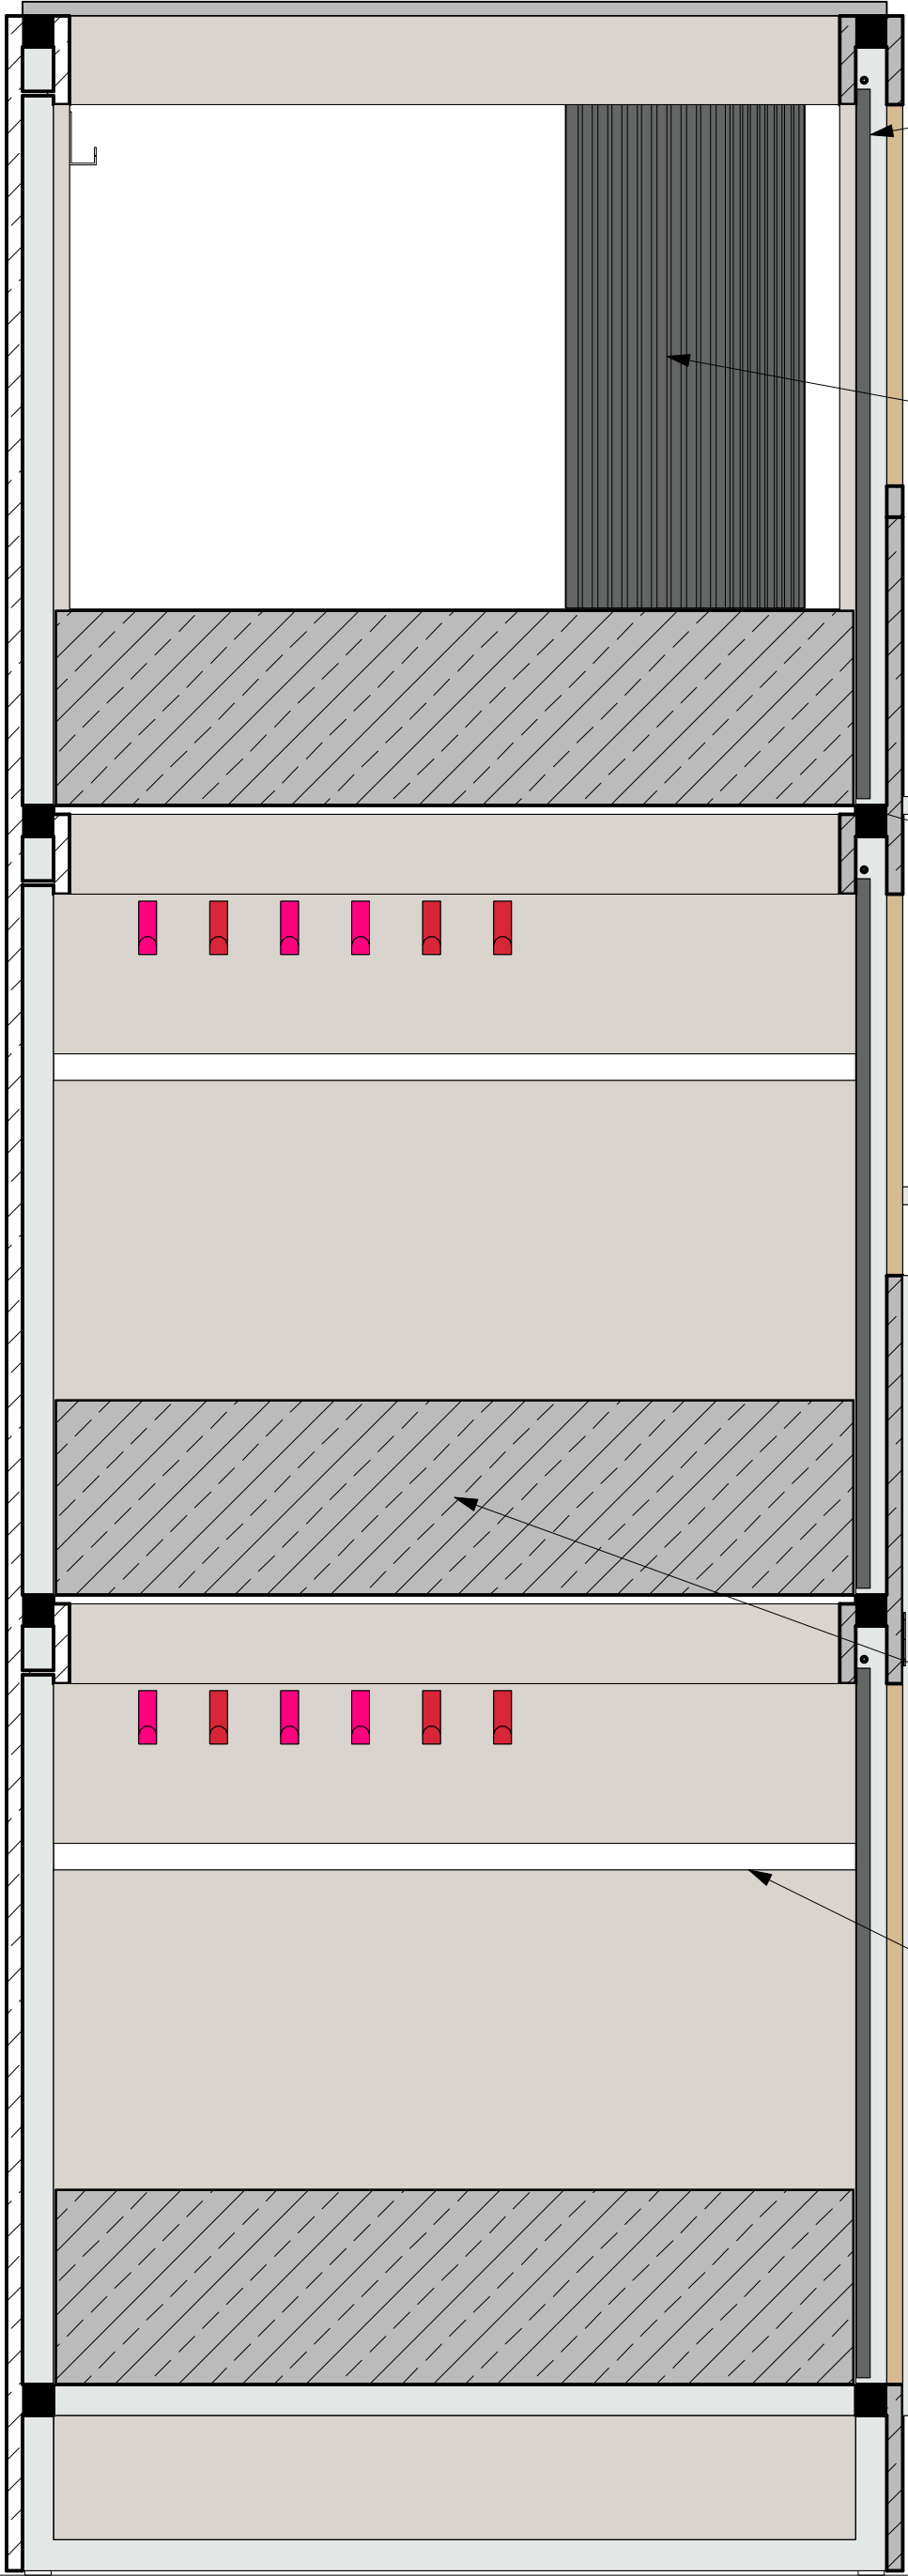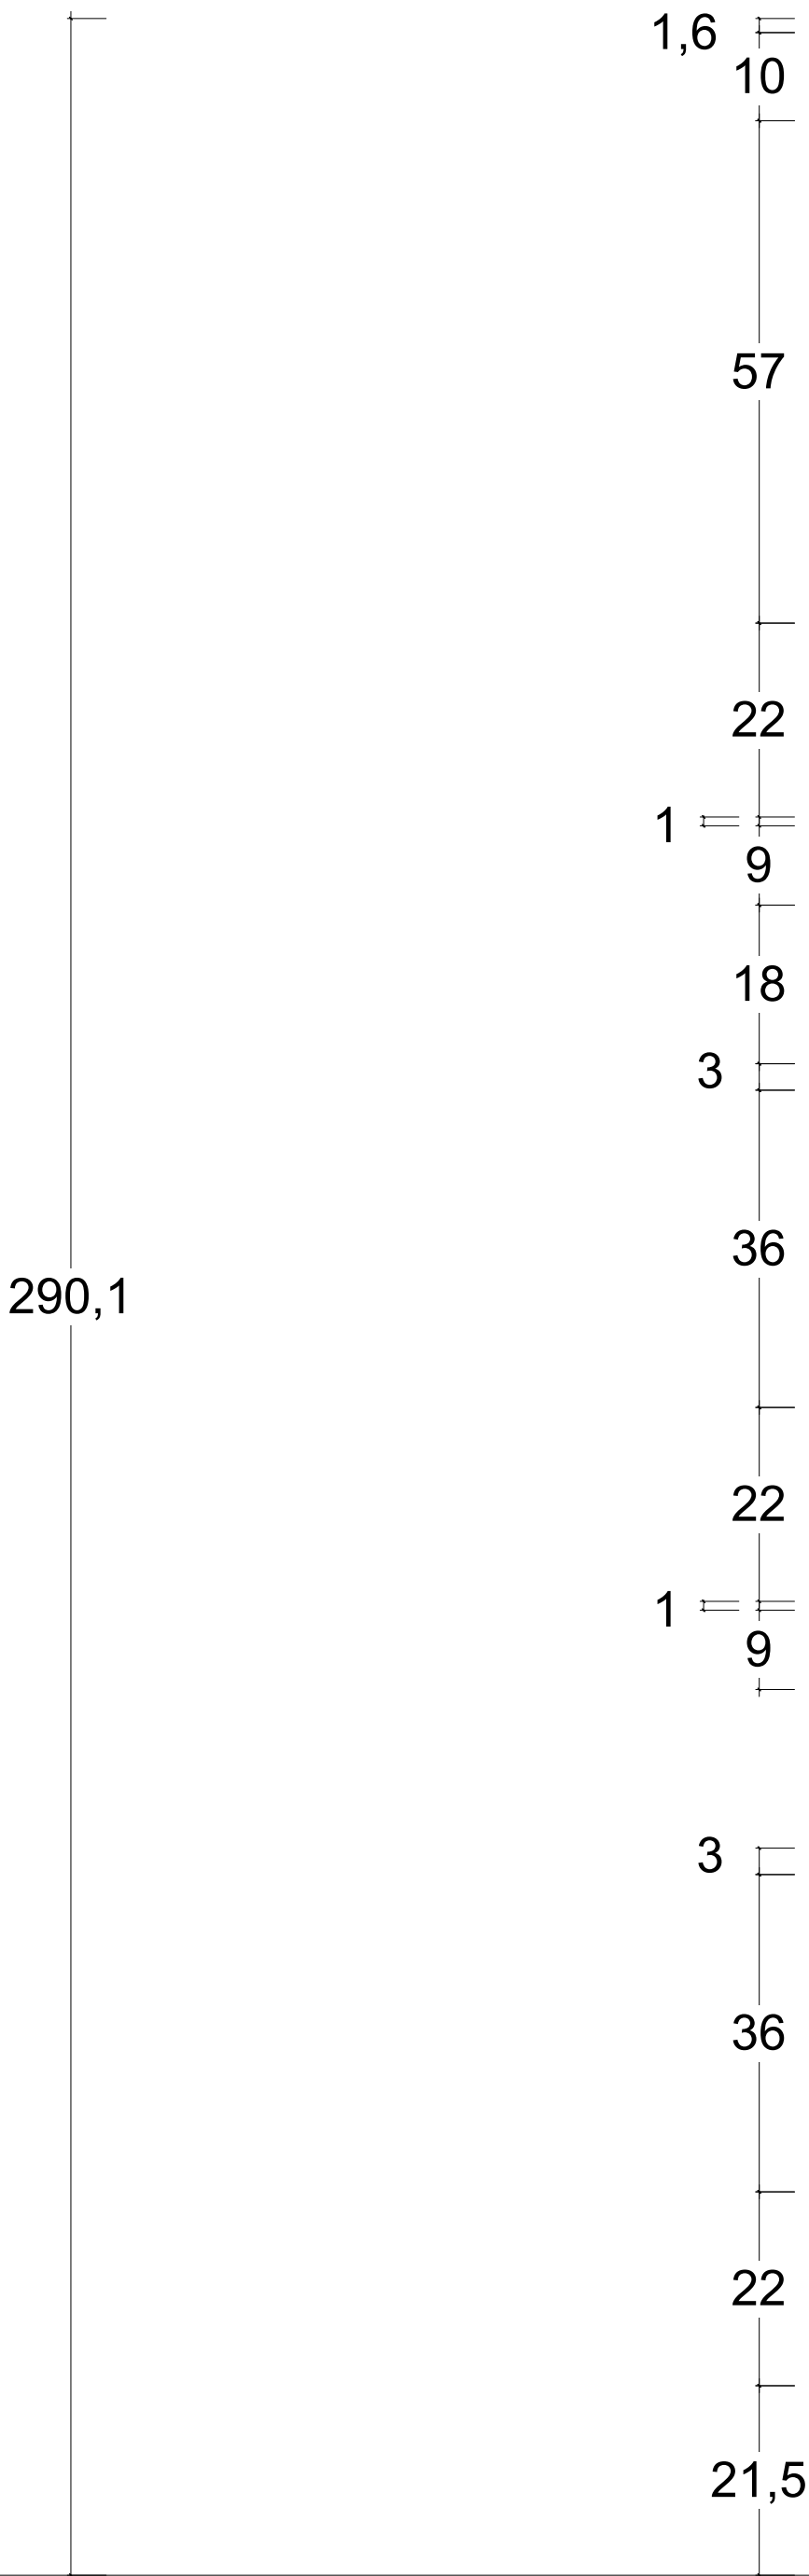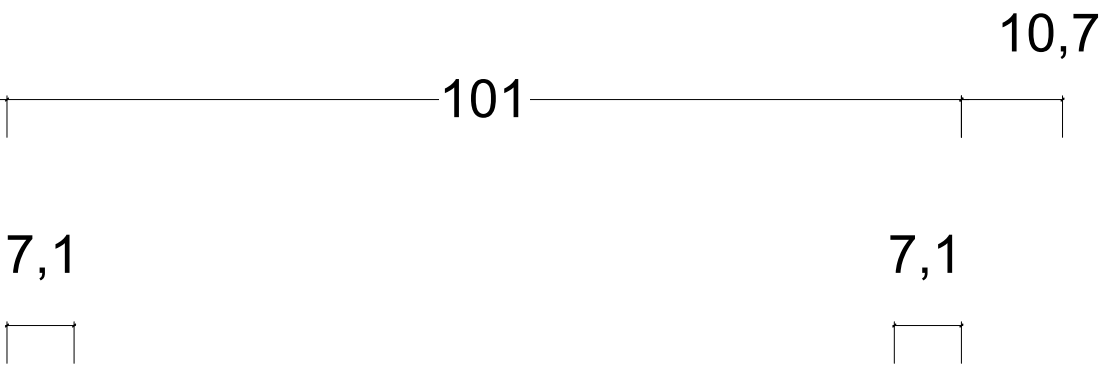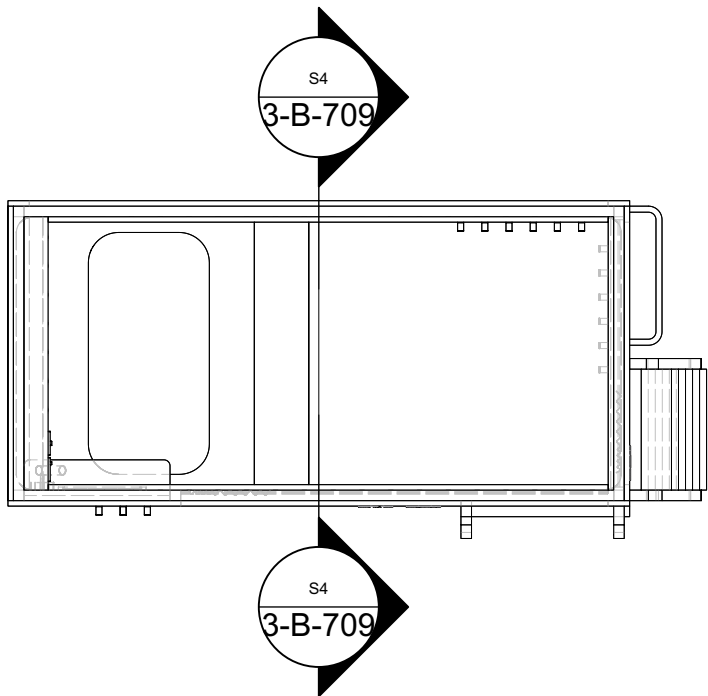


FF-C02
CURTAINS 06_BUNKBED 3-AB
FF-C01/C02/C03 Privacy curtain - Washable Fabric
-colour: dark grey/ anthracite
less fold -Almost 1:1 fold factor to open horizontally-
fire-retardant fabric - Matt
Finish - CURTAINS-LUNA
BLACKOUT-by SKOPOS-
TEX L15 GUNMETAL-(RAL colour tbc by Clink)

FF-C02
CURTAINS 07_BUNKBED 3-B
FF-C01/C02/C03 Privacy curtain - Washable Fabric
-colour: dark grey/ anthracite
less fold -Almost 1:1 fold factor to open horizontally-
fire-retardant fabric - Matt
Finish - CURTAINS-LUNA
BLACKOUT-by SKOPOS-
TEX L15 GUNMETAL-(RAL colour tbc by Clink)

FF-M01
MATTRESS 06_BUNKBED 3-AB
FF-M01 Mattress -
90x200x22cm - (Foam
mattress - Fire retardant fabric
and foam (Crib 5) - 100gr/m2
polyester - Reinforcement -
Cover should be washable on
40 degrees) - Final height TBC
(18/20/22 cm)

SS-H00
HANDRAIL 01_BUNKBED 2-A-3
SS-H00 Handrail - 3.5x3.5 cm
Powder Coated Steel
Structure - Colour to match
Telegrey 4 RAL 7047 - Semi
gloss finish (RAL colour to be
confirmed by Clink)

FF-M01
MATTRESS 05_BUNKBED 3-AB
FF-M01 Mattress -
90x200x22cm - (Foam
mattress - Fire retardant fabric
and foam (Crib 5) - 100gr/m2
polyester - Reinforcement -
Cover should be washable on
40 degrees) - Final height TBC
(18/20/22 cm)
AA-R01
RACK 04_BUNKBED 3-AB
AA-R01 TOWEL RACK -
stainless steel - powder coated
- The same colour as the
metal frame, polished edges
for safety reasons, to fit into
the metal frame size -
according to the drawing (RAL
colour to be confirmed by
Clink)

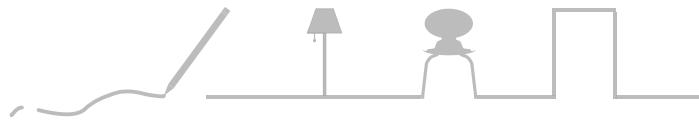

KEY

Index

A) 04.05.2026 Plan Set UP

All measurements have to be verified according to existing conditions by the contractor! Discrepancies must be reported immediately to the responsible project manager. The contractor has to produce fully dimensioned shop drawings prior to the start of the contract and they have to be approved by the client/ investor / interior designer

Project
CLINK 78 - BEDS




Project Address
CLINK 78
78 King's Cross Rd
London WC1X 9QG
United Kingdom

Client's Address
CLINK 78
78 King's Cross Rd
London WC1X 9QG
United Kingdom


Sheet Number 3-B-709		Total Sheets 82
Sheet Title BUNKBED 3-B SECTION 4		Level
File Name 260425_CLINK 78_BEDs AA DRAFT 03.vwx		
Date 28.04.26	Sheet Size A1	Scale 1:8
		Signed AA

Stefanie Jaensch INTERIOR DESIGNS
Global Headquarter | Stefanie Jaensch c/o WeWork
Taubusanlage 8 | 60329 Frankfurt a.M.
E-Mail info@stefaniejaensch.de | DE +49 (0) 174 6756098
www.stefaniejaensch.de
Legal address | Stefanie Jaensch | Offenbacher Landstraße 434 | 60599 Frankfurt a.M.
© 2023 All Rights Reserved | Stefanie Jaensch

LOCKERS - GA DRAWINGS

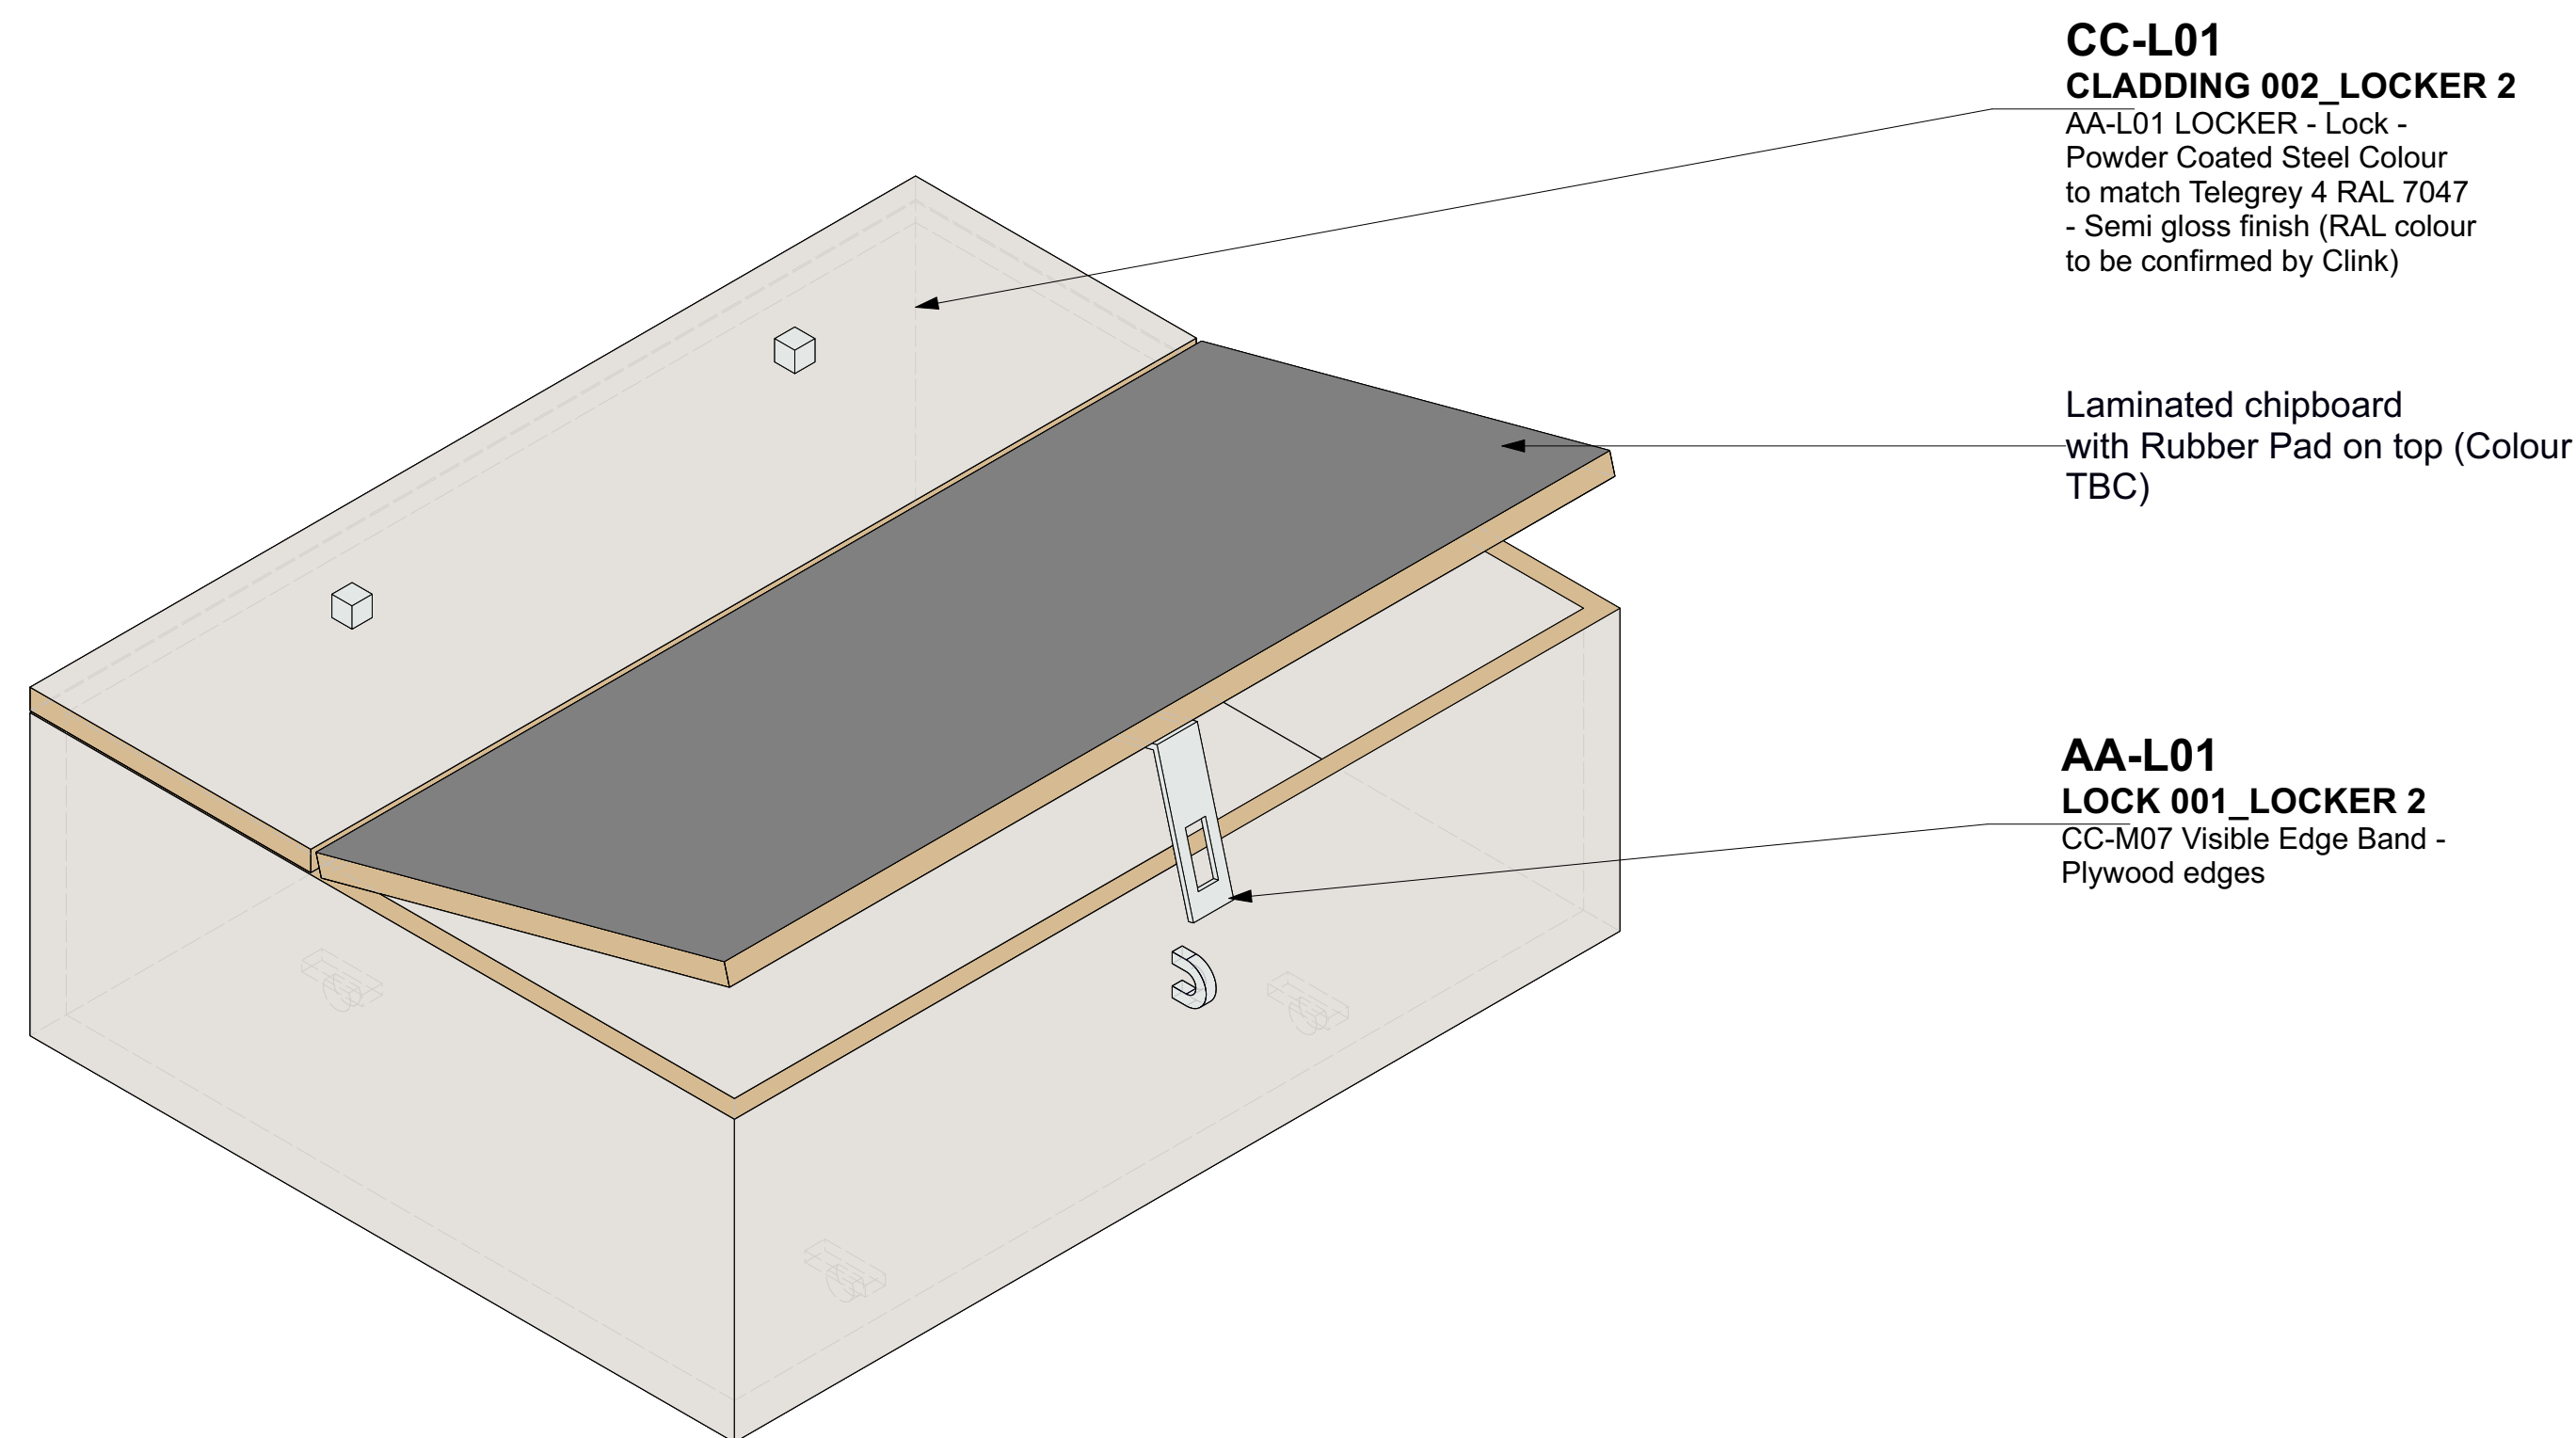


E2
4-L-000

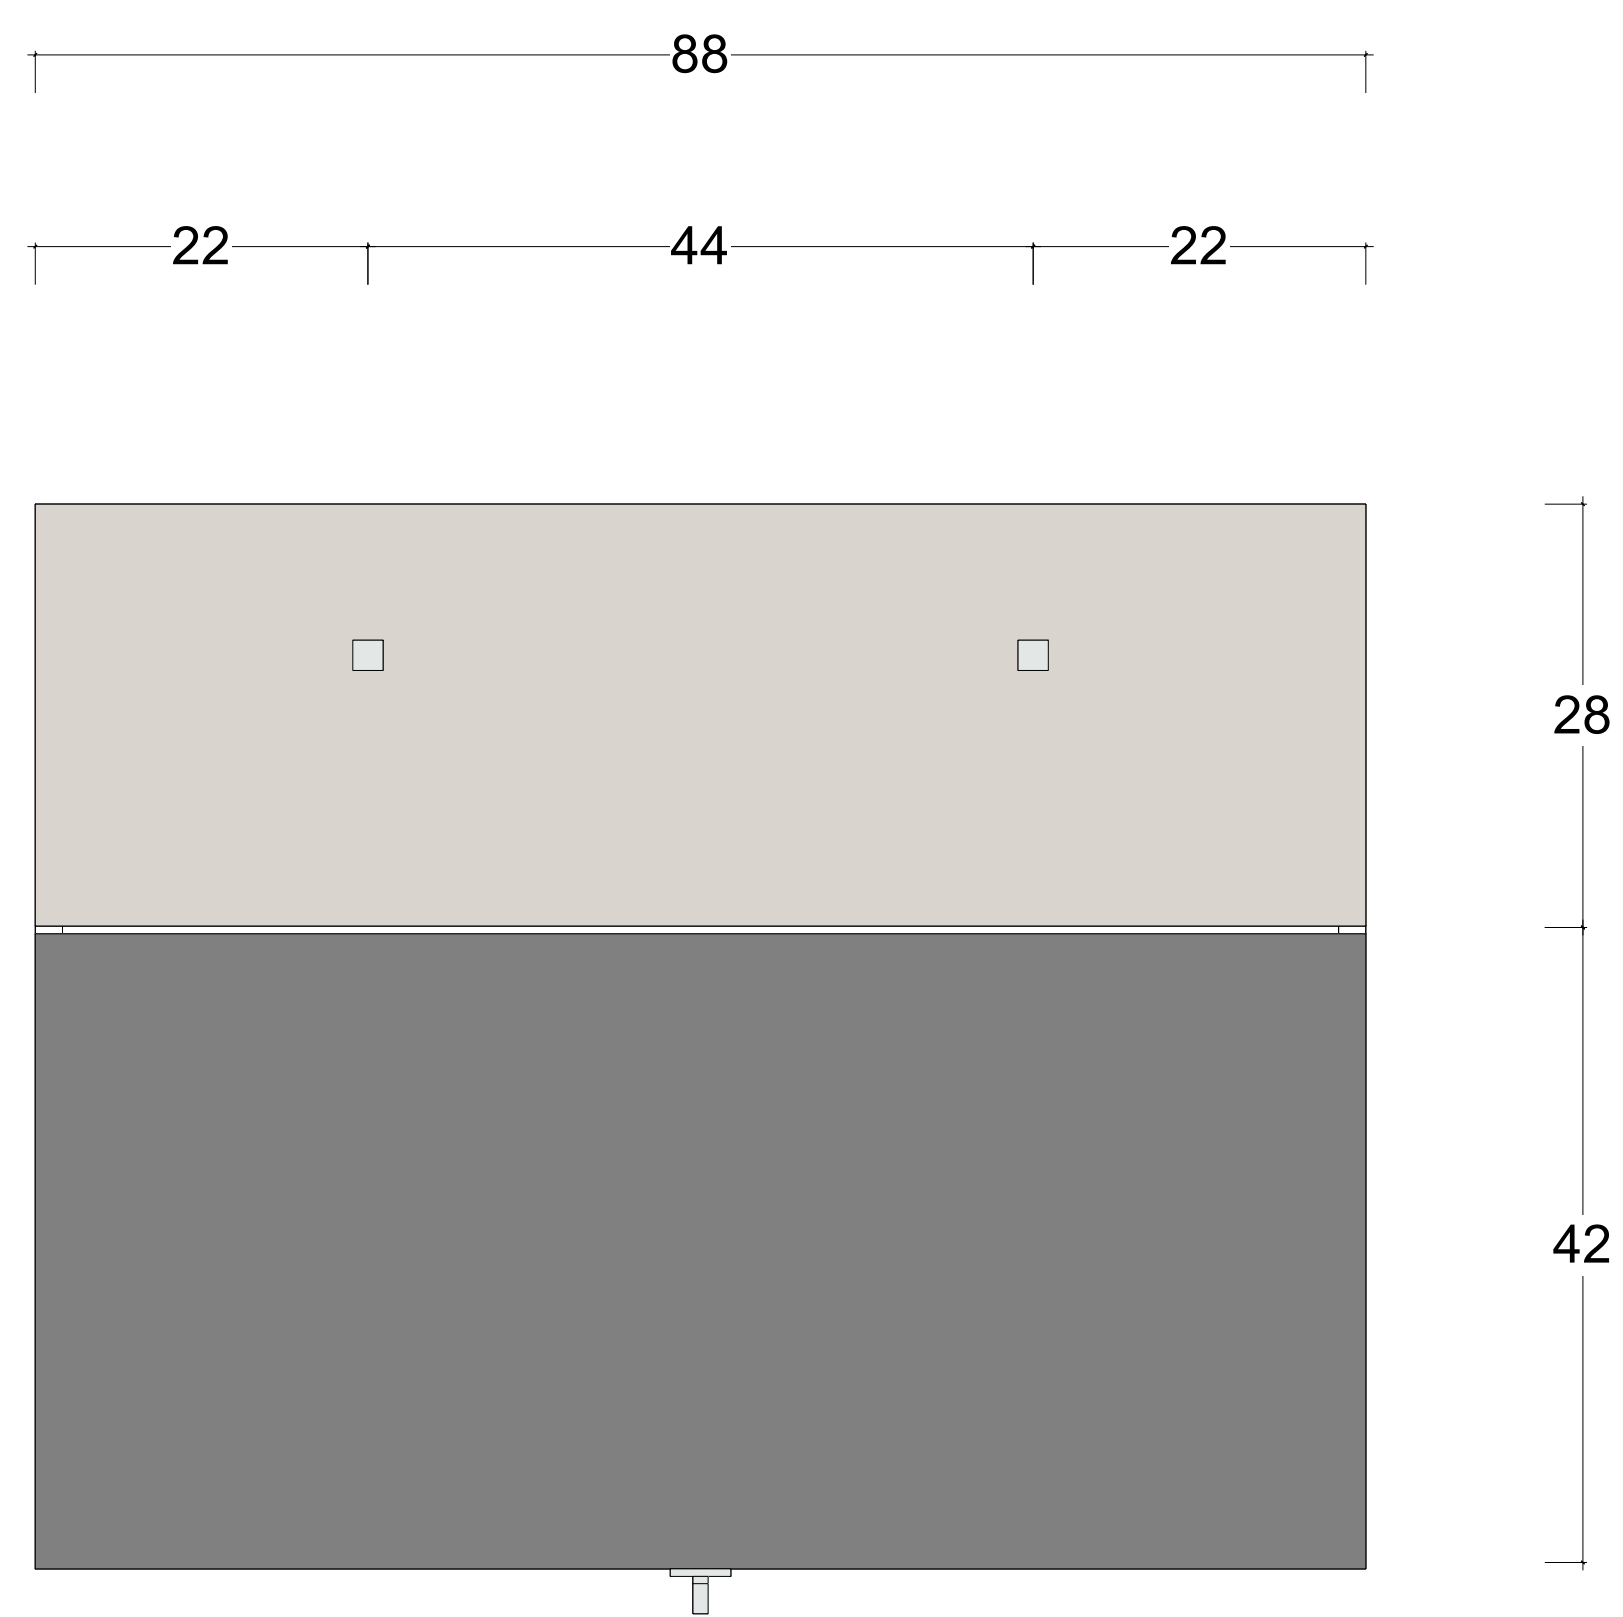


T LOCKERS - GA PLAN
Scale: 1:5


E1
4-L-000

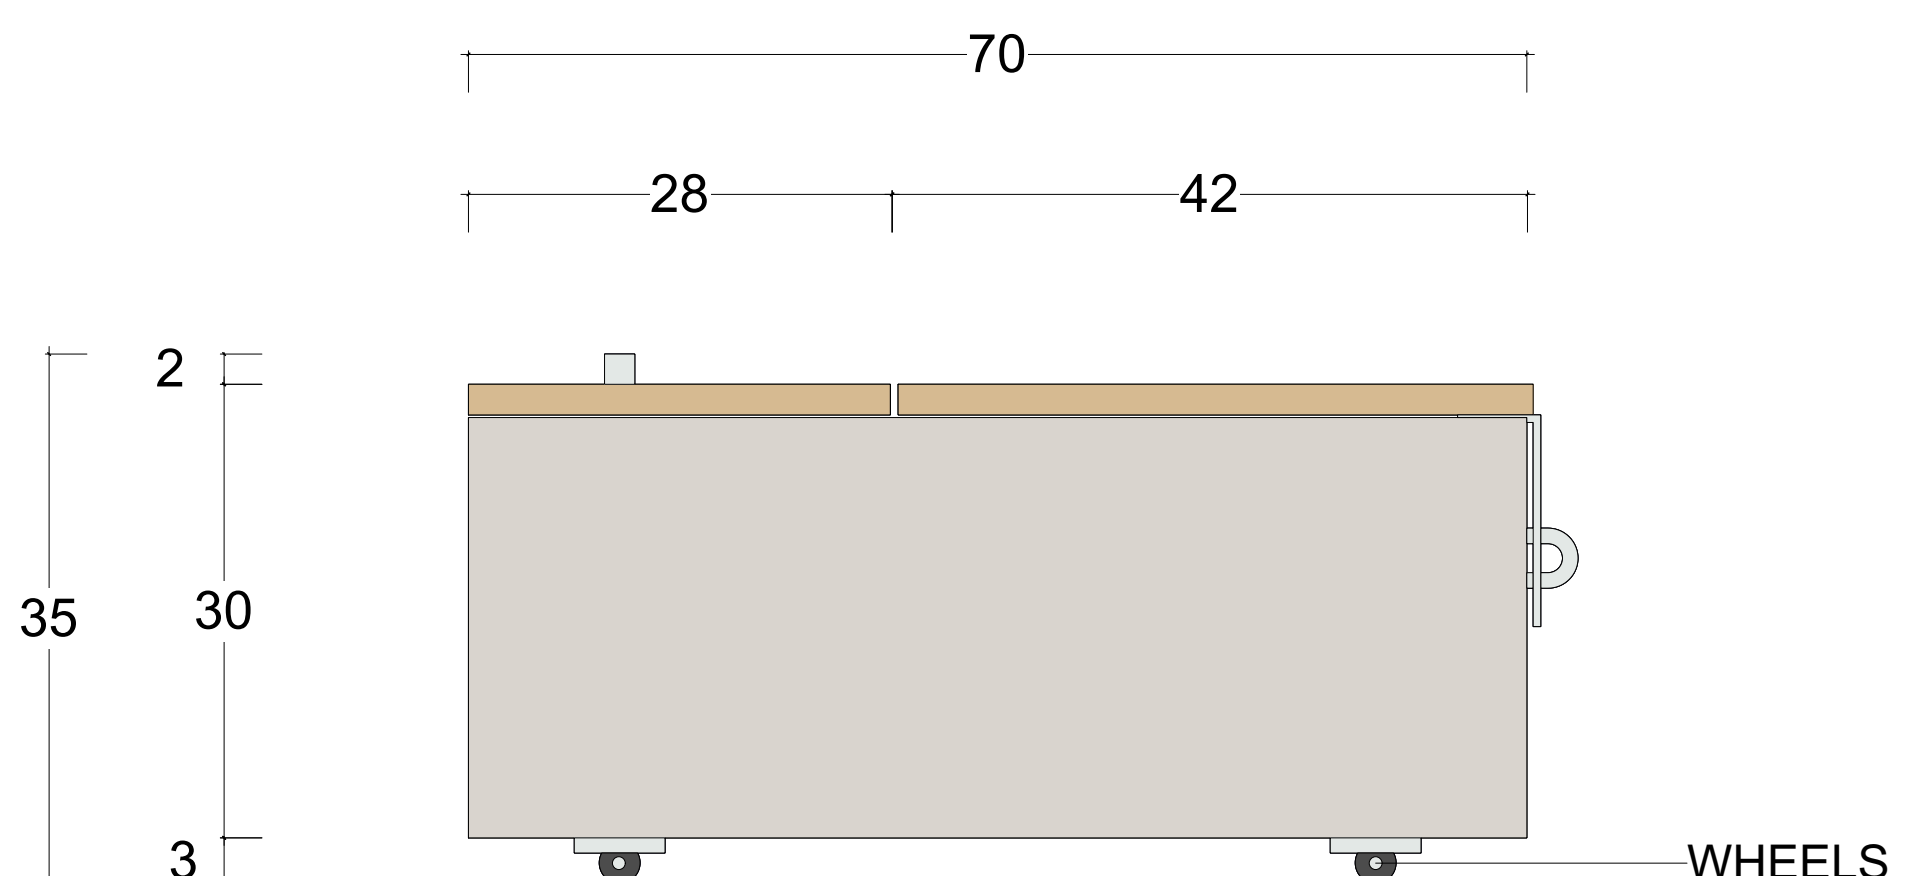

E2 LOCKERS - SIDE ELEVATION
Scale: 1:5

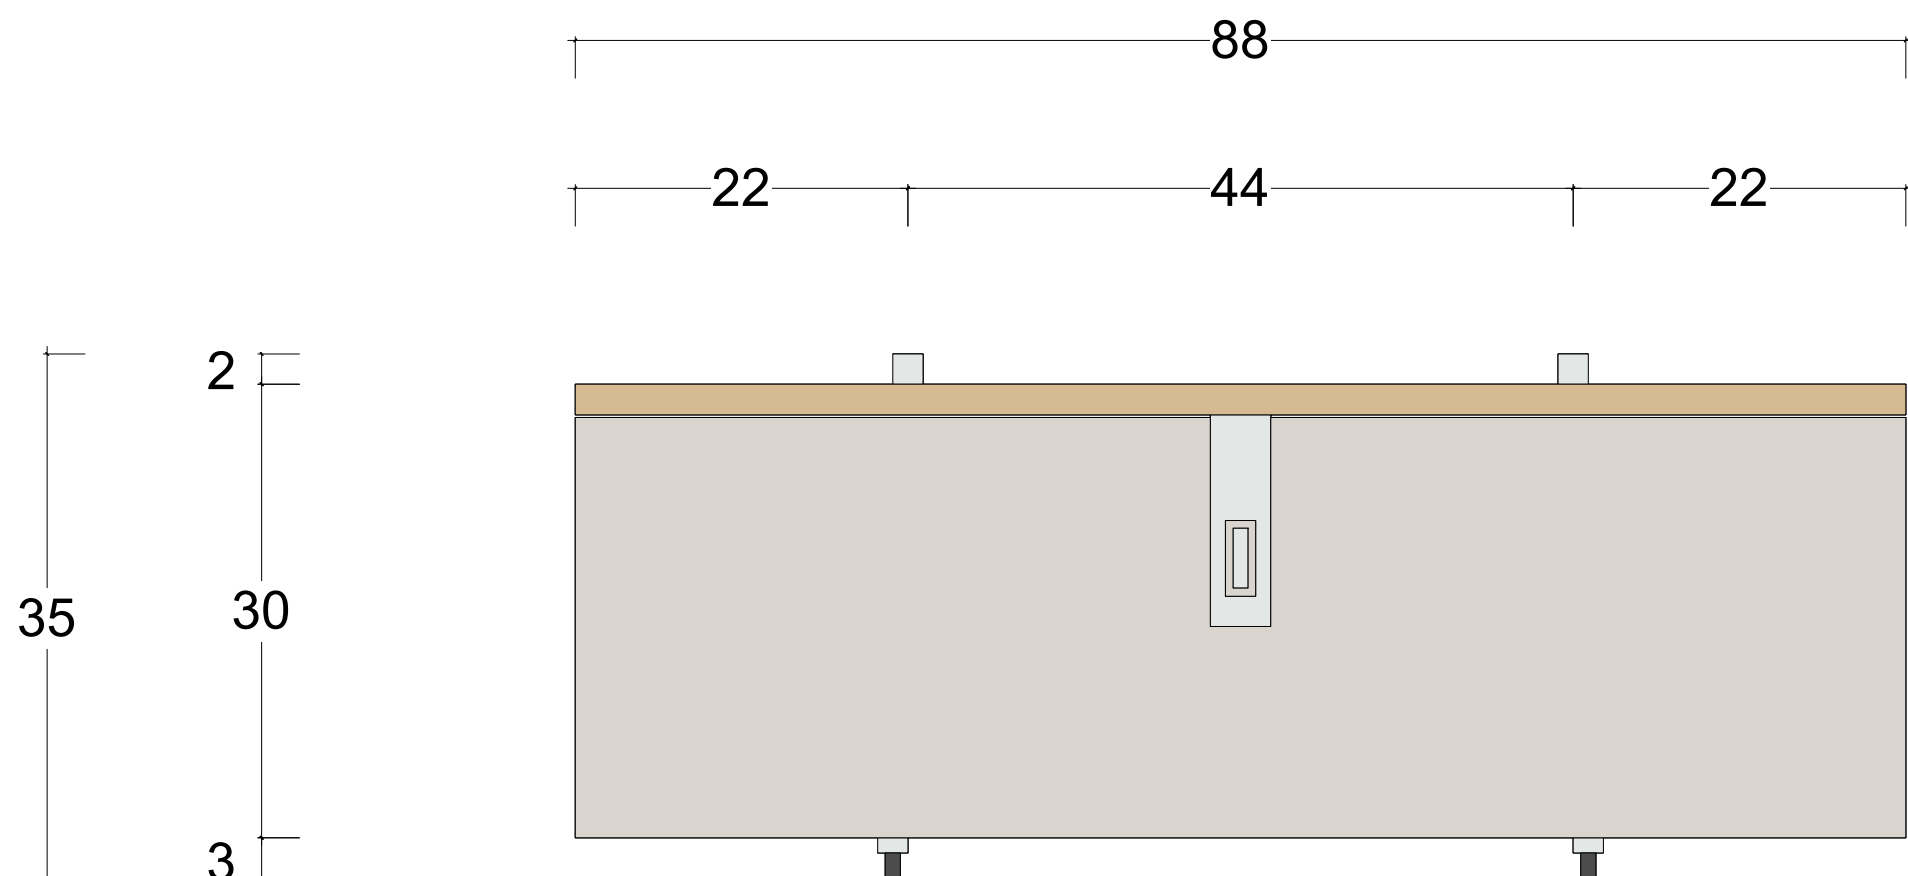

E1 LOCKERS - FRONT ELEVATION
Scale: 1:5

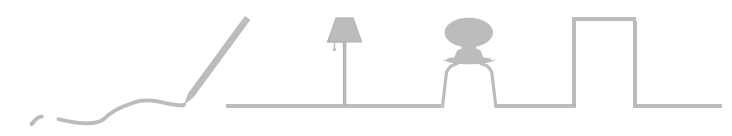

KEY

Index

A) 04.05.2026 Plan Set UP

All measurements have to be verified according to existing conditions by the contractor! Discrepancies must be reported immediately to the responsible project manager. The contractor has to produce fully dimensioned shop drawings prior to the start of the contract and they have to be approved by the client/ investor / interior designer

Project
CLINK 78 - BEDS



Project Address
CLINK 78
78 King's Cross Rd
London WC1X 9QG
United Kingdom

Client's Address
CLINK 78
78 King's Cross Rd
London WC1X 9QG
United Kingdom

Sheet Number 4-L-000 Total Sheets 82


Sheet Title LOCKERS Level

File Name 260425_CLINK 78_BEDs AA DRAFT 03.vwx

Date	Sheet Size	Scale	Signed
28.04.26	A1	1:5	AA

Stefanie Jaensch INTERIOR DESIGNS
Global Headquarter | Stefanie Jaensch c/o WeWork
Taubusanlage 8 | 60329 Frankfurt a.M.
E-Mail info@stefaniejaensch.de | DE +49 (0) 174 6756098
www.stefaniejaensch.de
Legal address | Stefanie Jaensch | Offenbacher Landstraße 434 | 60599 Frankfurt a.M.
© 2023 All Rights Reserved | Stefanie Jaensch

OVERVIEW - SPECS SHEET

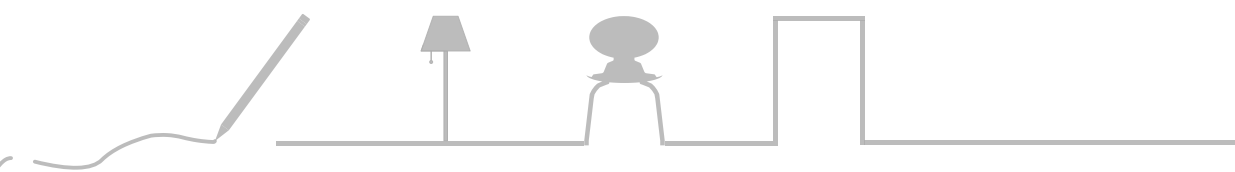

Stefanie Jaensch

INTERIOR DESIGNS

For



STRUCTURE

SOFT FURNITURE

CLADDING



SS-F/L/G
Frame/Ladder/Guard -
3.5x3.5 cm Powder
Coated Steel Structure -
Colour to match
Telegrey RAL 7047 -
Semi gloss finish
**FINAL RAL COLOUR
TBC BY CLINK**


SS-T01
Height Adjustable Feet

SS-B01
Bed Base - 90x200cm
Perforated metal slab for
ventilation



FF-C01
Metal ring curtains with a sturdy/durable pole
Privacy curtain - washable textile - colour: dark
grey/ anthracite less fold - Almost 1:1 fold
factor to open horizontally - fire-retardant fabric
LUNA BLACKOUT by SKOPOS
TEXTURED L15 GUNMETAL
FINAL COLOUR TBC BY CLINK

FF-M01
Mattress - 90/135 x 200 x 22cm -
(Foam Mattress - Fire retardant fabric
and foam (Crib 5) - 100gr/m2
polyester - Reinforcement - Cover
should be washable on 40 degrees)
**FINAL MATTRESS HEIGHT TBC
(18 / 20 / 22)cm**

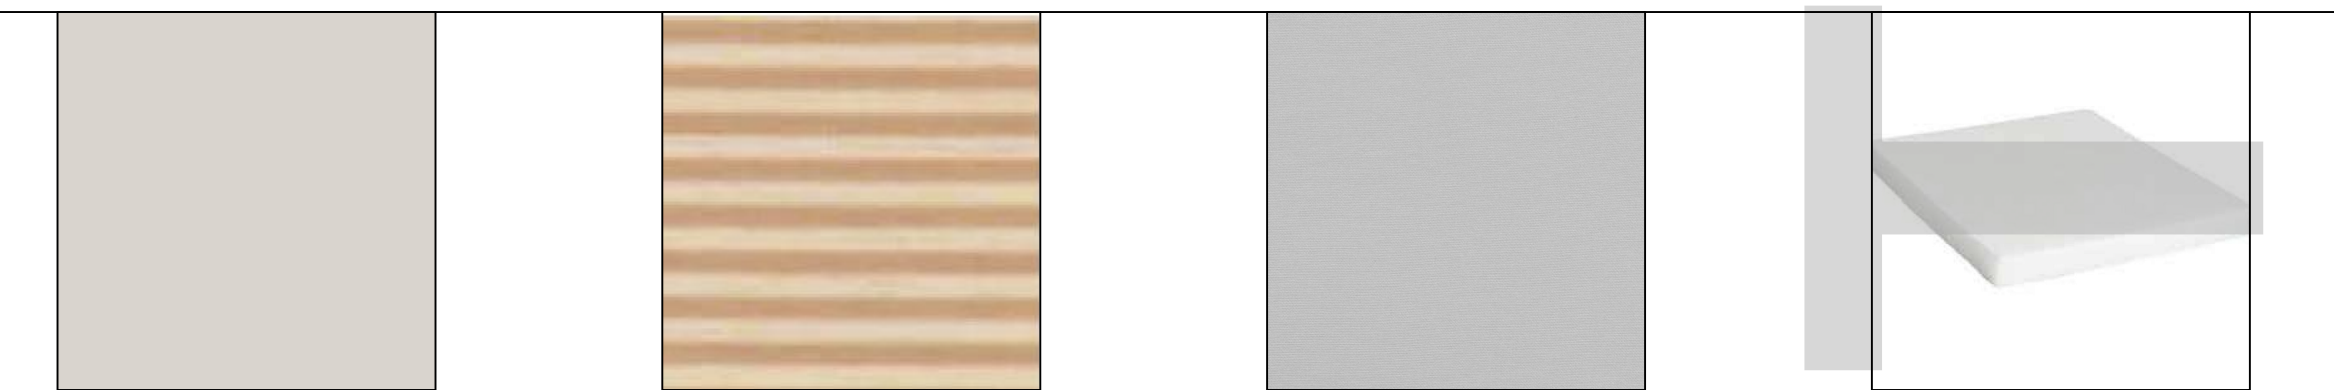


CC-M01
Cladding - Laminated
chipboard - Colour to
match RAL 7044,
Thickness 18m
**FINAL RAL COLOUR
TBC BY CLINK**

CC-M07
Visible Edges
Plywood edges

CC-H01
Headboard: Fabric
Spradling Silvertex
Aluminium 122-2101
14-4103 TPX
(PODS ONLY)
**FINAL COLOUR TBC
BY CLINK**

CC-S01
Sound insulation
material Ewona, 30mm
(PODS ONLY)

ACCESSORIES

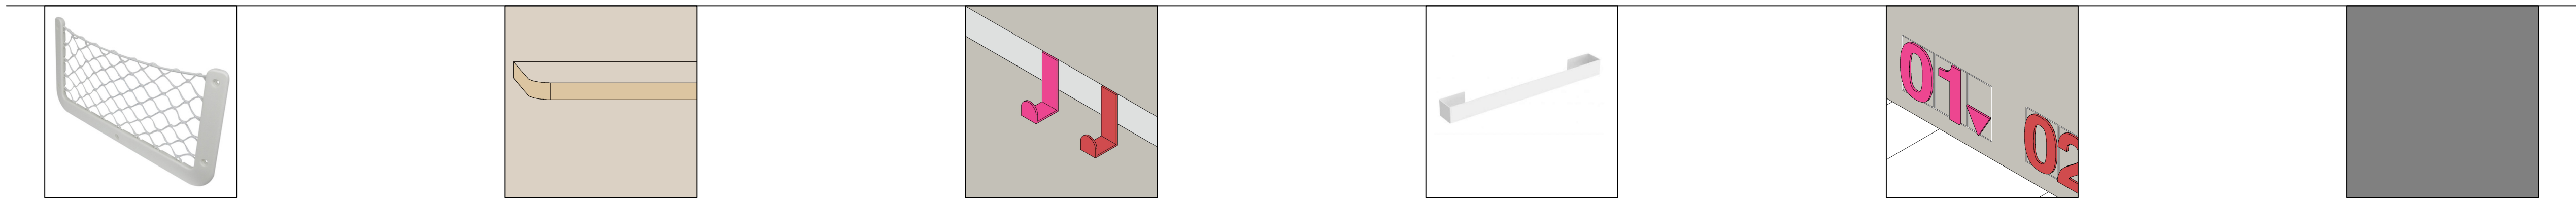

AA-M01
Mesh pocket 30x20cm
frame: white - net: white
- 2 pc. per bunk bed
**FINAL COLOUR TBC
BY CLINK**

AA-F01
Shelf - Laminated chipboard -
Colour to match RAL 7044,
Thickness 18m
**FINAL COLOUR TBC BY
CLINK**

AA-H01
Hooks - stainless steel
powder-coated (art.2326
PB12)- RAL 3020 Red &
RAL 4010 Rose
**FINAL HOOKS
QUANTITY & COLOUR
TBC BY CLINK**

AA-R01
TOWEL RACK - stainless steel -
powder coated - The same colour as
the metal frame, polished edges for
safety reasons, to fit into the metal
frame size - according to the drawing
FINAL COLOUR TBC BY CLINK

AA-S01
SIGNAGE - Numbers - laser-cut
acrylic or MDF - thickness 5mm -
spray painted - RAL 3020 Red &
RAL 4010 Rose - font according
to wayfinding signage design
**FINAL RAL COLOUR TBC BY
CLINK**

AA-P01
Rubber Pad on the top of
Steps & Lockers
(Colour TBC)

ELECTRICAL



EE-L02
LED light with light
diffuser - LED stripes -
2000 Calvin -
Warmwhite
(in AI profile, recessed)

EE-L01
Aron 16/3240 Wall Lamp
Textured Black,
LED 1x3W 3000K
315lm, CL.I, Integrated
LED, With switch,
Adjustable - 1 pc. per
bed

EE-D01
Smoke detector optical
(PODS ONLY)

ME-V01
Ventilation system:
Europlast NGA100
(PODS ONLY)


ME-V02
Ventilation system:
Vent-Axia VASF100TC
(479088)
(PODS ONLY)

**EE-S01
OPTION 1**
Socket / USB C plug / Switch
Brand: Definity Complete
Supplier: Scolmore.com
- 13A 1 Gang Switched Socket
Outlet With Twin Type C USB
(4A) Outlets - SFSS595GY
- 10AX 1 Gang 2 Way Plate
Switch - SFSS411GY
color: SS stainless steel

**EE-S01
OPTION 2**
Socket / USB C plug / Switch
Brand: Deco
Supplier: Scolmore.com
- 13A 1 Gang Switched Socket
Outlet With Twin Type C USB
(4A) Outlets - VPSS595GY
- 10AX 1 Gang 2 Way Plate
Switch - VPSS411GY
color: SS stainless steel

**EE-S01
OPTION 3**
Socket / USB C plug / Switch
Brand: Soho Lighting
Supplier: Elesi.com
- Flat Plate 1 Gang USB C+C
Socket (13A Socket + 2 USB C
3.1A Ports) - SKU:
SS-SH-10-SKT221-BCW
- 1 Gang 2 Way 10A Light Switch
Wht Ins Screwless
SKU: SS-SH-20-LTS101-BCW
color: Brushed Chrome

The drawing package shows the ventilation method for the pods only. SJID is not responsible for the ventilation of the bunk beds/pods. Clink is to confirm whether any additional ventilation, health, safety, or regulatory requirements apply.

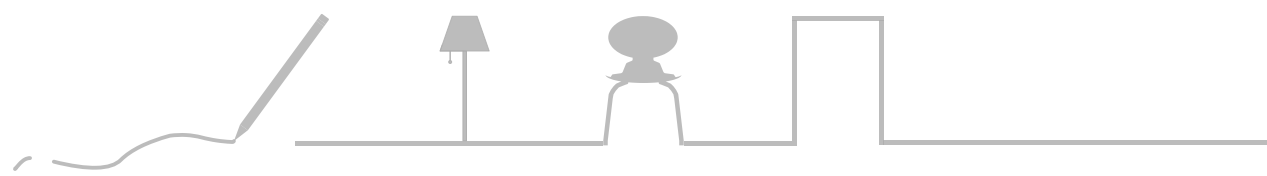

For



THANK YOU

THE
DRAWING